


Согласовано		Взам. инв. №	
		Подп. и дата	
Инв. № подл.			

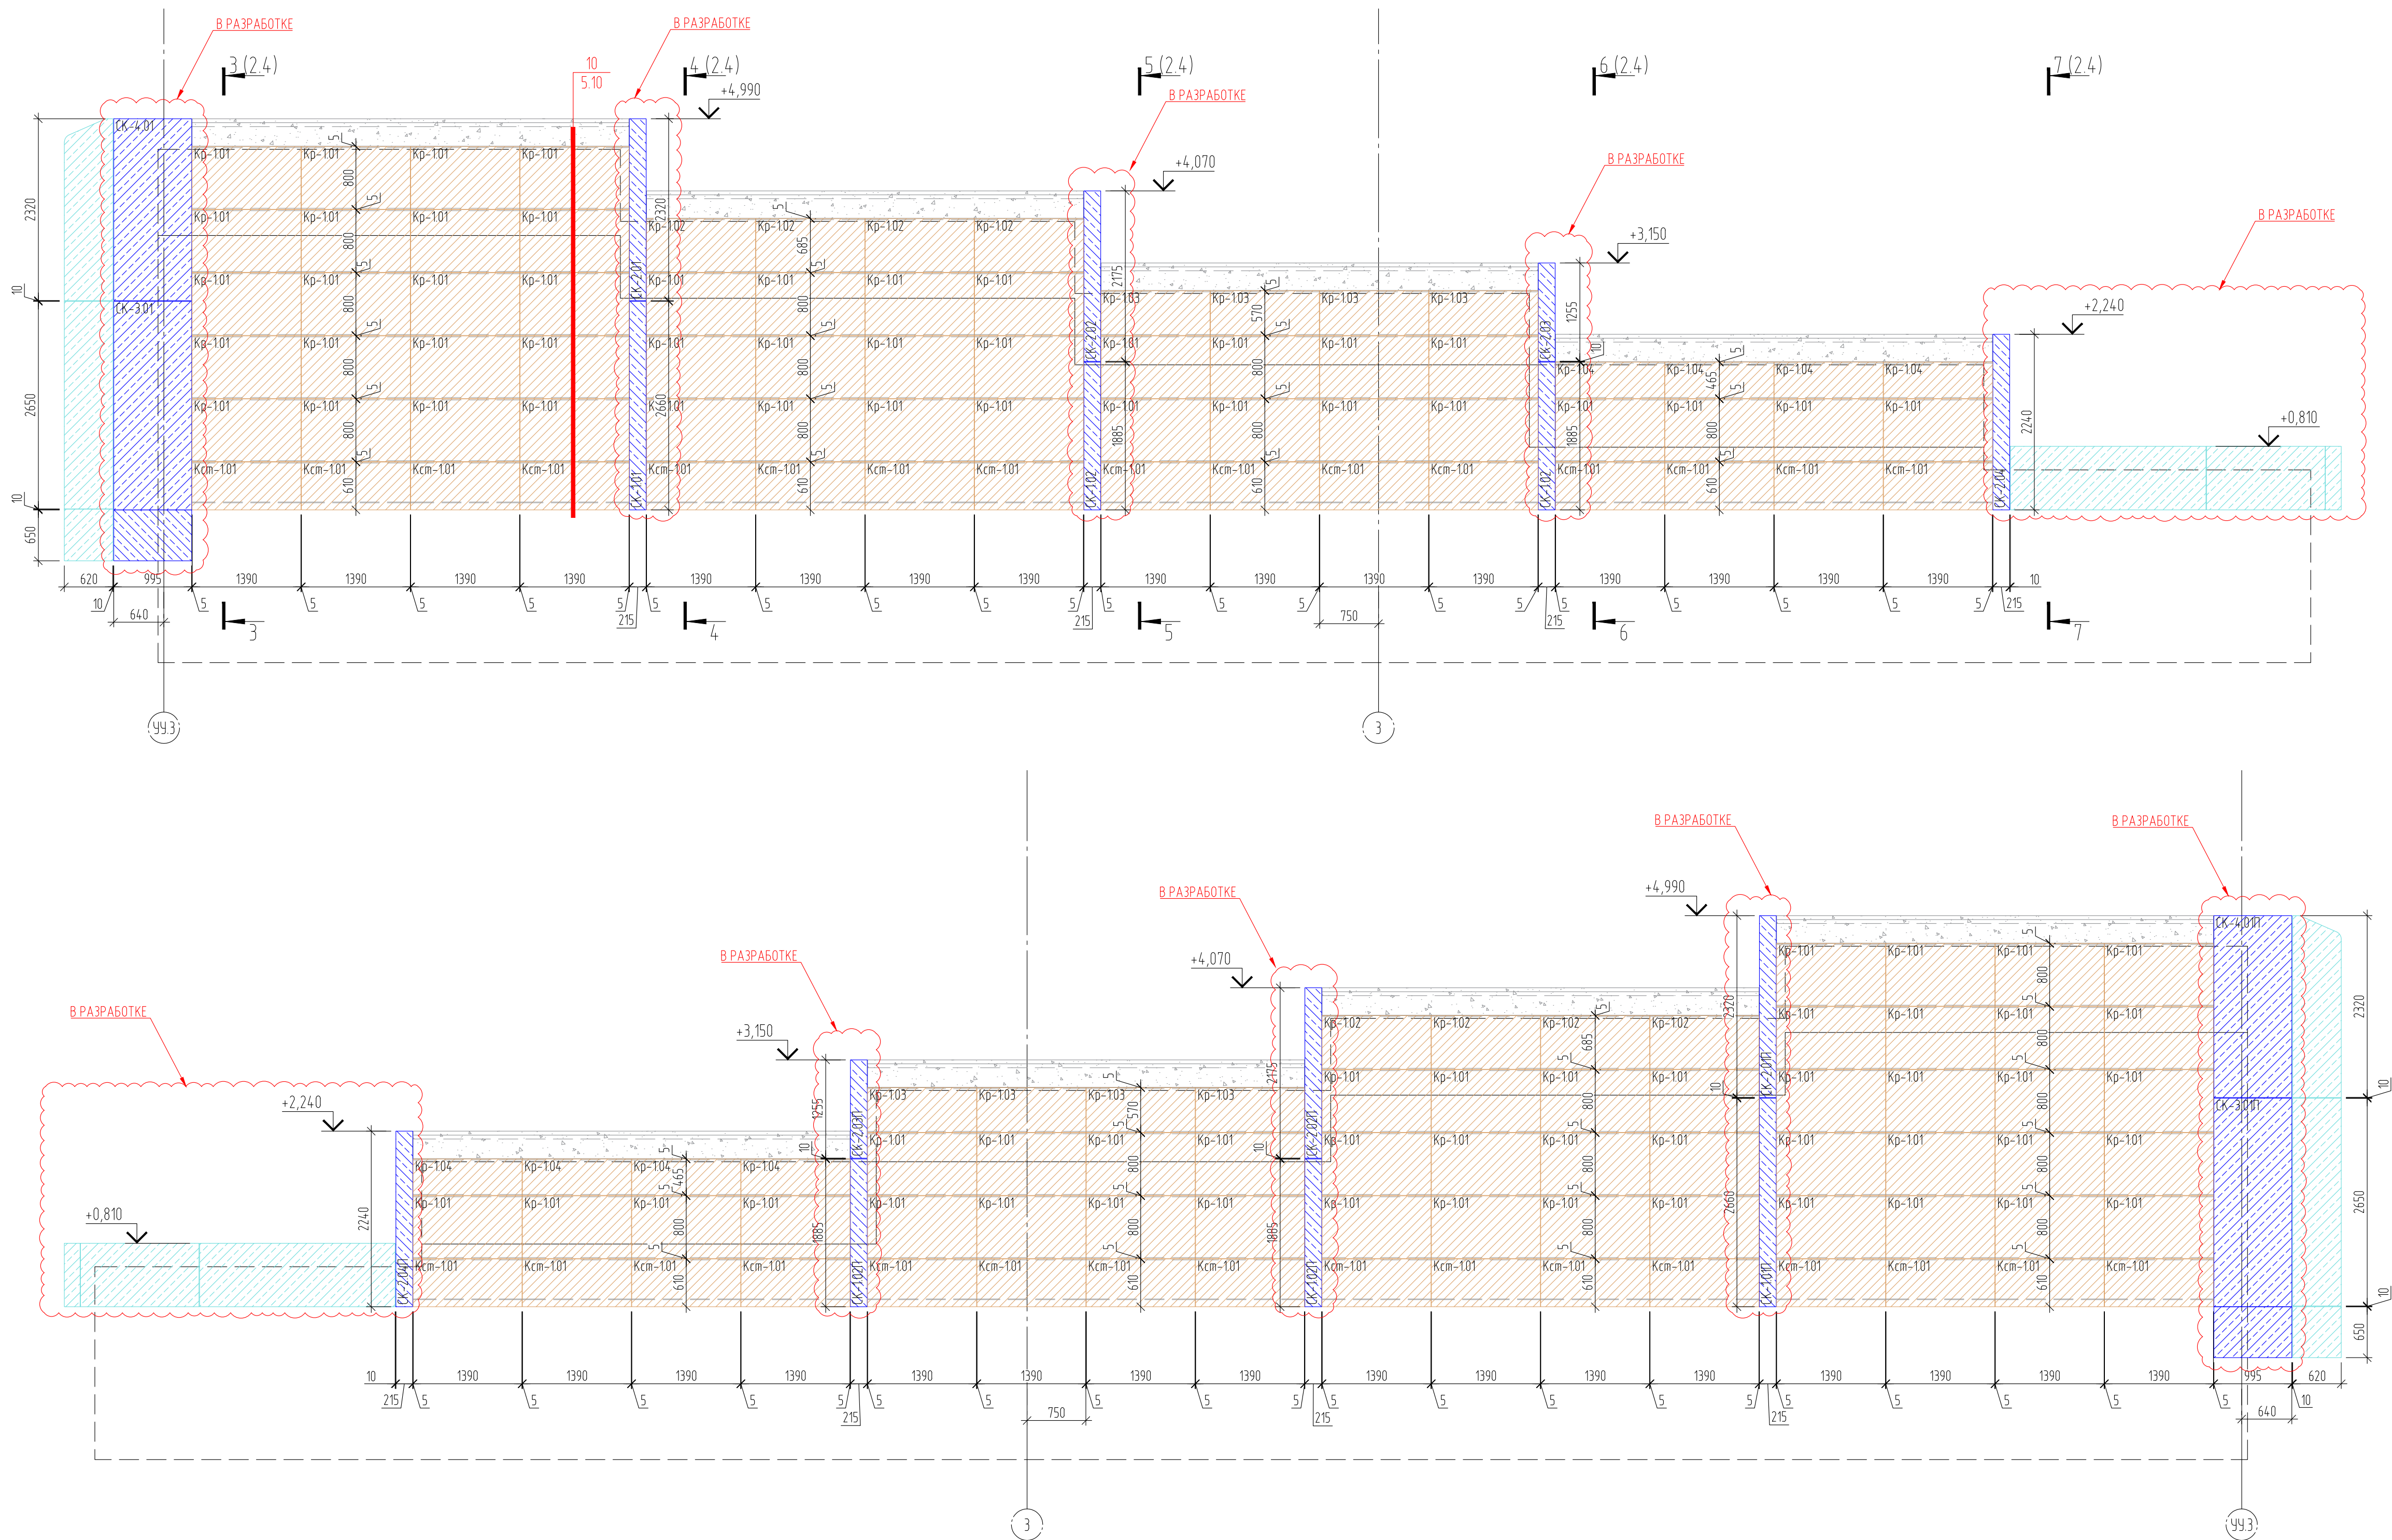

План-схема
М1:500

Условные обозначения	
Обозначение	Наименование
	Панель из стеклофибробетона (СФБ) RAL 9003
	Панель из стеклофибробетона (СФБ) RAL 7024
	Панель из стеклокомпозита (СКП) RAL 9003
	Натуральный камень 30 мм
	Чаша с элементами отлива (не входит в зону ответственности ООО "ДИАТ-ПРОЕКТ")

ДИАТ.4192.КМ1.РП-Д					
Многофункциональная комплексная жилая застройка, квартал 10, корпус 1, 2 по адресу: г. Москва, внутригородская территория муниципального округа Хорошево-Мневники, улица Нижние Мневники, земельный участок 14					
Изм.	Кол.уч.	Лист	№ док.	Подп.	Дата
Разработал	Яковичский				
ГИП					
Гл. констр.					
Утвердил					
Навесная фасадная система с воздушным зазором "ДИАТ" с облицовкой изделиями из стеклофибробетона (СФБ) и натурального камня				Стадия	Лист
Архитектурная раскладка фасада по оси АА.3 и ББ.3				Р	2.2
ООО "ДИАТ-ПРОЕКТ"				Формат А3х4	