



Тел: 8 (8553) 39-01-75, факс: 8 (8553) 39-01-97, e-mail: almat@tatar.ru, сайт: almetyevsk.tatar.ru

На № 26582 от 29.12.2025 г.

Решение
о согласовании архитектурно-градостроительного облика
объекта капитального строительства
от 14.01.2026 № 146и

По результатам рассмотрения проекта, в рамках предоставления муниципальной услуги по выдаче решения о согласовании архитектурно-градостроительного облика объекта капитального строительства, исполнительным комитетом Альметьевского муниципального района принято решение о согласовании архитектурно-градостроительного облика объекта капитального строительства «Склад металлопродукции» адресу: РТ, г. Альметьевск, ул. Базовая, д. 44.

Кадастровый номер земельного участка 16:45:040104:3626, имеет следующие основные параметры:

- Площадь уточненная: 13 450 кв. м;
- Разрешенное использование: Производственная деятельность;
- Форма собственности: Частная.

Основные параметры объекта капитального строительства:

- Общая площадь: 480 кв. м;
- Площадь надземной части: 480 кв. м;
- Этажность: 1 этаж.

Архитектурно-градостроительный облик объекта капитального строительства соответствует требованиям к архитектурно-градостроительному облику объекта капитального строительства, указанным в Правилах землепользования и застройки МО «город Альметьевск», утв. решением Альметьевского городского Совета от 21.05.2025г. № 175.

Приложение: материалы архитектурно-градостроительного облика объекта капитального строительства на 30 л.

Руководитель исполнительного
комитета района

А.М. Каюмов



ДОКУМЕНТ ПОДПИСАН
ЭЛЕКТРОННОЙ ПОДПИСЬЮ

СВЕДЕНИЯ О СЕРТИФИКАТЕ ЭП

Сертификат: 72B7910073B243B64FD66B424BF097BC

Владелец: Каюмов Айдар Маратович

Действителен с 28.01.2025 до 28.04.2026

Специалист отдела архитектуры ИК АМР
Кутлахметова Диляра Рашидовна
+7-904-713-57-28, Dilyara.K@tatar.ru



ЗАКРЫТОЕ АКЦИОНЕРНОЕ ОБЩЕСТВО

ПК «ТАТСЕЛЬХОЗХИМПРОЕКТ»

423461, Татарстан, г. Альметьевск, ул. Ленина, д.83; т/ф: (8553)33-81-11; e-mail: tshp@tshp.ru
СРО-П-114-043.5-1607002392-14032016 от 14.03.2016

Заказчик: ООО «Деталь»

Объект: «Здание склада металлопродукции по адресу: Республика Татарстан, г. Альметьевск, ул. Базовая, д. 44»

ПРОЕКТНАЯ ДОКУМЕНТАЦИЯ

Раздел 3. «Объемно-планировочные и архитектурные решения»

Часть 3.1 «Архитектурно-градостроительный облик»

22/25 – Т – АР (АГО)

Том 3.1.

2025 г.

СОДЕРЖАНИЕ

Том 3.1 "Архитектурно-градостроительный облик"

I. Текстовая часть

1. Исходные документы для проектирования.
2. Пояснительная записка
 - 2.1. Сведения о функциональном назначении
 - 2.2. Информация о применении или неприменении типовой серии
 - 2.3. Источник финансирования
 - 2.4. Сведения о технико-экономических показателях объекта
 - 2.5. Сведения о транспортной и пешеходной доступности объекта
 - 2.6. Приложения
 - 2.6.1. Задание на проектирование

II. Графическая часть

3. Фотофиксация современного состояния земельного участка, на котором планируется создание объекта
 - Лист 1 – фото №1, фото №2
 - Лист 2 – фото №3, фото №4
 - Лист 3 – схема видовых точек
4. Схема планировочной организации земельного участка
 - 4.1. Ситуационный план размещения объекта. Общие данные. Лист ПЗУ-1.
 - 4.2. План размещения существующих и проектируемых объектов. Лист ПЗУ-2.
 - 4.3. План по планировке и благоустройству, озеленению и освещению. Лист ПЗУ-3.
 - 4.4. План организации рельефа территории. Лист ПЗУ-4.
 - 4.5. Сводный план инженерно-технического обеспечения. Лист ПЗУ-5.
5. Схема благоустройства временных проездов, проходов, мест хранения авто-транспорта.
 - 5.1. Строительный генеральный план, М – 1:500. Лист ПОС-2.
6. Схемы разверток фасадов по основным улицам (или по фасаду с главным входом) с отображением существующей застройки и элементов природного ландшафта в ортогональной проекции.

Взам. инв. №		Подп. и дата		5. Система связи: строительство временных проездов, проходов, мостов при наличии автотранспорта.					
				5.1. Строительный генеральный план, М – 1:500. Лист ПОС-2.					
				6. Схемы разверток фасадов по основным улицам (или по фасаду с главным входом) с отображением существующей застройки и элементов природного ландшафта в ортогональной проекции.					
Изм.	Кол.уч	Лист	№док	Подп.	Дата	22/25 – Т	АР (АГО)		
Изм.	Кол.уч	Лист	№док	Подп.	Дата	Архитектурно-градостроительный облик	Стадия	Лист	Листов
							П	1	
							ЗАО ПК		
							«Татсельхозхимпроект»		
							г. А		
Документ создан в электронной форме. № 146и от 14.01.2026. Исполнитель: Кутлахметова Д.Р.									

- 6.1. Фасад в осях 1-8. Паспорт отделки фасадов. Лист АР-1.
 - 6.2. Фасад в осях 8-1. Лист АР-2.
 - 6.3. Фасад в осях А-Б, Б-А. Лист АР-3
 - 6.4. Общий вид объекта. Лист АР-4.
 - 6.5. Фасад в осях 1-8 и А-Б (варианты 1, 2). Лист АР-5.
 - 6.6. Фасад в осях 1-8, А-Б, Б-А. Общий вид (вариант 3). Лист АР-6
 7. Схемы фасадов в ортогональной проекции
 - 7.1. План склада. Лист АР-1.
 - 7.2. Разрез 1-1. Лист АР-2.
 - 7.3. Фасад 1-8. Лист АР-3.
 - 7.4. Фасад 8-1. Лист АР-4.
 - 7.5. Фасад А-Б, Б-А. Лист АР-5.
 - 7.6. План кровли. Лист АР-6.
 8. Схемы фрагментов фасадов
- Смотри лист АР-5 (поз. 6.5) «Фасад в осях 1-8 и А-Б (варианты 1, 2)»

Ишв № подл	Подпись и дата	Взам ишв №						
						22/25- Т	АР (АГО)	Лист
								2
Изм.	Лист	№ докум.	Подпись	Дата				

1. Текстовая часть

Проектная документация выполнена на основании нижеследующих документов:

- задание на проектирование;
- Градостроительный план земельного участка № РФ-16-4-45-1-04-2025-0508-0 от 31.08.2025 г.
- Инженерные изыскания, выполненные ООО «АльГеоМарк» в 2025г.

2. Пояснительная записка

2.1. сведения о функциональном назначении объекта

Проектируемое здание производственного назначения предназначено для временного хранения металлопродукции с максимальным весом до 5,0 тонн; для выгрузки или загрузки предусмотрен мостовой кран грузоподъемностью 5,0 тонн.

Класс по функциональной пожарной опасности – Ф5.2.

Категория помещений по взрывопожарной и пожарной опасности – «Д».

Согласно пункта 12, подпункта 5 ГПЗУ, требования к подсветке фасадов объекта капитального строительства не установлены.

2.2. Информация о применении или неприменении типовой серии

Разработан индивидуальный проект.

2.3. Источник финансирования

Источник финансирования строительства объекта – собственные средства инвесторов.

2.4. Сведения о технико-экономических показателях объекта

Технические показатели проектируемого объекта рассчитаны согласно приложению «А» СП 56.13330.2021 «Свод правил. Производственные здания» и сведены в нижеследующую таблицу:

№№ п/п	Наименование	Единицы измерения	Количество	Примечания
1	Площадь этажа	кв.м.	480,0	п. А2
2	Общая площадь здания	кв.м.	480,0	п. А1
3	Площадь застройки	кв.м.	490,0	п. А3
4	Количество этажей	шт.	1	п. А4
5	Высота этажа (средняя)	м.	7,85	-
6	Строительный объем	куб.м.	3849,6	п. А5

Изм. №	Лист	№ докум.	Подпись	Дата	22/25- Т	АР (АГО)	Лист
							3

2.5. Сведения о транспортной о пешеходной доступности объекта

Проектируемое здание расположено на территории действующей производственной базы, по адресу: РТ, г. Альметьевск, ул. Базовая, з/у 44. К базе имеется проезд от улицы Базовая с твердым покрытием. Заезд на территорию осуществляется только через КПП.

Пешеходная доступность осуществляется от остановки автобуса №8 до КПП производственной базы, ориентировочная протяженность составляет 320 м. По улице Базовая проложена велосипедная дорожка совмещенная с тротуаром.

Или № подл	Подпись и дата	Взлм или №						Лист	
			22/25- Т					АР (АГО)	4
Изм.	Лист	№ докум.	Подпись	Дата					

Техническое задание

для выполнения проектных работ по объекту: "Здание оклада металлопродукции по адресу:
Республика Татарстан, г. Альметьевск, ул. Базовая, д. 44, строение №6"

№/п	Перечень основных данных и требований	Описание основных данных и требований
1	2	3
1	Наименование заказчика и его адрес	ООО «Деталь» Адрес: 423458, РТ, Альметьевский МР, город Альметьевск, ул. Базовая, д. 44, строение 5. Эл. почта – detalmet2018@yandex.ru
2	Генеральная проектная организация	ЗАО ПК "Татсельхозхимпроект" 423461, Республика Татарстан, г. Альметьевск, ул. Ленина, 83 тел/факс (8553)33-81-11
3	Генеральная подрядная организация	На основе торгов подряда
4	Источник финансирования	Собственные средства
5	Расположение участка	Участок расположен в южной части города, в промышленной зоне по улице Базовая города Альметьевск. Земельный участок расположен южнее главного производственного корпуса и офисного здания. До начала проектных работ выполнить инженерные изыскания (геодезические и геологические).
6	Стадийность проектирования	Проектная документация (в объеме для получения разрешения на строительство).
7	Требования к генеральному плану и трудоустройству	Разобрать генплан участка с учетом требований действующих нормативных документов и утвержденного градостроительного плана земельного участка. Подъездные дороги, отсыпки и площадки принять асфальтобетонными. Со стороны ворот здания предусмотреть площадку для временной автостоянки.
8	Требования к технологии	Объект предназначен для хранения металлопродукции с мостовым краном до 5 тонн. Категория помещений по взрывопожарной и пожарной опасности – «Д». Количество работников – 4 чел. Вспомогательные бытовые помещения имеются на расстоянии до 50 м. Режим работы – односменный, круглогодичный. Использование труда инвалидов и МГН не предусматривается. Разработка раздела: "Технологические решения" не требуется.
9	Требования к архитектурно-планировочным решениям	Проектом предусмотреть строительство каркасного одноэтажного здания, состоящее из двух блоков размерами 36×12 и 12×12 м, высотой до низа ферм – 6,4 м. Здание принять отапливаемым.

10	Требования к конструктивным решениям	Проектом предусмотреть: - <u>фундаменты</u> - буронабивные сваи; - <u>наружные стены</u> - из сэндвич-панелей; - <u>колонны</u> - из профильных труб по ГОСТ 30245-2003 заводского изготовления; - <u>перегородки</u> - из профнастила по стальным направляющим с заполнением полости мин. ватой; - <u>крыша</u> - двухскатная с кровлей из сэндвич-панелей по металлической ферме из профильных труб; - <u>ворота</u> - автоматические, утепленные шириной 3,6 м, высотой 4,2 м. - <u>окна</u> - из ПВХ профиля с 2х камерным стеклопакетом; - <u>двери наружные</u> - по типу "Гардиан" (утепленные); - <u>полы</u> - бетонные с износостойким покрытием;
11	Требования к инженерному оборудованию	Внутреннее инженерное оборудование и наружные подводящие сети выполняются отдельным проектом на стадии "Рабочая документация", согласно техническим условиям владельцев инженерных сетей.
12	Сроки строительства	2025-2026 г.
13	Очередность проектирования и строительства	В одну очередь
14	Требования к проектной документации	Проектную документацию выполнить в объеме для получения разрешения на строительство нижеследующих разделов: • пояснительная записка; • схема планировочной организации земельного участка; • объемно-планировочные и архитектурные решения; • конструктивные решения; • проект организации строительства. Содержание разделов выполнить согласно постановлению Правительства РФ от 16.02.2008 №87.
15	Дополнительные условия	Проектную документацию выдать в 2-х экземплярах в бумажном виде и 1 экз. на электронном носителе.

ЗАДАНИЕ СОСТАВИЛИ

От заказчика

Главный инженер

ООО «Деталь»

Р.С. Мингатын /
«_____» _____ 2025 г.



От проектной организации

Главный инженер проектов

ЗАО ПК «Татсельхозхимпроект»

М.Т. Минабутдинов /
«_____» _____ 2025 г.





Фото 1. (09.09.2025)



Изм.	Кол.	уч.	Лист	№ док.	Подп.

Фотофиксация

22-25-

Лист
1

Фото2. (09.09.2025)



Фото 3. (09.09.2025)



Фото 4. (09.09.2025)


Изм.	Кол.	уч.	Лист	№ док.	Подп.

Фотофиксация

22-25-

Лист

2

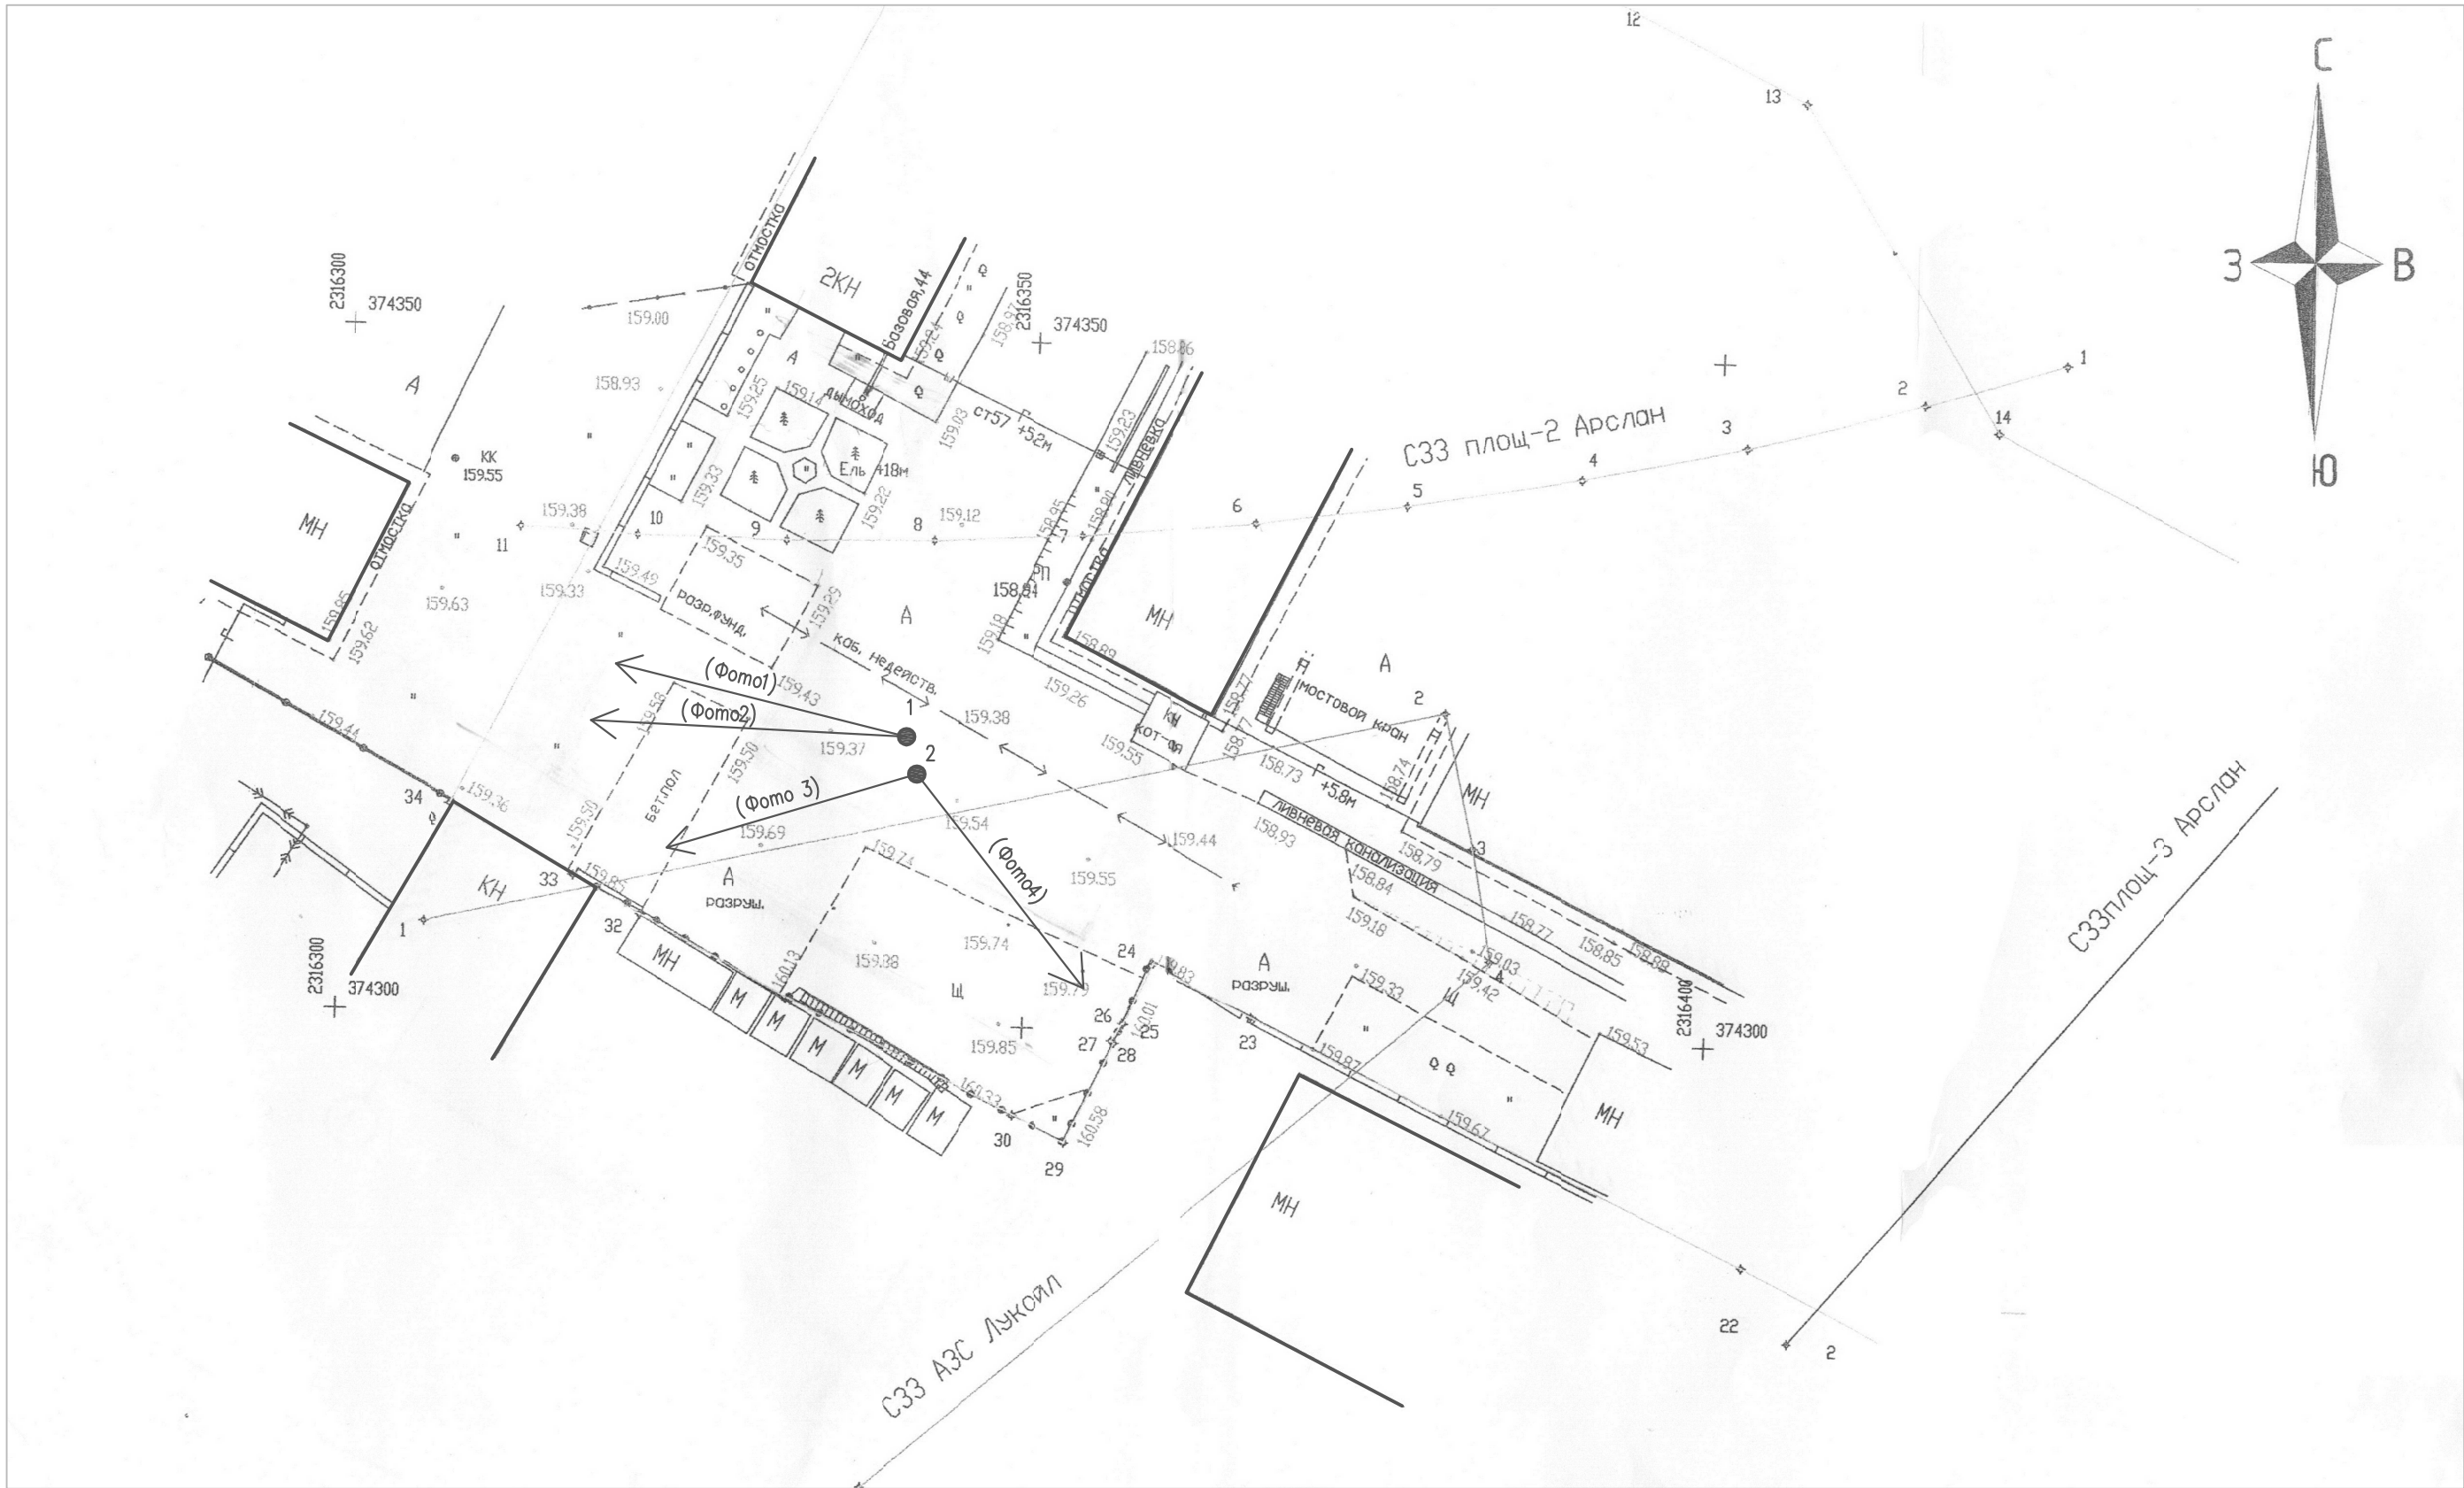

					22/25-Т			АГО							
					Здание склада металлопродукции по адресу: Республика Татарстан, г. Альметьевск, ул. Базовая, д.44, строение №6										
Изм.		Лист		докум.		Подп.		дата		Архитектурно-градостроительный облик Схема видовых точек					
ГАП		Минабутдинов											Стадия	Лист	Листов
Тех. контр.		Ишуков											П		
Разработал		Мирхайдаров													
									ЗАО ПК "Татсельхозхимпроект" г. Альметьевск						

Ситуационный план



Объект проектирования

Общие указания

1. Проектная документация объекта: "Здание склада металлопродукции по адресу: Республика Татарстан, г. Альметьевск, ул. Базовая, д.44." на основании:
 - задания на проектирование;
 - инженерно-топографического плана выполненного ООО "АльГеоМарк" в сентябре 2025г.
 - нормативных документов по строительству, действующих в РФ и РТ.
 - градостроительного плана на земельный участок РФ-16-4-45-1-04-2025-0508-0 от 31.08.25г.
2. Система координат МСК-16
3. Система высот Балтийская
4. Все размеры и отметки даны в метрах.
5. Строительно-монтажные и земляные работы выполняемые, в охранной зоне инженерных сетей, осуществлять в присутствии представителей от организаций, в чьем ведении они находятся.
6. Графические условные обозначения даны согласно – ГОСТ 21.508-2020, ГОСТ 21.204-2020, ГОСТ Р 21207-97, ГОСТ 2.306-68, , ГОСТ 2.303-68.
Условные обозначения, отличные от ГОСТ, приведены на чертежах.
7. Производство и приемку строительно-монтажных работ производить согласно требованиям:
 - СП49.13330.2010 "Безопасность труда в строительстве Ч.1. Общие требования";
 - СП48.13330.2019 "Организация строительства"
 - СП 78.13330.2012 "Автомобильные дороги." Актуализированная редакция СНиП 3.06-03-85;
 - СП 82.13330.2016 "Благоустройство территорий" Актуализированная редакция СНиП III-10-75.

Ведомость рабочих чертежей основного комплекта ПЗУ

Лист	Наименование	Примечание
1	Общие данные. Ситуационный план размещения объекта.	
2	План размещения существующих и проектируемых объектов. М 1:500	
3	План по планировке, благоустройству, озеленению и освещению.	
4	План организации рельефа территории. М 1:500	
5	Сводный план инженерно-технического обеспечения. М 1:500	

Ведомость ссылочных и прилагаемых документов

Обозначение	Наименование	Примечание
Ссылочные документы		
ГОСТ 21.204-2020	Условные графические обозначения и изображения элементов генеральных планов и сооружений транспорта	
СП 42.13330.2016	"Градостроительство. Планировка и застройка городских и сельских поселений"	
СП 18.13330.2019	"Производственные объекты. Планировочная организация земельного участка"	
СП 82.13330.2016	"Благоустройство территорий"	

Технико – экономические показатели по участку

N n/p	Наименование	Ед. изм.	Количество
1	Площадь земельного участка территории КН 16:45:040104:3626	га	1.3450
2	Площадь земельного участка в условной границе проектирования	м²	1036.0
3	Площадь застройки в условной границе проектирования	м²	490.00
4	Площадь покрытия в условной границе проектирования	м²	227.00
5	Площадь зеленой зоны	м²	319.00

						22/25–Т		ПЗУ	
						Здание склада металлопродукции по адресу: Республика Татарстан, г. Альметьевск, ул. Базовая, д.44.			
Изм.	Кол.уч.	Лист	N док.	Подп.	Дата	Здание склада	Стадия	Лист	Листов
							П	1	5
ГИП	Шакирова					Общие данные. Ситуационный план размещения объекта	ЗАО ПК		
Тех. контроль	Ишуков А.К.						"Татсельхозхимпроект"		
Проектировал	Губайдуллина								

Согласовано

Взам инв. N

Подп. и дата


Инв. N подл.

Согласовано

Взам инв. N

Подп. и дата


Инв. N подл.

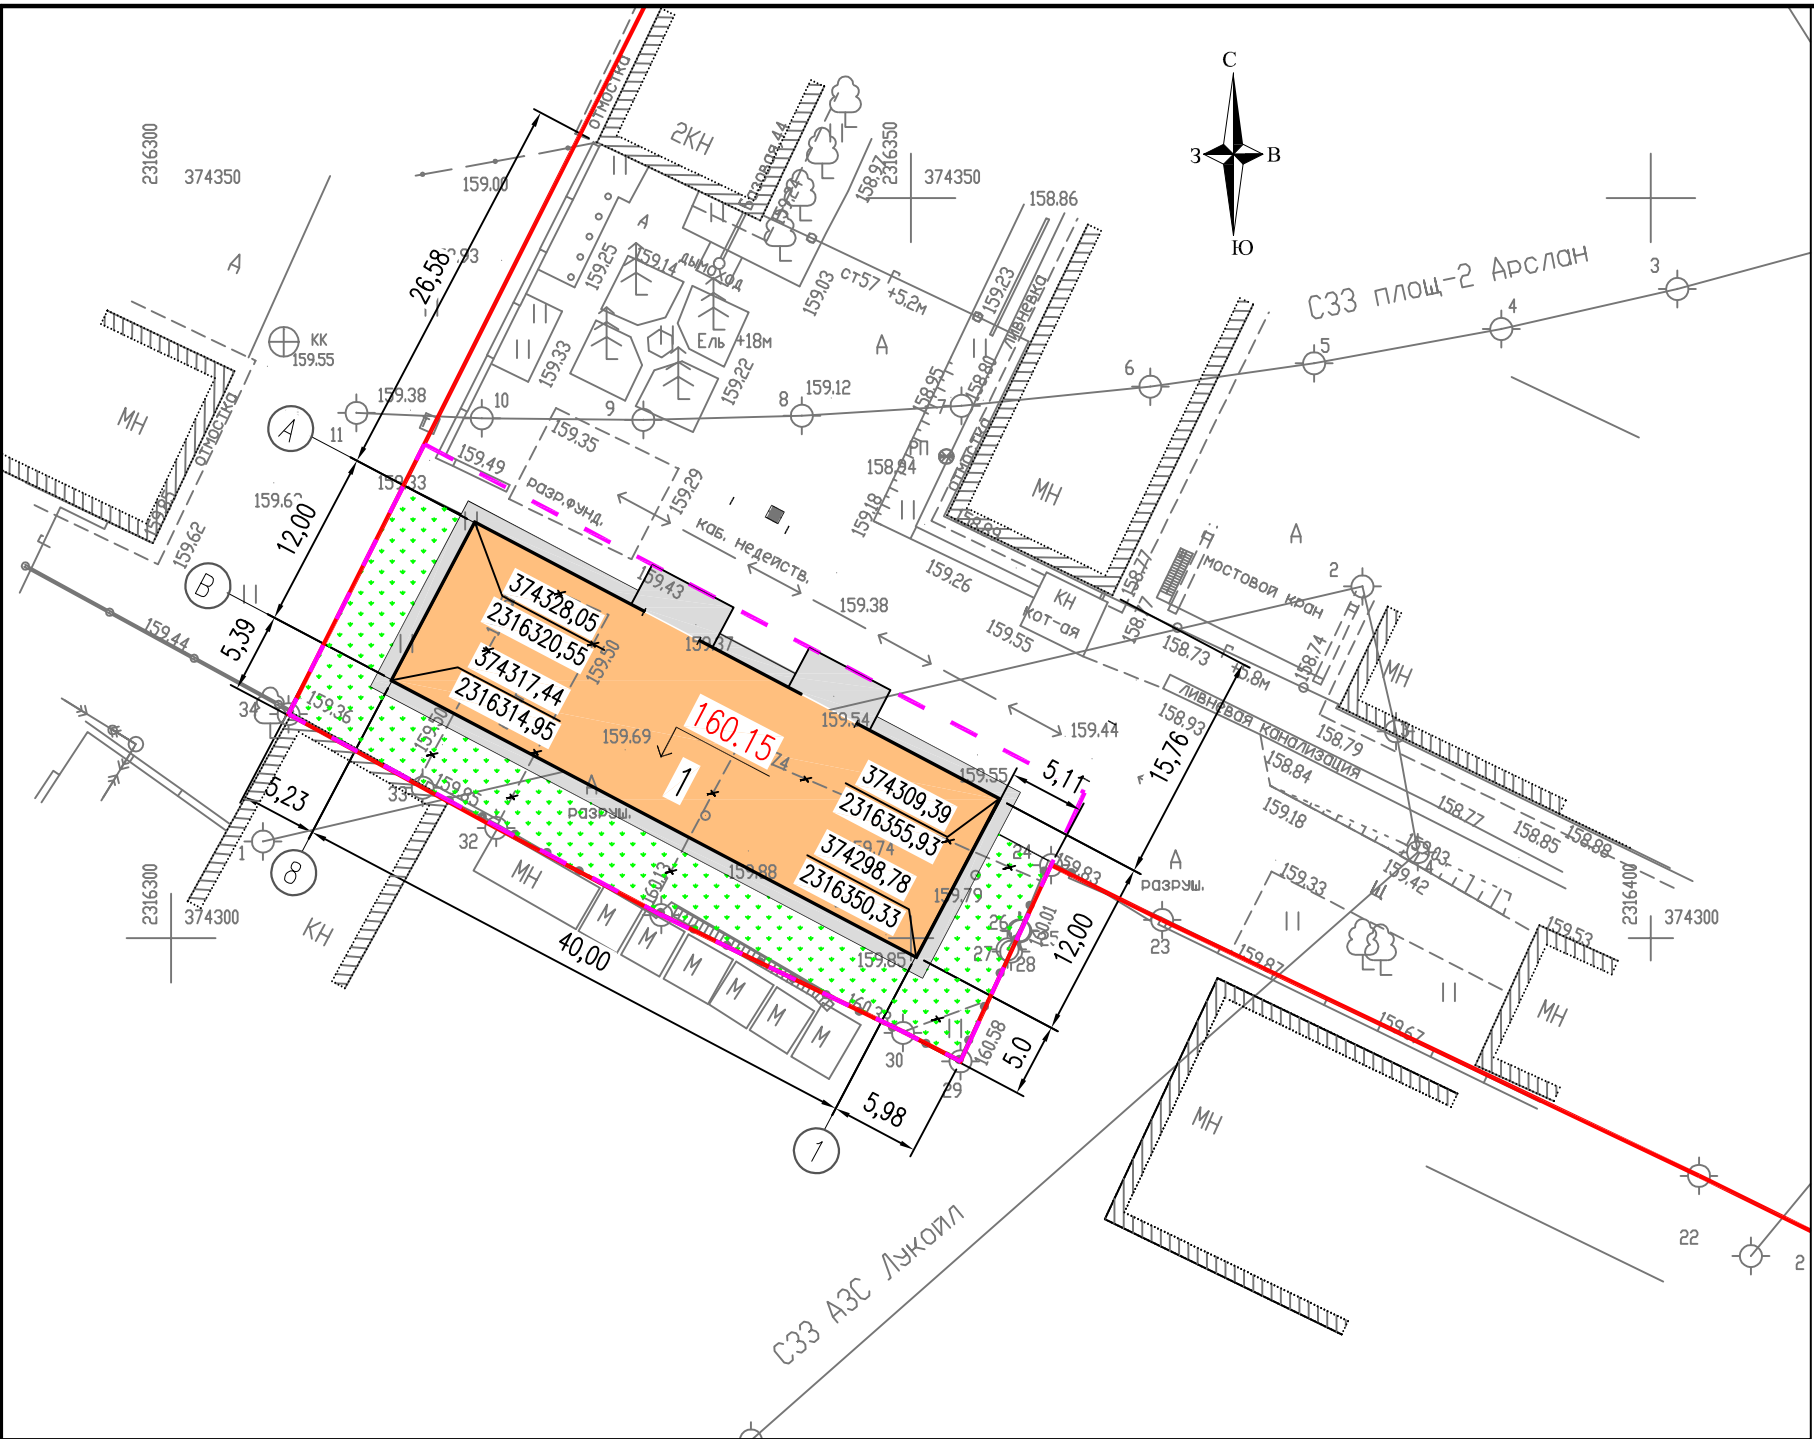

Экспликация зданий и сооружений

Номер на плане	Наименование	Примечание
1	Здание склада металлопродукции	проект.

						22/25-Т		ПЗУ	
						Здание склада металлопродукции по адресу: Республика Татарстан, г. Альметьевск, ул. Базовая, д.44.			
Изм.	Кол.уч.	Лист	N док.	Подп.	Дата				
						Здание склада		Стадия	Лист
								П	2
ГИП	Шакирова					План размещения существующих и проектируемых объектов М 1:500		ЗАО ПК "Татсельхозхимпроект"	
Тех. контроль	Ишуков А.К.								
Проектировал	Губайдуллина								

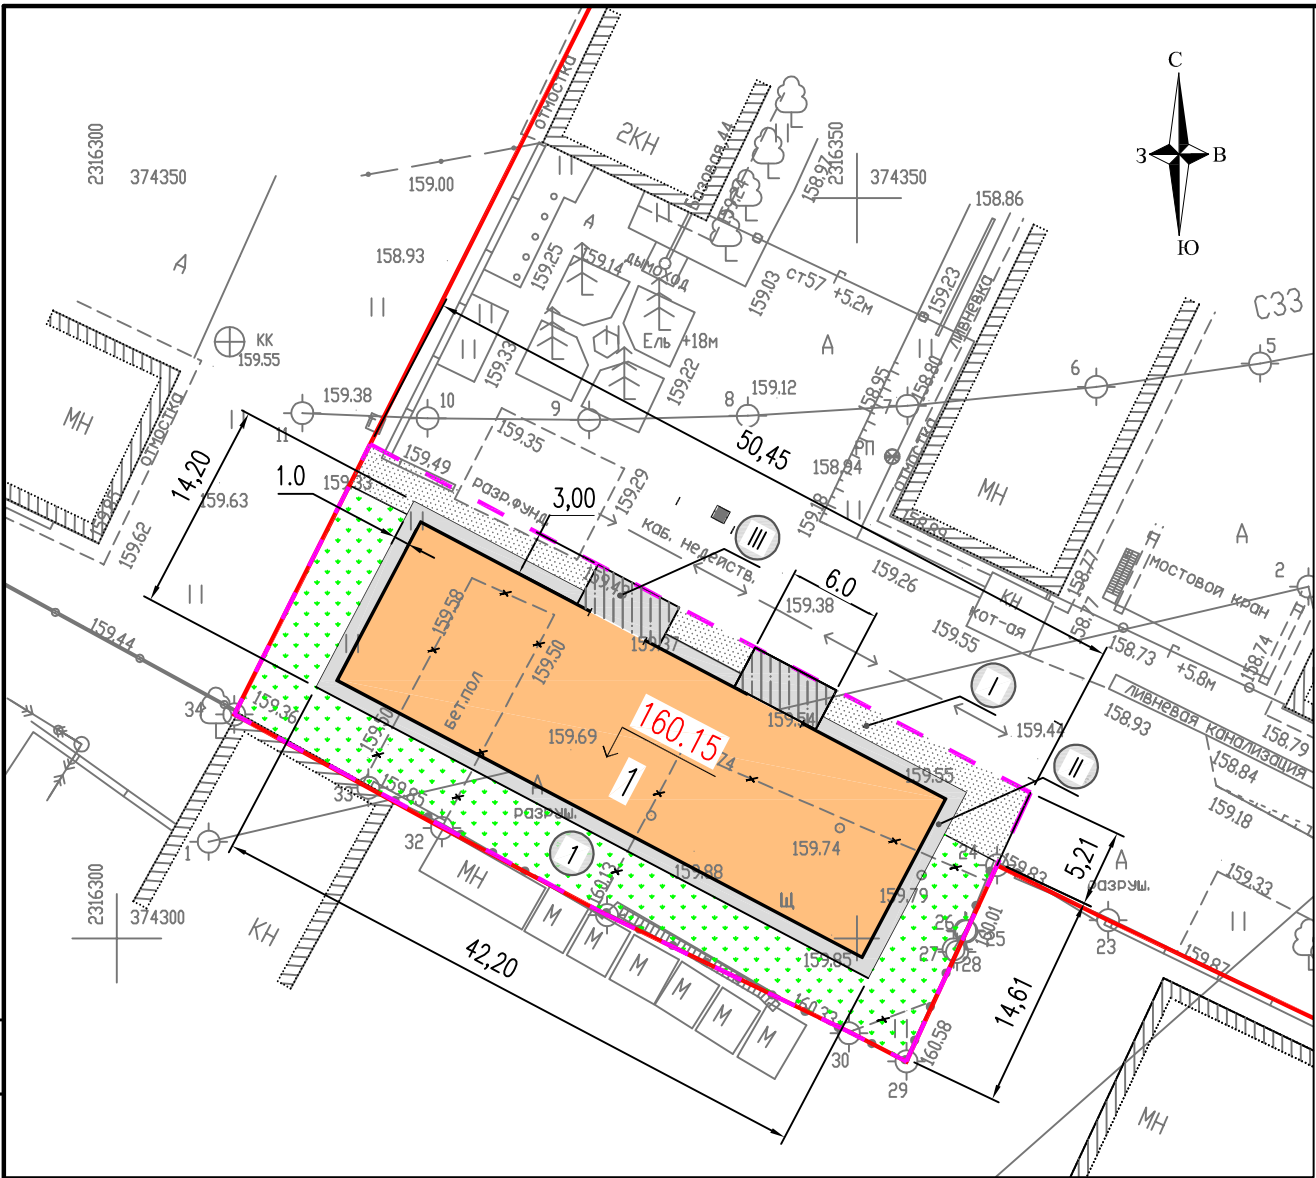

Конструкция покрытия Тип А-1

Асфальтобетон плотный м/з, Тип Б, М1 на ПБВ 60 ГОСТ 9128-2013	– 0,05м
Асфальтобетон плотный м/з, Тип Б, М1 ГОСТ 9128-2013	– 0,07м
Щебень М800 ГОСТ 8257-2014	h–0,30м
Песок крупнозернистый ГОСТ 32824-2014	h–0,30м
Уплотненный грунт	Купл.–0,98

Конструкция покрытия Тип Б-1

Мелкозернистый асфальтобетон	h–0,05м
Монолитный цементобетон марки В20	ГОСТ 26633-2012
h–0,15м (армированный сеткой арматуры Ф–4мм, ячейка 50х50)	
Геотекстиль Geoflax ТН-33	
Песок средне-зернистый ГОСТ 8736-2014	h–0,20м
Уплотненный грунт	Купл.–0,98

Конструкция покрытия Тип А-2

Мелкозернистый асфальтобетон	h–0,05м
Щебень М400 ГОСТ 8257-2014	h–0,15м
Песок среднезернистый ГОСТ 32824-2014	h–0,10м
Геотекстиль "Dorpix"	
Уплотненный грунт	Купл.–0,98

Условные обозначения

	Граница земельного участка
	Линия застройки земельного участка
	Проектируемое здание
	Существующие здания
	Покрытие въездного пандуса (проект.)
	Покрытие а/бетонное (проектное)
	Проектируемое покрытие отмостки
	Зеленая зона земельного участка
	Разборка существующих покрытий

Ведомость проездов, тротуаров, дорожек и площадок

N (поз.)	Наименование	Тип	Площадь покрытия м²	Примечание
I	Площадь дорожного покрытия	А-1	93.00	
II	Площадь покрытия отмостки	А-2	98.00	
III	Площадь покрытия въездных пандусов	Б-1	36.00	

Покрытие въездных пандусов (для автотранспорта) Б-1
Ведомость элементов озеленения

Поз	Наименование	Ед. изм.	Возр. лет	Кол-во	Примечание
1	Зеленая зона (раст. грунт h–0.15м)	м²	–	319.00	

						22/25-Т			ПЗУ			
						Здание склада металлопродукции по адресу: Республика Татарстан, г. Альметьевск, ул. Базовая, д.44.						
Изм.	Кол.уч.	Лист	N док.	Подп.	Дата	Здание склада			Стадия	Лист	Листов	
									П	3		
ГИП	Шакирова					План по планировке, благоустройству, озеленению и освещению. М 1:500			ЗАО ПК "Татсельхозхимпроект"			
Тех. контроль	Ишуков А.К.											
Проектировал	Губайдуллина											

Согласовано

Взам инв. N

Подп. и дата


Инв. N подл.

Согласовано

Взам инв. N

Подп. и дата

Инв. N подл.

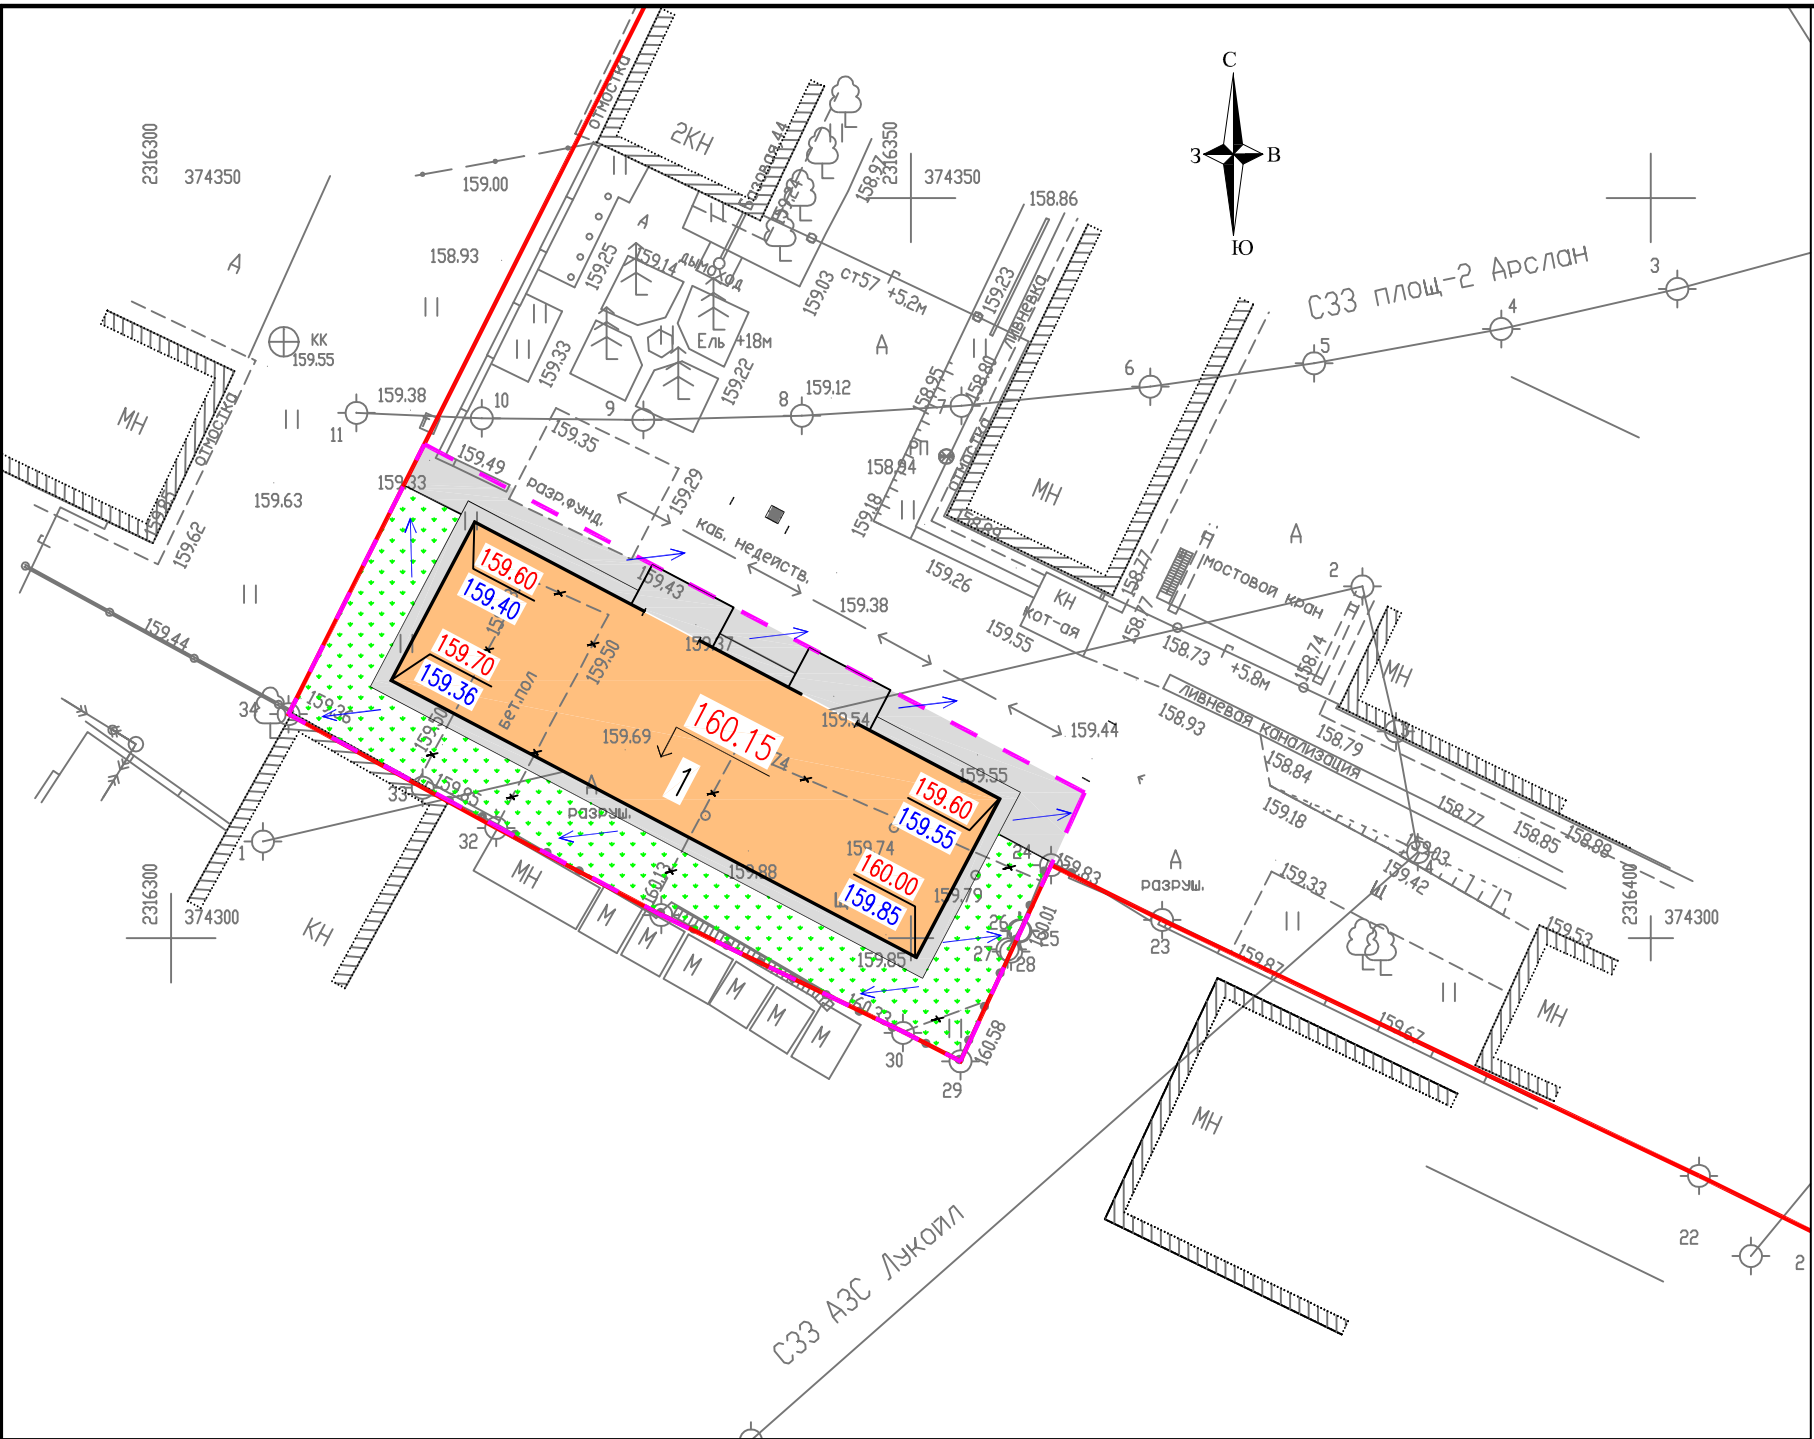

Условные обозначения


- Граница земельного участка
- Условная граница проектирования
- Проектируемое здание
- Существующие здания
- Проектируемое покрытие
- Зеленая зона
- Разборка существующих покрытий
- 159.60 Отметка низ отмостки
- 159.55 Существующая отметка рельефа
- 160.15 Отметка пола
- Направление поверхностного водоотвода

Экспликация зданий и сооружений

Номер на плане	Наименование	Примечание
1	Здание склада металлопродукции	проект.

						22/25-Т		ПЗУ		
						Здание склада металлопродукции по адресу: Республика Татарстан, г. Альметьевск, ул. Базовая, д.44.				
Изм.	Кол.уч.	Лист	N док.	Подп.	Дата	Здание склада		Стадия	Лист	Листов
								П	4	
ГИП	Шакирова					План организации рельефа территории. М 1:500		ЗАО ПК "Татсельхозхимпроект"		
Тех. контроль	Ишуков А.К.									
Проектировал	Губайдуллина									

Согласовано					
Инв. N подл.	Подп. и дата	Взам инв. N			

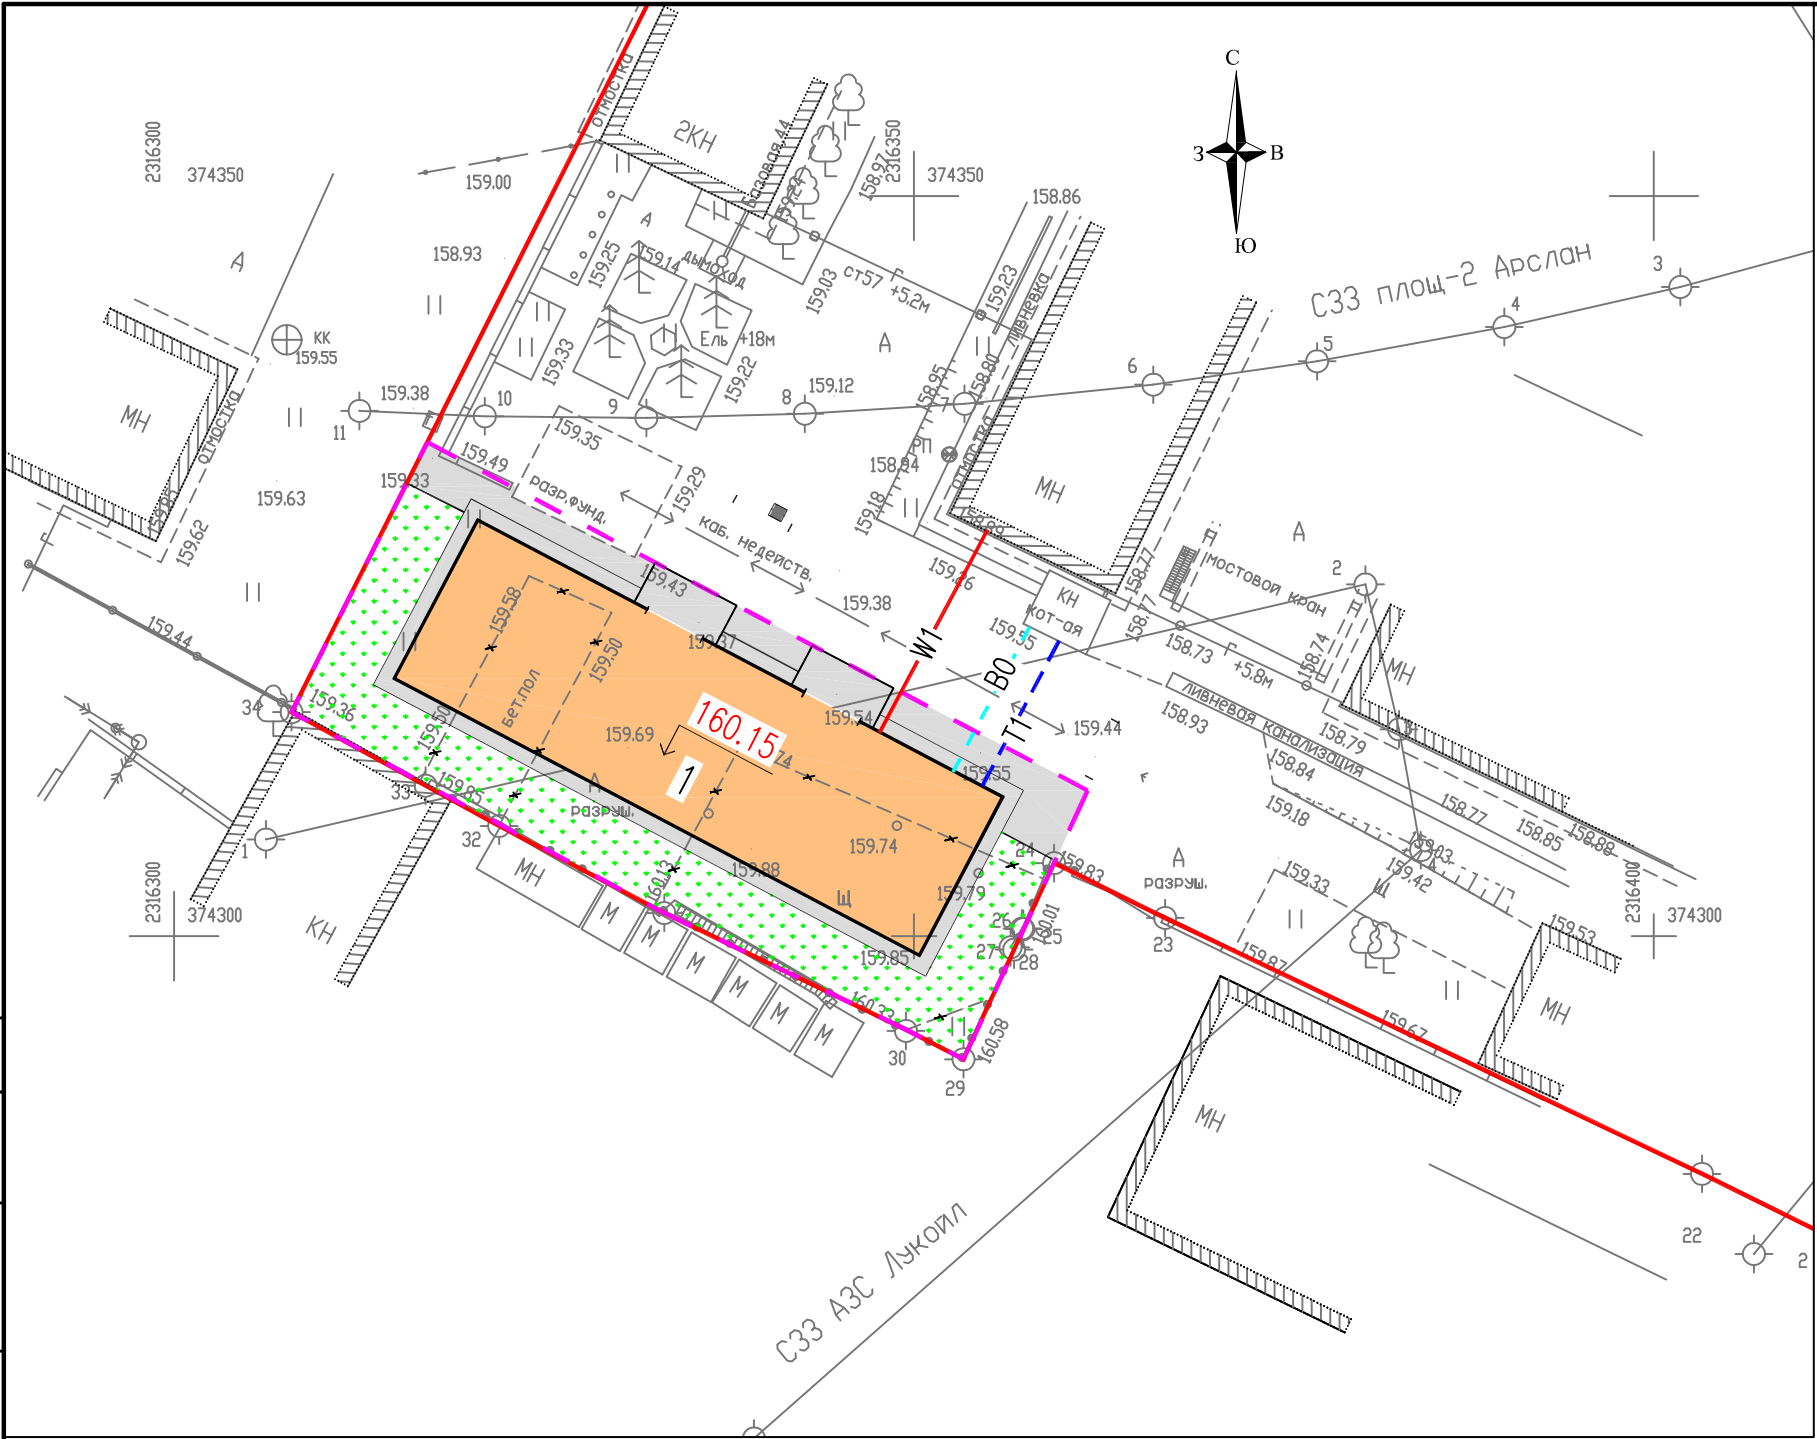

Условные обозначения

- Граница земельного участка
- Условная граница проектирования
- Проектируемое здание
- Существующие здания
- Проектируемое покрытие
- Зеленая зона
- Подводящая линия водоснабжения B0
- Проектируемая линия теплоснабжения T1
- Подводящая кабельная линия электроснабжения 0.4 кВ от существующего здания W1

Экспликация зданий и сооружений

Номер на плане	Наименование	Примечание
1	Здание склада металлопродукции	проект.


						22/25-Т		ПЗУ		
						Здание склада металлопродукции по адресу: Республика Татарстан, г. Альметьевск, ул. Базовая, д.44.				
Изм.	Кол.уч.	Лист	N док.	Подп.	Дата			Стадия	Лист	Листов
						Здание склада		П	5	
ГИП	Шакирова					Сводный план инженерно-технического обеспечения. М 1:500		ЗАО ПК "Татсельхозхимпроект"		
Тех. контроль	Ишуков А.К.									
Проектировал	Губайдуллина									

Согласовано

Взам инв. N

Подп. и дата

Инв. N подл.

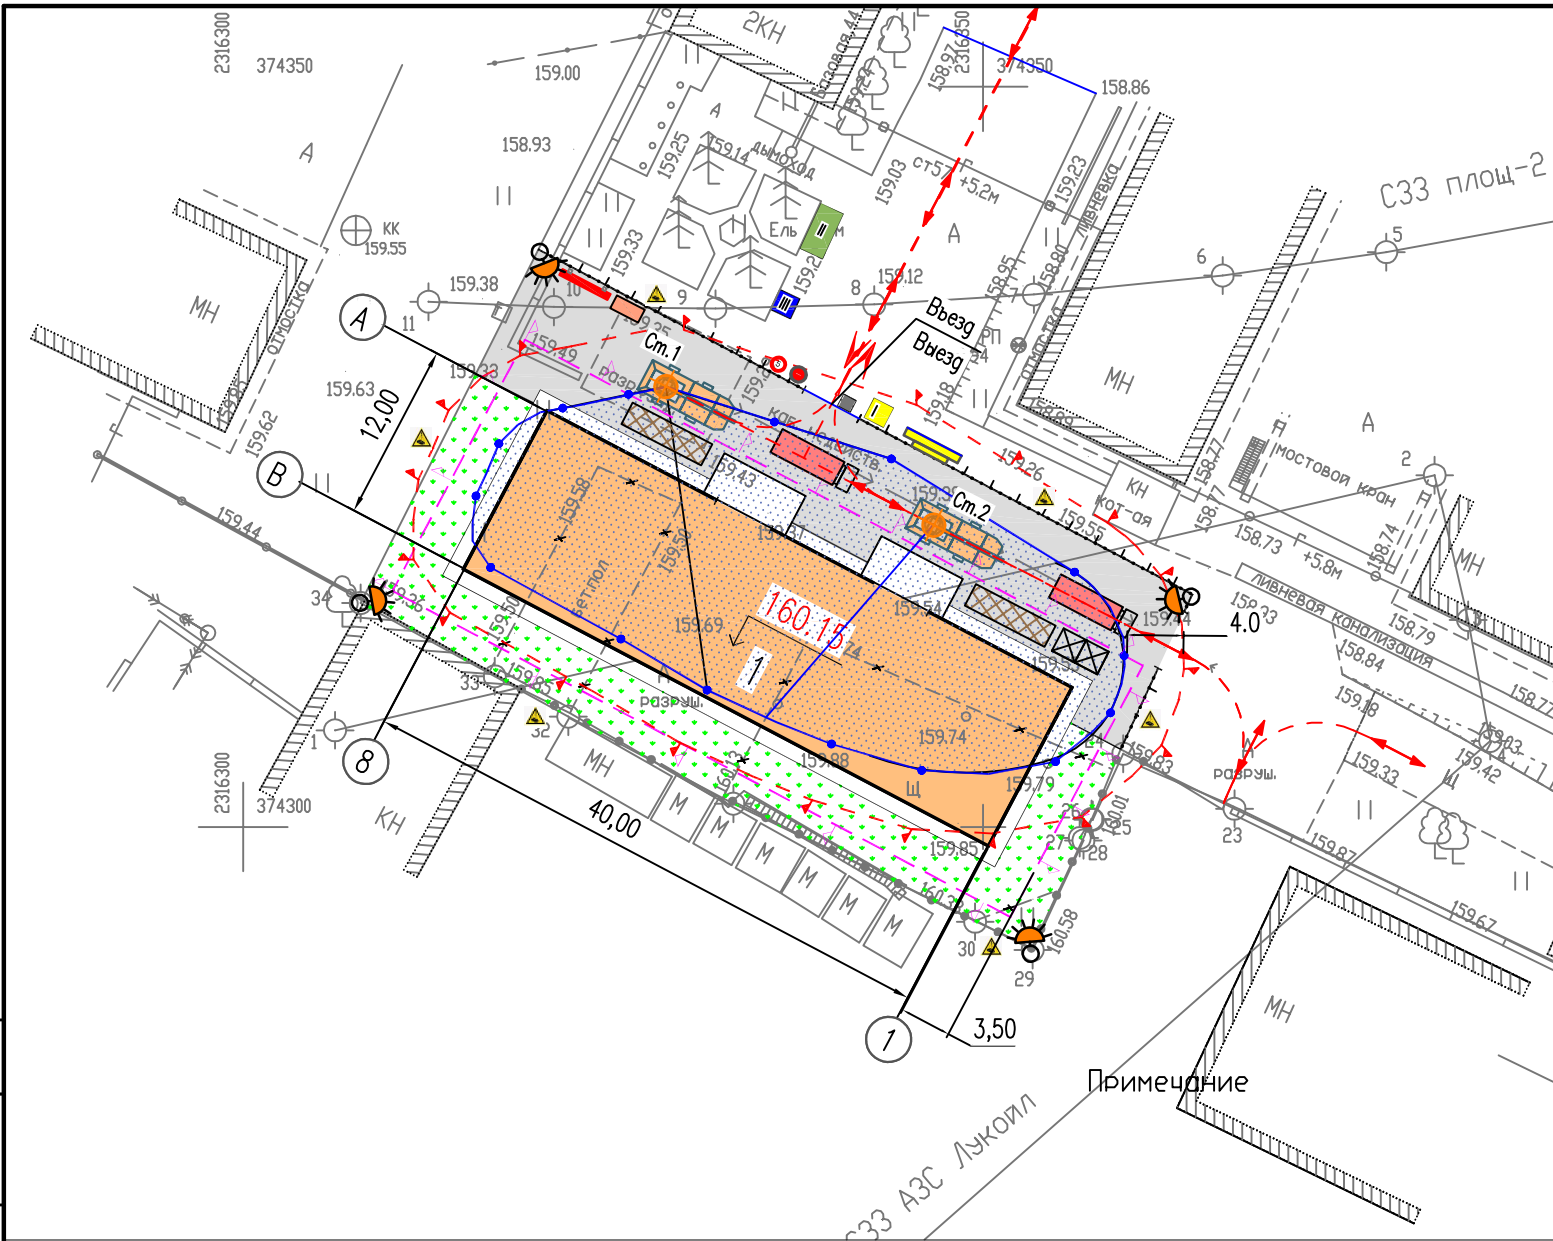

Примечание

Экспликация зданий и сооружений

Номер на плане	Наименование	
1	Здание склада металлопродукции	проект.


Экспликация временных зданий и сооружений

N на плане	Наименование	Габариты м	Колич-во шт	Примечание (усл. обозн.)
I	КПП		1	■
II	Административно-бытовой вагончик		2	■
III	Биотуалет		1	■

Условные обозначения

	Ограждение строительной площадки
	Линия ограничения действия крана
	Границы опасной зоны при перемещении груза краном
	Линия границы опасной зоны при падении предмета со здания
	Рабочая зона крана
	Контейнеры для строительного и бытового мусора
	Прожектор наружного освещения территории строительства
	Знак "Вход (проход) запрещен!"
	Знак ограничения максимальной скорости
	Автомобильный кран
	Автомобильный транспорт
	Место складирования грузов (временно)
	Устройство для мойки колес (установка для сухой чистки колес)
	Стоянка крана
	Паспорт объекта
	Въезд, выезд
	Противопожарный щит
	Ящик с песком
	Направление движения автотранспорта на стройплощадке
	Щебеночное покрытие стройплощадки (частично а/бетонное)
	Знак осторожно работает кран
	Устройство для мойки колес (установка для сухой чистки колес)

Фасад в осях 1-8

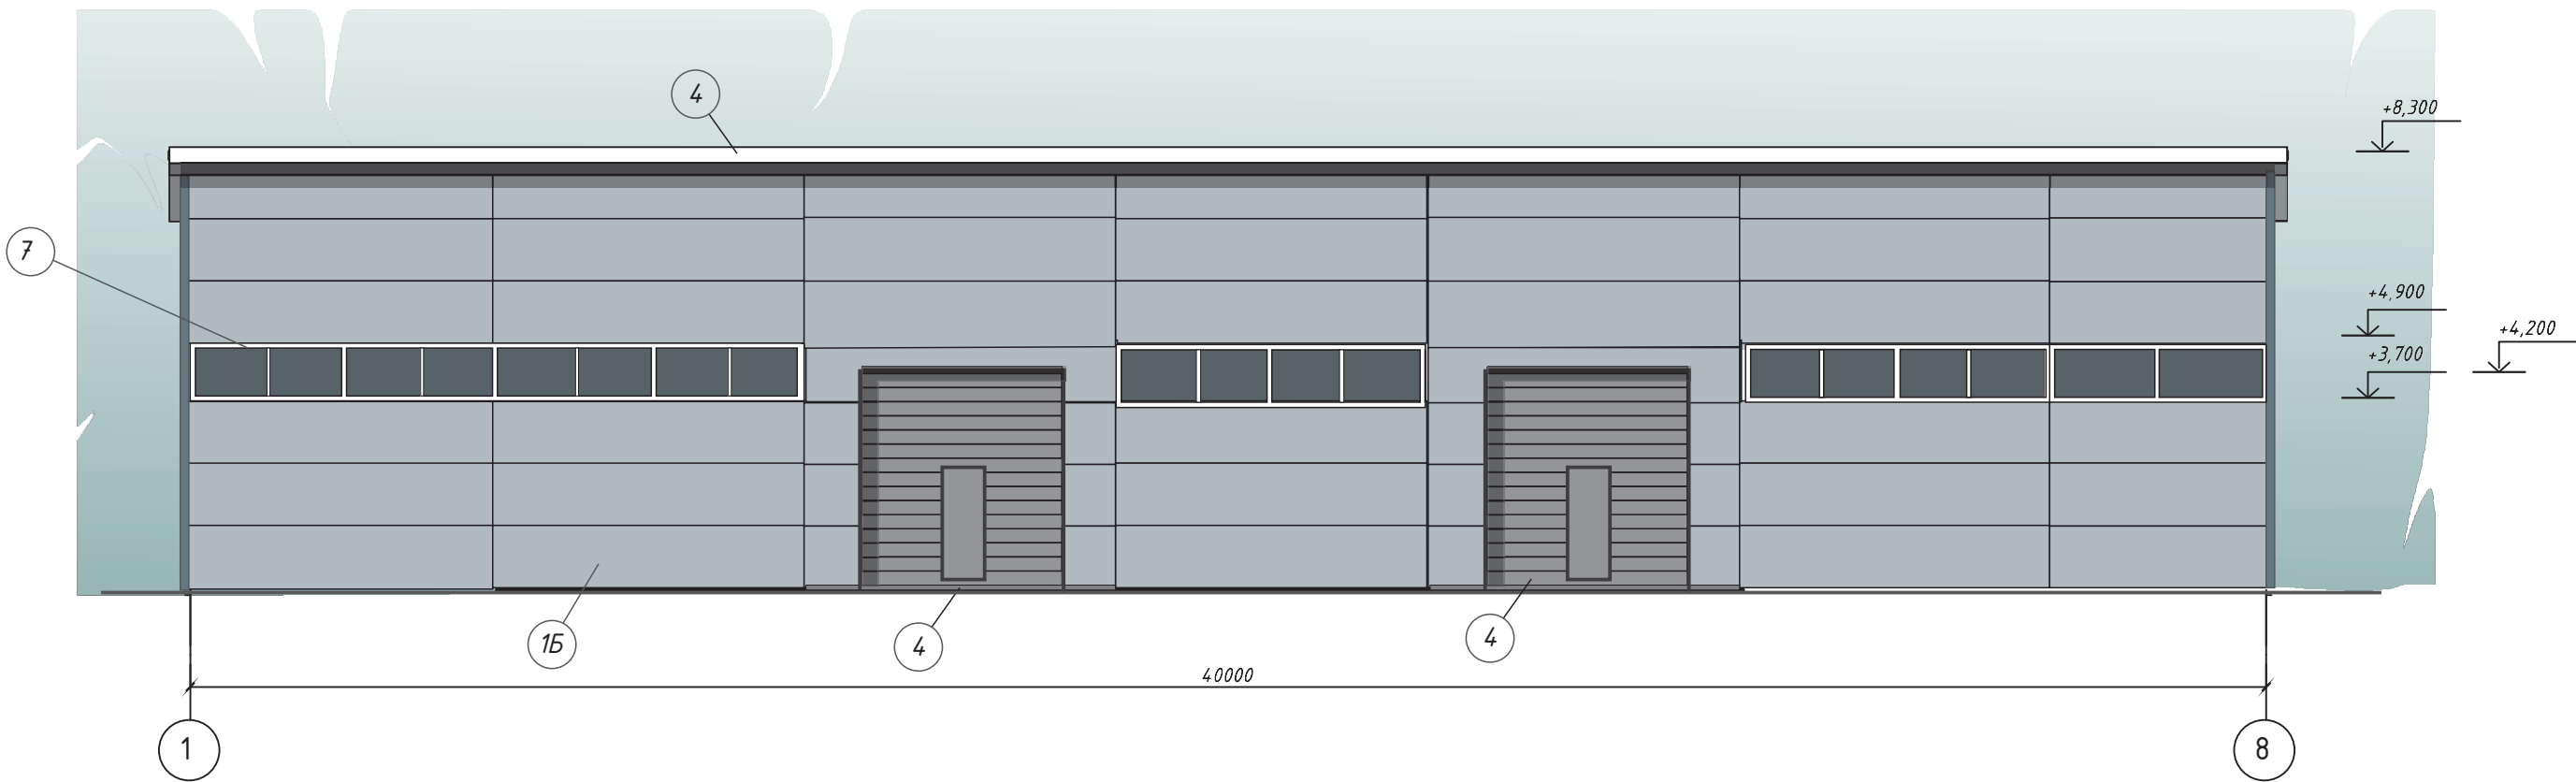


Паспорт отделки фасадов



п/п	Элемент фасада	Вид отделки и материалы	Колер/RAL
1	2	3	4
1	Наружные стены	-трехслойные сэндвич-панели полной заводской готовности с покрытием полиэстером	RAL 9003 сигнальный белый
			RAL 7004 сигнальный серый
2	Цоколь	Сталь g=0,55мм по каркасу полной заводской готовности с покрытием полиэстер	RAL 7024 графитовый серый
3	Слив оконных проемов		RAL 7004 сигнальный серый
4	Лицевая поверхность экрана на фасаде в осях 1-8	Козырек навеса - металлические кассеты полной заводской готовности по мет. каркасу;	RAL 7024 графитовый серый
5	Входные двери,ворота	из алюминиевого профиля типа "Татпроф"	RAL 7024 графитовый серый
6	Металлические элементы фасада, кровли	Сталь g=0,55мм полной заводской готовности с покрытием полиэстер	RAL 9003 сигнальный белый
7	Оконные переплеты	из профиля ПВХ	RAL 9003 сигнальный белый

						22-25-Т-АР			
						Здание склада металлопродукции по адресу : Республика Татарстан ,г. Альметьевск,ул. Базовая,д44,строение №6			
Изм.	Кол.уч.	Лист	№ док	Подп.	Дата	Архитектурные решения	Стадия	Лист	Листов
							П	1	
ГАП		Минабутдинов							
Н.контр		Ишуков А.К.				Фасад в осях 1-8 Паспорт отделки фасадов	ЗАО ПК «Татсельхозхимпроект» г. Альметьевск		
Разработал		Минабутдинов							

Фасад 8-1

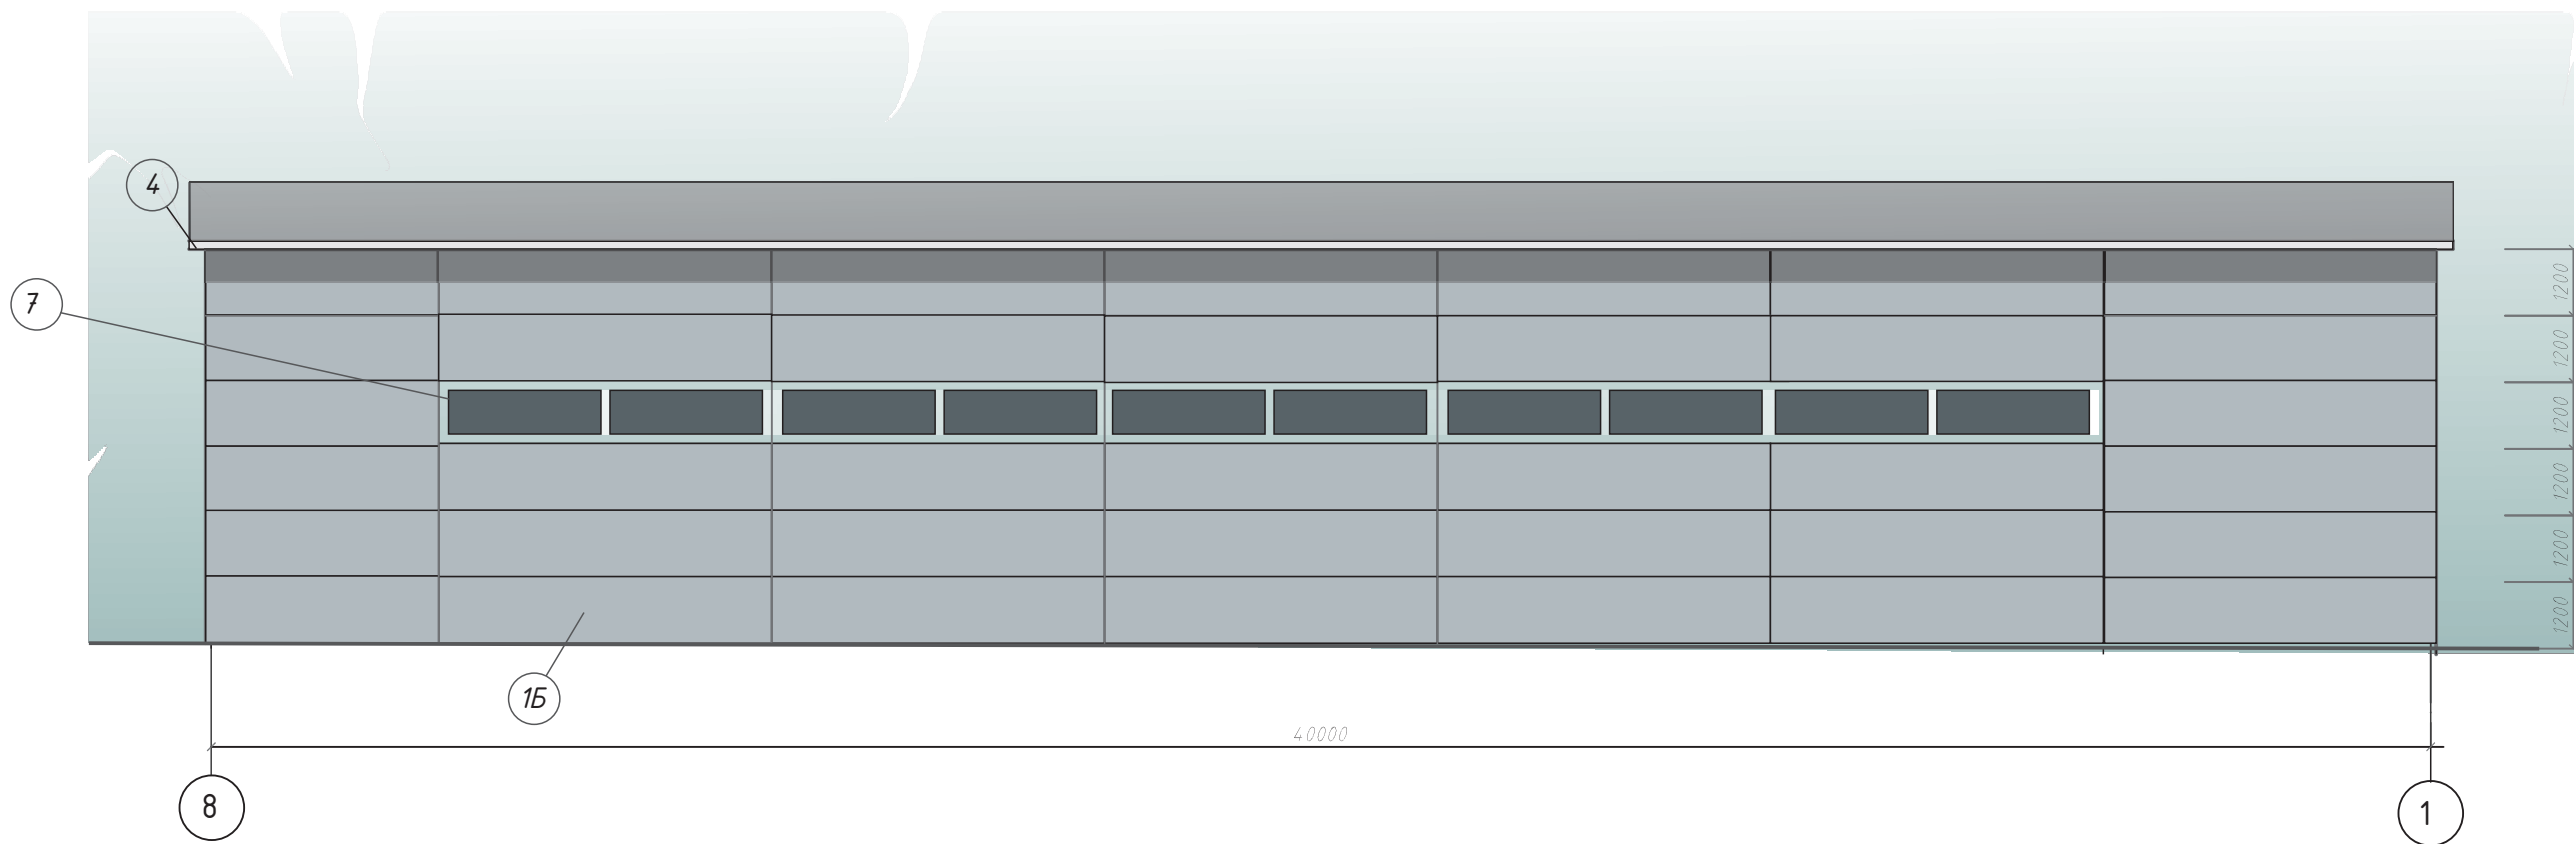

						22-25-Т-АР					
						Здание склада металлопродукции по адресу : Республика Татарстан ,г. Альметьевск,ул. Базовая,д44,строение №6					
Изм.	Кол.уч.	Лист	№ док	Подп.	Дата	Архитектурные решения			Стадия	Лист	Листов
									П	1	
ГАП		Минабутдинов				Фасад в осях 8-1			ЗАО ПК «Татсельхозхимпроект» г. Альметьевск		
Н.контр		Ишуков А.К.									
Разработал		Минабутдинов									

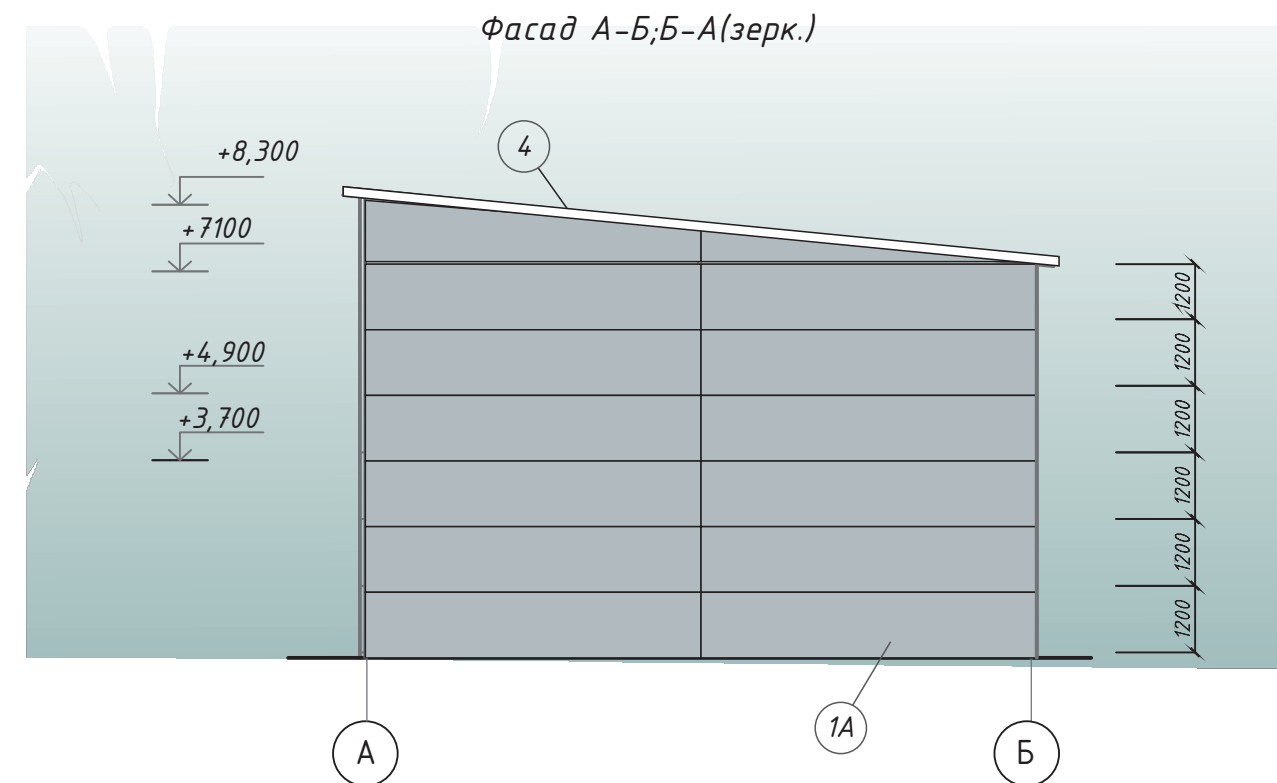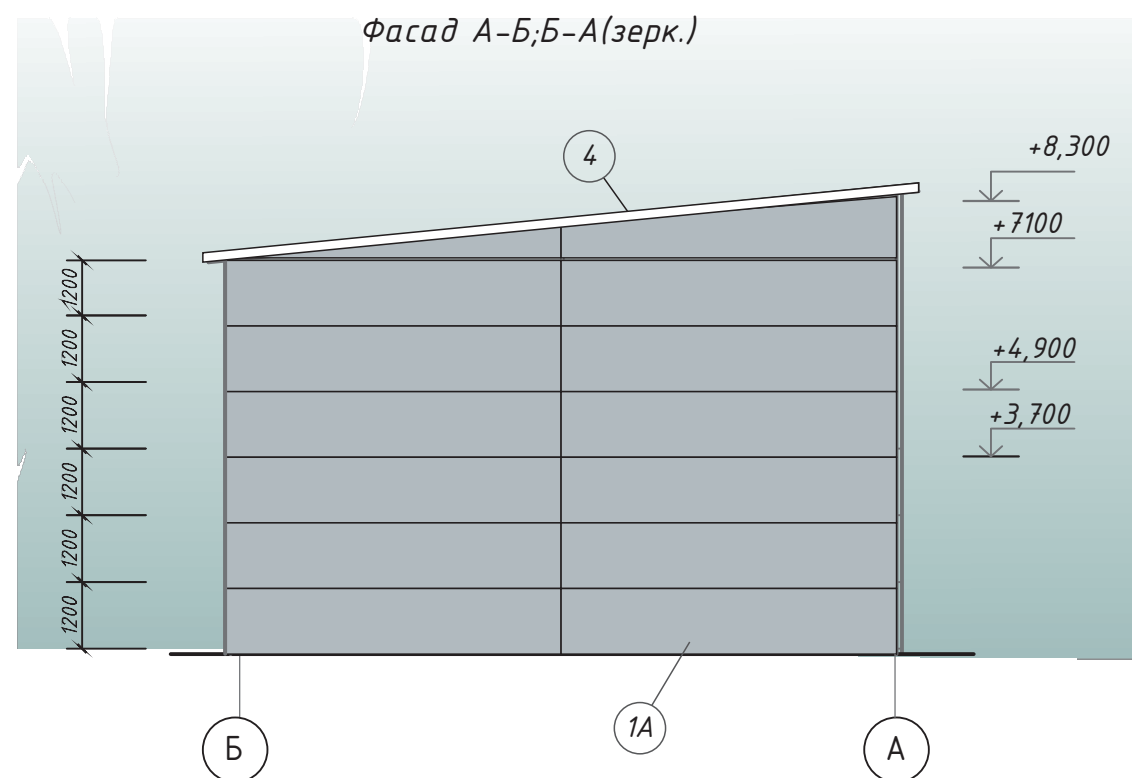


						22-25-Т-АР			
						Здание склада металлопродукции по адресу : Республика Татарстан ,г. Альметьевск,ул. Базовая,д44,строение №6			
Изм.	Кол.уч.	Лист	№ док	Подп.	Дата				
						Архитектурные решения	Стадия	Лист	Листов
							П	1	
ГАП		Минабутдинов				Фасад А-Б;Б-А(зерк.)	ЗАО ПК «Татсельхозхимпроект» г. Альметьевск		
Н.контр		Ишуков А.К.							
Разработал		Минабутдинов							

Общий вид объекта




						22-25-Т-АР			
						Здание склада металлопродукции по адресу : Республика Татарстан ,г. Альметьевск,ул. Базовая,д44,строение №6			
Изм.	Кол.уч.	Лист	№ док	Подп.	Дата	Архитектурные решения	Стадия	Лист	Листов
							П	1	
ГАП		Минадутдинов				Общий вид объекта	ЗАО ПК «Татсельхозхимпроект» г. Альметьевск		
Н.контр		Ишуков А.К.							
Разработал		Минадутдинов							


Фасад в осях 8-1 (вариант1)

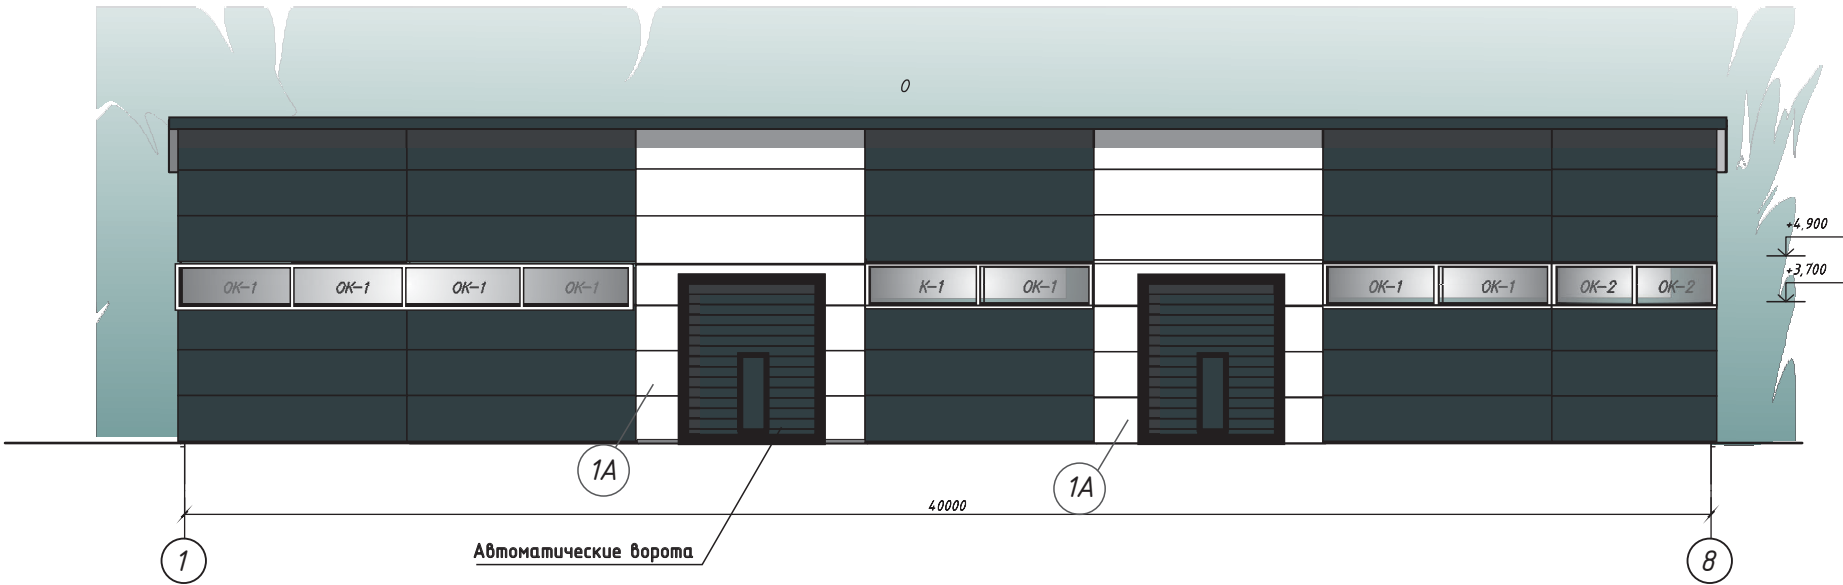


Фасад в осях 1-8 (вариант 2)

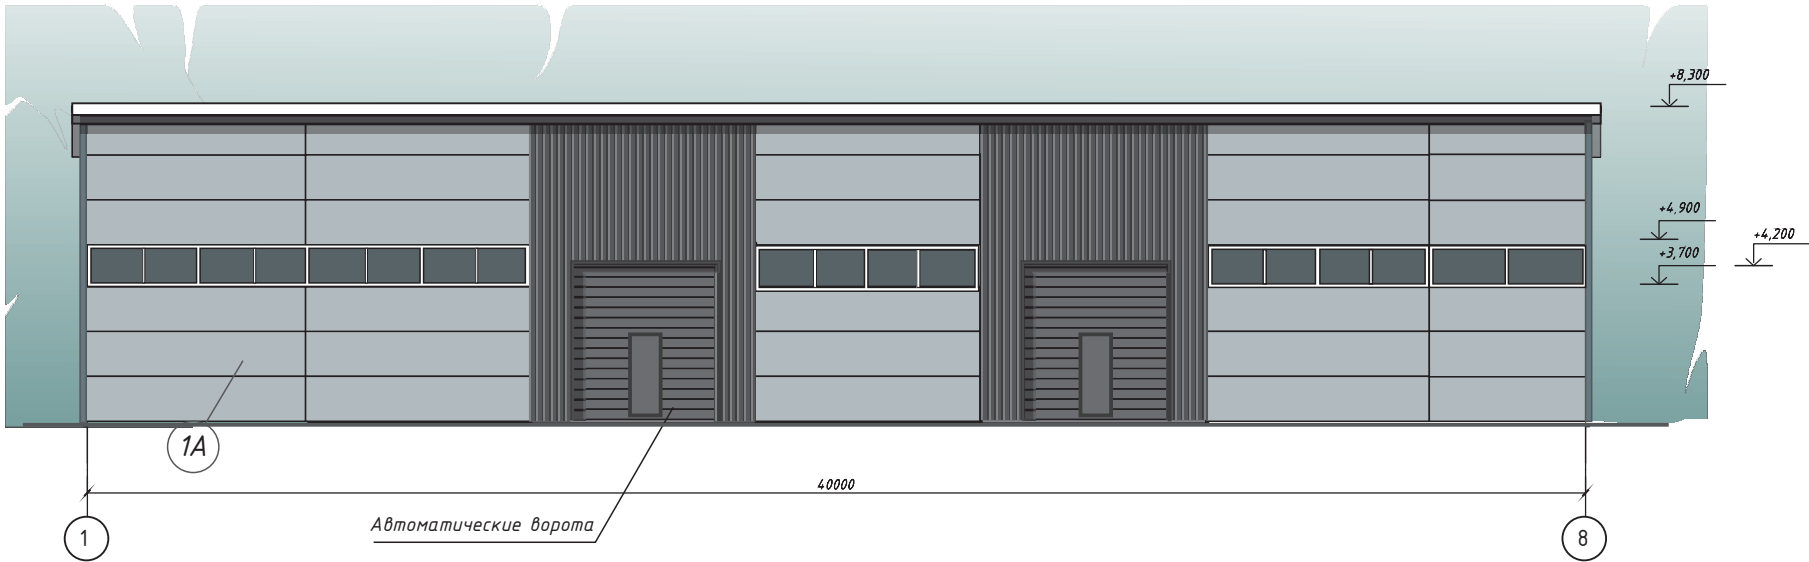

Фасад А-Б

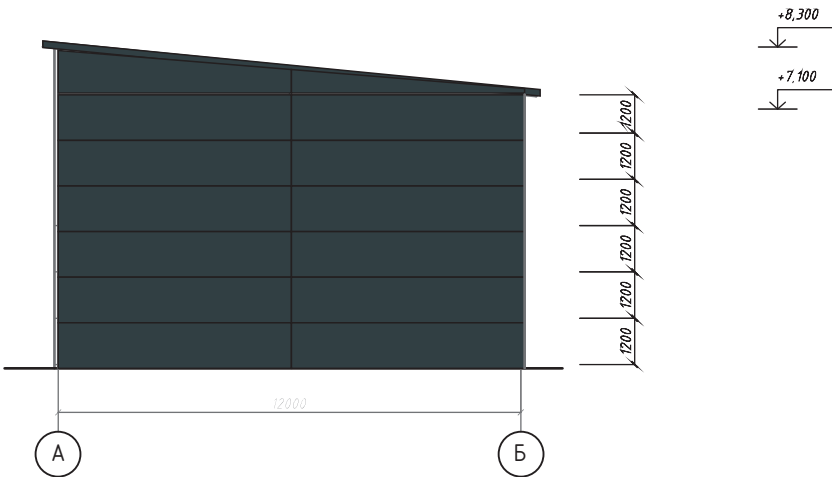


Фасад А-Б

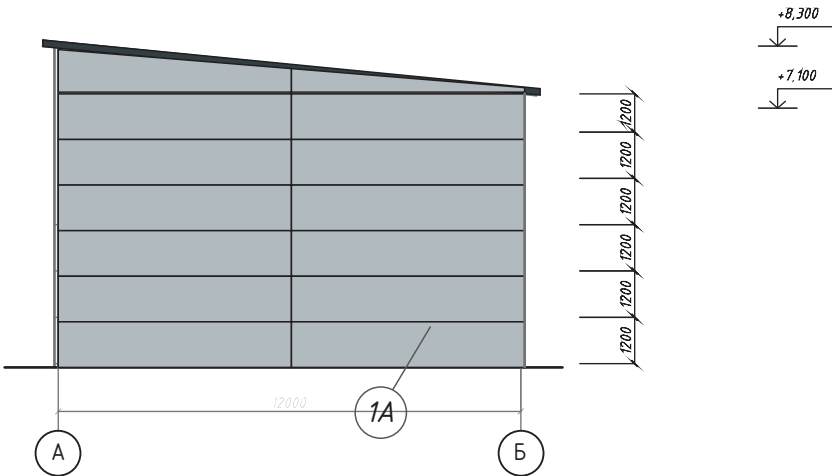


						22-25-Т-АР			
						Здание склада металлопродукции по адресу : Республика Татарстан ,г. Альметьевск,ул. Базовая,д44,строение №6			
Изм.	Кол.уч.	Лист	№ док	Подп.	Дата	Архитектурные решения	Стадия	Лист	Листов
							П	1	
ГАП		Минабутдинов							
Н.контр		Ишуков А.К.				Фасад в осях 1-8;А-Б вариант №1,2	ЗАО ПК «Татсельхозхимпроект» г. Альметьевск		
Разработал		Минабутдинов							


Фасад в осях 1-8 (вариант3)

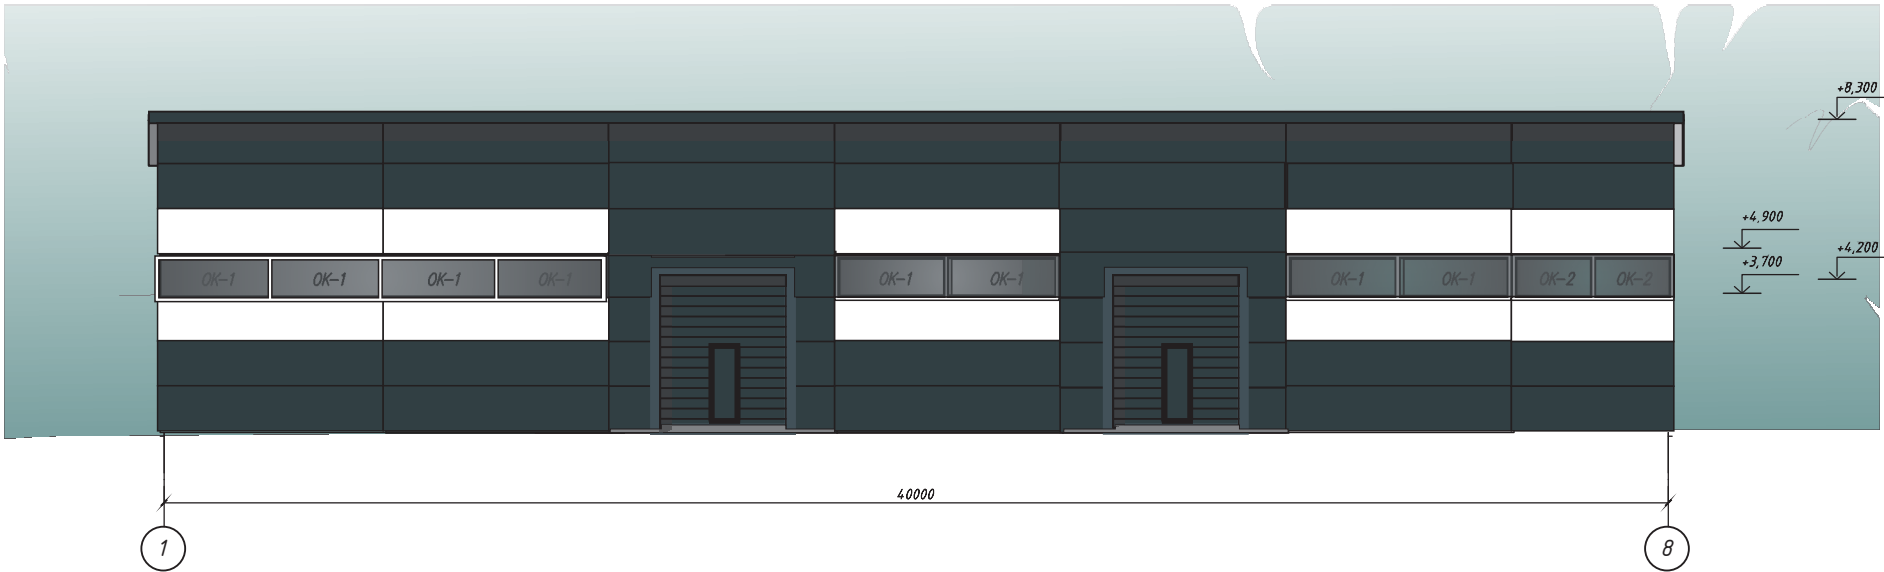


Фасад в осях А-Б

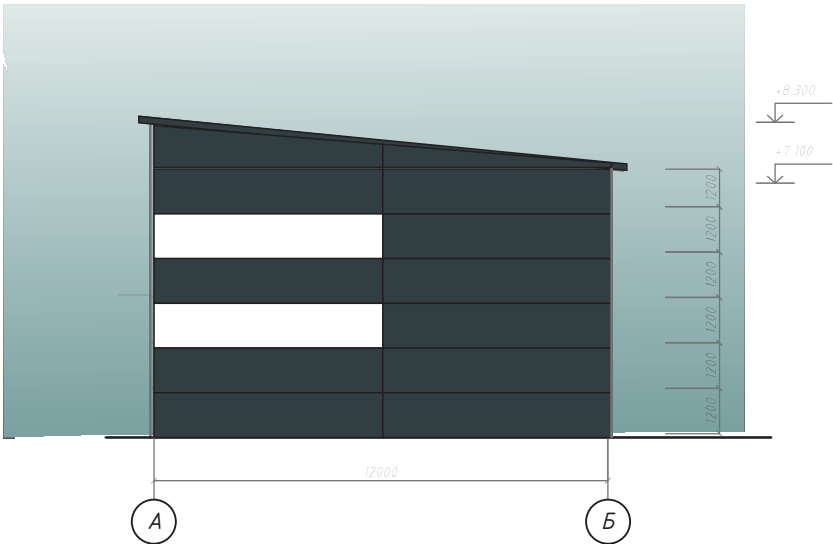

Фасад в осях 1-8 (вариант3)

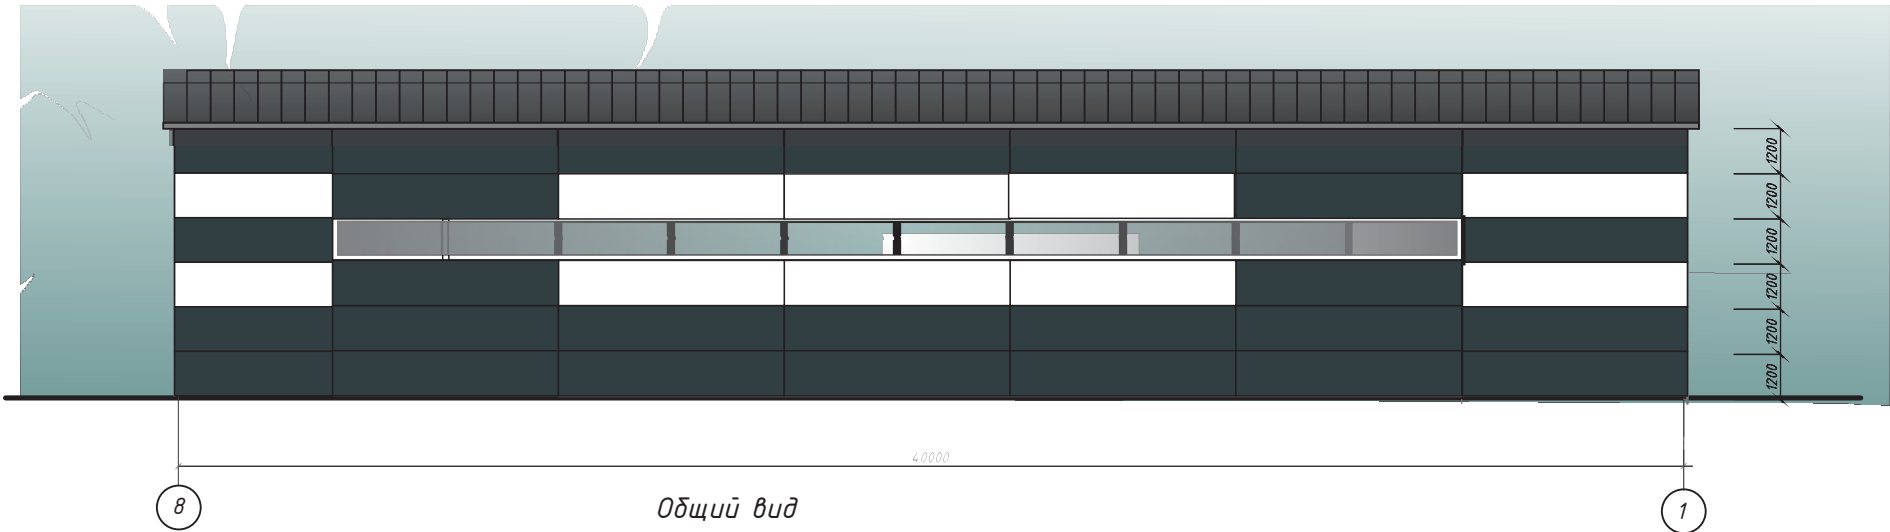


Фасад в осях Б-А

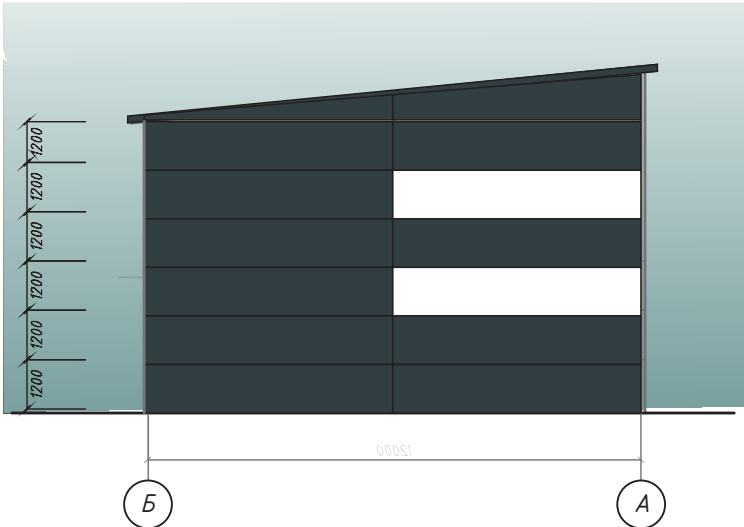

						22-25-Т-АР			
						Здание склада металлопродукции по адресу : Республика Татарстан ,г. Альметьевск,ул. Базовая,д44,строение №6			
Изм.	Кол.уч.	Лист	№ док	Подп.	Дата	Архитектурные решения	Стадия	Лист	Листов
							П	1	
ГАП		Минабутдинов				Фасад в осях 1-8;А-Б;Б-А вариант №3 Общий вид	ЗАО ПК «Татсельхозхимпроект» г. Альметьевск		
Н.контр		Ишуков А.К.							
Разработал		Минабутдинов							


План склада

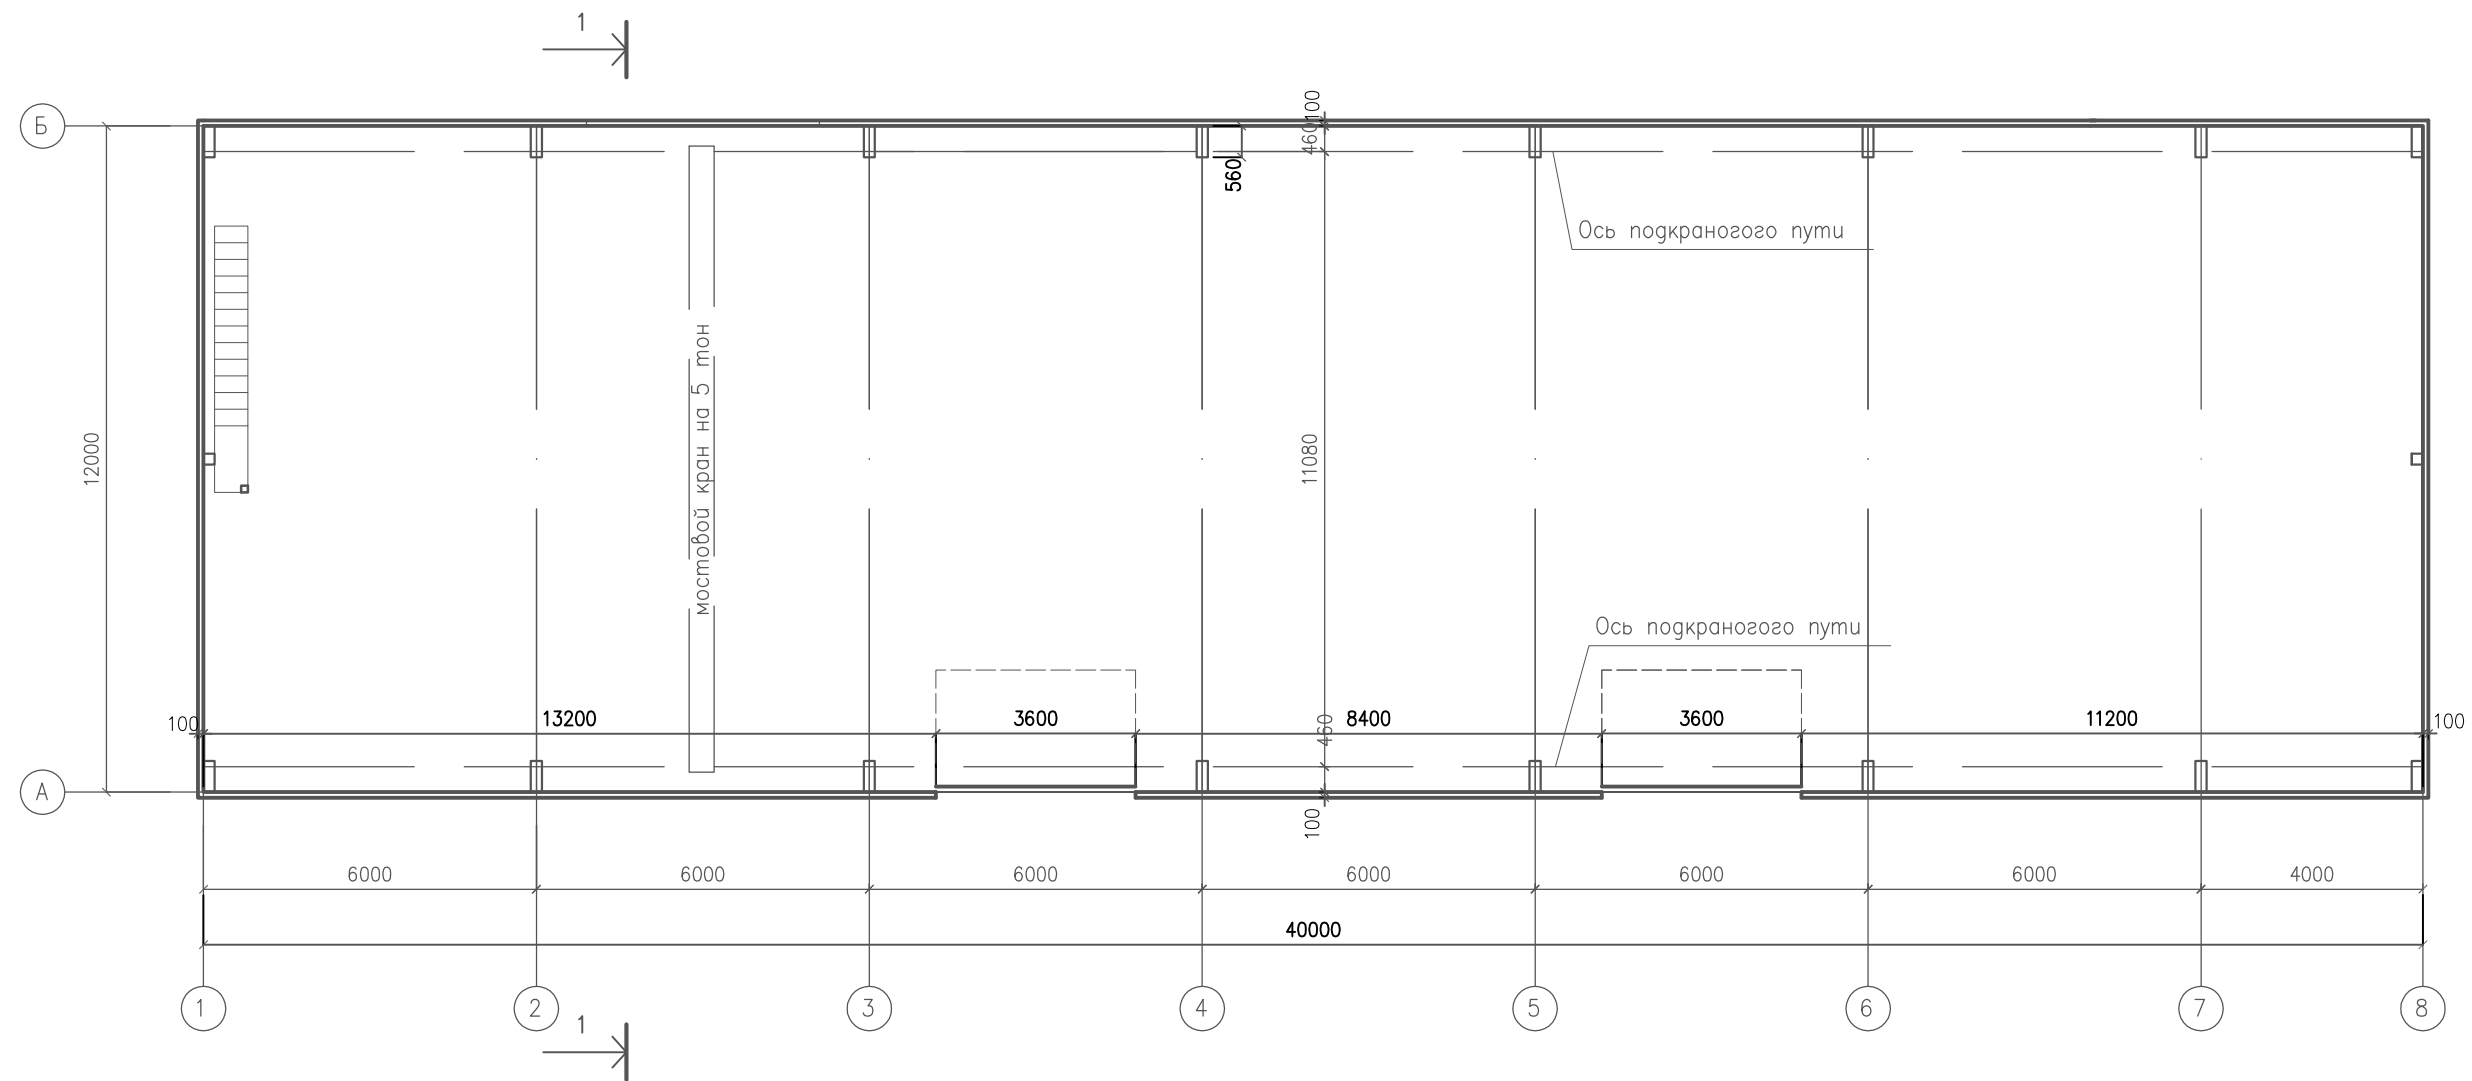

Примечание:
Окна условно не показаны. Местоположение окон
смотри лист АР-3,4

					22/25—Т				АР			
					Здание склада металлопродукции по адресу: Республика Татарстан, г. Альметьевск, ул. Базовая, д.44.							
Изм.	Лист	докум.	Погн.	дата	Объемно— планировочные и архитектурные решения	Стадия	Лист	Листов				
ГАП	Минабутдинов					П	1					
Тех. контроль	Исупов											
Разработал	Мирзибаиров				План склада	ЗАО ПК "Татсельхозхимпроект"						
						г. Алт						


Фасад 1–8

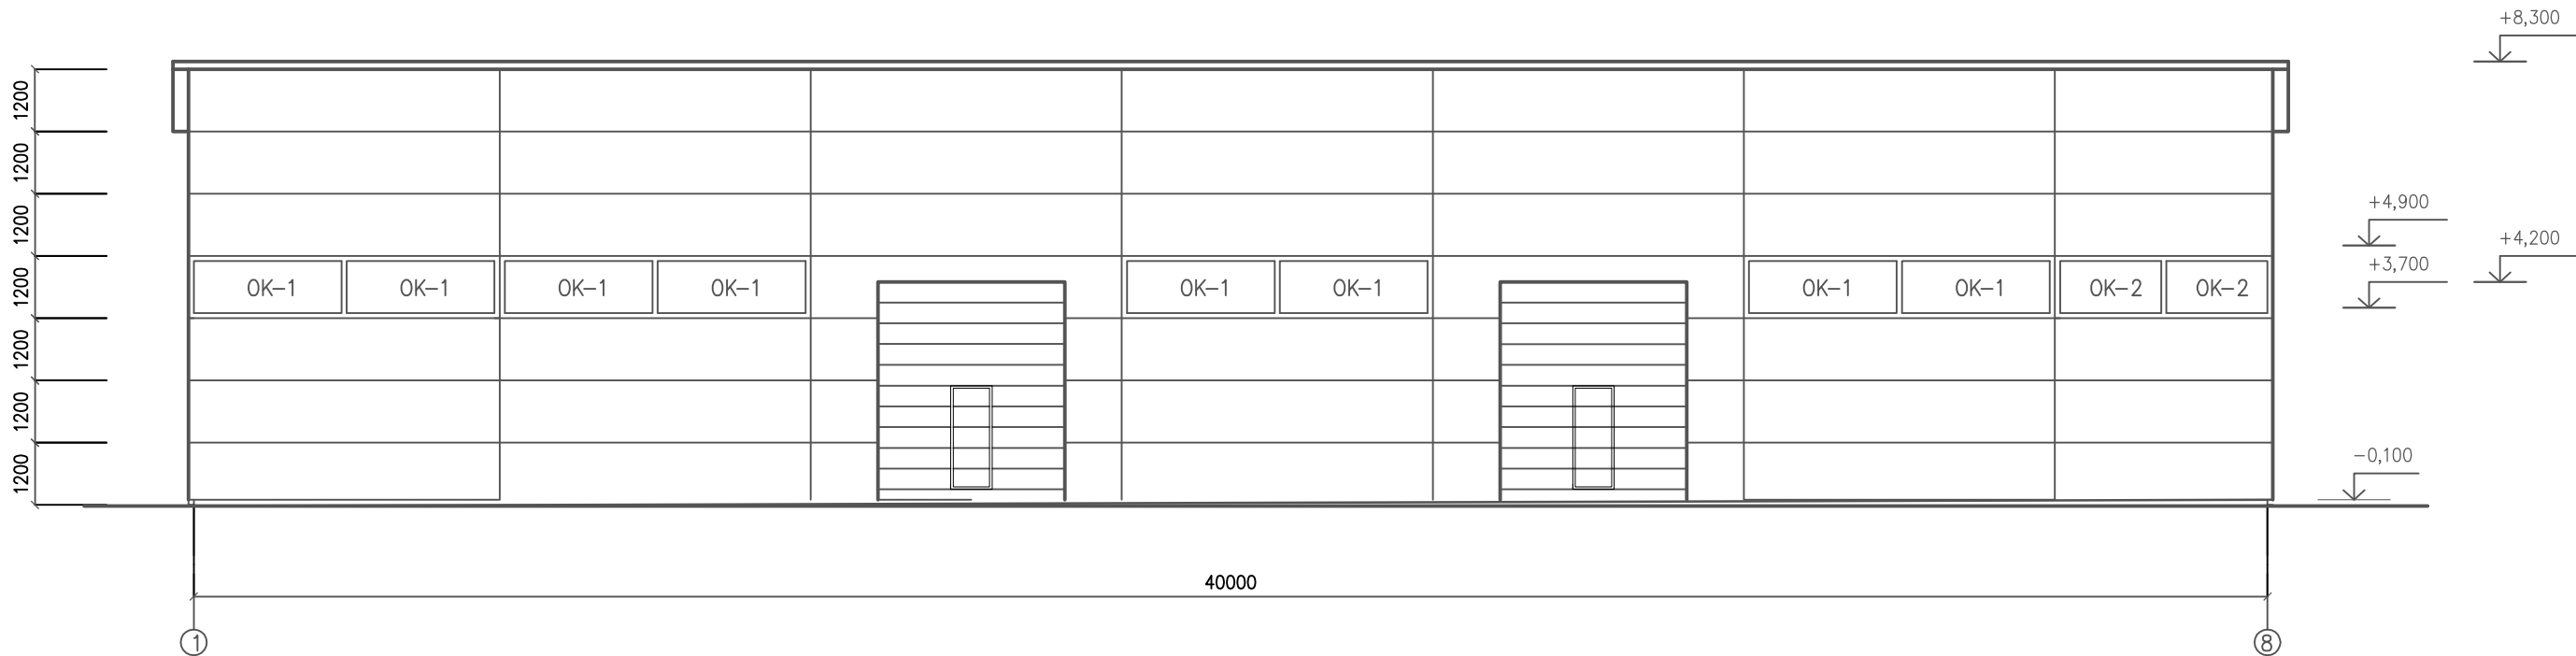



Примечание:
Окна приняты марки 34914–2022
Автоматические ворота взяты марки "Алютеск"

					22/25–Т	АР		
					Здание склада металлопродукции по адресу: Республика Татарстан, г. Альметьевск, ул. Базовая, д.44.			
Изм.	Лист	докум.	Погн.	дата	Объемно– планировочные и архитектурные решения	Стадия	Лист	Листов
ГАП	Минабутдинов					П	3	
Тех. контроль	Исупов							
Разработал	Мирзибаиров							
					Фасад 1–8	ЗАО ПК "Татсельхозхимпроект"		
						г. Алт		


Фасад 8-1

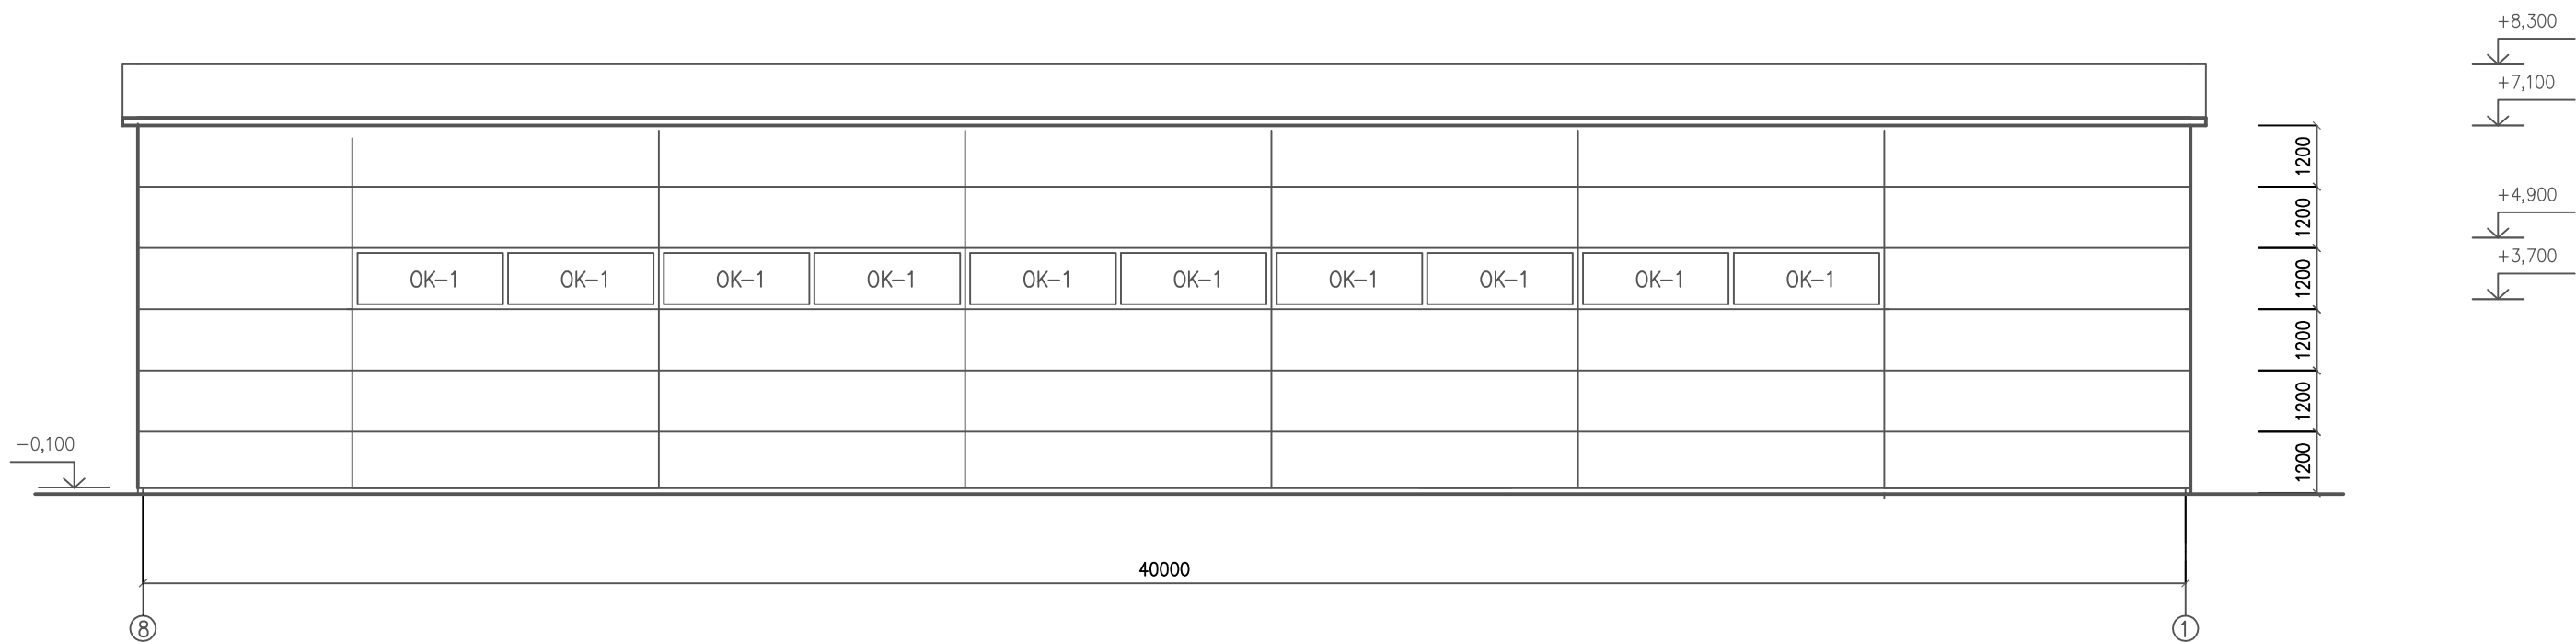

					22/25–Т	АР			
Изм.	Лист	докум.	Погн.	дата	Здание склада металлопродукции по адресу: Республика Татарстан, г. Альметьевск, ул. Базовая, д.44.				
ГАП	Минабутдинов				Объемно–планировочные и архитектурные решения	Стадия	Лист	Листов	
Тех. контроль	Исупов					П	4		
Разработал	Мирзабаев								
					Фасад 8–1	ЗАО ПК "Татсельхозхимпроект"			
						г. Алт			

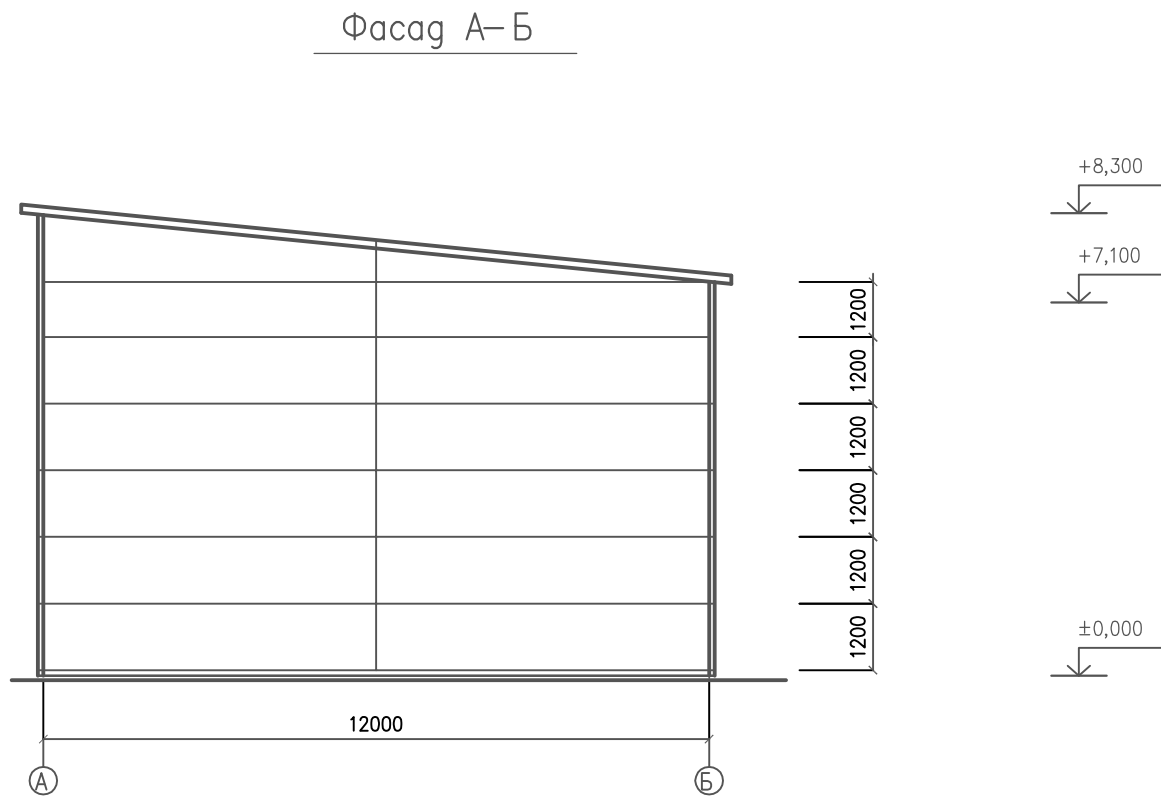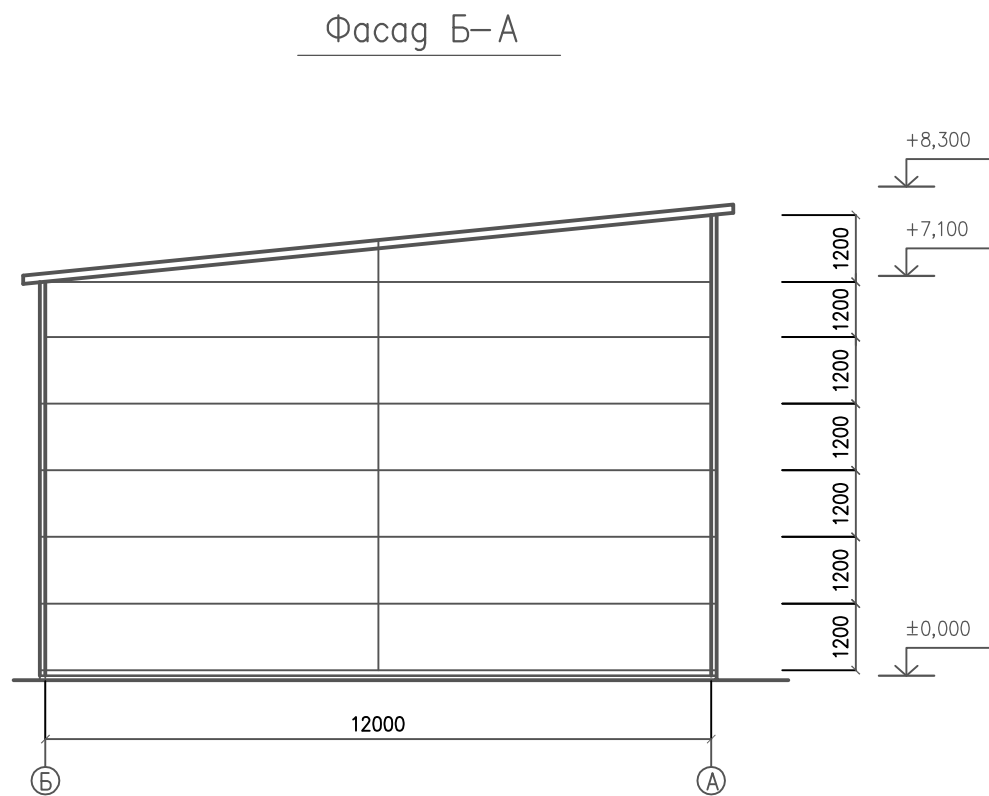

					22/25–Т	АР				
					Здание склада металлопродукции по адресу: Республика Татарстан, г. Альметьевск, ул. Базовая, д.44.					
Изм.	Лист	докум.	Погн.	дата	Объемно– планировочные и архитектурные решения	Стадия	Лист	Листов		
ГАП	Минабутдинов					П	5			
Тех. контроль	Исупов									
Разработал	Мирзабаиров									
					Фасад А–Б и Б–А	ЗАО ПК "Татсельхозхимпроект"				
						г. Алт				

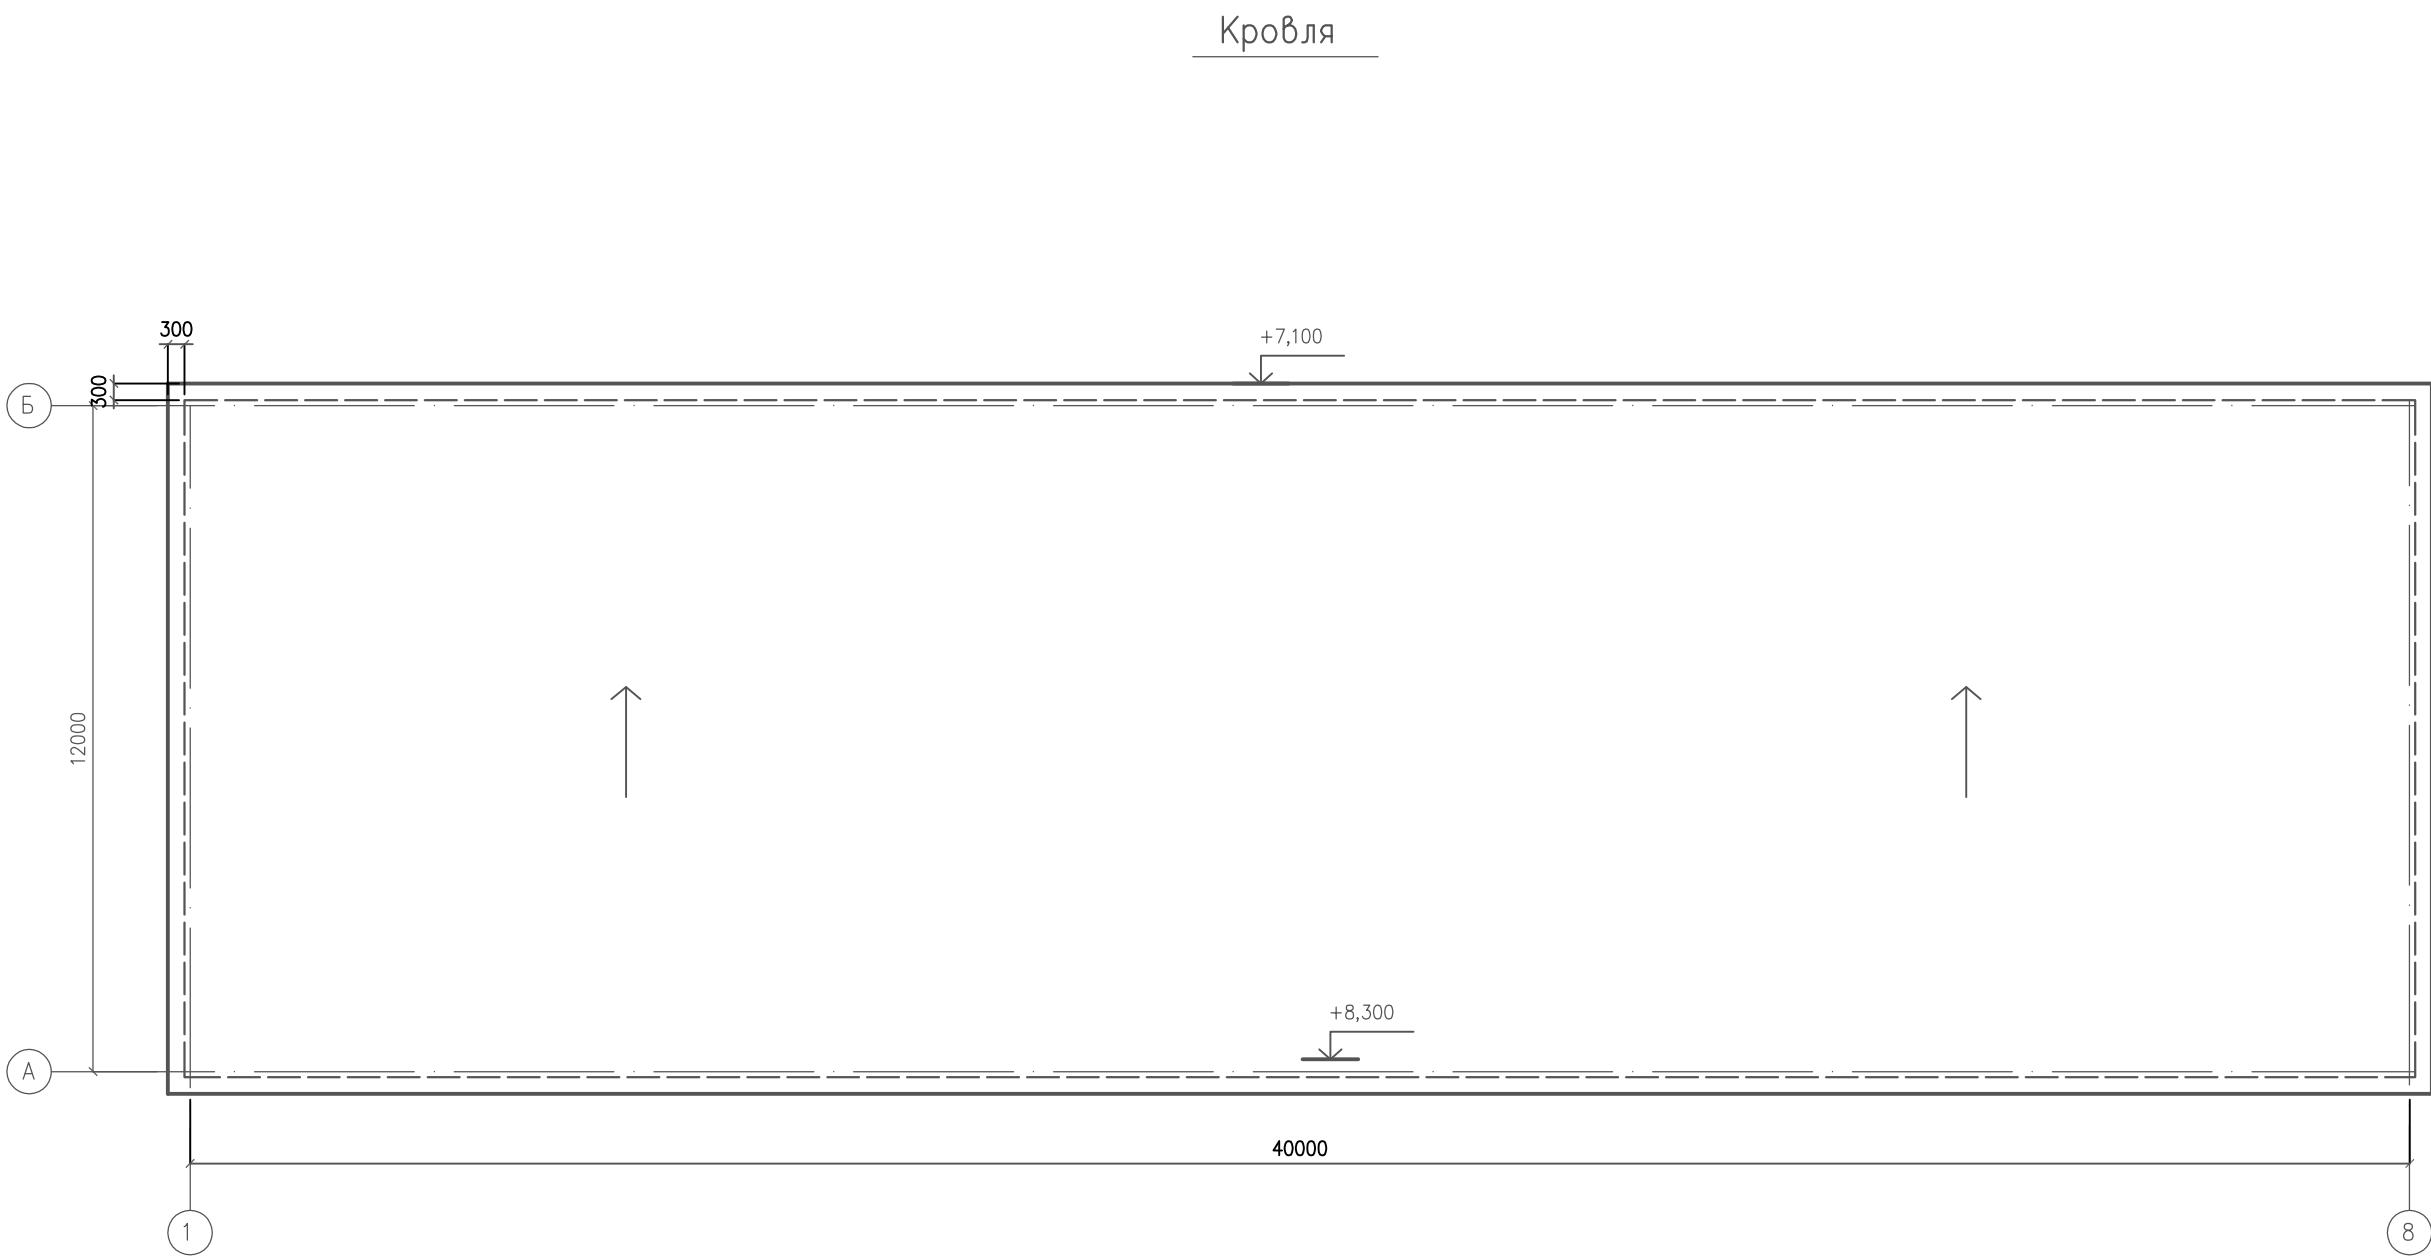

					22/25–Т				АР		
					Здание склада металлопродукции по адресу: Республика Татарстан, г. Альметьевск, ул. Базовая, д.44.						
Изм.	Лист	докум.	Погн.	дата	Объемно– планировочные и архитектурные решения	Стадия	Лист	Листов			
ГАП	Минабутдинов					П	6				
Тех. контроль	Исупов										
Разработал	Мирзибаиров				Кровля	ЗАО ПК "Татсельхозхимпроект"					
						г. Алт					