

ВЕДОМОСТЬ ОСНОВНЫХ КОМПЛЕКТОВ ЧЕРТЕЖЕЙ		
Обозначен.	Наименование	Примеч.
ГП	Генплан	
ТЭТ	Наружное электроснабжение, наружн.освещение	
ТГ	Наружное газоснабжение	
ТСО	Наружные инженерные сети водопровода и канал.	
АТС	Наружные сети связи	
ЙТ	Дорога	
ИТ	Наружные инженерные сети отопление	

ВЕДОМОСТЬ ОСНОВНЫХ МАРКИРОВОЧНЫХ ЧЕРТЕЖЕЙ		
Листь	Наименование	Объяснение
1	Общие данные	
2	Местонахождение территории	
3	Генеральный план	М 1:500
4	Разбивочный чертеж	М 1:500
5		
6		
7		

СПИСОК СПРАВОЧНЫХ ДОКУМЕНТОВ

Белгилари	Номланиши	Изоҳ
ШНК 2.07.01-23	Планирование застройки и	
	застройки территорий населенных	
	пунктов с учетом	
	градостроительных норм	
	градостроительства	
ШНК 1.03.02-23	Структура и содержание	
	градостроительных документов	
	по планированию развития и	
	застройки территорий в условиях	
	градостроительства.	

Проект соответствует требованиям технологических,противопожарных и других норм, действующих на территории Республики Узбекистан и беспечивает безопасную для жизни и здоровья эксплуатации объектов при соблюдение предусмотренных рабочими чертежами мероприятий

Гл.архитектор проекта

Валижонов

Валижонов Х

ОБЩИЕ ДАННЫЕ

Капитальный ремонт школы №10 на 460 учащихся мест в СГМ "Пахтаобод" Китабского района Кашкадарьинской области на основание постановление Президента РУ №_____от _____года в целях реализацим программе "Исламского банка развитие ОПЕК".

Основаные грунтово - почвенный слой воды находится на расстояние 2,8-3,0 метров от поверхности земли.

- сесмичность района - 7 баллов.
- категория отвестственности - III.
- максимальное глубина премерз грунтов - 0,45 на каждый 10 лет 0,57 м на каждый 50 лет.
- колебания температуры воздуха
- среднегодовая темпер.воздуха +18°С
- максимальъная темпер воздуха +40°С
- минимальная темпер воздуха -20°С

Направление ветра:

- в июне - августе северо - восточная
- в декабре - феврале восточная
- Показатель грунтового основания следующие:
- земельный участок расположена на IV кlementической зоны. Земельный участок проектируомах зданий граничит:
- с севера - пашней;
- с юга - существующие индивидуальные жилые дома;
- с запада - существующие индивидуальные жилые дома;
- с востока - существующие индивидуальные жилые дома;

Данный проект разработаm на основания нормативных документов действующих на территории Республики Узбекистан, а также, проект инженерных коммуникаций разработанны оснавания представленных технических условий.

ВЕДЕМОСТЬ МАЛЫХ ФОРМ АРХИТЕКТУРЫ

№ по ГП	Условное изображение	Наименование	Количество	Обозначения типового поекта
		Ажурные ворота (проект.)	2 шт	
		Глухие ворота (сущ.)	1 шт	
		Противопожарный щит (проект.)	2 шт	
		Скамейка (проект.)	4 шт	
		Урна (проект.)	4 шт	
		Глухие ограждения (сущ.)	410.0 п.м	
		Ажурные металлические ограждения (проект.)	140.0 п.м	
		Глухие корсетные ограждения (проект.)	140.0 п.м	

ВЕДЕМОСТЬ ЖИЛЫХ И ОБЩЕСТВЕННЫХ ЗДАНИЙ И СООРУЖЕНИЙ

№ по ГП	Наименование	Этажность	Количество	Показателей			Тип номер проекта	
				Общ. площ. м2	Площ. застр. м2	Стр. объём. м3		
1	Существующий корпус капитальный ремонт (сущ.)	2	1					
2	Футбольное поле (сущ.)	1	2					
3	Котельная (сущ. не рабочая)	1	1					
4	Склад хранения угля (сущ.)	1	1					
5	Уборная (сущ.)	1	1					
6	Склад (сущ.)	1	1					
7	Противопожарный хауз 80 м3 (снос.)	1	1					
8	Хауз (снос.)	1	1					
9	Ажурные ворота (сущ.)	1	2					
10	Глухие ворота (сущ.)		1					
11	Ажурные металлические ограждения (сущ.)							
12	Глухие ограждения (сущ.)							
13	Противопожарный щит (проект.)		2					
14	Автостоянка (проект.)		8					
15	Трансформатор (сущ. 250 кВт)							
16	Глухие корсетные ограждения (сущ.)							
17	Выгребная яма (сущ.)							
18	Фанкойл, Чиллер (проект.)	-	1					
19	ЛОС 12м3/сут (проект.)	-	1					
20	Накопительная емкость с насосом (проект.)	-	1					
21	Модульная котельная (проект.)	-	1					
22	Резервуар питьевой воды 25 м³ (проект.)	-	1					

ВЕДЕМОСТЬ МАЛЫХ ФОРМ АРХИТЕКТУРЫ

№ по ГП	Условное изображение	Наименование	Количество	Обозначения типового поекта
		Ажурные ворота (проект.)	2 шт	
		Глухие ворота (сущ.)	1 шт	
		Противопожарный щит (проект.)	2 шт	
		Скамейка (проект.)	4 шт	
		Урна (проект.)	4 шт	
		Глухие ограждения (сущ.)	410.0 п.м	
		Ажурные металлические ограждения (сущ.)	140.0 п.м	
		Глухие корсетные ограждения (сущ.)	140.0 п.м	

БАЛАНС ТЕРРИТОРИИ

№ по ГП	Наименование	Ед. изме. рение	Площадь	%
1	Общая площадь участка	га	2.16	100.0
2	Площадь застройки	га	0.23	12.0
3	Площадь дороги и площадки	га	0.34	15.0
4	Площадь озеленения	га	1.59	73.0
5				

						Клиент: Исламский банк развития и Фонд международного развития ОПЕК. Проект «Устойчивое развитие сельских территорий»
						Капитальный ремонт школы №10 на 460 учащихся мест в СГМ "Пахтаобод" Китабского района Кашкадарьинской области
Улч.	Мик.	Варақ	Хуж.№	Имзо	Сана	Генеральный план
						И.П
						1
						4
Начальник отдела	Жураев И.					Общие данные
ГИП	Собирова М					
Исполнитель	Валижонов Х					




"QISHLOQQURILISHLOIHA"
Государственное учреждение Глав-
ной проектной институт
г.Ташкент - 2025г

СИТУАЦИОННЫЙ ПЛАН



СИТУАЦИОННЫЙ ПЛАН

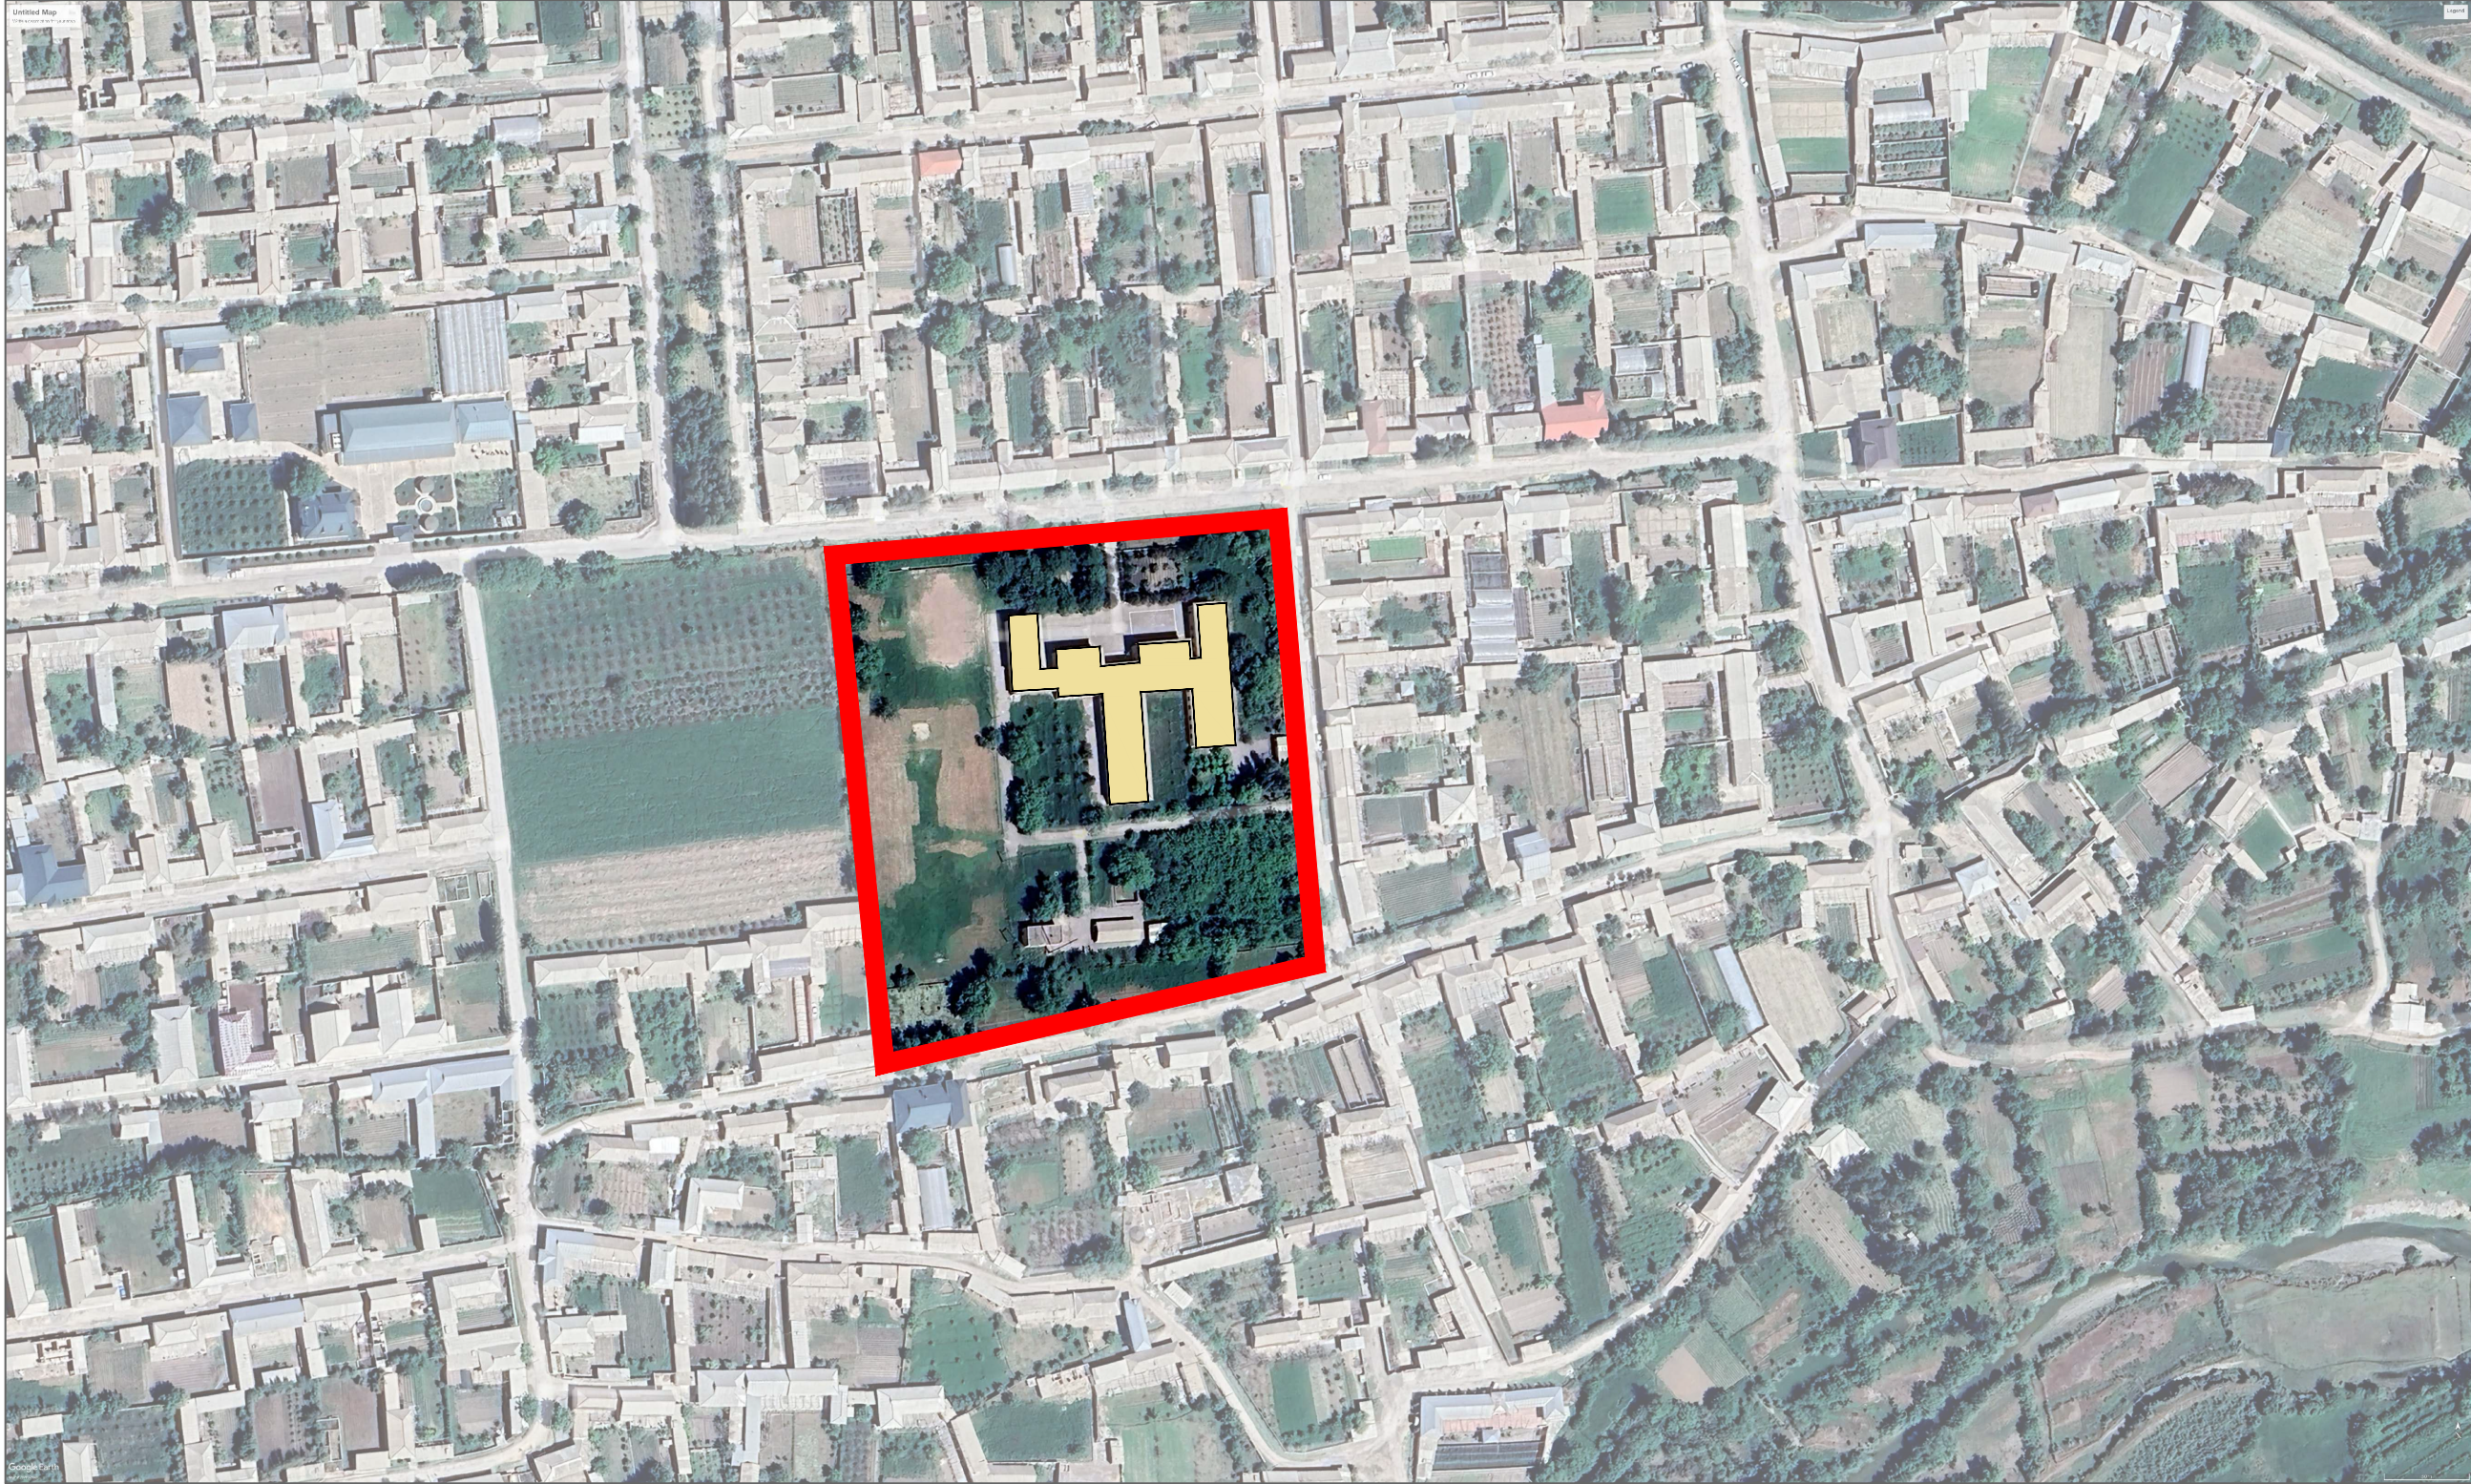

ВЕДЕМОСТЬ ЖИЛЫХ И ОБЩЕСТВЕННЫХ ЗДАНИЙ И СООРУЖЕНИЙ

№ по ГП	Наименование	Этажность	Количество	Показателей			Тип номер проекта	
				Общ. площ. м2	Площ. застр. м2	Стр. объём. м3		
1	Существующий корпус капитальный ремонт (сущ.)	2	1					
2	Футбольное поле (сущ.)	1	2					
3	Котельная (сущ. не рабочая)	1	1					
4	Склад хранения угля (сущ.)	1	1					
5	Уборная (сущ.)	1	1					
6	Склад (сущ.)	1	1					
7	Противопожарный хауз 80 м3 (снос.)	1	1					
8	Хауз (снос.)	1	1					
9	Ажурные ворота (сущ.)	1	2					
10	Глухие ворота (сущ.)		1					
11	Ажурные металлические ограждения (сущ.)							
12	Глухие ограждения (сущ.)							
13	Противопожарный шит (проект.)		2					
14	Автостоянка (проект.)		8					
15	Трансформатор (сущ. 250 кВт)							
16	Глухие корсетные ограждения (сущ.)							
17	Выгребная яма (сущ.)							
18	Фанкойл, Чиллер (проект.)	-	1					
19	ЛОС 12м3/сут (проект.)	-	1					
20	Накопительная емкость с насосом (проект.)	-	1					
21	Модульная котельная (проект.)	-	1					
22	Резервуар питьевой воды 25 м³ (проект.)	-	1					

ВЕДЕМОСТЬ МАЛЫХ ФОРМ АРХИТЕКТУРЫ

№ по ГП	Условное изображение	Наименование	Количество	Обозначения типового поекта
		Ажурные ворота (проект.)	2 шт	
		Глухие ворота (сущ.)	1 шт	
		Противопожарный шит (проект.)	2 шт	
		Скамейка (проект.)	4 шт	
		Урна (проект.)	4 шт	
		Глухие ограждения (сущ.)	410.0 п.м	
		Ажурные металлические ограждения (сущ.)	140.0 п.м	
		Глухие корсетные ограждения (сущ.)	140.0 п.м	

						Договор:	ГП					
						Капитальный ремонт школы №10 на 460 учащихся мест в СГМ "Пахтаобод" Китабского района Кашкадарьинской области						
Изм.	Кол.уч	Лист	Док №	Подпись	Дата			Стадия	Лист	Листов		
								РП	2	4		
Начальник отдела	Жураев И.					Ситуационный план		"QISHLOQQURILISHLPYINA" DM Ташкент 2025 г.				
ГИП	Собирова М											
Исполнитель	Валижонов Х											






№ по ГП	Наименование	Этажность	Количество	Показателей			Тип номер проекта	
				Общ. площ. м2	Площ. застр. м2	Стр. объём. м3		
1	Существующий корпус капитальный ремонт (сущ.)	2	1					
2	Футбольное поле (сущ.)	1	2					
3	Котельная (сущ. не рабочая)	1	1					
4	Склад хранения угля (сущ.)	1	1					
5	Уборная (сущ.)	1	1					
6	Склад (сущ.)	1	1					
7	Противопожарный хауз 80 м3 (снос.)	1	1					
8	Хауз (снос.)	1	1					
9	Ажурные ворота (сущ.)	1	2					
10	Глухие ворота (сущ.)		1					
11	Ажурные металлические ограждения (сущ.)							
12	Глухие ограждения (сущ.)							
13	Противопожарный щит (проект.)		2					
14	Автостоянка (проект.)		8					
15	Трансформатор (сущ. 250 кВт)							
16	Глухие корсетные ограждения (сущ.)							
17	Выгребная яма (сущ.)							
18	Фанкойл, Чиллер (проект.)	-	1					
19	ЛОС 12м3/сут (проект.)	-	1					
20	Накопительная емкость с насосом (проект.)	-	1					
21	Модульная котельная (проект.)	-	1					
22	Резервуар питьевой воды 25 м³ (проект.)	-	1					

№ по ГП	Условное изображение	Наименование	Количество	Обозначения типового проекта
		Ажурные ворота (проект.)	2 шт	
		Глухие ворота (сущ.)	1 шт	
		Противопожарный щит (проект.)	2 шт	
		Скамейка (проект.)	4 шт	
		Урна (проект.)	4 шт	
		Глухие ограждения (сущ.)	410.0 п.м	
		Ажурные металлические ограждения (сущ.)	140.0 п.м	
		Глухие корсетные ограждения (сущ.)	140.0 п.м	

№ по ГП	Наименование	Ед изме рение	Пло щадь	%
1	Общая площадь участка	га	2.16	100.0
2	Площадь застройки	га	0.23	12.0
3	Площадь дороги и площадки	га	0.34	15.0
4	Площадь озеленения	га	1.59	73.0
5				

						Договор:	ГП					
						Капитальный ремонт школы №10 на 460 учащихся мест в СГМ "Пахтабод" Китабского района Кашкадарьинской области						
Изм.	Кол.уч	Лист	Док №	Подпись	Дата	Генеральный план			Стадия	Лист	Листов	
									РП	3	4	
Начальник отдела	Жураев И.					М1:500			"КИШЛОҚҚУРИЛИШ ЛОЙИХА" ГУ город Ташкент 2025 г.			
ГИП	Собирова М											
Исполнитель	Валижонов Х											

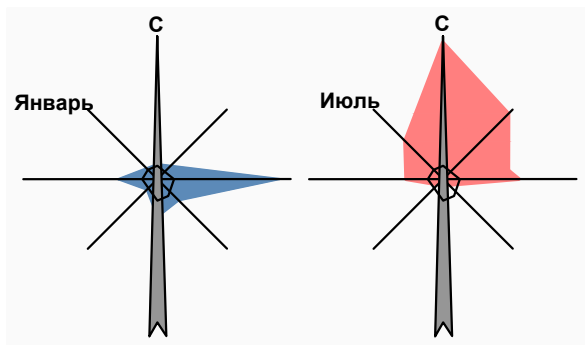

УСЛОВНЫЕ ОБОЗНАЧЕНИЕ

- Existing buildings
- Greenery
- Existing roads and sidewalks

ВЕДЕМОСТЬ ЖИЛЫХ И ОБЩЕСТВЕННЫХ ЗДАНИЙ И СООРУЖЕНИЙ

№ по ГП	Наименование	Этажность	Количество	Показателей			Тип номер проекта	
				Общ. площ. м2	Площ. застр. м2	Стр. объём. м3		
1	Существующий корпус капитальный ремонт (сущ.)	2	1					
2	Футбольное поле (сущ.)	1	2					
3	Котельная (сущ. не рабочая)	1	1					
4	Склад хранения угля (сущ.)	1	1					
5	Уборная (сущ.)	1	1					
6	Склад (сущ.)	1	1					
7	Противопожарный хауз 80 м3 (снос.)	1	1					
8	Хауз (снос.)	1	1					
9	Ажурные ворота (сущ.)	1	2					
10	Глухие ворота (сущ.)		1					
11	Ажурные металлические ограждения (сущ.)							
12	Глухие ограждения (сущ.)							
13	Противопожарный щит (проект.)		2					
14	Автостоянка (проект.)		8					
15	Трансформатор (сущ. 250 кВт)							
16	Глухие корсетные ограждения (сущ.)							
17	Выгребная яма (сущ.)							
18	Фанкойл, Чиллер (проект.)	-	1					
19	ЛОС 12м3/сут (проект.)	-	1					
20	Накопительная емкость с насосом (проект.)	-	1					
21	Модульная котельная (проект.)	-	1					
22	Резервуар питьевой воды 25 м³ (проект.)	-	1					

Обрезка
(размеры указаны в сантиметрах)

Цементно-бетонное покрытие марки V20 (M250) F / 2100
По ГОСТ 26633-2012
Металлическая сетка VR-1 Ø 4 мм шаг 200x150 мм
Выравнивающий слой из каменно-песчаной смеси 5-20 фракций, смешанной с песком до 30%

Базовый слой песчано-гравийной смеси S4-S7 по ГОСТ 25607-2009

Грунт дорожного полотна

Слой полиэтилена марки V (v1) по ГОСТ 10354-82 толщиной 0,3-0,4 мм

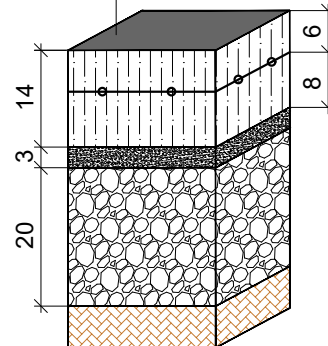


Таблица объемов работ по благоустройству автостоянка

NN п/п	Услов. обоз.	Наименование работ	Ед. изм.	Кол-во
1		II Благоустройство Объем работ по укладке дорожного покрытия - Полиэтиленовый слой - Цементно-бетонное покрытие марки V20 (M250) F / 2100 - Н=14 см по ГОСТ 26633-2012; - Металлическая сетка VR-1 Ø 4 мм шаг 200x150 мм - Щебень-песок 5-20 фракций, смешанный с песком до 30% - выравнивающий слой из смеси Н / SR = 3 см; - Базовый слой песчано-гравийной смеси ГОСТ 25607-2009 по S4-S7 h / SR=20 см; - Дорожный грунт;	м2 м3	150 55.5

						Договор:	ГП				
						Капитальный ремонт школы №10 на 460 учащихся мест в СГМ "Пахтаобод" Китабского района Кашкадарьинской области					
Изм.	Кол.уч	Лист	Док №	Подпись	Дата				Стадия	Лист	Листов
						Генеральный план			РП	4	4
Начальник отдела	Жураев И.					Вертикальная планировка М1:500			"КИШЛОҚҚУРИЛИШ ЛОЙИХА" ГУ город Ташкент 2025 г.		
ГИП	Собирова М										
Исполнитель	Валижонов Х										

Ведомость основных комплектов рабочих чертежей		
Обозначение	Наименование	Примечание
АР	Архитектурное решение	
КС	Конструктивное решение	
ТХ	Технологическое решение	
ОВ	Отопление, вентиляция и кондиционирование	
	воздуха.	
ВК	Водопровод и канализация	
ЭМ	Электроосвещение и электрооборудование	
ПС	Пожарная сигнализация	
СС	Связь и сигнализация	
АСС	Автоматизация сантехсистем	

Ведомость рабочих чертежей основного комплекта марки АР.

Лист	№	НАИМЕНОВАНИЕ	ПРИМЕ-НИЕ
	1	Общие данные	
	2	План стен 1-го этажа после реконструкция.	
	3	План кровля после реконструкция.	
	4	Разрез 1-1	
	5	Фасад в осях 1-2	
	6	Схема элементов заполнения дверных проемов	
	7	Экспликация полов; План полов 1-этажа	
	8	Схема крепления плит утеплителя; Схема усиления оконных и дверных проемов	
	9	Узлы по наружным стенам; Пример схемы отлива	
	10		
	11		

Проект соответствует требованиям технологических,санитарно-гигиенических, противопожарных и других норм, действующих на территории Республики Узбекистан и обеспечивает безопасную для жизни и здоровья эксплуатацию объекта при соблюдении предусмотренных рабочими чертежами мероприятий.

Главный инженер проекта



Ведомость ссы лочных и прилагаемых		
Обозначение	Наименование	Примечание
	Ссылочных	
ГОСТ 24698-81	Двери наружные и служебные для жилых и общественных зданий.	
Серия 2.244-1 вып. 5	Детали полов общественных зданий.	
Серия 2.130-6с вып. 1	Узлы стен жилых и общественных зданий возводимых в районах сейсмичн. 7;8 и 9 балл.	
Серия 2.260-1 вып. 2	Детали покрытий общественных зданий.	


Общие указания

Характеристика участка строительства:
Расчетная зимняя температура воздух - 15 °С.
Скоростной напор ветра - 38кг/м^д.
Вес снегового покрова - 50кг/м².
Сейсмичность площадки - 7 баллов.
Категория грунтов по сейсмическим свойствам - III.
Расчетная сейсмичность площадки - 8 баллов.
Глубина промерзания грунта - 0.32 м.
Класс ответственности здания - II
Классификация зданий по функциональной пожарной опасности - Ф 3.4
Коэффициент надежности по назначению - 0.95
Степень огнестойкости - II
Проектом реконструкции предусматривается следующие виды работ:
1. Зачистка потолков с окраской 100%.
2. Демонтаж существующей кровли и устройство нового покрытия профнастила 100%.
3. Устройство 14 шт дополнительных слуховых окон;
4. Демонтаж и установка новых оконных и дверных блоков - 100%
5. Ремонт существующей штукатурки фасадов 100 %
6. Демонтаж сущ. штукатурки внутренних стен перегородок 100 %
7. Окраска фасадов фасадными красками
8. Штукатурка внутренних стен см. ведомость отделки
9. Цоколь и вертикальные поверхности крылец облицевать бетонными плитками.

Объемно-планировочные показатели:
Общая площадь- 151.9 м²
Строительный объем - 820.3 м³
Площадь застройки --172.4 м²


						Договор №	АР				
						Капитальный ремонт школы №10 на 460 учащихся мест в СГМ "Пахтаобод" Китабского района Кашкадарьинской области					
Изм.	Кол.уч	Лист	Н.док	Подпись	Дата	Существующий учебный корпус Блок 1			Стадия	Лист	Листов
ГИП		Собирова М							РП	1	
ГАП		Валижонов X									
Разраб.		Пазилов.К.М									
						Общие данные			ГУ QISHLOQQURILISHLOYIHA Фаргона 2025 г.		


План стен 1-го этажа после реконструкция.

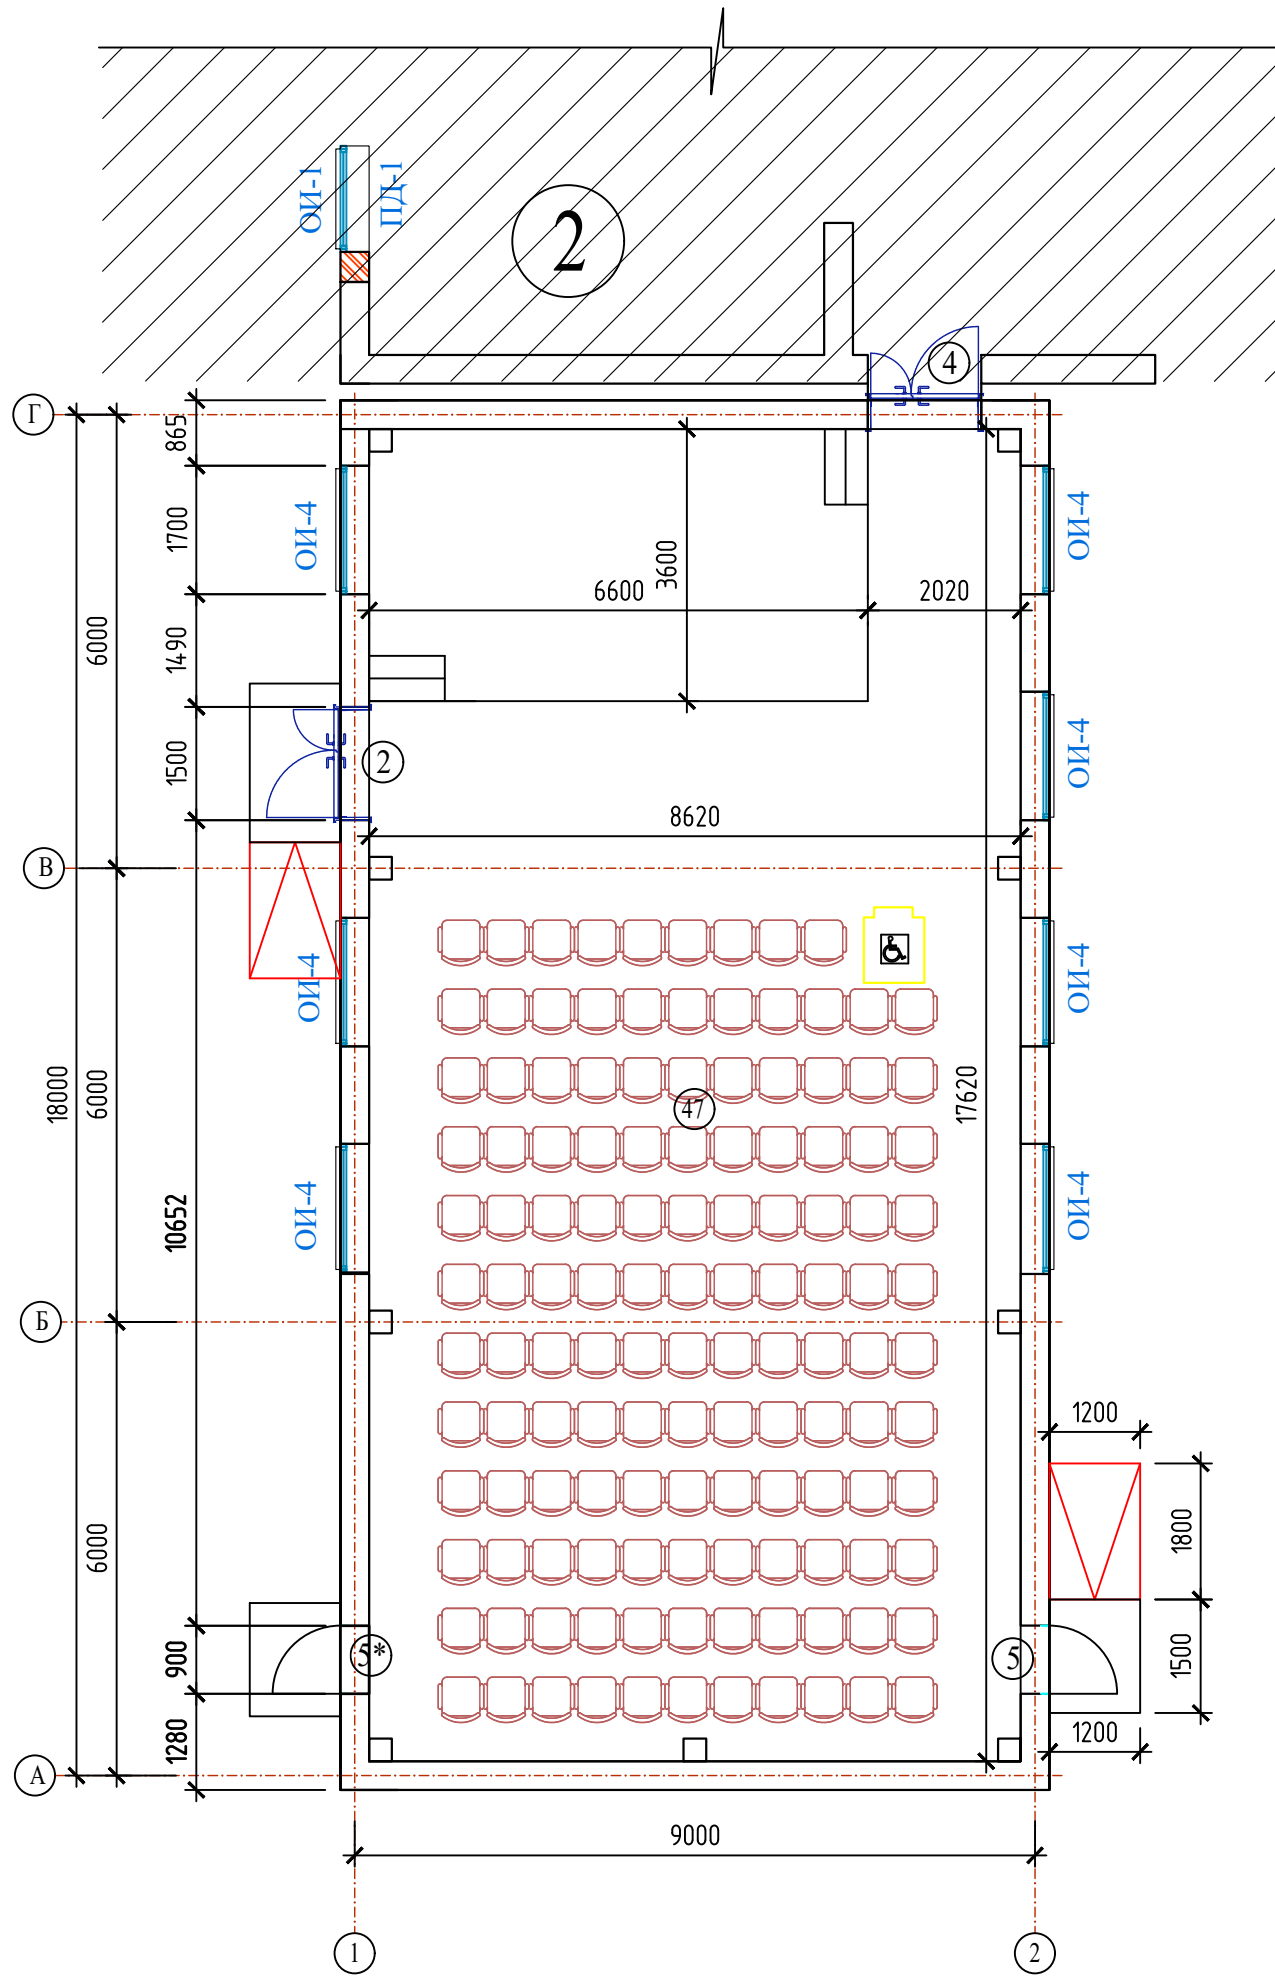

Экспликация помещений		
Номер пом.	Наименование	Площадь м²
47	Актальный зал	152.0

Схема блокировки

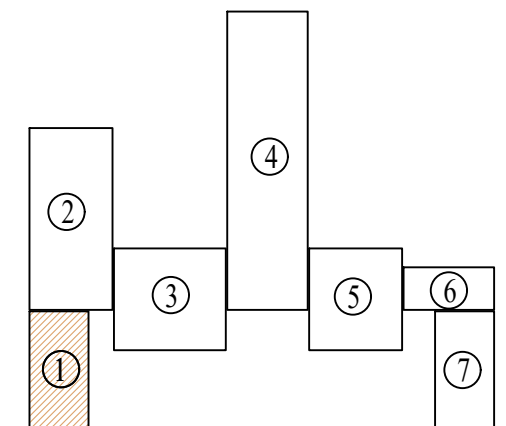

 						Договор №	АР					
						Капитальный ремонт школы №10 на 460 учащихся мест в СГМ "Пахтаобод" Китабского района Кашкадарьинской области						
Изм.	Кол.уч	Лист	N.док	Подпись	Дата							
ГИП		Собирова М				Существующий учебный корпус Блок 1		Стадия	Лист	Листов		
ГАП		Валижонов X						РП	2			
Разраб.		Пазиров.К.М										
						План стен 1-го этажа после реконструкция.		ГУ QISHLOQQURILISHLOYUNA Фаргона 2025 г.				

План кровля после реконструкция .




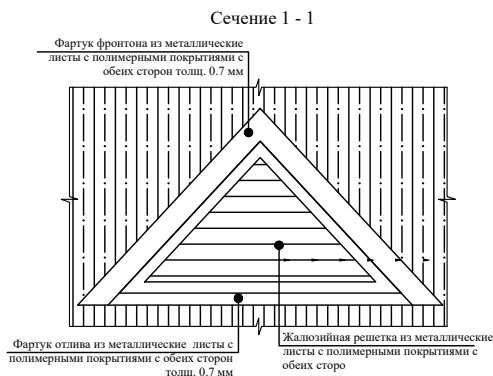


Схема блокировки

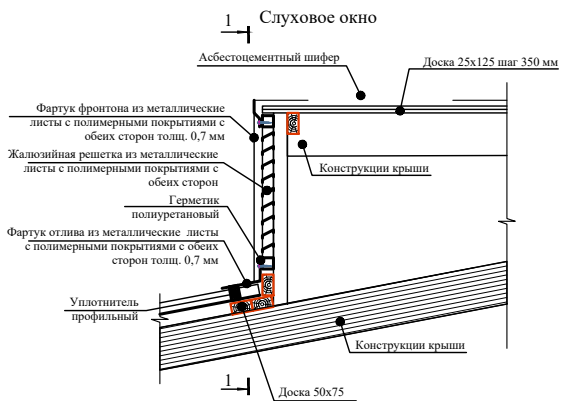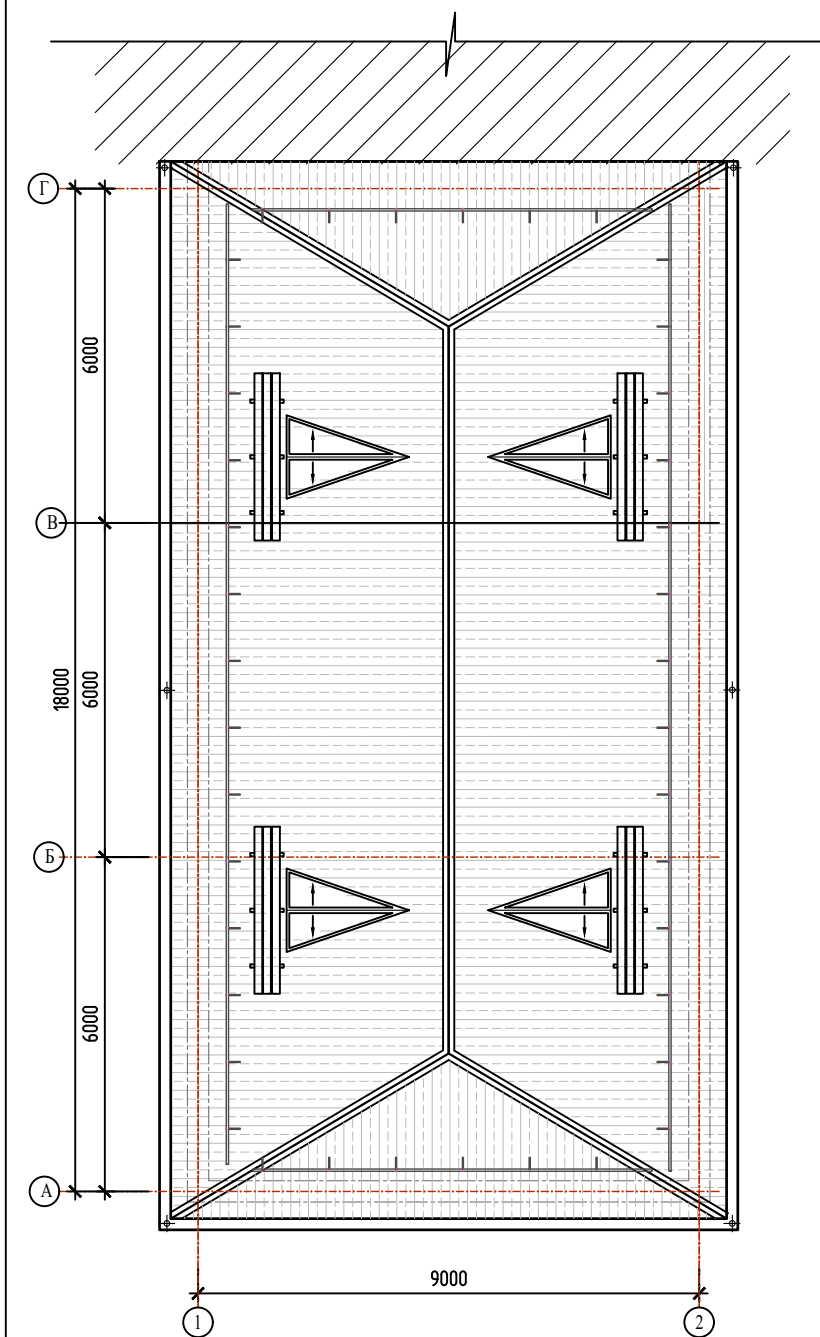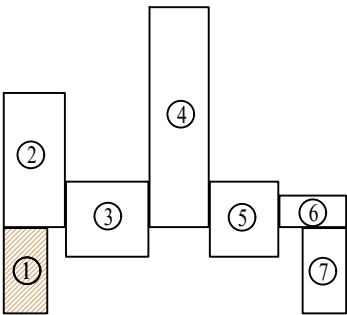

Спецификация элементов кровли


Поз.	Обозначение	Наименование	Кол.	Масса ед.,кг.	Приме- чание
		Расход материалов для кровли			
		Профилированные листы с полимерным покрытием СН3000х1064-17(Кровля,)			189.9 м²
		Профилированные листы с полимерным покрытием СН3000х1064-17(Козырек,)			39.0м²
1	Индивидуальный изготовление	Конек упрощенный пм	27.9		
2		Водосточная латок пм	48.8		
3		Труба водосточная пм	30.6		
4		Воронки шт	5		
5		Колено шт	15		
6		Снегозадержател пм	48.8		
7		Кронштейн -30x4 L=600мм	60	0.60	36.0 кг
8	Материал:	Слуховое окно	4		

Спецификация элементов жалюзийных решеток


Поз.	Обозначение	Наименование	Кол.	Масса ед. кг	Примеч.
Жр-1	Расход дан на одну жалюзийную решетку общ. кол. 4 шт.				
	Данный лист	Жалюзийная решетка	1		шт.
	ГОСТ 8509-93	Рама из гн.уголка 50х5	2.8	3.77	п.м.
	ГОСТ 103-76	"Перо"-3х120 L=перем. ш.75мм	10	5.652	шт.
	ГОСТ 5781-82	Каркас из арматуры Ø6A240	2.9	0,222	п.м.
	ГОСТ 19903-74*	Клямеры из полосы -1х10 L=50 шагом 300	10	0,004	шт.
	ГОСТ 5336-80*	Сетка стальная Р-15-1.6-0	0.5	2,57	м²

						Договор №	АР				
						Капитальный ремонт школы №10 на 460 учащихся мест в СГМ "Пахтаобод" Китабского района Кашкадарьинской области					
Изм.	Кол.у	Лист	N.доп	Подпись	Дата	Существующий учебный корпус Блок 1			Стадия	Лист	Листов
ГИП				Собирова М.	11/11/2024				РП	3	
ГАП				Валижонов X	11/11/2024						
Разраб.				Пазиров.К.М	11/11/2024						
						План кровля после реконструкция .			ГУ QISHLOQQURILISHLOYINA Фаргона 2025 г.		


Фасад

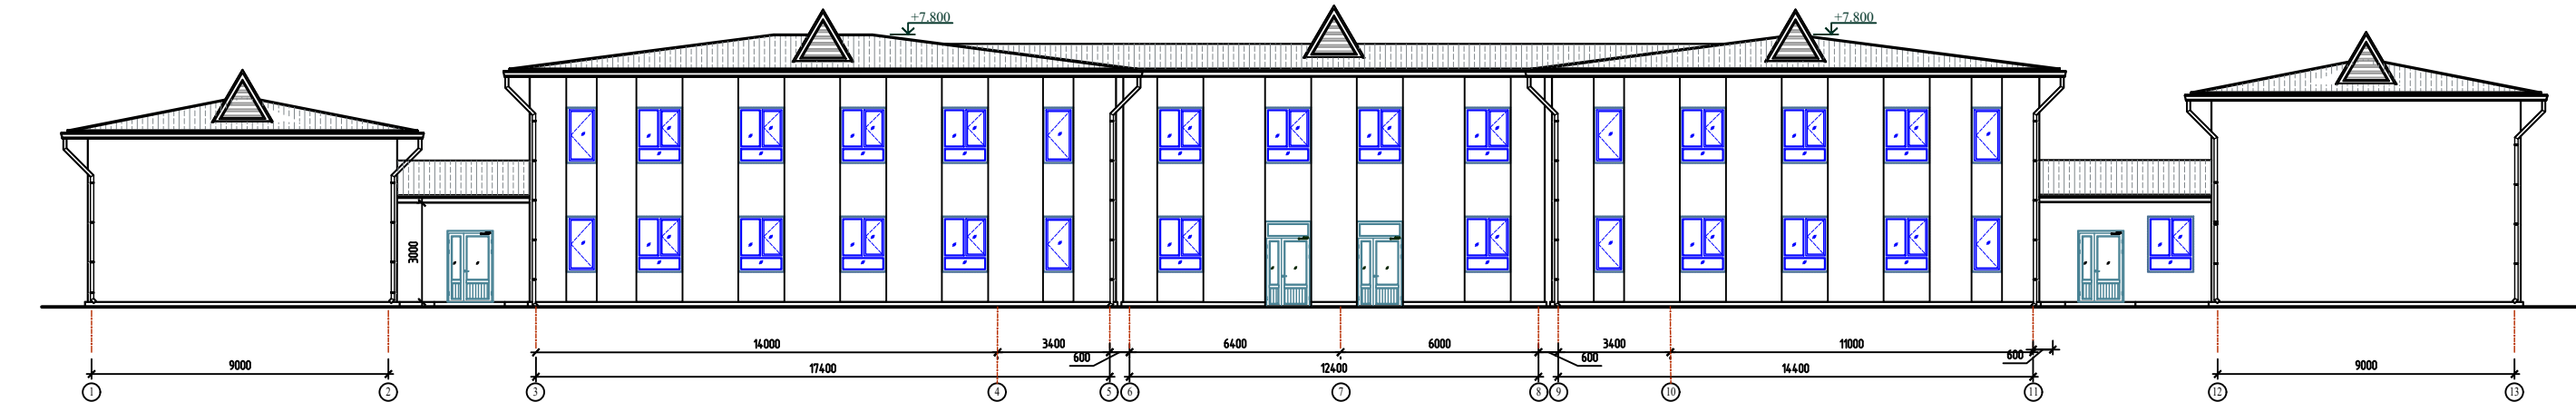

Разрез 1-1

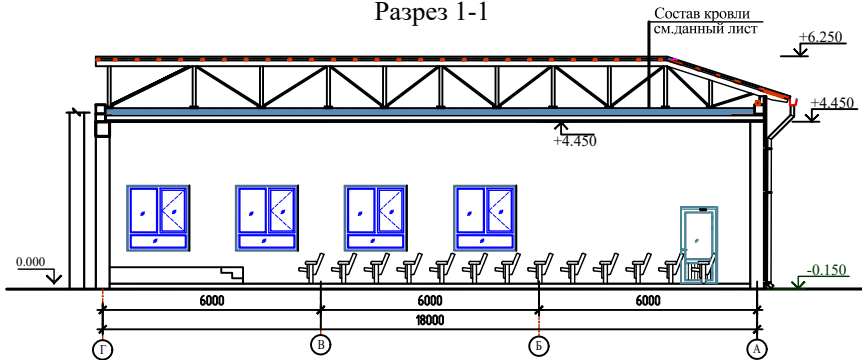

Узел-1

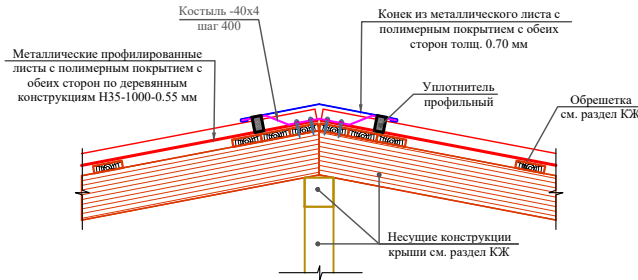

СОСТАВ КРОВЛИ №1

- Металлические профилированные листы с полимерным покрытием с обеих сторон, по деревянным конструкциям (РСТУз 24045-94)Н35-1000-0,55 мм(см. КЖ)
- Цементно-песчаная смесь - ЦПС, М 150 (ГОСТ 28013-98), из полусухой смеси - толщ.50 мм. с армированием сеткой из Ø4 АСК (АБК) шаг 150 х 150 мм. с устройством деформационных швов шагом 6.0 х 6.0 м (с заполнением д.ш. герметиком)
- Гидроизоляционная мембрана из нетканного полипропиленового полотна*) -1 слой
- Утеплитель - минеральные плиты на основе базальтового волокна $\gamma = 120\text{кг/м}^3$,толщ. 50 мм. (в два слоя) - 100 мм.
- Пароизоляция из полиэтиленовой пленки - 200мм.
- Сборная железобетонная плита покрытия - 220 мм

*) Нетканое полипропиленовое полотно – это материал изготавливаемый из полипропиленовых нитей, скрепленных термическим способом (термоскрепление). Поверхностная плотность возможна от 10 до 150 г/м².

Примечание

Состав утеплителя наружных стен

- Простая штукатурка цементно-песчаным раствором
- Клеевая смесь.
- Утеплитель (минераловатная плита).
- Штукатурный клеевой слой толщ. 3мм.
- Стекловолоконная сетка (ячейка 5х5мм)
- Штукатурный клеевой слой толщ. 2мм.
- Декоративно - отделочный слой толщ. 2мм.

-10мм.
-10мм.
-50мм.

- 5-7мм.

- Цветовое решение фасадов, текстуру и фактуру материалов см. согласованный демонстрационный материал.
- Все материалы применяемые для устройства фасадов должны соответствовать техническим условиям и иметь сертификаты соответствия с обязательным предоставлением их фирмой изготовителем, исполнителем заказчику.
- Работы по отделке фасадов выполнять в соответствии с требованиями СНиП 3.04.01-87 "Изоляционные и отделочные покрытия".
- Цвета отделочных материалов фирме исполнителю согласовать с заказчиком.
- По периметру откосов и по наружным углам стен установить угол перфорированный с сеткой.
- Ведомость отделки фасадов см. АР-13.

Ведомость отделки фасада

Поз. отделки	Наименование элемента фасада	Наименование материала отделки	Наименование и номер эталона цвета или образца колера	Примечан. Площадь, м²
1	Цоколь	Изоляция цоколя теплоизолирующие декоративные фасадные сэндвич панели с пенополиуретаном 16мм	(цвета- подбирать по показательному материалу)	8.35
2	Стены	Очистка 100% существующей отделки фасада с последующей заменой и нанесением новых слоев	-	256
2*		(Состав утеплителя см.раздел-КЖ).	-	
3		2. Декоративный отделочный слой под травертин по готовым поверхностям.	(цвета- подбирать по показательному материалу)	
4	Покрывтие крыльца	Мрамор (нескользящие)	-	5.20

						Договор №	АР				
						Капитальный ремонт школы №10 на 460 учащихся мест в СГМ "Пахтабод" Китабского района Кашкадарьинской области					
Изм.	Кол.уч/лист	№ док	Подпис.	Дата		Существующий учебный корпус Блок 1			Стадия	Лист	Листов
ГИП	Собирова Н								РП	4	
ТАП	Валижонян Х					Фасад в осях 1-2			ГУ QISHLOQQURILISH LOYIHASI Фаргона 2025 г.		
Разраб.	Пазилон К.М										

ВЕДОМОСТЬ ОСНОВНЫХ КОМПЛЕКТОВ РАБОЧИХ ЧЕРТЕЖЕЙ

Обозначение	Наименование	Примечание
АР	Архитектурное решение	
КС	Конструктивное решение	
ТХ	Технологическое решение	
ОВ	Отопление, вентиляция и кондиционирование	
	воздуха.	
ВК	Водопровод и канализация	
ЭМ	Электроосвещение и электрооборудование	
ПС	Пожарная сигнализация	
СС	Связь и сигнализация	
АСС	Автоматизация сантехсистем	

ВЕДОМОСТЬ ССЫЛОЧНЫХ И ПРИЛАГАЕМЫХ ДОКУМЕНТОВ

Обозначение	Наименование	Примечание
	Ссылочных	
ГОСТ 24698-81	Двери наружные и служебные для жилых и общественных зданий.	
Серия 2.244-1 вып. 5	Детали полов общественных зданий.	
Серия 2.130-6с вып. 1	Узлы стен жилых и общественных зданий возводимых в районах сейсмичн. 7;8 и 9 балл.	
Серия 2.260-1 вып. 2	Детали покрытий общественных зданий.	

Ведомость рабочих чертежей основного комплекта марки АР.

№ Лист	НАИМЕНОВАНИЕ	ПРИМЕ-НИЕ
1	Общие данные	
2	План стен 1-го этажа после реконструкция.	
3	План кровля после реконструкция.	
4	Разрез В-А	
5	Фасад	
6	Схема элементов заполнения дверных проемов	
7	Схема элементов заполнения оконных проемов	
8	Ведомость отделки помещений	
9	Экспликация полов; План полов 1-этажа	
10	Схема крепления плит утеплителя; Схема усиления оконных и дверных проемов	
11	Узлы по наружным стенам; Пример схемы отлива	

ОБЪЕМНО-ПЛАНИРОВОЧНЫЕ ПОКАЗАТЕЛИ

№ п/п	Наименование показателей	Ед.изм	Площадь
1	Общая площадь	м ²	328.6
2	Строительный объем	м ³	1609.2
3	Площадь застройки	м ²	392.5

ОБЩИЕ УКАЗАНИЯ

Характеристика участка строительства:

Расчетная зимняя температура воздух

- 15 °С.

Скоростной напор ветра

- 38кг/м².

Вес снегового покрова

- **50**кг/м².

Сейсмичность площадки

- 8 баллов.

Категория грунтов по сейсмическим свойствам

- III.

Расчетная сейсмичность площадки

- 7-8 баллов.

Глубина промерзания грунта

- 0.57 м.

Класс ответственности здания

- II

Классификация зданий по функциональной пожарной опасности

- Ф 3.4

Коэффициент надежности по назначению

- 0.95

Степень огнестойкости

- II

Проектом реконструкции предусматривается следующие виды работ:

1. Зачистка потолков с окраской

100%.

2. Демонтаж существующей кровли и устройство нового покрытия профнастила

100%.

3. Устройство 14 шт дополнительных слуховых окон;

4. Демонтаж и установка новых оконных и дверных блоков

- 100%

5. Ремонт существующей штукатурки фасадов

100 %

6. Демонтаж сущ. штукатурки внутренних стен перегородок

100 %

7. Окраска фасадов фасадными красками

8. Штукатурка внутренних стен см. ведомость отделки

9. Цоколь и вертикальные поверхности крылец

облицевать бетонными плитками.

Согласовано:

Изм. N инв. N

Подпись и дата

Взам. инв. N

Инв. N подл.


Проект соответствует требованиям технологических,санитарно-гигиенических, противопожарных и других норм, действующих на территории Республики Узбекистан и обеспечивает безопасную для жизни и здоровья эксплуатацию объекта при соблюдении предусмотренных рабочими чертежами мероприятий.

Главный инженер проекта



М.Собирова


								Договор	АР						
								Капитальный ремонт школы №10 на 460 учащихся мест в СГМ "Пахтаобод" Китабского района Кашкадарьинской области							
Изм.	Колич.	Лист	Ндок.	Подпись	Дата			Существующий учебный корпус Блок 2	<table><tr><td>Стадия</td><td>Лист</td><td>Листов</td></tr><tr><td>ТП</td><td>1</td><td></td></tr></table>	Стадия	Лист	Листов	ТП	1	
Стадия	Лист	Листов													
ТП	1														
ГИП	Собирова М														
ГАП	Валижонов Х														
Разраб.	Пазиров.К.М														
								Общие данные	ГҲ "QISHLOQ QURILISH LOYIHA" г. Фергана 2025 г. 						

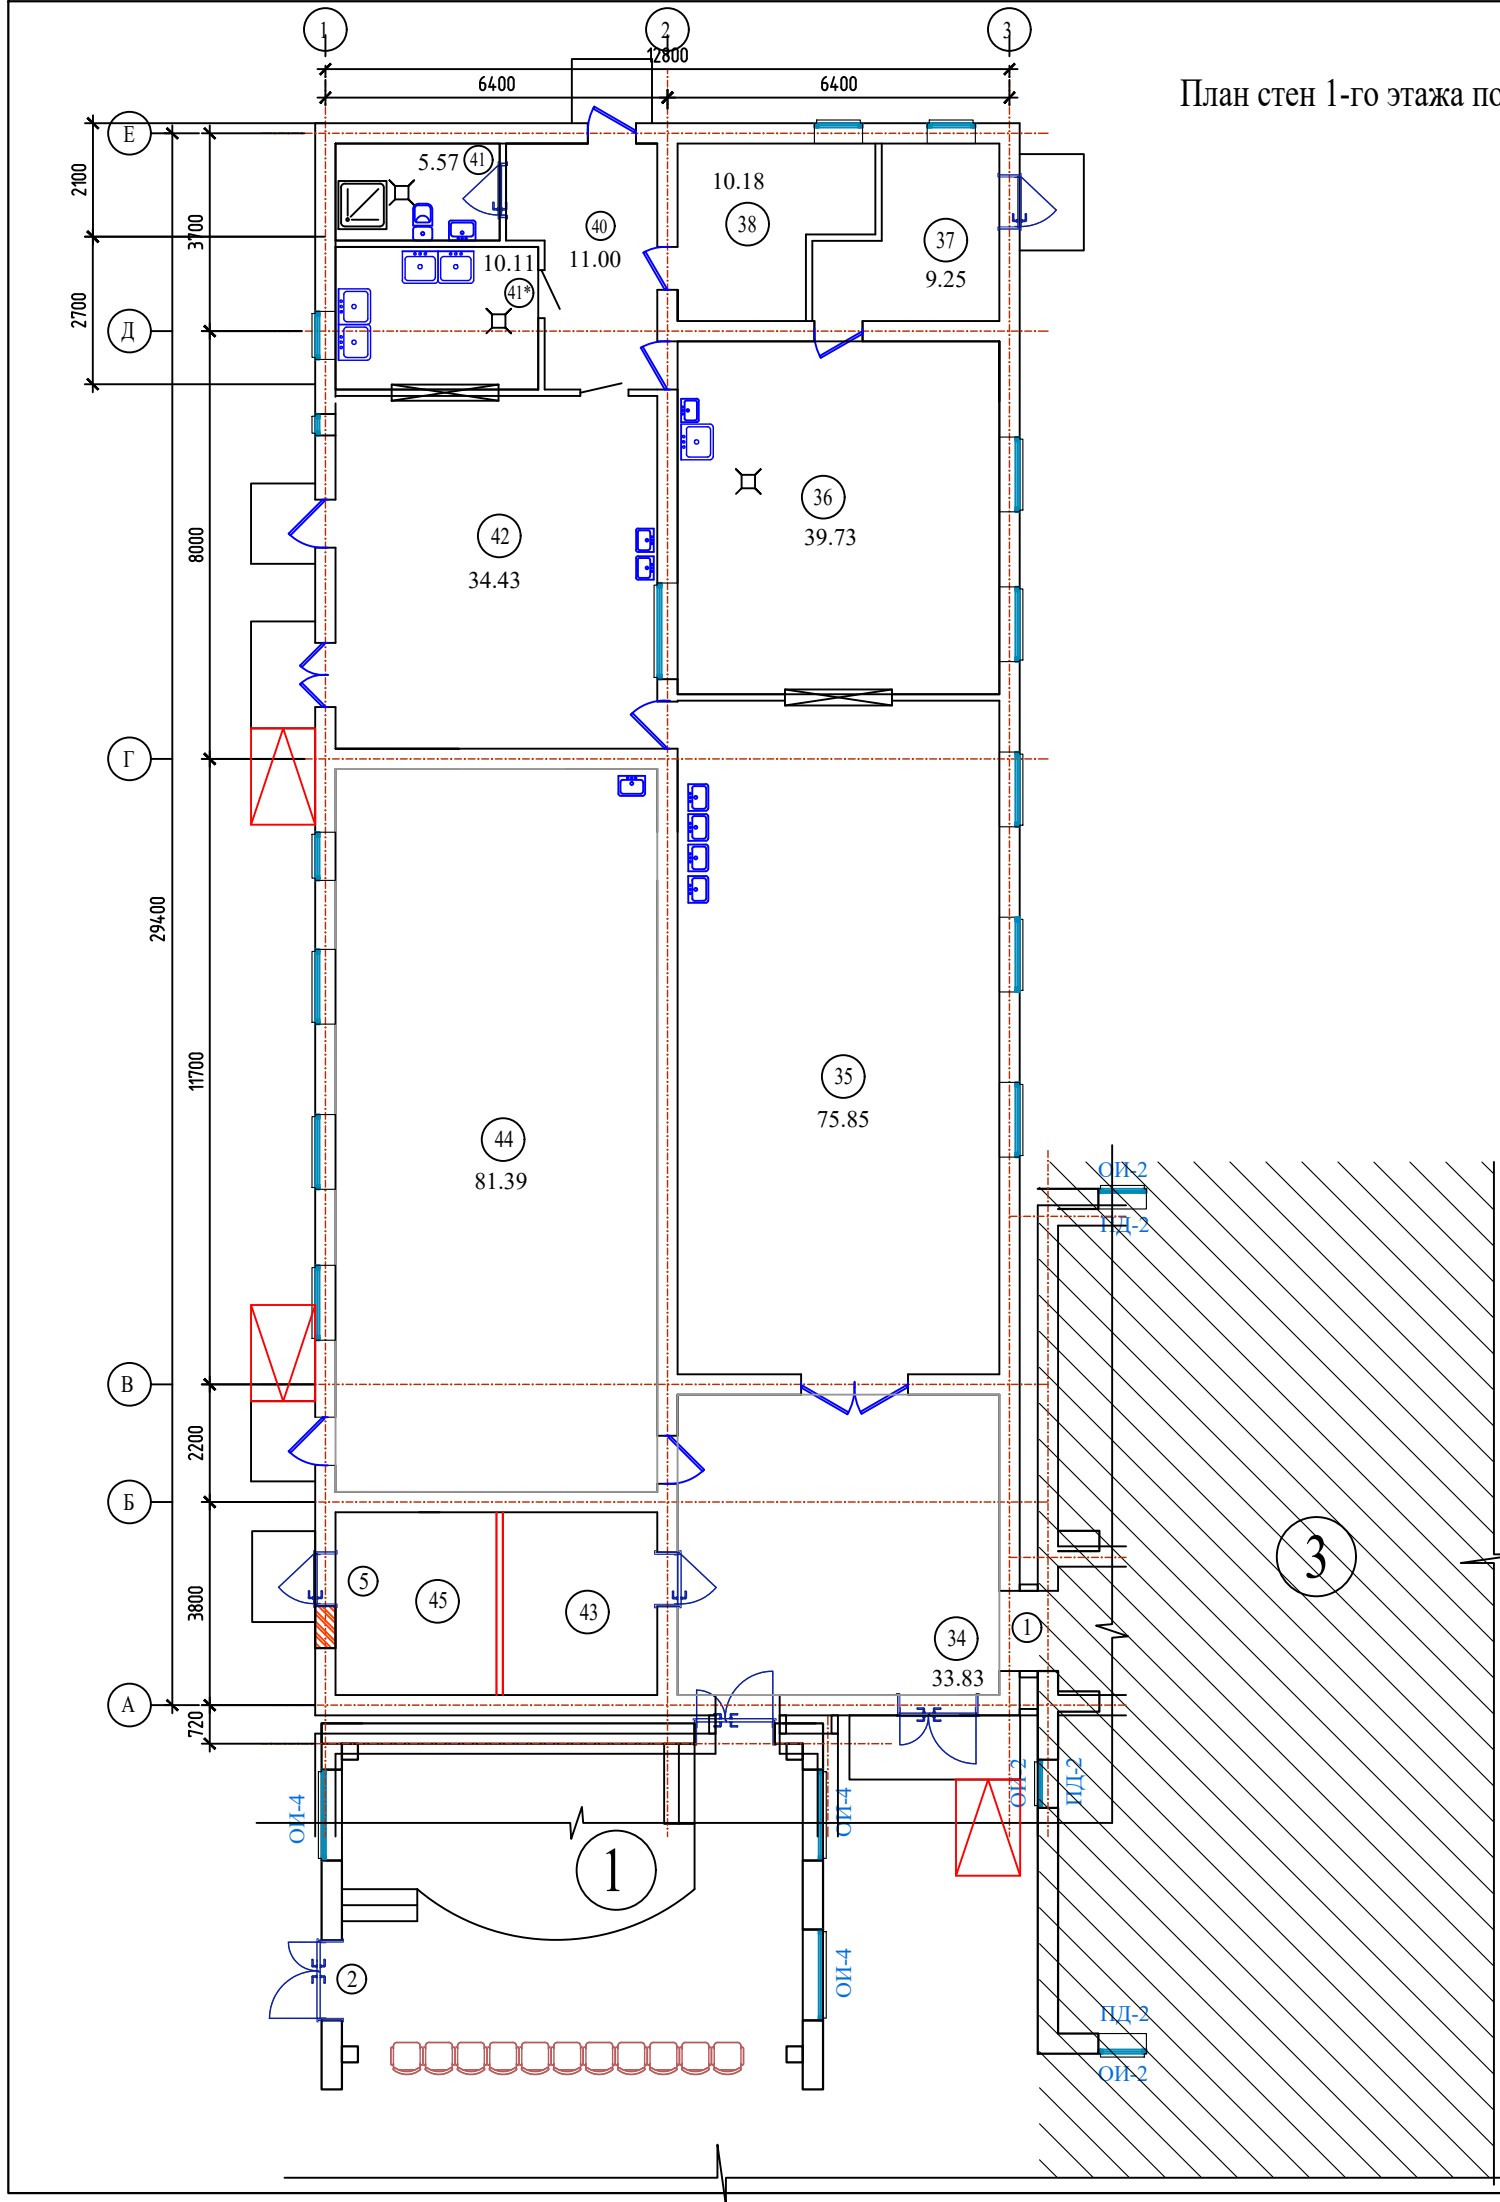




План стен 1-го этажа после реконструкция.

Экспликация помещений		
Номер пом.	Наименование	Площадь м²
34	Коридор	33.83
35	Обеденный зал	75.85
36	Кухня с раздаточной	36.62
37	Загрузочная	9.25
38	Комната персонала	10.18
39	Коридор	11.00
40	Санузел	5.57
41	Мойка	10.11
42	Обеденный зал	34.43
43	Инвентарная	10.2
44	Кабинет труда	81.39
45	Узел ввода	10.2
		328.6

Схема блокировки

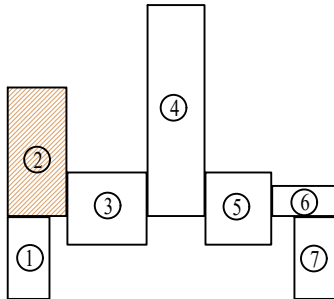

						Договор	АР				
						Капитальный ремонт школы №10 на 460 учащихся мест в СГМ "Пахтаобод" Китабского района Кашкадарьинской области					
Изм.	Колич.	Лист	Ндок.	Подпись	Дата	Существующий учебный корпус Блок 2	Стадия	Лист	Листов		
ГИП		Собирова М					ТП	2	-		
ГАП		Валижонов Х									
Разраб.		Пазиров.К.М				План стен 1-го этажа после реконструкция.	ГУ "QISHLOQ QURILISH LOYIHA" г. Фергана 2025 г.				
											

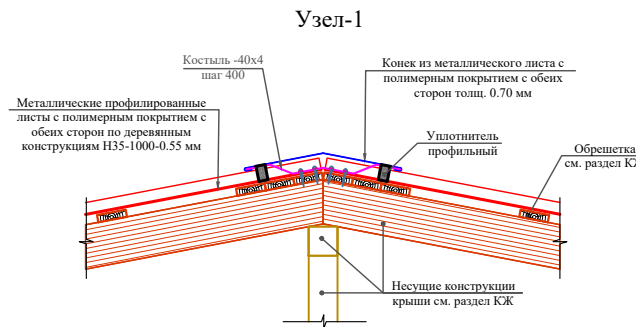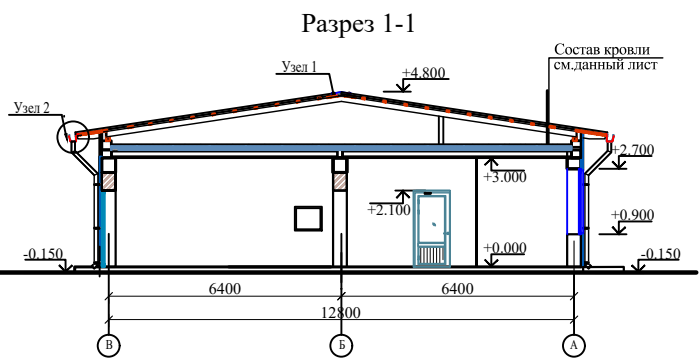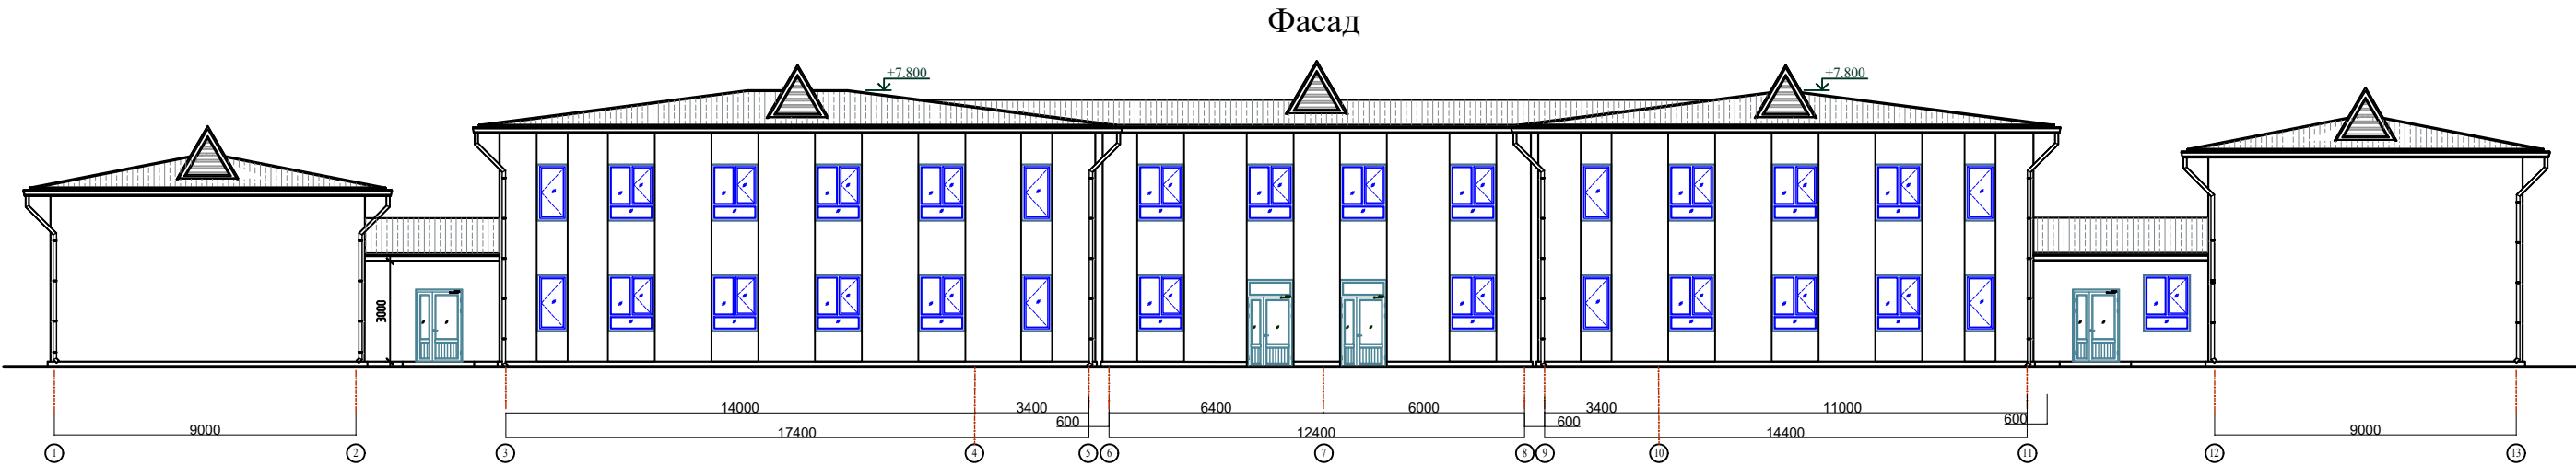

- Состав утеплителя наружных стен**
- | | |
|---|----------|
| 1. Простая штукатурка цементно-песчаным раствором | -10мм |
| 2. Клеевая смесь. | -10мм. |
| 3. Утеплитель (минераловатная плита). | -50мм. |
| 4. Штукатурный клеевой слой толщ. 3мм. | - 5-7мм. |
| 5. Стекловолоконная сетка (ячейка 5x5мм) | |
| 6. Штукатурный клеевой слой толщ. 2мм. | |
| 7. Декоративно - отделочный слой толщ. 2мм. | |

- Примечание**
- Цветовое решение фасадов, текстуру и фактуру материалов см. согласованный демонстрационный материал.
 - Все материалы применяемые для устройства фасадов должны соответствовать техническим условиям и иметь сертификаты соответствия с обязательным предоставлением их фирмой изготовителем, исполнителем заказчику.
 - Работы по отделке фасадов выполнять в соответствии с требованиями СНиП 3.04.01-87 "Изоляционные и отделочные покрытия".
 - Цвета отделочных материалов фирме исполнителю согласовать с заказчиком.
 - По периметру откосов и по наружным углам стен установить угол перфорированный с сеткой.
 - Ведомость отделки фасадов см. АР-13.

- СОСТАВ КРОВЛИ №1**
- Металлические профилированные листы с полимерным покрытием с обеих сторон, по деревянным конструкциям (РСТУз 24045-94)Н35-1000-0,55 мм(см. КЖ)
 - Цементно-песчаная смесь - ЦПС, М 150 (ГОСТ 28013-98), из полусухой смеси - толщ.50 мм. с армированием сеткой из Ø4 АСК (АБК) шаг 150 х 150 мм. с устройством деформационных швов шагом 6.0 х 6.0 м (с заполнением д.ш. герметиком)
 - Гидроизоляционная мембрана из нетканного полипропиленового полотна*) -1 слой
 - Утеплитель - минеральные плиты на основе базальтового волокна
 $\gamma = 120 \text{ кг/м}^3$, толщ. 50 мм. (в два слоя) - 100 мм.
 - Пароизоляция из полиэтиленовой пленки - 200мкм.
 - Сборная железобетонная плита покрытия - 220 мм
- *) Нетканое полипропиленовое полотно – это материал изготавливаемый из полипропиленовых нитей, скрепленных термическим способом (термоскрепление). Поверхностная плотность возможна от 10 до 150 г/м².

Ведомость отделки фасада				
Поз. отделки	Наименование элемента фасада	Наименование материала отделки	Наименование и номер эталона цвета или образец колера	Примечан. Площадь, м²
1	Цоколь	Изоляция цоколя теплоизолирующие декоративные фасадные сэндвич панели с пенополиуретаном 16мм	(цвета- подбирать по показательному материалу)	11.0
2	Стены	Очистка 100% существующей отделки фасада с последующей заменой и нанесением новых слоев	-	195.0
2*		(Состав утеплителя см.раздел-КЖ).	-	
3		2. Декоративный отделочный слой под травертин по готовым поверхностям.	(цвета- подбирать по показательному материалу)	
4	Покрытие крыльца	Мрамор (нескользящие)	-	8,76

						Договор	АР				
						Капитальный ремонт школы №10 на 460 учащихся мест в СГМ "Пахтабод" Китабского района Кашкадарьинской области					
Изм.	Кол.уч.	Лист	Н.док	Подпись	Дата	Существующий учебный корпус Блок 2			Стация	Лист	Листов
Гип				Собинова М.					РП	4	-
ГАП				Валижонов Х.		Фасад			ГУ "QISHLOQ QURILISH LOYIHA" г. Фергана 2025 г.		
Разраб.				Назиев К.М.							
											

ВЕДОМОСТЬ ОСНОВНЫХ КОМПЛЕКТОВ РАБОЧИХ ЧЕРТЕЖЕЙ		
Обозначение	Наименование	Примечание
АР	Архитектурное решение	
КС	Конструктивное решение	
ТХ	Технологическое решение	
ОВ	Отопление, вентиляция и кондиционирование	
	воздуха.	
ВК	Водопровод и канализация	
ЭМ	Электроосвещение и электрооборудование	
ПС	Пожарная сигнализация	
СС	Связь и сигнализация	
АСС	Автоматизация сантехсистем	

ВЕДОМОСТЬ ССЫЛОЧНЫХ И ПРИЛАГАЕМЫХ ДОКУМЕНТОВ		
Обозначение	Наименование	Примечание
	Ссылочных	
ГОСТ 24698-81	Двери наружные и служебные для жилых и общественных зданий.	
Серия 2.244-1 вып. 5	Детали полов общественных зданий.	
Серия 2.130-6с вып. 1	Узлы стен жилых и общественных зданий возводимых в районах сейсмичн. 7;8 и 9 балл.	
Серия 2.260-1 вып. 2	Детали покрытий общественных зданий.	

Проект соответствует требованиям технологических,санитарно-гигиенических, противопожарных и других норм, действующих на территории Республики Узбекистан и обеспечивает безопасную для жизни и здоровья эксплуатацию объекта при соблюдении предусмотренных рабочими чертежами мероприятий.

Главный инженер проекта



М.Собирова




Ведомость рабочих чертежей основного комплекта марки АР.		
№ Лист	НАИМЕНОВАНИЕ	ПРИМЕ-НИЕ
1	Общие данные	
2	План стен 1-го этажа после реконструкция.	
3	План стен 2-го этажа после реконструкция.	
4	План кровля после реконструкция.	
5	Разрез Г-А	
6	Фасад	
7	Схема элементов заполнения дверных проемов	
8	Схема элементов заполнения оконных проемов	
9	Ведомость отделки помещений	
10	Экспликация полов; План полов 1-этажа	
11	Экспликация полов; План полов 2-этажа	
12	Схема крепления плит утеплителя; Схема усиления оконных и дверных проемов	
13	Узлы по наружным стенам; Пример схемы отлива	

ОБЪЕМНО-ПЛАНИРОВОЧНЫЕ ПОКАЗАТЕЛИ			
№ п/п	Наименование показателей	Ед.изм	Площадь
1	Общая площадь	м ²	490.0
2	Строительный объем	м ³	2071.4
3	Площадь застройки	м ²	287.7


ОБЩИЕ УКАЗАНИЯ

Характеристика участка строительства:
Расчетная зимняя температура воздух - 15 °С.
Скоростной напор ветра - 38кг/м².
Вес снегового покрова - **50**кг/м².
Сейсмичность площадки - 8 баллов.
Категория грунтов по сейсмическим свойствам - III.
Расчетная сейсмичность площадки - 7-8 баллов.
Глубина промерзания грунта - 0.57 м.
Класс ответственности здания - II
Классификация зданий по функциональной пожарной опасности - Ф 3.4
Коэффициент надежности по назначению - 0.95
Степень огнестойкости - II

- Проектом реконструкции предусматривается следующие виды работ:
- Зачистка потолков с окраской 100%.
 - Демонтаж существующей кровли и устройство нового покрытия профнастила 100%.
 - Устройство 14 шт дополнительных слуховых окон;
 - Демонтаж и установка новых оконных и дверных блоков - 100%
 - Ремонт существующей штукатурки фасадов 100 %
 - Демонтаж сущ. штукатурки внутренних стен перегородок 100 %
 - Окраска фасадов фасадными красками
 - Штукатурка внутренних стен см. ведомость отделки
 - Цоколь и вертикальные поверхности крылец облицевать бетонными плитками.

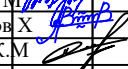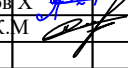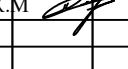
						Договор №	АР				
						Капитальный ремонт школы №10 на 460 учащихся мест в СГМ "Пахтаобод" Китабского района Кашкадарьинской области					
Изм.	Кол.уч	Лист	№ док	Подпись	Дата	Существующий учебный корпус Блок 3		Стадия	Лист	Листов	
ГИП		Собирова М						РП	1		
ГАП		Валижонов Х									
Разраб.		Пазиров.К.М									
						Общие данные		ГУ QISHLOQQURILISHLOYIHA Фаргона 2025 г.			

План стен 1-го этажа после реконструкция.

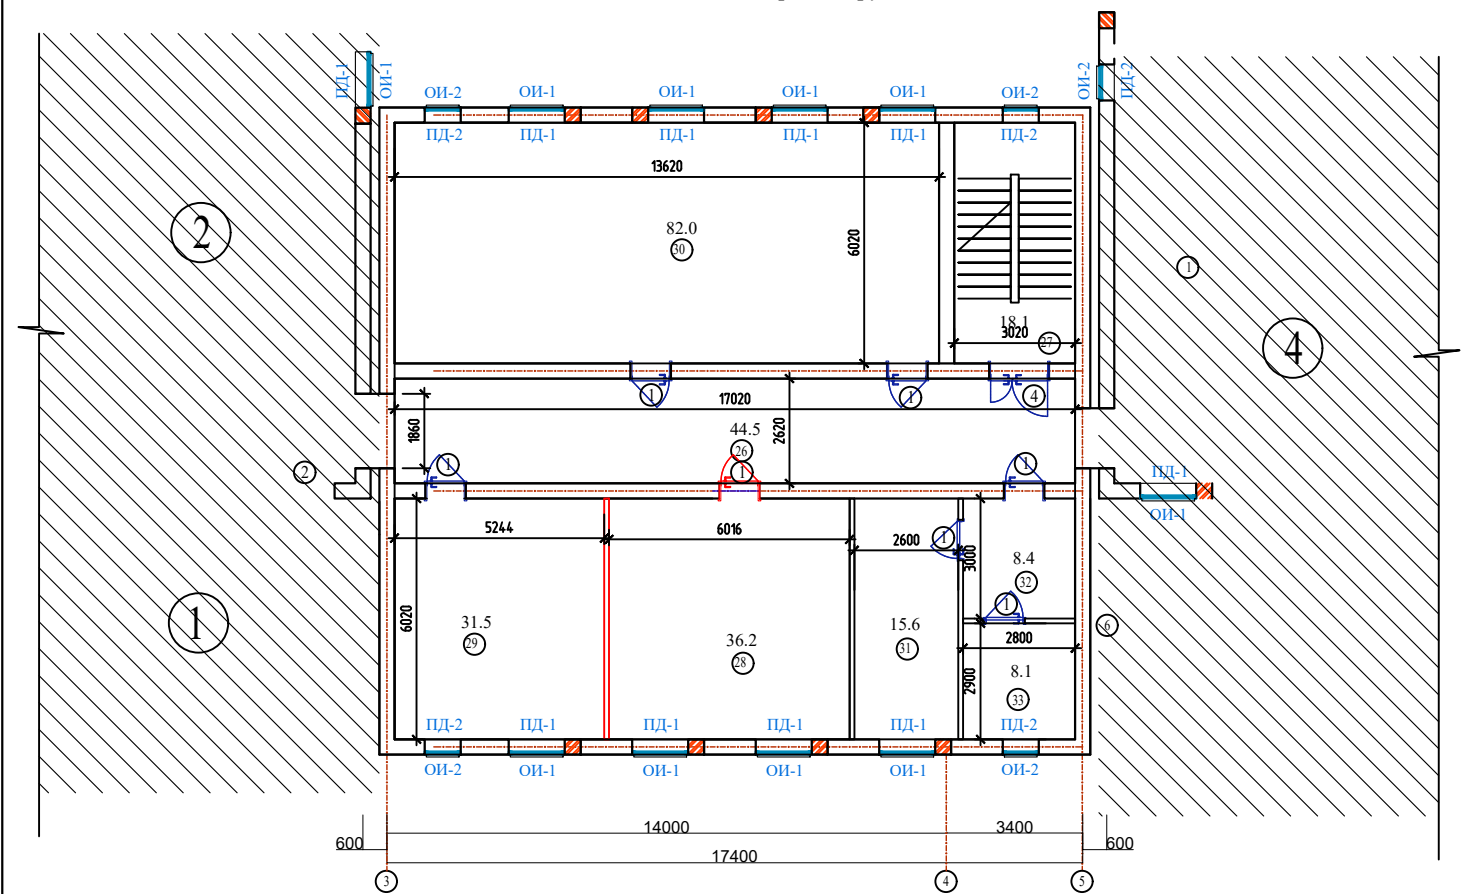


Экспликация помещений		
Номер пом.	Наименование	Площадь м²
26	Коридор	44.5
27	Лестничная клетка	18.1
28	Учительская	36.2
29	Учебный класс	31.5
30	STEM - лаборатория	82.0
31	Кабинет директора	15.6
32	Кабинет методиста	8.4
33	Кабинет заместителей директора	8.1
		244.4




Экспликация помещений 2-этаже		
Номер пом.	Наименование	Площадь м²
15	Кабинет	30.1
16	Кабинет информатики	71.6
17	Коридор	44.5
18	Лестничная клетка	18.1
19	Кабинет	16.8
20	Кабинет химии	64.5
		245.6

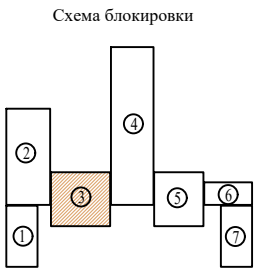

План стен 2-го этажа после реконструкция.

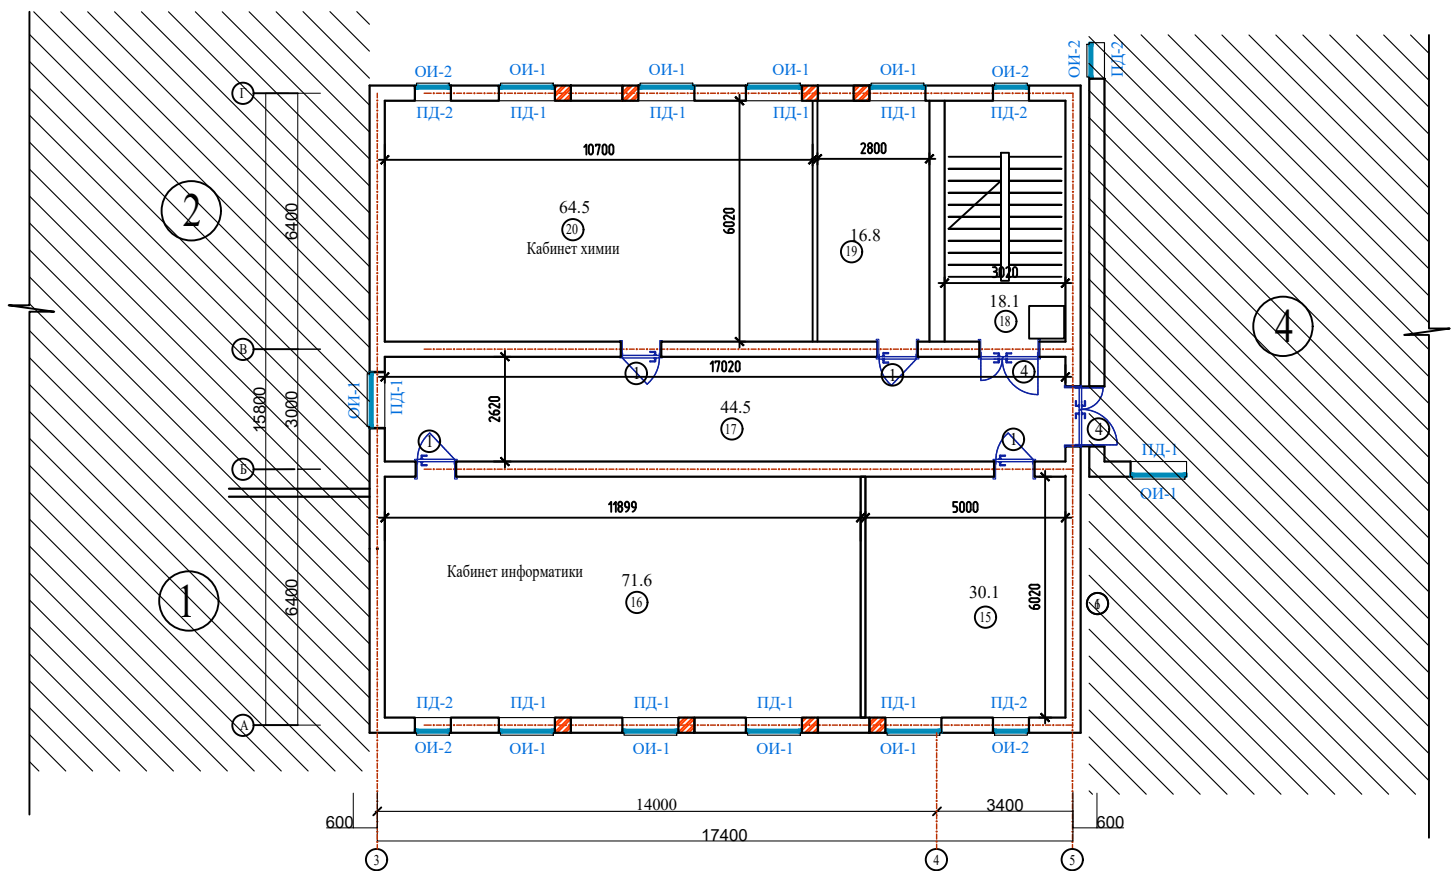

						Договор	АР					
						Капитальный ремонт школы №10 на 460 учащихся мест в СГМ "Пахтаобод" Китабского района Кашкадарьинской области						
Изм.	Коплич.	Лист	№доп.	Подпись	Дата	Существующий учебный корпус Блок 3	Стадия	Лист	Листов			
ГПП	Собирова М						ТП	2	-			
ГАП	Валижонов Х											
Разраб.	Пазилов К.М					План стен 1-го этажа после реконструкция. План стен 2-го этажа после реконструкция.	ГУ "QISHLOQ QURILISH LOYHNA" г. Фергана 2025 г.					
												

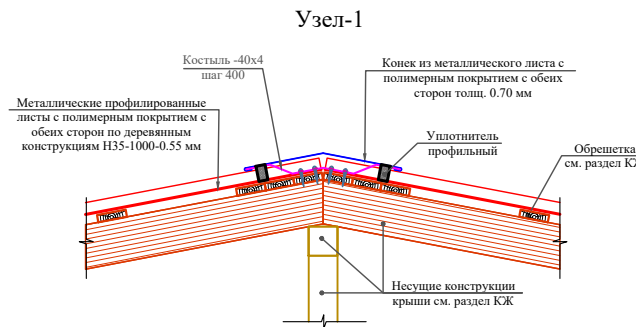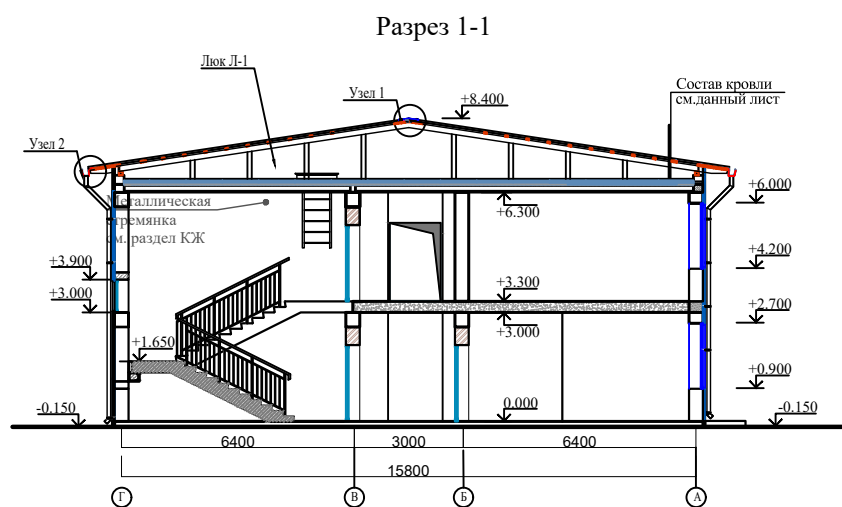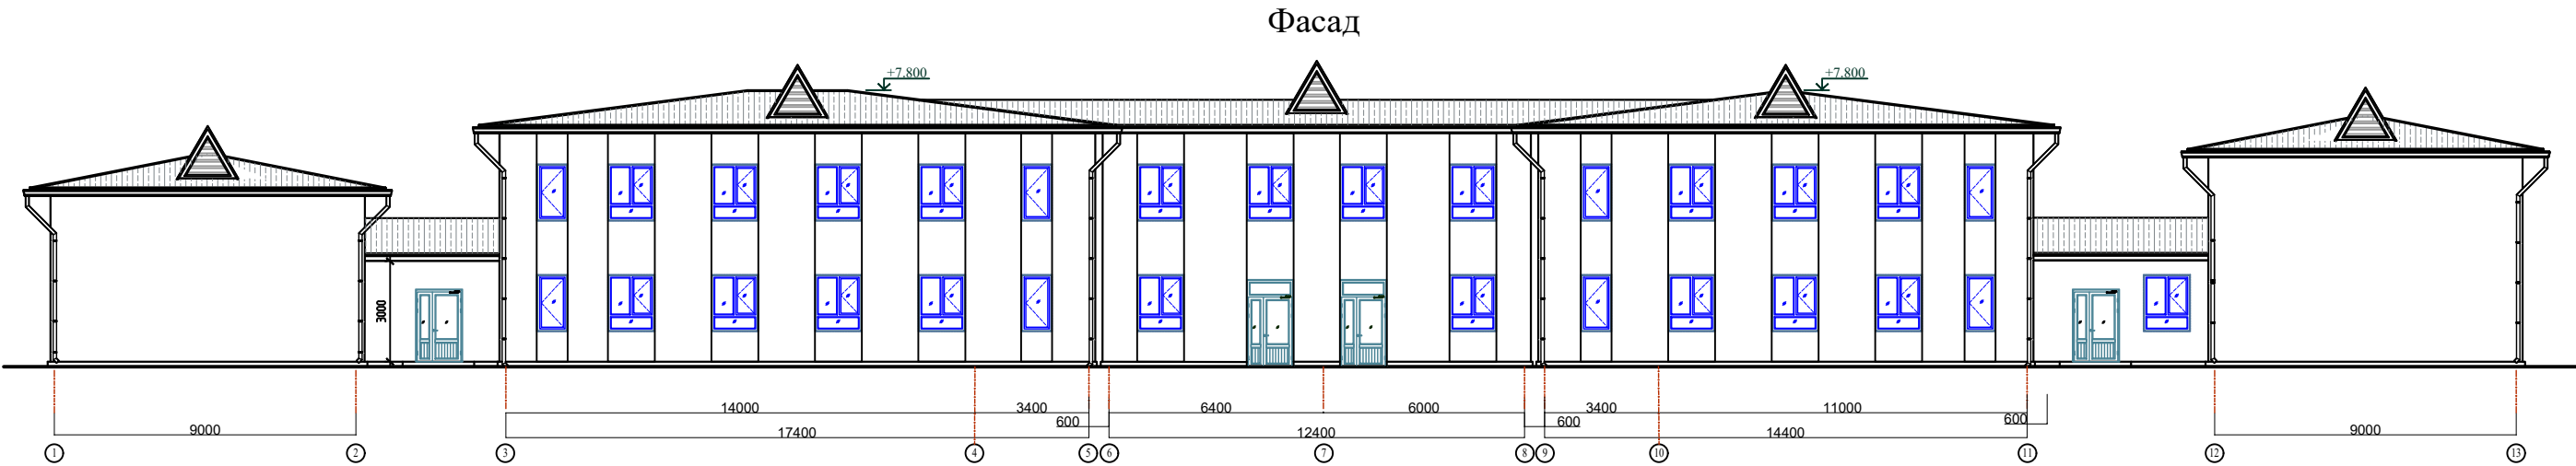


СОСТАВ КРОВЛИ №1

- Металлические профилированные листы с полимерным покрытием с обеих сторон, по деревянным конструкциям (РСТУз 24045-94)Н35-1000-0,55 мм(см. КЖ)
- Цементно-песчаная смесь - ЦПС, М 150 (ГОСТ 28013-98), из полусухой смеси - толщ.50 мм. с армированием сеткой из Ø4 АСК (АБК) шаг 150 х 150 мм. с устройством деформационных швов шагом 6.0 х 6.0 м (с заполнением д.ш. герметиком)
- Гидроизоляционная мембрана из нетканного полипропиленового полотна*) -1 слой
- Уплотнитель - минеральные плиты на основе базальтового волокна $\gamma = 120 \text{ кг/м}^3$, толщ. 50 мм. (в два слоя) - 100 мм.
- Пароизоляция из полиэтиленовой пленки - 200мкм.
- Сборная железобетонная плита покрытия - 220 мм

*) Нетканое полипропиленовое полотно – это материал изготавливаемый из полипропиленовых нитей, скрепленных термическим способом (термоскрепление). Поверхностная плотность возможна от 10 до 150 г/м².

Схема блокировки

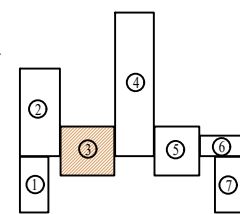

- Состав утеплителя наружных стен**
- Простая штукатурка цементно-песчаным раствором -10мм.
 - Клеевая смесь. -10мм.
 - Утеплитель (минераловатная плита). -50мм.
 - Штукатурный клеевой слой толщ. 3мм.
 - Стекловолоконная сетка (ячейка 5х5мм) - 5-7мм.
 - Штукатурный клеевой слой толщ. 2мм.
 - Декоративно - отделочный слой толщ. 2мм.

- Примечание**
- Цветовое решение фасадов, текстуру и фактуру материалов см. согласованный демонстрационный материал.
 - Все материалы применяемые для устройства фасадов должны соответствовать техническим условиям и иметь сертификаты соответствия с обязательным представлением их фирмой изготовителем, исполнителем заказчику.
 - Работы по отделке фасадов выполнять в соответствии с требованиями СНиП 3.04.01-87 "Изоляционные и отделочные покрытия".
 - Цвета отделочных материалов фирме исполнителю согласовать с заказчиком.
 - По периметру откосов и по наружным углам стен установить угол перфорированный с сеткой.
 - Ведомость отделки фасадов см. АР-13.

Ведомость отделки фасада

Поз. отделки	Наименование элемента фасада	Наименование материала отделки	Наименование и номер эталона цвета или образец колера	Примечан. Площадь, м²
1	Цоколь	Изоляция цоколя теплоизолирующие декоративные фасадные сэндвич панели с пенополиуретаном 16мм	(цвета- подбирать по показателю материалу)	8.0
2	Стены	Очистка 100% существующей отделки фасада с последующей заменой и нанесением новых слоев	-	297.0
2*		(Состав утеплителя см.раздел-КЖ).	-	
3		2. Декоративный отделочный слой под травертин по готовым поверхностям.	(цвета- подбирать по показателю материалу)	
4	Покрытие крыльца	Мрамор (нескользящие)	-	

						Договор	АР					
						Капитальный ремонт школы №10 на 460 учащихся мест в СГМ "Пахтабод" Китабского района Кашкадарьинской области						
Изм.	Кол.	Лист	№ док	Подпись	Дата	Существующий учебный корпус Блок 3			Стadia	Лист	Листов	
ТИП	Собинова М.								РП	6	-	
ТАП	Валижонов Х.											
Разраб.	Назиев К.М.											
						Фасад			ГУ "QISHLOQ QURILISH LOYIHA" г. Фергана 2025 г.			
												

Обозначение	Наименование	Примечание
АР	Архитектурное решение	
КС	Конструктивное решение	
ТХ	Технологическое решение	
ОВ	Отопление, вентиляция и кондиционирование	
	воздуха.	
ВК	Водопровод и канализация	
ЭМ	Электроосвещение и электрооборудование	
ПС	Пожарная сигнализация	
СС	Связь и сигнализация	
АСС	Автоматизация сантехсистем	

№ Лист	НАИМЕНОВАНИЕ	ПРИМЕЧАНИЕ
1	Общие данные	
2	План стен 1-го этажа после реконструкция.	
3	План стен 2-го этажа после реконструкция.	
4	План кровля после реконструкция.	
5	Разрез В-А	
6	Фасад	
7	Схема элементов заполнения дверных проемов	
8	Схема элементов заполнения оконных проемов	
9	Ведомость отделки помещений	
10	Экспликация полов; План полов 1-этажа	
11	Экспликация полов; План полов 2-этажа	
12	Схема крепления плит утеплителя; Схема усиления оконных и дверных проемов	
13	Узлы по наружным стенам; Пример схемы отлива	

ОБЪЕМНО-ПЛАНИРОВОЧНЫЕ ПОКАЗАТЕЛИ			
№ п/п	Наименование показателей	Ед.изм	Площадь
1	Общая площадь	м ²	1052.8
2	Строительный объем	м ³	4420.1
3	Площадь застройки	м ²	605.5

ОБЩИЕ УКАЗАНИЯ

Характеристика участка строительства:

Расчетная зимняя температура воздуха	- 15 °С.
Скоростной напор ветра	- 38кг/м ² .
Вес снегового покрова	- 50кг/м ² .
Сейсмичность площадки	- 8 баллов.
Категория грунтов по сейсмическим свойствам	- III.
Расчетная сейсмичность площадки	- 7-8 баллов.
Глубина промерзания грунта	- 0.57 м.
Класс ответственности здания - II	
Классификация зданий по функциональной пожарной опасности	
Коэффициент надежности по назначению - 0.95	
Степень огнестойкости - II	

Проектом реконструкции предусматриваются следующие виды работ:

1. Зачистка потолков с окраской 100%.
2. Демонтаж существующей кровли и устройство нового покрытия профнастила 100%.
3. Устройство 14 шт дополнительных слуховых окон;
4. Демонтаж и установка новых оконных и дверных блоков - 100%
5. Ремонт существующей штукатурки фасадов 100 %
6. Демонтаж сущ. штукатурки внутренних стен перегородок 100 %
7. Окраска фасадов фасадными красками
8. Штукатурка внутренних стен см. ведомость отделки
9. Цоколь и вертикальные поверхности крылец облицевать бетонными плитками.

Обозначение	Наименование	Примечание
	Ссылочных	
ГОСТ 24698-81	Двери наружные и служебные для жилых и общественных зданий.	
Серия 2.244-1 вып. 5	Детали полов общественных зданий.	
Серия 2.130-6с вып. 1	Узлы стен жилых и общественных зданий возводимых в районах сейсмичн. 7;8 и 9 балл.	
Серия 2.260-1 вып. 2	Детали покрытий общественных зданий.	

Согласовано:	


Инв. N подл.	Подпись и дата	Взам. инв. N

Проект соответствует требованиям технологических, санитарно-гигиенических, противопожарных и других норм, действующих на территории Республики Узбекистан и обеспечивает безопасную для жизни и здоровья эксплуатацию объекта при соблюдении предусмотренных рабочими чертежами мероприятий.


Главный инженер проекта  М.Собирова

						Договор №	АР				
						Капитальный ремонт школы №10 на 460 учащихся мест в СГМ "Пахтаобод" Китабского района Кашкадарьинской области					
Изм.	Кол.ун	Лист	N.док	Подпись	Дата	Существующий учебный корпус Блок 4		Стадия	Лист	Листов	
ГИП	Собирова М							РП	1	-	
ГАП	Валижонов X										
Разраб.	Пазиллов К.М										
						Общие данные		ГУ QISHLOQQURILISHLOYIHA Фаргона 2025 г.			

План стен 1-го этажа после реконструкция.

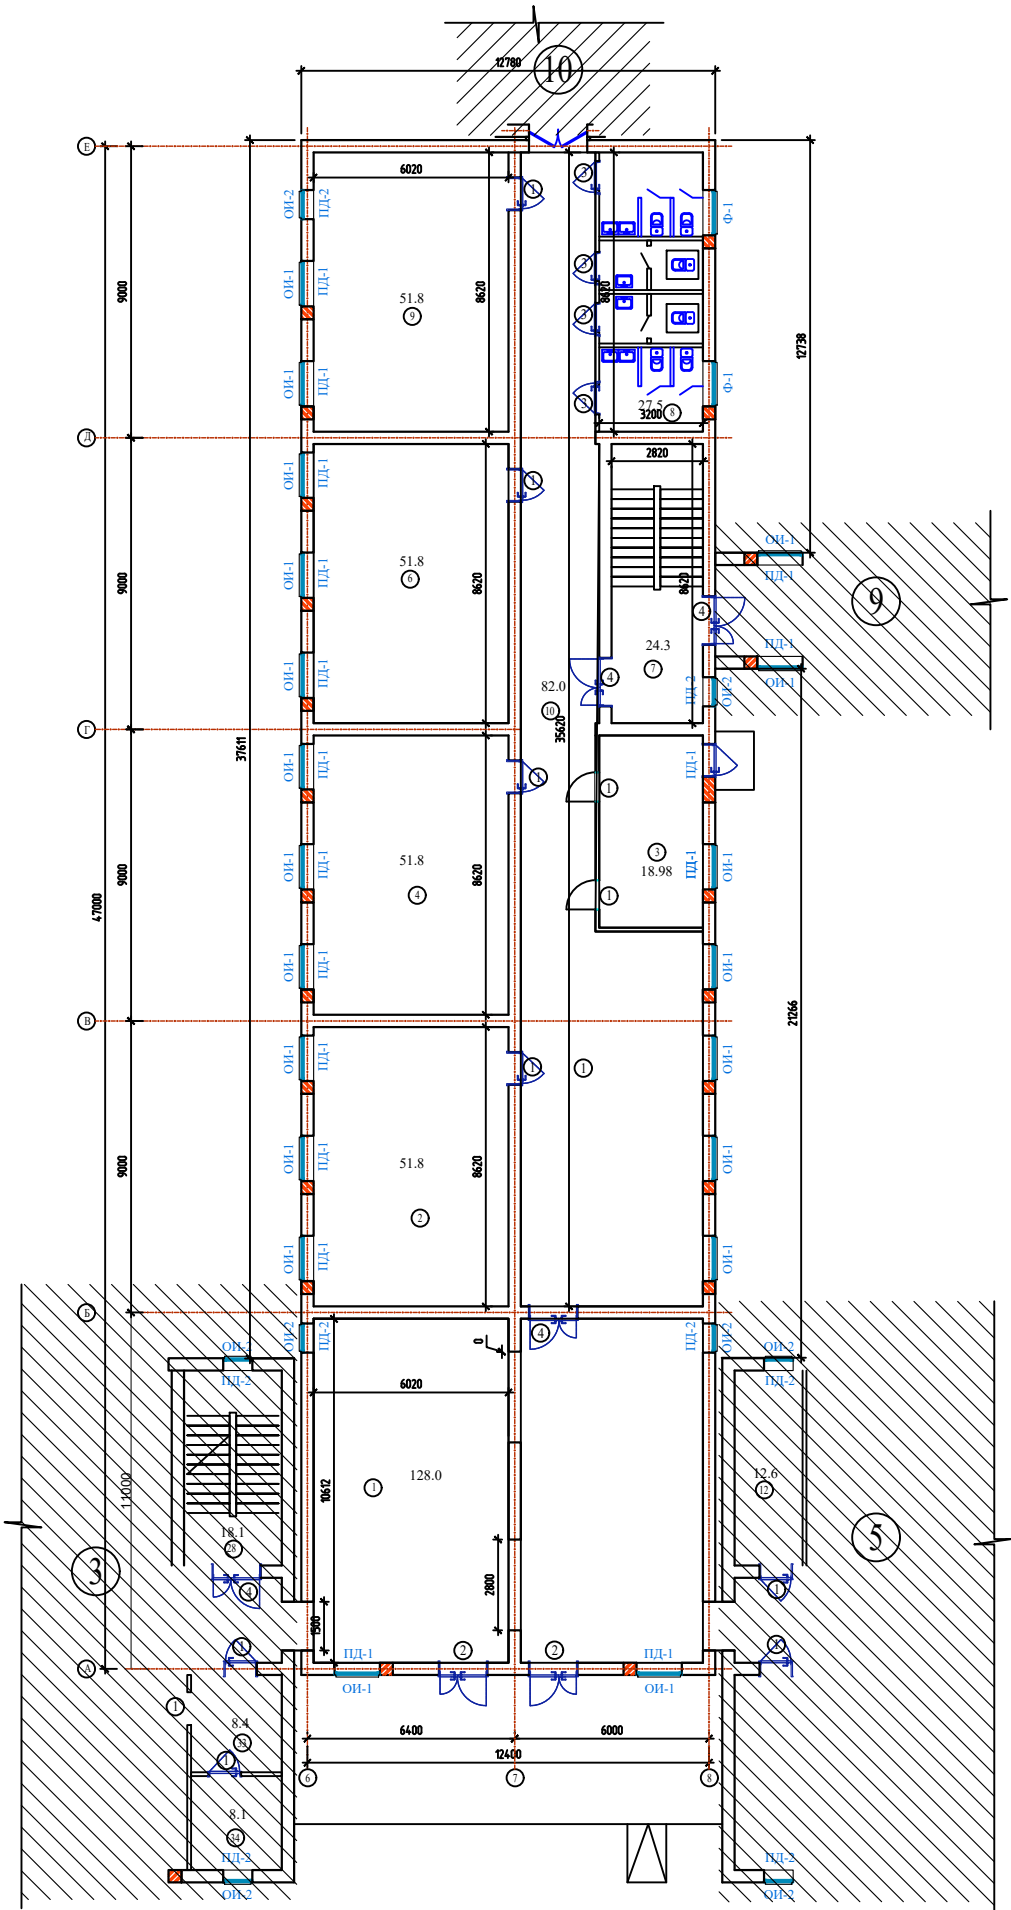


План стен 2-го этажа после реконструкция.

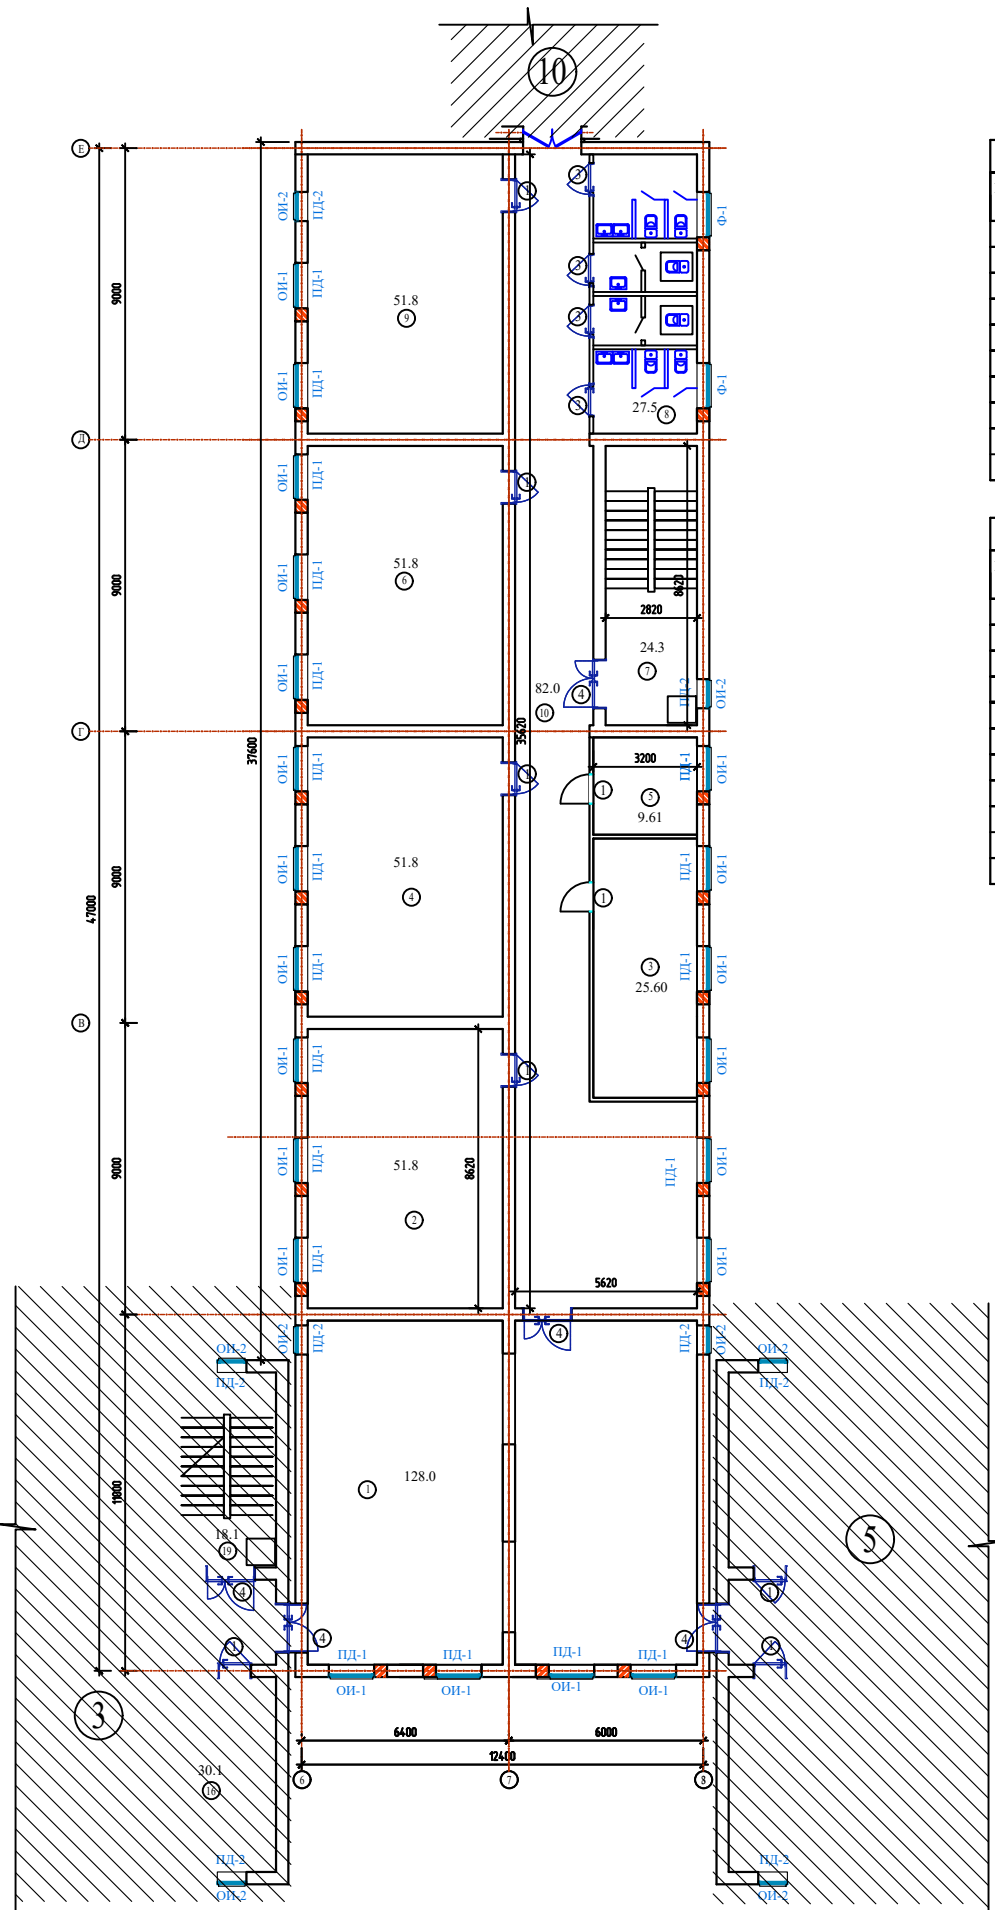

Экспликация помещений		
Номер п.м.	Вестибюль Наименование	Площадь м²
1	Вестибюль	128.0
2	Учебный класс	51.8
3	Кабинет	19.0
4	Учебный класс	51.8
5	Лестничная клетка	24.3
6	Учебный класс	51.8
7	Учебный класс	51.8
8	Сан-узлы	27.5
9	Коридор	120.35
		526.35


Экспликация помещений 2-этаж		
Номер п.м.	Вестибюль Наименование	Площадь м²
1	Фойе	128.0
2	Учебный класс	51.8
3	Кабинет	25.60
4	Учебный класс	51.8
5	Кабинет	9.61
6	Учебный класс	51.8
7	Лестничная клетка	24.3
8	Сан-узлы	27.5
9	Учебный класс	51.8
10	Коридор	104.31
		526.52

Схема блокировки

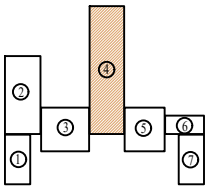



					Договор №	АР					
					Капитальный ремонт школы №10 на 460 учащихся мест в СТМ "Пахтабод" Китабского района Кашкадарьинской области						
Изм.	Кол.	уч.	Ист.	Н.д.м.	Подпис.	Дата					
ГНП	Собирова	М.	Х.	М.	2025						
ГАП	Валижон	Х.	М.	М.	2025						
Разраб.	Пазиров	К.	М.	М.	2025						
Существующий учебный корпус							Стадия	Лист	Листов		
Блок 4							РП	1	-		
							Гу				
План стен 1-го этажа после реконструкции							QISHLOQQURILISHLOVIHA				
План стен 2-го этажа после реконструкции							Фаргона 2025 г.				

План кровля после реконструкция.



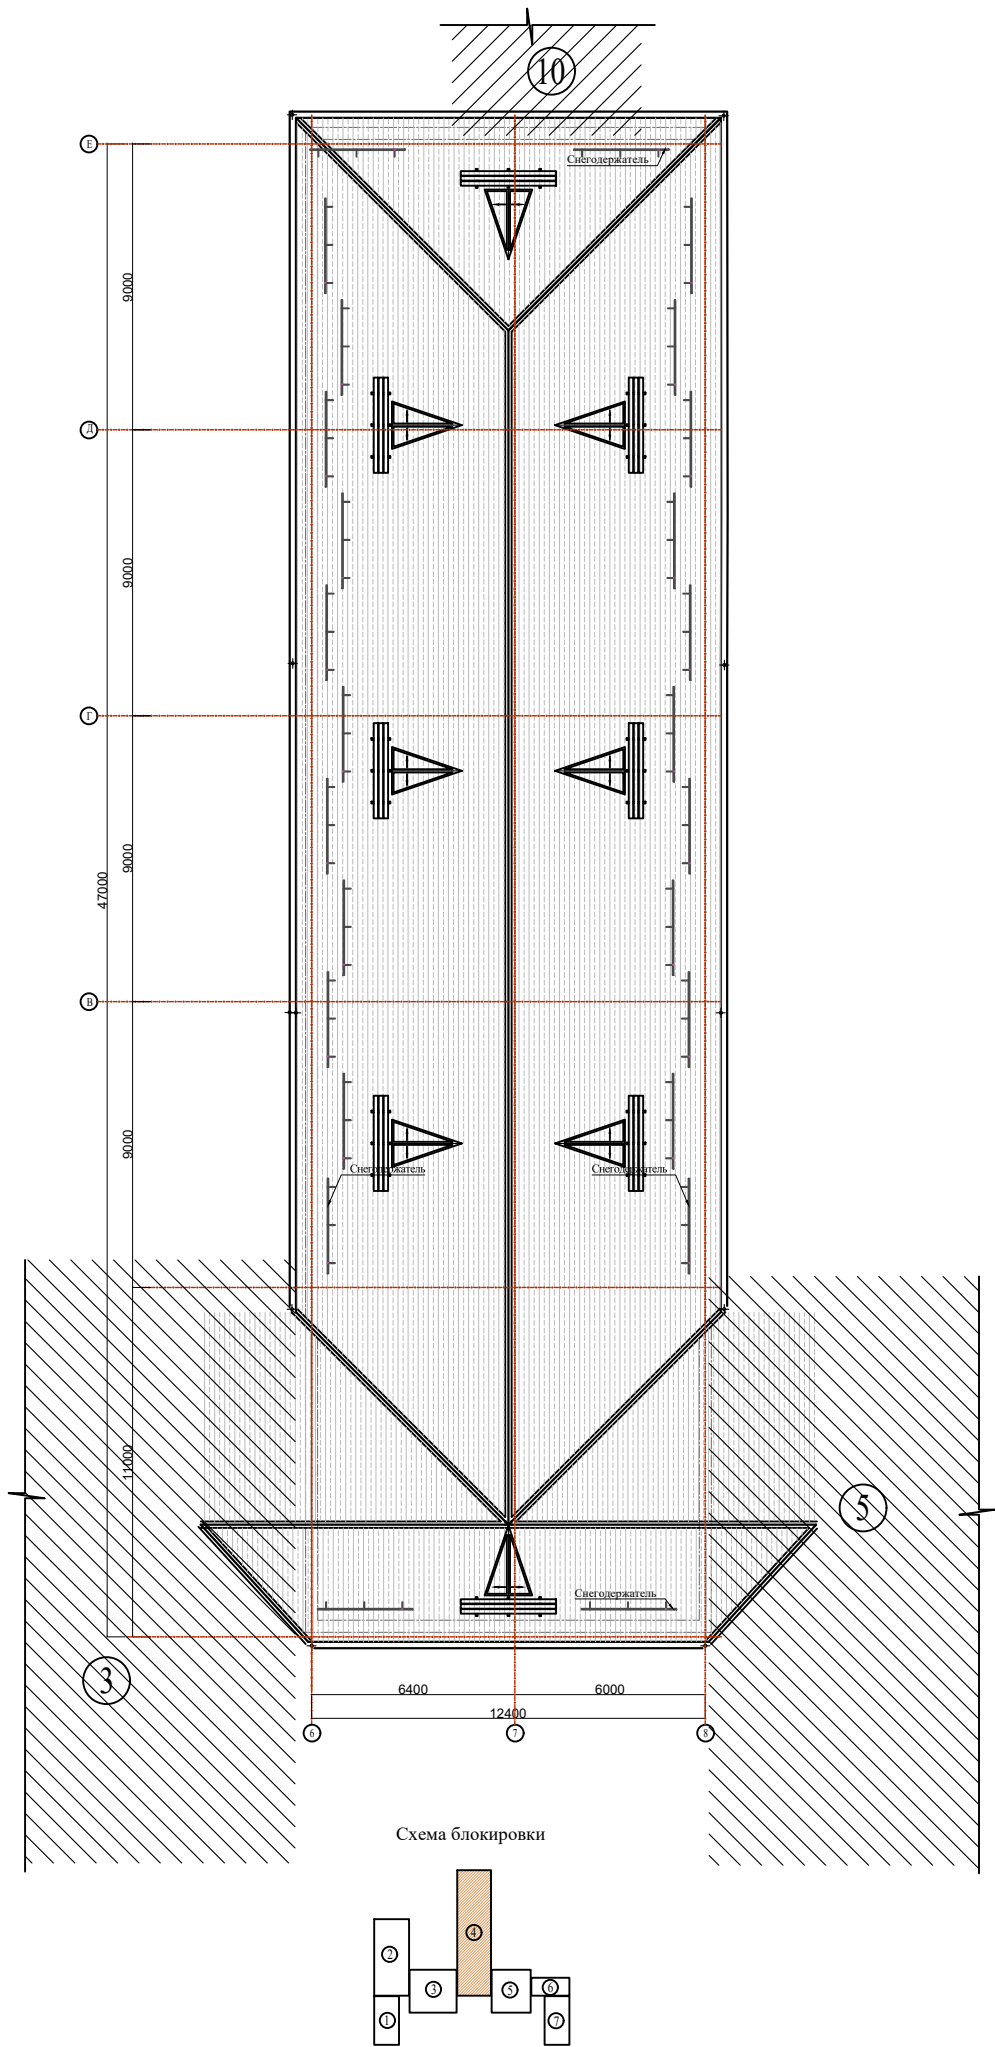


Спецификация элементов кровли					
Поз.	Обозначение	Наименование	Кол.	Масса ед. кг.	Приме- чание
		Расход материалов для кровли			
		Профилированные листы с полимерным покрытием СН3000х1064-17 т 0.55м(Крыша.)			708.9 м²
		Профилированные листы с полимерным покрытием СН3000х1064-17(Козырек.)			81.1 м²
1	Индивидуальный изготовление	Конек упрощенный	пм	123.4	
2		Водосточная латок	пм	101.2	
3		Труба водосточная	пм	28.4	
4		Воронки	шт	5	
5		Колено	шт	15	
6		Снегозадержатель	пм	101.0	
7		Кронштейн -30х4 L=600мм	60	0.60	36.0 кг
		Слуховое окно	8		

Спецификация элементов жалюзийных решеток					
Поз.	Обозначение	Наименование	Кол.	Масса ед. кг	Примеч.
Расход дан на одну жалюзийную решетку общ. кол. 8 шт.					
Жр-1	Данный лист	Жалюзийная решетка	1		шт.
	ГОСТ 8509-93	Рама из гн. уголка 50х5	2.8	3.77	п.м.
	ГОСТ 103-76	"Перо"-3х120 L=перем. ш.75мм	10	5.652	шт.
	ГОСТ 5781-82	Каркас из арматуры Ø6A240	2.9	0.222	п.м.
	ГОСТ 19903-74*	Клямеры из полосы -1х10 L=50 шагом 300	10	0.004	шт.
	ГОСТ 5336-80*	Сетка стальная P-15-1.6-0	0.5	2.57	м²

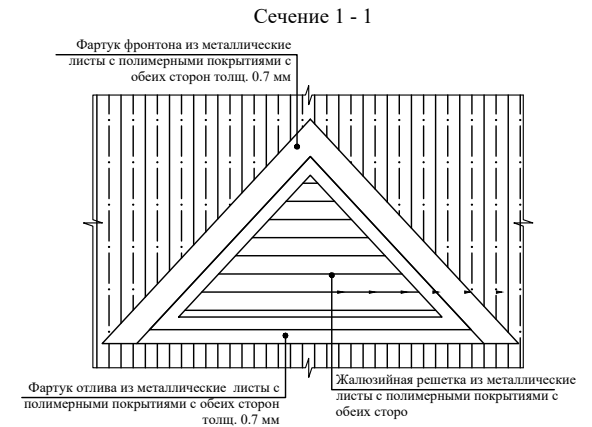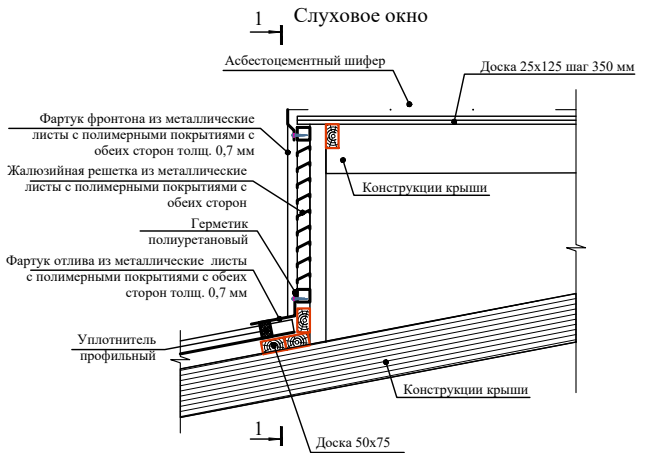

					Договор №	АР
Изм.	Кол.	Шифр	№ док	Подпись	Дата	Капитальный ремонт школы №10 на 460 учащихся мест в СГМ "Пахтабод" Китабского района Кашкадарьинской области
ГИП	Собирова М.					Существующий учебный корпус
ГАП	Валиконов Х.					Блок 4
Разраб.	Пазилов К.М.					План кровля после реконструкция.
						Студия РП
						Лист 1
						Листов -
						ГУ QISHLOOQURILISHLOYIHА Фаргона 2025 г.

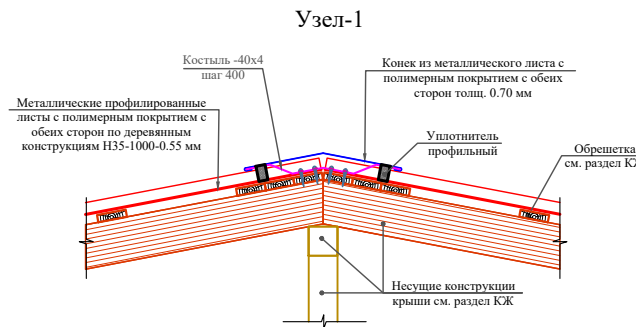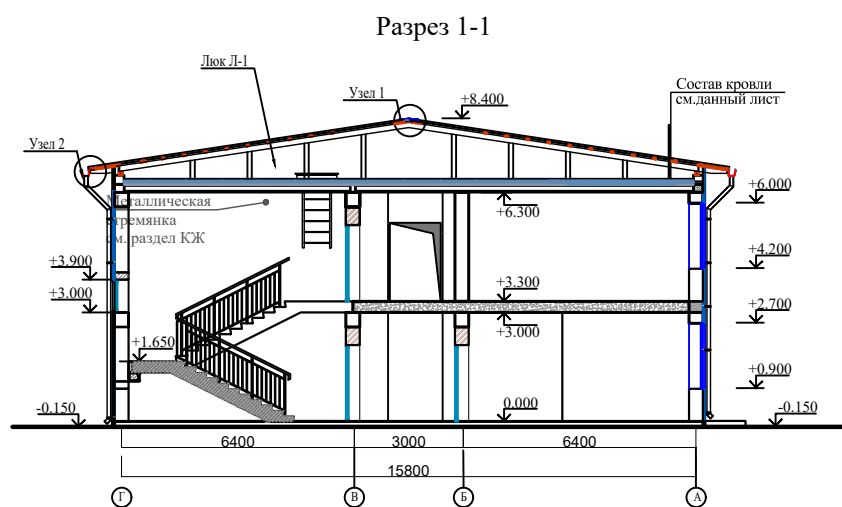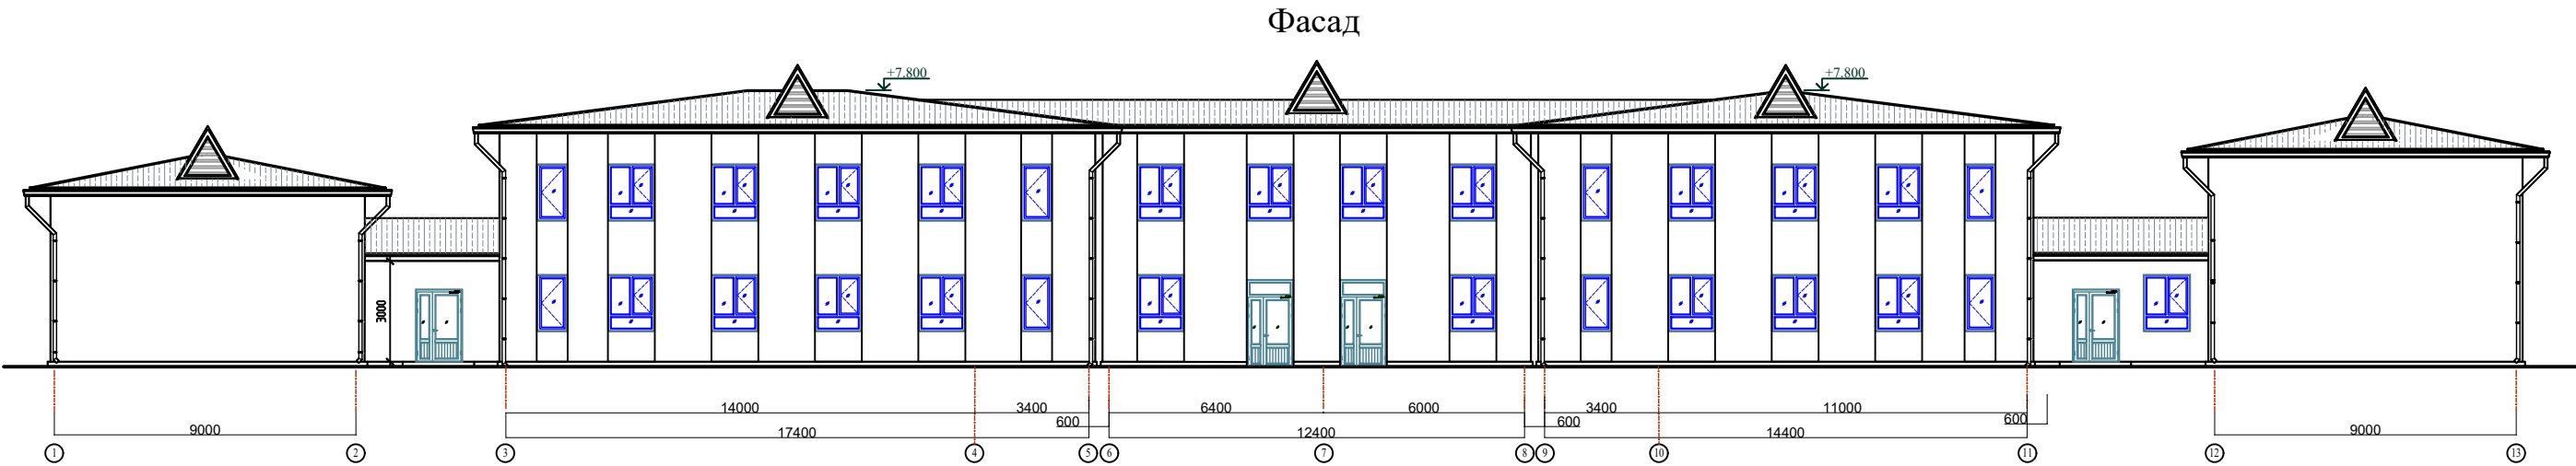


СОСТАВ КРОВЛИ №1

- Металлические профилированные листы с полимерным покрытием с обеих сторон, по деревянным конструкциям (РСТУз 24045-94)Н35-1000-0,55 мм(см. КЖ)
- Цементно-песчаная смесь - ЦПС, М 150 (ГОСТ 28013-98), из полусухой смеси - толщ.50 мм. с армированием сеткой из Ø4 АСК (АБК) шаг 150 х 150 мм. с устройством деформационных швов шагом 6.0 х 6.0 м (с заполнением д.ш. герметиком)
- Гидроизоляционная мембрана из нетканного полипропиленового полотна*) -1 слой
- Уплотнитель - минеральные плиты на основе базальтового волокна
 $\gamma = 120 \text{ кг/м}^3$, толщ. 50 мм. (в два слоя) - 100 мм.
- Пароизоляция из полиэтиленовой пленки - 200мкм.
- Сборная железобетонная плита покрытия - 220 мм

*) Нетканое полипропиленовое полотно – это материал изготавливаемый из полипропиленовых нитей, скрепленных термическим способом (термоскрепление). Поверхностная плотность возможна от 10 до 150 г/м².

Схема блокировки

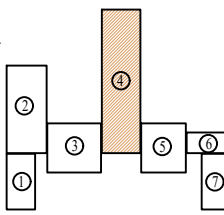

Примечание

- Цветовое решение фасадов, текстуру и фактуру материалов см. согласованный демонстрационный материал.
- Все материалы применяемые для устройства фасадов должны соответствовать техническим условиям и иметь сертификаты соответствия с обязательным представлением их фирмой изготовителем, исполнителем заказчику.
- Работы по отделке фасадов выполнять в соответствии с требованиями СНиП 3.04.01-87 "Изоляционные и отделочные покрытия".
- Цвета отделочных материалов фирме исполнителю согласовать с заказчиком.
- По периметру откосов и по наружным углам стен установить угол перфорированный с сеткой.
- Ведомость отделки фасадов см. АР-13.

Состав утеплителя наружных стен

- Простая штукатурка цементно-песчаным раствором
- Клеевая смесь.
- Утеплитель (минераловатная плита).
- Штукатурный клеевой слой толщ. 3мм.
- Стекловолоконная сетка (ячейка 5х5мм)
- Штукатурный клеевой слой толщ. 2мм.
- Декоративно - отделочный слой толщ. 2мм.

-10мм
-10мм.
-50мм.
- 5-7мм.

Ведомость отделки фасада

Поз. отделки	Наименование элемента фасада	Наименование материала отделки	Наименование и номер эталона цвета или образец колера	Примечан. Площадь, м²
1	Цоколь	Изоляция цоколя теплоизолирующие декоративные фасадные сэндвич панели с пенополиуретаном 16мм	(цвета- подбирать по показателю материалу)	18.0
2	Стены	Очистка 100% существующей отделки фасада с последующей заменой и нанесением новых слоев	-	542.0
2*		(Состав утеплителя см.раздел-КЖ).	-	
3		Декоративный отделочный слой под травертин по готовым поверхностям.	(цвета- подбирать по показателю материалу)	

						Договор	АР					
						Капитальный ремонт школы №10 на 460 учащихся мест в СГМ "Пахтабод" Китабского района Кашкадарьинской области						
Изм.	Колуч	Лист	Н.док	Подпись	Дата	Существующий учебный корпус Блок 4			Стadia	Лист	Листов	
ГИП	Собирова М.								РП	6	-	
ГАП	Валижонов Х.											
Разраб.	Назиев К.М.											
						Фасад			ГУ "QISHLOQ QURILISH LOYIHA" г. Фергана 2025 г.			
												

ВЕДОМОСТЬ ОСНОВНЫХ КОМПЛЕКТОВ РАБОЧИХ ЧЕРТЕЖЕЙ

Обозначение	Наименование	Примечание
АР	Архитектурное решение	
КС	Конструктивное решение	
ТХ	Технологическое решение	
ОВ	Отопление, вентиляция и кондиционирование	
	воздуха.	
ВК	Водопровод и канализация	
ЭМ	Электроосвещение и электрооборудование	
ПС	Пожарная сигнализация	
СС	Связь и сигнализация	
АСС	Автоматизация сантехсистем	

ВЕДОМОСТЬ ССЫЛОЧНЫХ И ПРИЛАГАЕМЫХ
ДОКУМЕНТОВ

Обозначение	Наименование	Примечание
	Ссылочных	
ГОСТ 24698-81	Двери наружные и служебные для жилых и общественных зданий.	
Серия 2.244-1 вып. 5	Детали полов общественных зданий.	
Серия 2.130-6с вып. 1	Узлы стен жилых и общественных зданий возводимых в районах сейсмичн. 7;8 и 9 балл.	
Серия 2.260-1 вып. 2	Детали покрытий общественных зданий.	

Ведомость рабочих чертежей основного
комплекта марки АР.

№ Лист	НАИМЕНОВАНИЕ	ПРИМЕ-НИЕ
1	Общие данные	
2	План стен 1-го этажа после реконструкция.	
3	План стен 2-го этажа после реконструкция.	
4	План кровля после реконструкция.	
5	Разрез Г-А	
6	Фасад	
7	Схема элементов заполнения дверных и оконных проемов	
8	Ведомость отделки помещений	
9	Экспликация полов; План полов 1-этажа	
10	Экспликация полов; План полов 2-этажа	
11	Схема крепления плит утеплителя; Схема усиления оконных и дверных проемов	
12	Узлы по наружным стенам; Пример схемы отлива	

ОБЪЕМНО-ПЛАНИРОВОЧНЫЕ ПОКАЗАТЕЛИ

№ п/п	Наименование показателей	Ед.изм.	Площадь
1	Общая площадь	м²	406,8
2	Строительный объем	м³	1745.4
3	Площадь застройки	м²	239.1

ОБЩИЕ УКАЗАНИЯ

Характеристика участка строительства:


Расчетная зимняя температура воздуха	- 15 °С.
Скоростной напор ветра	- 38кг/м ² .
Вес снегового покрова	- 50кг/м ² .
Сейсмичность площадки	- 8 баллов.
Категория грунтов по сейсмическим свойствам	- III.
Расчетная сейсмичность площадки	- 7-8 баллов.
Глубина промерзания грунта	- 0.57 м.
Класс ответственности здания	- II
Классификация зданий по функциональной пожарной опасности	- Ф 3.4
Коэффициент надежности по назначению	- 0.95
Степень огнестойкости	- II

Проектом реконструкции предусматриваются следующие виды работ:

1. Зачистка потолков с окраской 100%.
2. Демонтаж существующей кровли и устройство нового покрытия профнастила 100%.
3. Устройство 14 шт дополнительных слуховых окон;
4. Демонтаж и установка новых оконных и дверных блоков - 100%
5. Ремонт существующей штукатурки фасадов 100 %
6. Демонтаж сущ. штукатурки внутренних стен перегородок 100 %
7. Окраска фасадов фасадными красками
8. Штукатурка внутренних стен см. ведомость отделки
9. Цоколь и вертикальные поверхности крылец облицевать бетонными плитками.

						Договор №	АР				
						Капитальный ремонт школы №10 на 460 учащихся мест в СГМ "Пахтаобод" Китабского района Кашкадарьинской области					
Изм.	Кол.уч.	Ист.	Н.док	Подпись	Дата	Существующий учебный корпус Блок 5		Стадия	Лист	Листов	
ГИП				Собирова М.				РП	1	-	
ГАП				Валижонов Х.							
Разраб.				Пазилев К.М.							
						Общие данные		ГУ			
								QISHLOQQURILISHLOYIHA Фаргона 2025 г.			

План стен 1-го этажа после реконструкция.

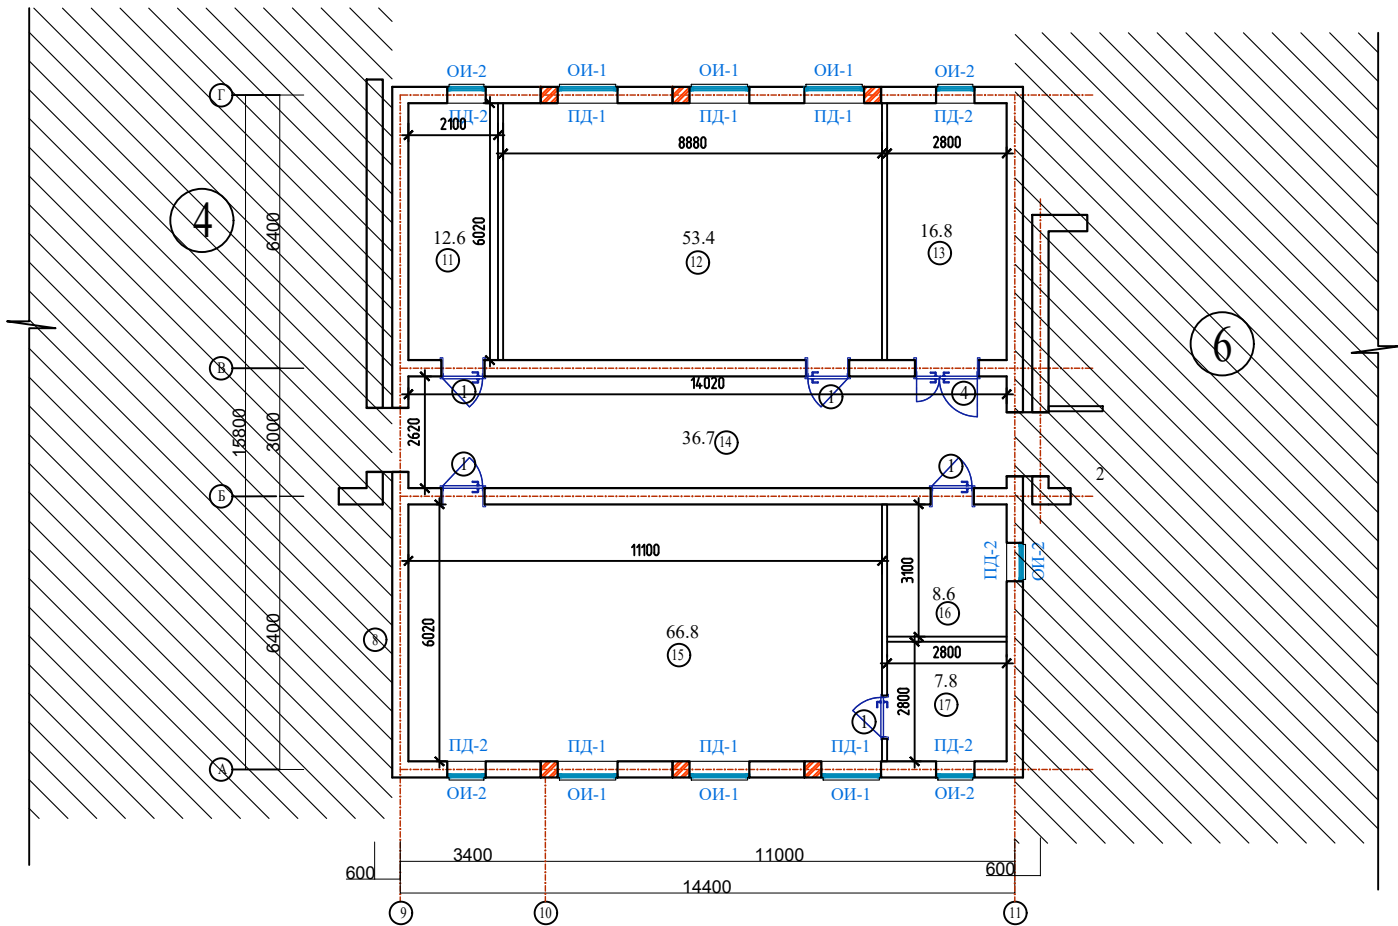

Экспликация помещений 1-этаж		
Номер пом.	Наименование	Площадь м²
11	Комната охраны	12.6
12	Кабинет истории	53.4
13	Кабинет медсестры	16.8
14	Коридор	36.7
15	Учебный класс	66.8
16	Кабинет	8.6
17	Кабинет	7.8
		202.7

Экспликация помещений 2-этаж		
Номер пом.	Наименование	Площадь м²
11	Кабинет биология	67.0
12	Кабинет	16.8
13	Коридор	36.7
14	Кабинет физика	66.8
15	Кабинет	16.8
		204.1

План стен 2-го этажа после реконструкция.





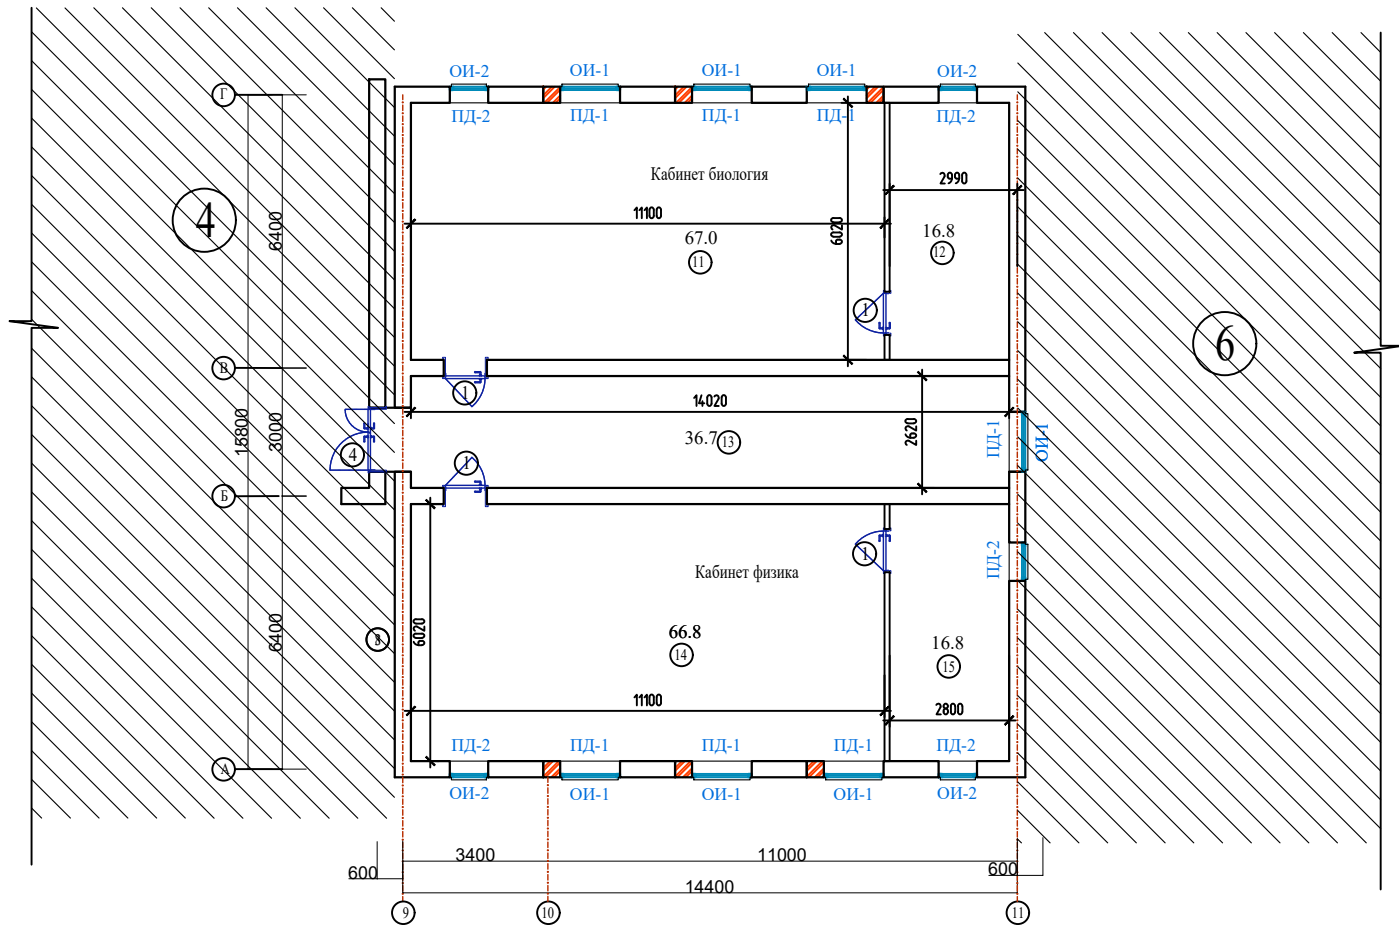


Схема блокировки

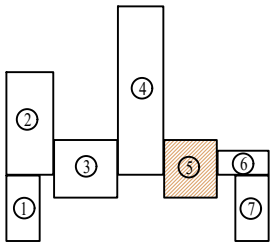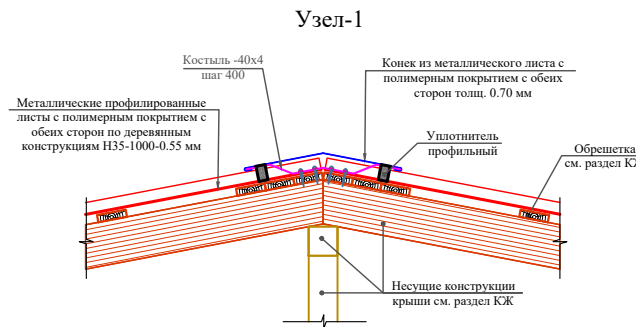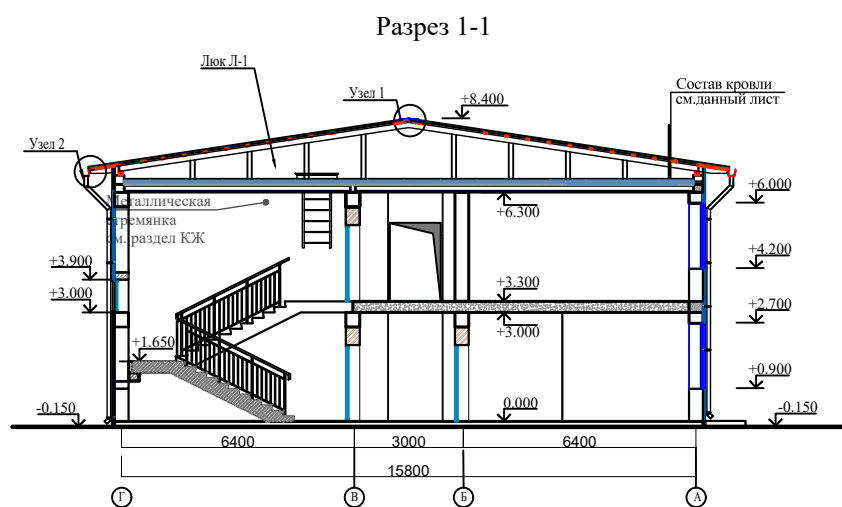

					Договор	АР			
					Капитальный ремонт школы №10 на 460 учащихся мест в СГМ "Пахтаобод" Китабского района Кашкадарьинской области				
Изм.	Коллич.	Лист	Ндос.	Подпись	Дата	Существующий учебный корпус Блок 5	Стадия	Лист	Листов
ГПП		Собирова М					ТП	2	-
ГАП		Валижонов Х							
Разраб.		Пазылов К.М				План стен 1-го этажа после реконструкция. План стен 2-го этажа после реконструкция.	ГУ "QISHLOQ QURILISH LOYIHA" г. Фергана 2025 г.		

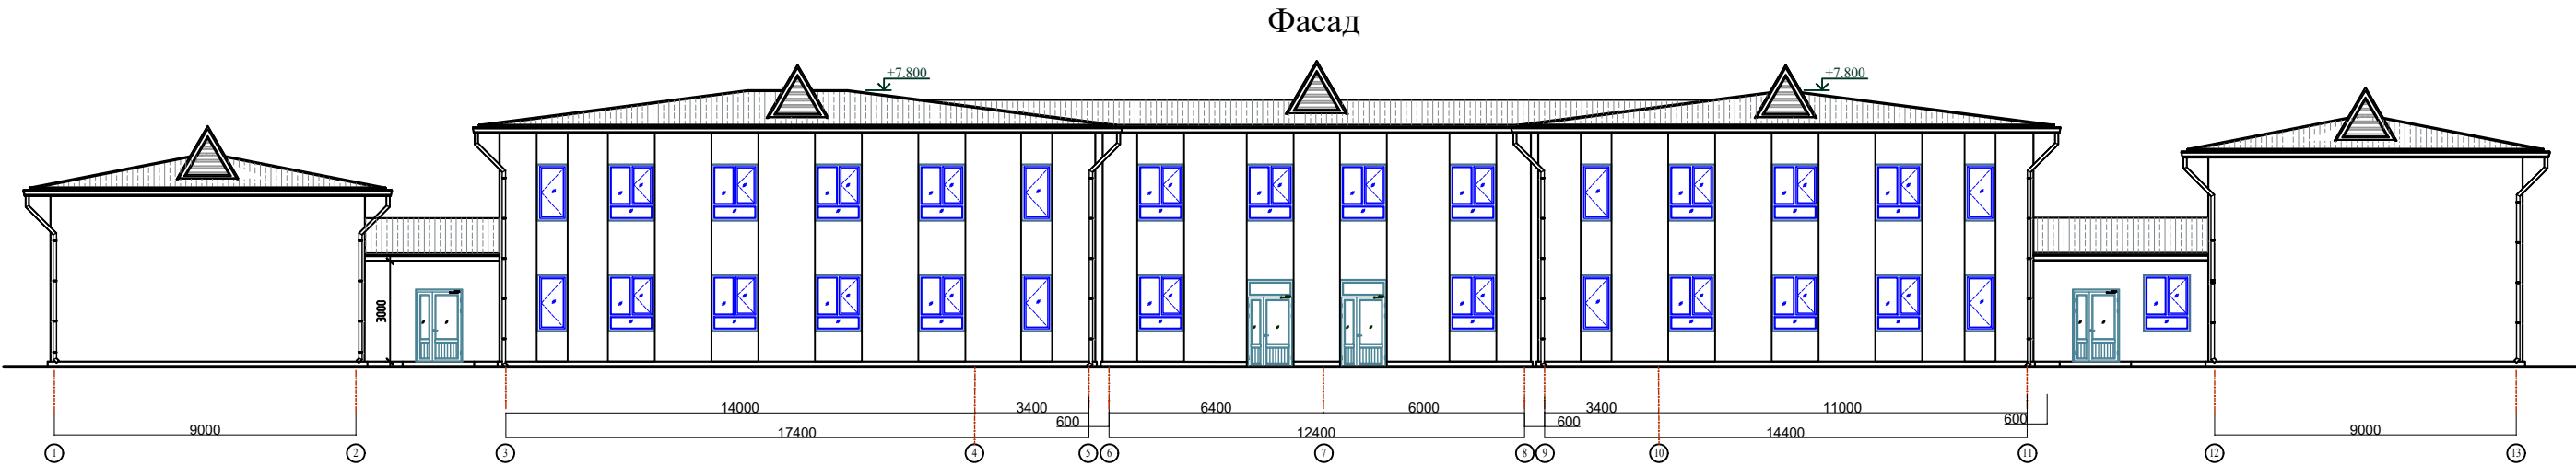

СОСТАВ КРОВЛИ №1

- Металлические профилированные листы с полимерным покрытием с обеих сторон, по деревянным конструкциям (РСТУз 24045-94)Н35-1000-0,55 мм(см. КЖ)
- Цементно-песчаная смесь - ЦПС, М 150 (ГОСТ 28013-98), из полусухой смеси - толщ.50 мм. с армированием сеткой из Ø4 АСК (АБК) шаг 150 х 150 мм. с устройством деформационных швов шагом 6.0 х 6.0 м (с заполнением д.ш. герметиком)
- Гидроизоляционная мембрана из нетканного полипропиленового полотна*) -1 слой
- Уплотнитель - минеральные плиты на основе базальтового волокна
 $\gamma = 120 \text{ кг/м}^3$; толщ. 50 мм. (в два слоя) - 100 мм.
- Пароизоляция из полиэтиленовой пленки - 200мкм.
- Сборная железобетонная плита покрытия - 220 мм

*) Нетканое полипропиленовое полотно – это материал изготавливаемый из полипропиленовых нитей, скрепленных термическим способом (термоскрепление). Поверхностная плотность возможна от 10 до 150 г/м².

Примечание

- Цветовое решение фасадов, текстуру и фактуру материалов см. согласованный демонстрационный материал.
- Все материалы применяемые для устройства фасадов должны соответствовать техническим условиям и иметь сертификаты соответствия с обязательным предоставлением их фирмой изготовителем, исполнителем заказчику.
- Работы по отделке фасадов выполнять в соответствии с требованиями СНиП 3.04.01-87 "Изоляционные и отделочные покрытия".
- Цвета отделочных материалов фирме исполнителю согласовать с заказчиком.
- По периметру откосов и по наружным углам стен установить угол перфорированный с сеткой.
- Ведомость отделки фасадов см. АР-13.

Состав утеплителя наружных стен

- Простая штукатурка цементно-песчаным раствором
 - Клеевая смесь.
 - Утеплитель (минераловатная плита).
 - Штукатурный клеевой слой толщ. 3мм.
 - Стекловолоконная сетка (ячейка 5х5мм)
 - Штукатурный клеевой слой толщ. 2мм.
 - Декоративно - отделочный слой толщ. 2мм.
- 10мм
-10мм.
-50мм.
- 5-7мм.

Ведомость отделки фасада

Поз. отделки	Наименование элемента фасада	Наименование материала отделки	Наименование и номер эталона цвета или образца колера	Примечан. Площадь, м²
1	Цоколь	Изоляция цоколя теплоизолирующие декоративные фасадные сэндвич панели с пенополиуретаном 16мм	(цвета- подбирать по показательному материалу)	15,0
2	Стены	Очистка 100% существующей отделки фасада с последующей заменой и нанесением новых слоев	-	318,0
2*		(Состав утеплителя см.раздел-КЖ).	-	
3		2. Декоративный отделочный слой под травертин по готовым поверхностям.	(цвета- подбирать по показательному материалу)	

Изм.	Колуч.	Лист	№ док.	Подпись	Дата	Договор	АР		
							Капитальный ремонт школы №10 на 460 учащихся мест в СГМ "Пахтаобод" Китабского района Кашкадарьинской области		
							Существующий учебный корпус Блок 5		
							Стация	Лист	Листов
							РП	6	-
							Фасад		
							ГУ "QISHLOQ QURILISH LOYIHASI" г. Фергана 2025 г.		

ВЕДОМОСТЬ ОСНОВНЫХ КОМПЛЕКТОВ РАБОЧИХ ЧЕРТЕЖЕЙ

Обозначение	Наименование	Примечание
АР	Архитектурное решение	
КС	Конструктивное решение	
ТХ	Технологическое решение	
ОВ	Отопление, вентиляция и кондиционирование	
	воздуха.	
ВК	Водопровод и канализация	
ЭМ	Электроосвещение и электрооборудование	
ПС	Пожарная сигнализация	
СС	Связь и сигнализация	
АСС	Автоматизация сантехсистем	

ВЕДОМОСТЬ ССЫЛОЧНЫХ И ПРИЛАГАЕМЫХ ДОКУМЕНТОВ

Обозначение	Наименование	Примечание
	Ссылочных	
ГОСТ 24698-81	Двери наружные и служебные для жилых и общественных зданий.	
Серия 2.244-1 вып. 5	Детали полов общественных зданий.	
Серия 2.130-6с вып. 1	Узлы стен жилых и общественных зданий возводимых в районах сейсмичн. 7;8 и 9 балл.	
Серия 2.260-1 вып. 2	Детали покрытий общественных зданий.	

Проект соответствует требованиям технологических,санитарно-гигиенических, противопожарных и других норм, действующих на территории Республики Узбекистан и обеспечивает безопасную для жизни и здоровья эксплуатацию объекта при соблюдении предусмотренных рабочими чертежами мероприятий.

Главный инженер проекта

М.Собирова

Согласовано:

Изм. N

подп.

Подпись и дата

Взам. инв. N

Ведомость рабочих чертежей основного комплекта марки АР.		
№ Лист	НАИМЕНОВАНИЕ	ПРИМЕ-НИЕ
1	Общие данные	
2	План стен 1-го этажа после реконструкция.	
3	План кровля после реконструкция.	
4	Разрез В-А	
5	Фасад	
6	Схема элементов заполнения дверных и оконныхпроемов	
7	Ведомость отделки помещений	
8	Экспликация полов; План полов 1-этажа	
9	Схема крепления плит утеплителя; Схема усиления оконных и дверных проемов	
10	Узлы по наружным стенам; Пример схемы отлива	

ОБЪЕМНО-ПЛАНИРОВОЧНЫЕ ПОКАЗАТЕЛИ

№ п/п	Наименование показателей	Ед.изм	Площадь
1	Общая площадь	м ²	78.2
2	Строительный объем	м ³	399.7
3	Площадь застройки	м ²	97.5

ОБЩИЕ УКАЗАНИЯ

Характеристика участка строительства:


Расчетная зимняя температура воздух - 15 °С.
Скоростной напор ветра - 38кг/м².
Вес снегового покрова - **50**кг/м².
Сейсмичность площадки - 8 баллов.
Категория грунтов по сейсмическим свойствам - III.
Расчетная сейсмичность площадки - 7-8 баллов.
Глубина промерзания грунта - 0.57 м.
Класс ответственности здания - II
Классификация зданий по функциональной пожарной опасности - Ф 3.4
Коэффициент надежности по назначению - 0.95
Степень огнестойкости - II

Проектом реконструкции предусматривается следующие виды работ:


1. Зачистка потолков с окраской 100%.
2. Демонтаж существующей кровли и устройство нового покрытия профнастила 100%.
3. Устройство 14 шт дополнительных слуховых окон;
4. Демонтаж и установка новых оконных и дверных блоков - 100%
5. Ремонт существующей штукатурки фасадов 100 %
6. Демонтаж сущ. штукатурки внутренних стен перегородок 100 %
7. Окраска фасадов фасадными красками
8. Штукатурка внутренних стен см. ведомость отделки
9. Цоколь и вертикальные поверхности крылец облицевать бетонными плитками.

							Договор №	АР			
							Капитальный ремонт школы №10 на 460 учащихся мест в СГМ "Пахтаобод" Китабского района Кашкадарьинской области				
Изм.	Кол.уч	Лист	N док	Подпись	Дата	Существующий учебный корпус Блок 6		Стадия	Лист	Листов	
ГИП				Собирова М				РП	1	-	
ГАП				Валижонов X				ГУ QISHLOQQURILISHLOYIHА Фаргона 2025 г.			
Разраб.				Пазилев.К.М							
						Общие данные					

План стен 1-го этажа после реконструкция.

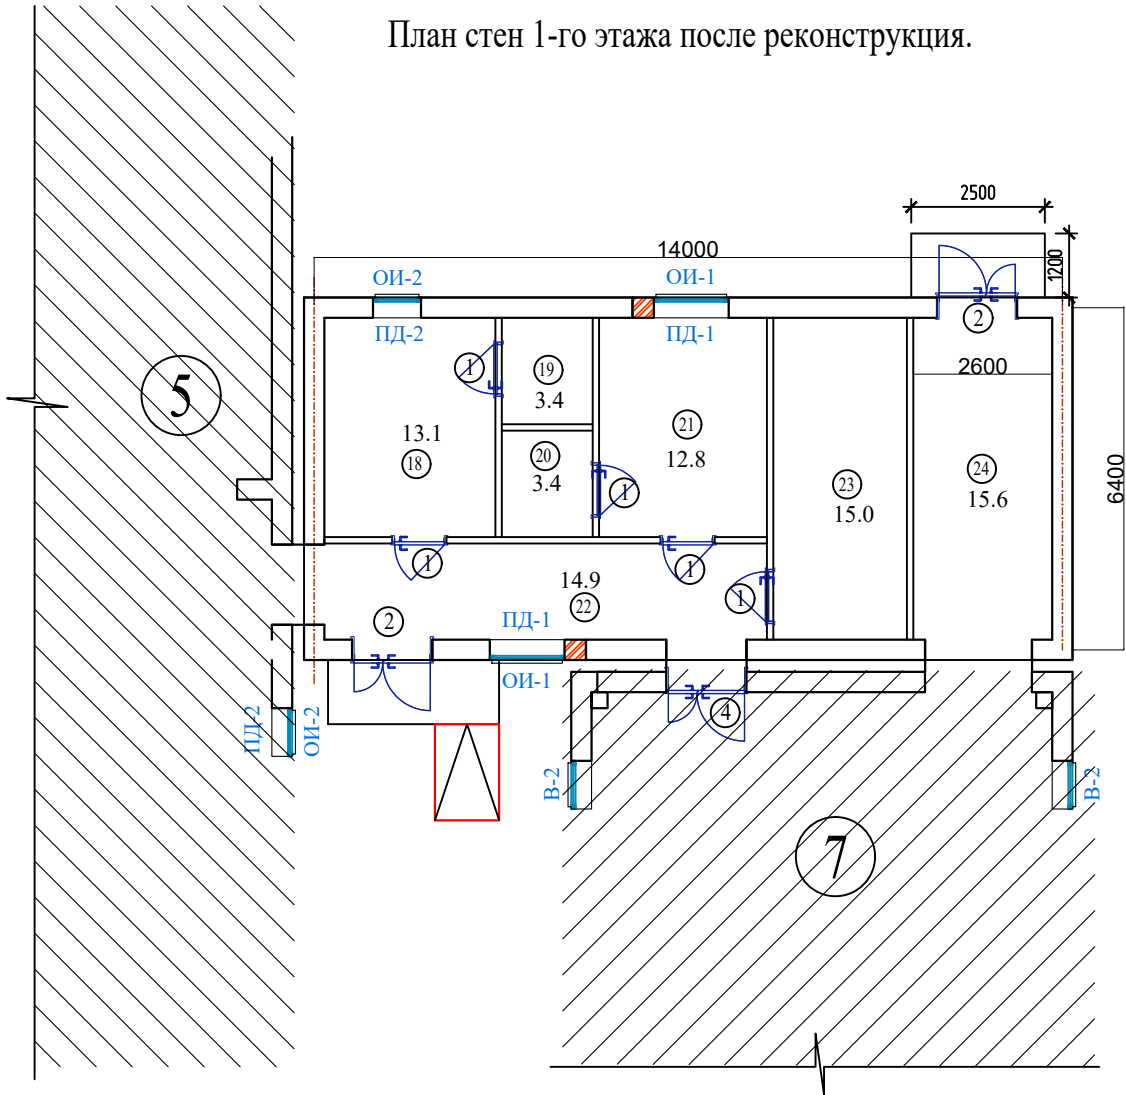

План кровля после реконструкция.

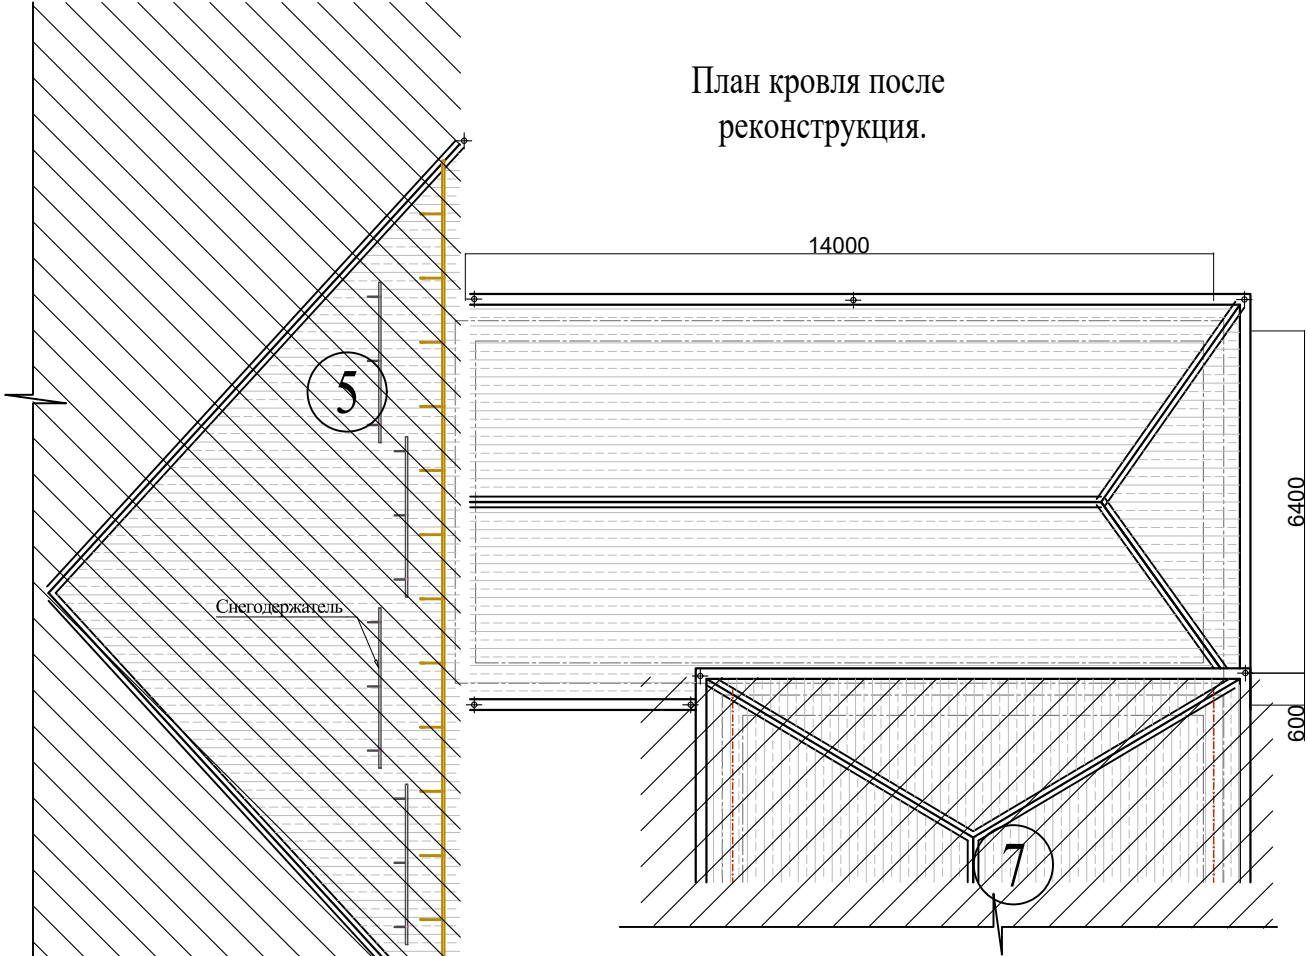


Экспликация помещений		
Номер пом.	Наименование	Площадь м²
18	Раздевальные для девочек	13.1
19	Душевая	3.4
20	Душевая	3.4
21	Раздевальные для мальчиков	12.8
22	Коридор	14.9
23	Снарядные	15.0
24	Комната инвентаря	15.6
		78.2


Спецификация элементов кровли

Поз.	Обозначение	Наименование	Кол.	Масса ед.,кг.	Приме-чание
		Расход материалов для кровли			
		Профилированные листы с полимерным покрытием СН3000х1064-17 т 0.55м(Кровля,)			110.9 м²
		Профилированные листы с полимерным покрытием СН3000х1064-17(Козырек,)			29.6 м²
1	Индивидуальный изготовление	Конек упрощенный пм	19.4		
2		Водосточная латок пм	25.2		
3		Труба водосточная пм	36.6		
4		Воронки шт	5		
5		Колено шт	15		
6		Снегозадержател пм	36.0		
7		Кронштейн -30х4 L=600мм	60	0.60	36.0 кг


Схема блокировки

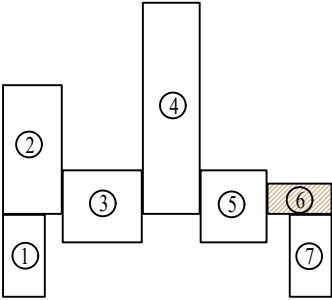


						Договор	АР		
						Капитальный ремонт школы №10 на 460 учащихся мест в СГМ "Пахтаобод" Китабского района Кашкадарьинской области			
Изм.	Колич.	Лист	Ндок.	Подпись	Дата	Существующий учебный корпус Блок 6	Стадия	Лист	Листов
ГИП		Собирова М					ТП	2	-
ГАП		Валижонов Х							
Разраб.		Пазиров.К.М				План стен 1-го этажа после реконструкция.	ГУ "QISHLOQ QURILISH LOYIHA" г. Фергана 2025 г.		
									

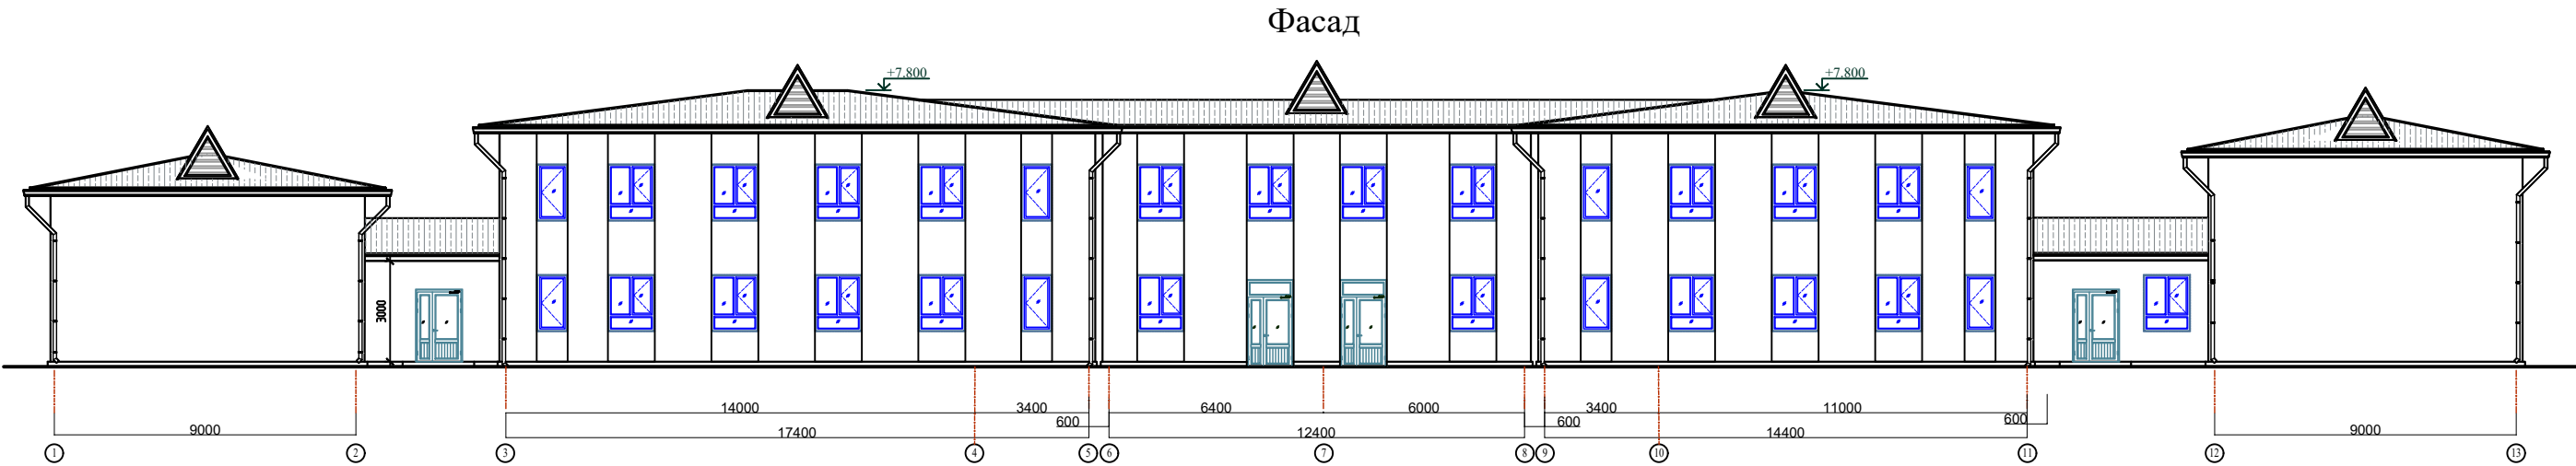

Разрез 1-1

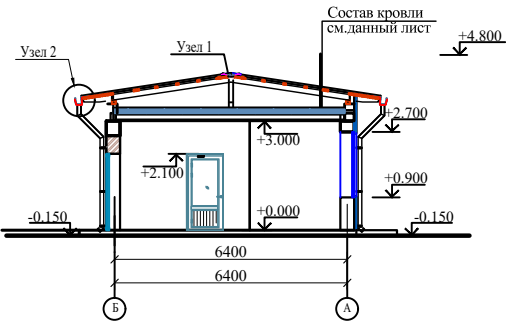

Узел-1

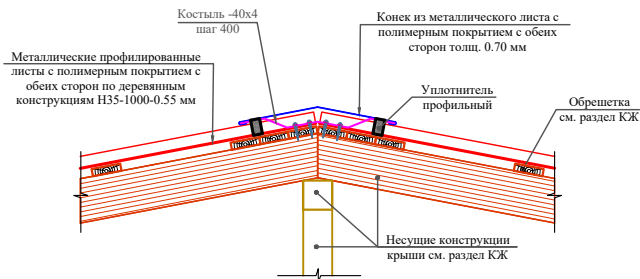

Примечание

- Состав утеплителя наружных стен**
- Простая штукатурка цементно-песчаным раствором -10мм
 - Клеевая смесь. -10мм.
 - Утеплитель (минераловатная плита). -50мм.
 - Штукатурный клеевой слой толщ. 3мм.
 - Стекловолоконная сетка (ячейка 5х5мм) } - 5-7мм.
 - Штукатурный клеевой слой толщ. 2мм.
 - Декоративно - отделочный слой толщ. 2мм.

- Цветовое решение фасадов, текстуру и фактуру материалов см. согласованный демонстрационный материал.
- Все материалы применяемые для устройства фасадов должны соответствовать техническим условиям и иметь сертификаты соответствия с обязательным предоставлением их фирмой изготовителем, исполнителем заказчику.
- Работы по отделке фасадов выполнять в соответствии с требованиями СНиП 3.04.01-87 "Изоляционные и отделочные покрытия".
- Цвета отделочных материалов фирме исполнителю согласовать с заказчиком.
- По периметру откосов и по наружным углам стен установить угол перфорированный с сеткой.
- Ведомость отделки фасадов см. АР-13.

СОСТАВ КРОВЛИ №1

- Металлические профилированные листы с полимерным покрытием с обеих сторон, по деревянным конструкциям (РСТУз 24045-94)Н35-1000-0,55 мм(см. КЖ)
- Цементно-песчаная смесь - ЦПС. М 150 (ГОСТ 28013-98), из полусухой смеси - толщ.50 мм. с армированием сеткой из Ø4 АСК (АБК) шаг 150 х 150 мм. с устройством деформационных швов шагом 6.0 х 6.0 м (с заполнением д.ш. герметиком)
- Гидроизоляционная мембрана из нетканного полипропиленового полотна*) -1 слой
- Утеплитель - минеральные плиты на основе базальтового волокна
- Пароизоляция из полиэтиленовой пленки - 200мкм.
- Сборная железобетонная плита покрытия - 220 мм

*) Нетканое полипропиленовое полотно – это материал изготавливаемый из полипропиленовых нитей, скрепленных термическим способом (термоскрепление). Поверхностная плотность возможна от 10 до 150 г/м².

Ведомость отделки фасада

Поз. отделки	Наименование элемента фасада	Наименование материала отделки	Наименование и номер эталона цвета или образец колера	Примечан. Площадь, м²
1	Цоколь	Изоляция цоколя теплоизолирующие декоративные фасадные сэндвич панели с пенополиуретаном 16мм	(цвета- подбирать по показателю материалу)	5.0
2	Стены	Очистка 100% существующей отделки фасада с последующей заменой и нанесением новых слоев	-	87.5
2*		(Состав утеплителя см.раздел-КЖ).		
3		2. Декоративный отделочный слой под травертин по готовым поверхностям.	(цвета- подбирать по показателю материалу)	
4	Покрывтие крыльца	Мрамор (нескользящие)	-	6.0

Изм.	Кол.уч.	Лист	№ док.	Подпись	Дата	Договор	АР
ТИП	Собинова М.	Валижонов Х.	Назидов К.М.			Капитальный ремонт школы №10 на 460 учащихся мест в СГМ "Пахтабод" Китабского района Кашкадарьинской области	
ТАП	Валижонов Х.	Назидов К.М.				Существующий учебный корпус Блок 6	Стадия РП
Разраб.	Валижонов Х.	Назидов К.М.				Фасад	Лист 6
							Листов -
							ГУ "QISHLOQ QURILISH LOYIHASI" г. Фергана 2025 г.

ВЕДОМОСТЬ ОСНОВНЫХ КОМПЛЕКТОВ РАБОЧИХ ЧЕРТЕЖЕЙ

Обозначение	Наименование	Примечание
АР	Архитектурное решение	
КС	Конструктивное решение	
ТХ	Технологическое решение	
ОВ	Отопление, вентиляция и кондиционирование	
	воздуха.	
ВК	Водопровод и канализация	
ЭМ	Электроосвещение и электрооборудование	
ПС	Пожарная сигнализация	
СС	Связь и сигнализация	
АСС	Автоматизация сантехсистем	

ВЕДОМОСТЬ ССЫЛОЧНЫХ И ПРИЛАГАЕМЫХ
ДОКУМЕНТОВ

Обозначение	Наименование	Примечание
	Ссылочных	
ГОСТ 24698-81	Двери наружные и служебные для жилых и общественных зданий.	
Серия 2.244-1 вып. 5	Детали полов общественных зданий.	
Серия 2.130-6с вып. 1	Узлы стен жилых и общественных зданий возводимых в районах сейсмичн. 7;8 и 9 балл.	
Серия 2.260-1 вып. 2	Детали покрытий общественных зданий.	

Ведомость рабочих чертежей основного
комплекта марки АР.

№ Лист	НАИМЕНОВАНИЕ	ПРИМЕЧАНИЕ
1	Общие данные	
2	План стен 1-го этажа после реконструкция.	
3	План кровля после реконструкция.	
4	Разрез 1-1	
5	Фасад	
6	Схема элементов заполнения дверных и оконных проемов	
7	Ведомость отделки помещений	
8	Экспликация полов; План полов 1-этажа	
9	Схема крепления плит утеплителя; Схема усиления оконных и дверных проемов	
10	Узлы по наружным стенам; Пример схемы отлива	

ОБЪЕМНО-ПЛАНИРОВОЧНЫЕ ПОКАЗАТЕЛИ

№ п/п	Наименование показателей	Ед.изм	Площадь
1	Общая площадь	м ²	151.9
2	Строительный объем	м ³	820.3
3	Площадь застройки	м ²	172.4

ОБЩИЕ УКАЗАНИЯ

Характеристика участка строительства:


Расчетная зимняя температура воздух	- 15 °С.
Скоростной напор ветра	- 38кг/м ² .
Вес снегового покрова	- 50кг/м ² .
Сейсмичность площадки	- 8 баллов.
Категория грунтов по сейсмическим свойствам	- III.
Расчетная сейсмичность площадки	- 7-8 баллов.
Глубина промерзания грунта	- 0.57 м.
Класс ответственности здания	- II
Классификация зданий по функциональной пожарной опасности	- Ф 3.4
Коэффициент надежности по назначению	- 0.95
Степень огнестойкости	- II

Проектом реконструкции предусматриваются следующие виды работ:

1. Зачистка потолков с окраской 100%.
2. Демонтаж существующей кровли и устройство нового покрытия профнастила 100%.
3. Устройство 14 шт дополнительных слуховых окон;
4. Демонтаж и установка новых оконных и дверных блоков - 100%
5. Ремонт существующей штукатурки фасадов 100 %
6. Демонтаж сущ. штукатурки внутренних стен перегородок 100 %
7. Окраска фасадов фасадными красками
8. Штукатурка внутренних стен см. ведомость отделки
9. Цоколь и вертикальные поверхности крылец облицевать бетонными плитками.


[illegible]

План стен 1-го этажа после реконструкция.

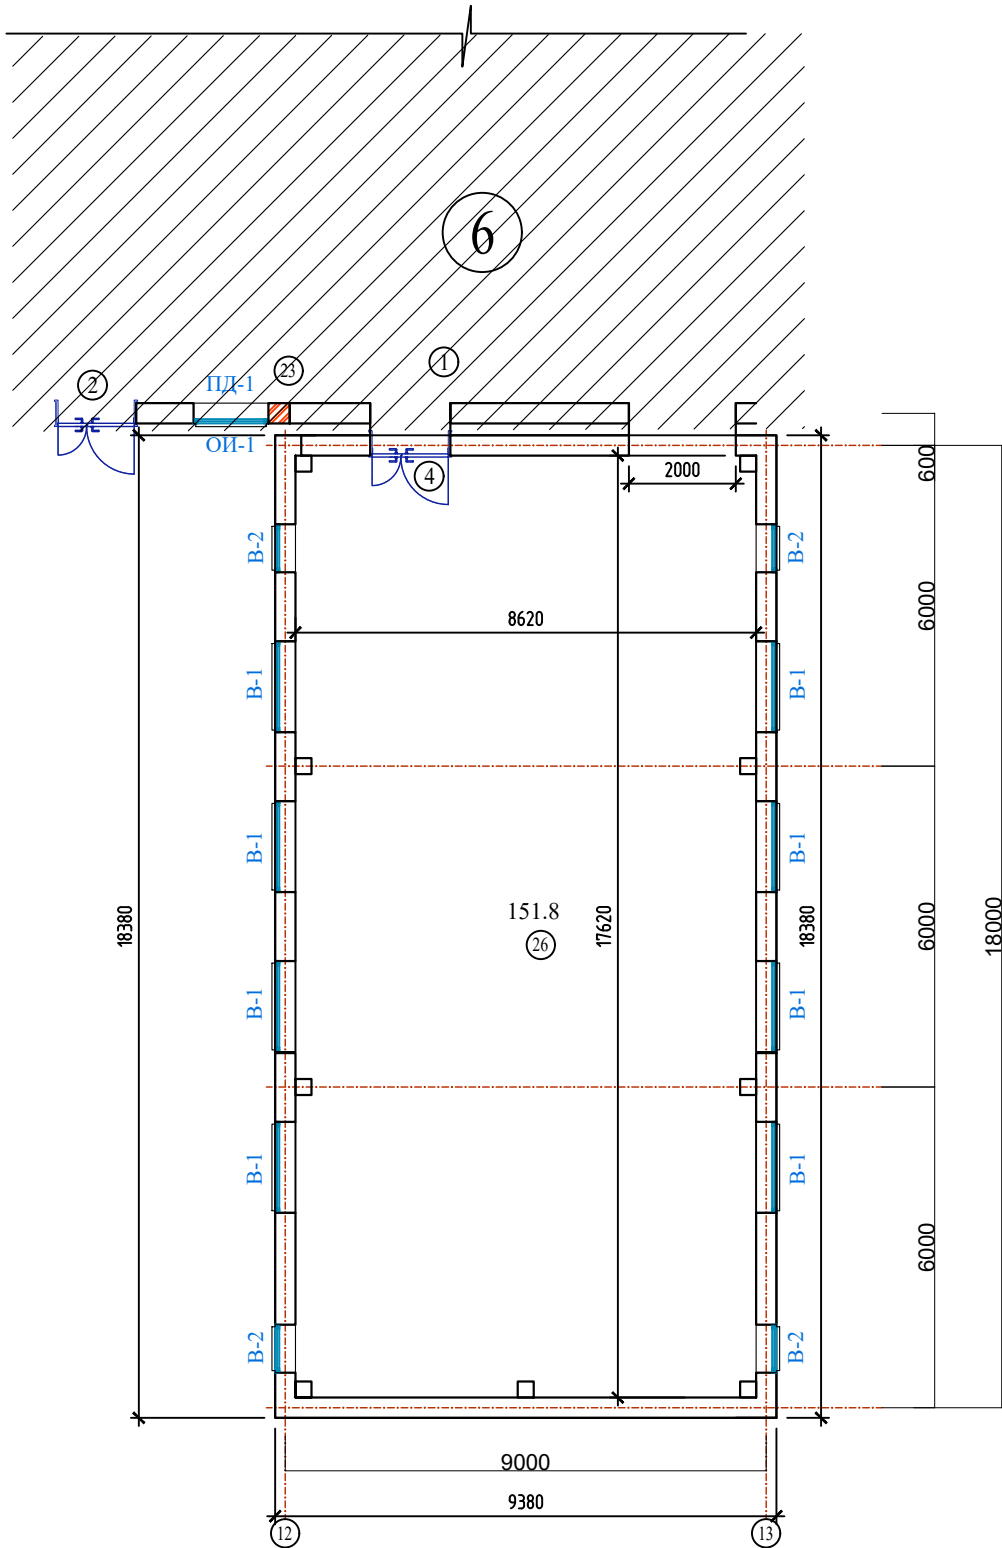


Экспликация помещений		
Номер пом.	Наименование	Площадь м²
26	Спортзал	151.8

Схема блокировки

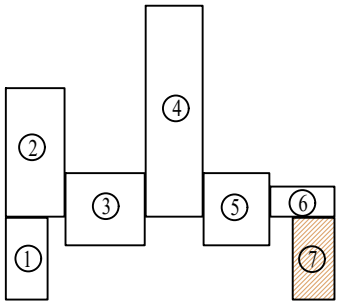

План кровля после реконструкция.

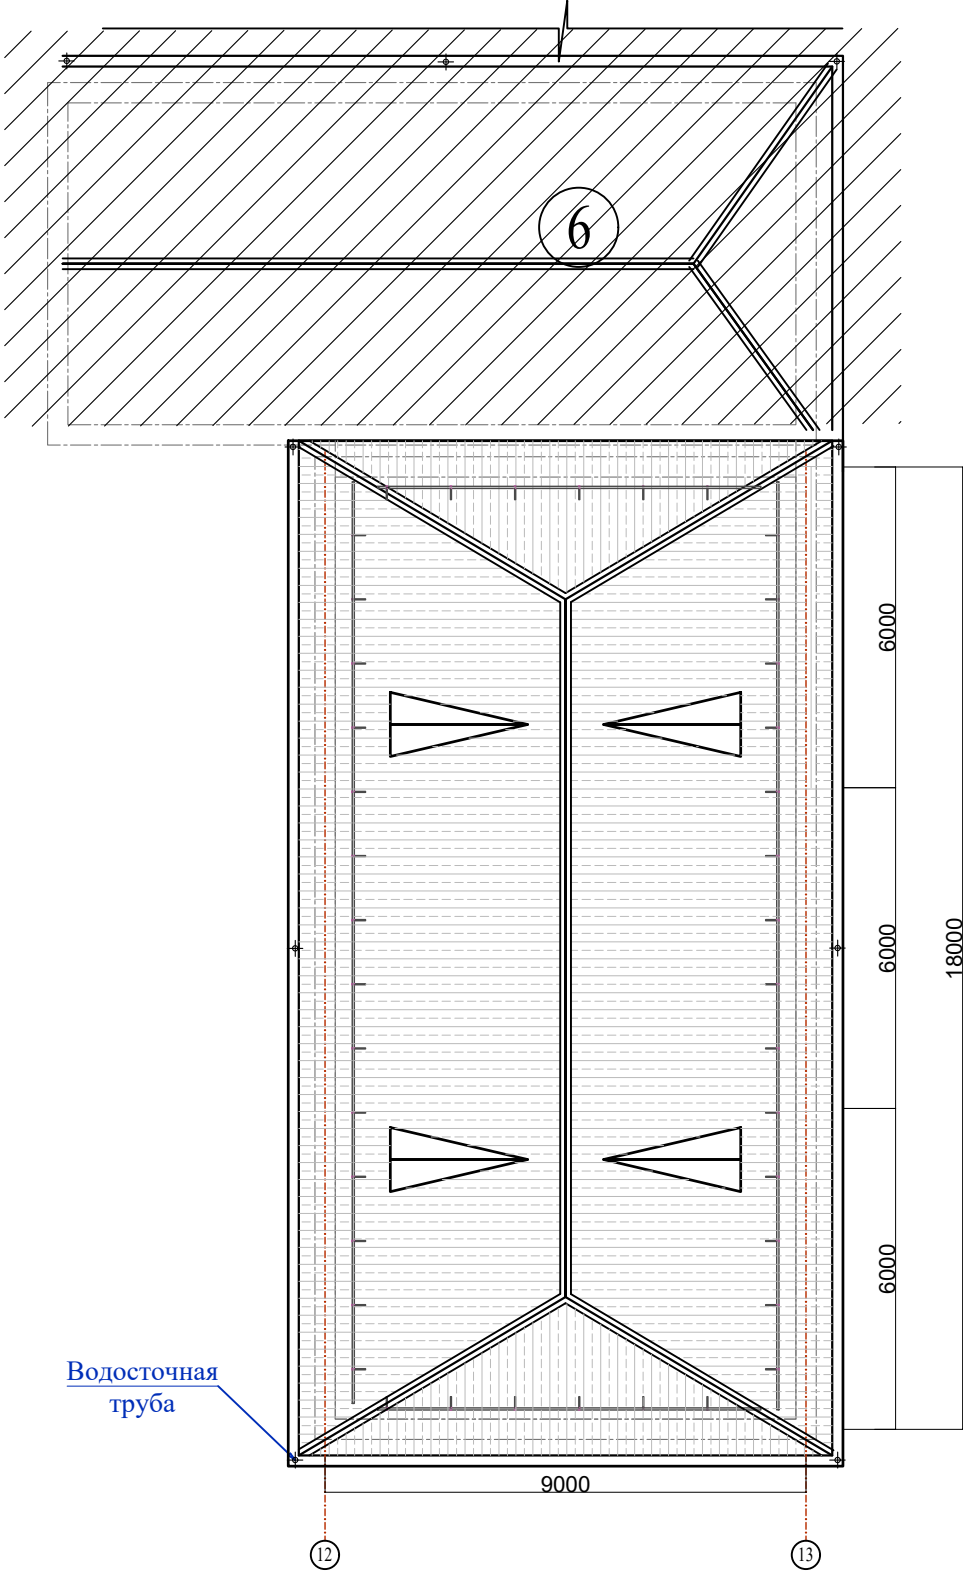


Водосточная труба

Спецификация элементов кровли

Поз.	Обозначение	Наименование	Кол.	Масса ед.,кг.	Примечание
Расход материалов для кровли					
		Профилированные листы с полимерным покрытием СН3000х1064-17 т 0.55м(Кровля.)			189.9 м²
		Профилированные листы с полимерным покрытием СН3000х1064-17(Козырек.)			14.3 м²
1	Индивидуальный изготовление	Конек упрощенный пм	27.9		
2		Водосточная латок пм	48.8		
3		Труба водосточная пм	30.6		
4		Воронки шт	5		
5		Колено шт	15		
6		Снегозадержател пм	48.8		
7		Кронштейн -30х4 L=600мм	60	0.60	36.0 кг
8					

Спецификация элементов жалюзиных решеток

Поз.	Обозначение	Наименование	Кол.	Масса ед. кг	Примеч.
Расход дан на одну жалюзийную решетку общ. кол. 8 шт.					
Жр-1	Данный лист	Жалюзийная решетка	1		шт.
	ГОСТ 8509-93	Рама из гн. уголка 50х5	2.8	3.77	п.м.
	ГОСТ 103-76	"Перо"-3х120 L=перем. ш.75мм	10	5.652	шт.
	ГОСТ 5781-82	Каркас из арматуры Ø6A240	2.9	0,222	п.м.
	ГОСТ 19903-74*	Клямеры из полосы -1х10 L=50 шагом 300	10	0,004	шт.
	ГОСТ 5336-80*	Сетка стальная Р-15-1.6-0	0.5	2,57	м²

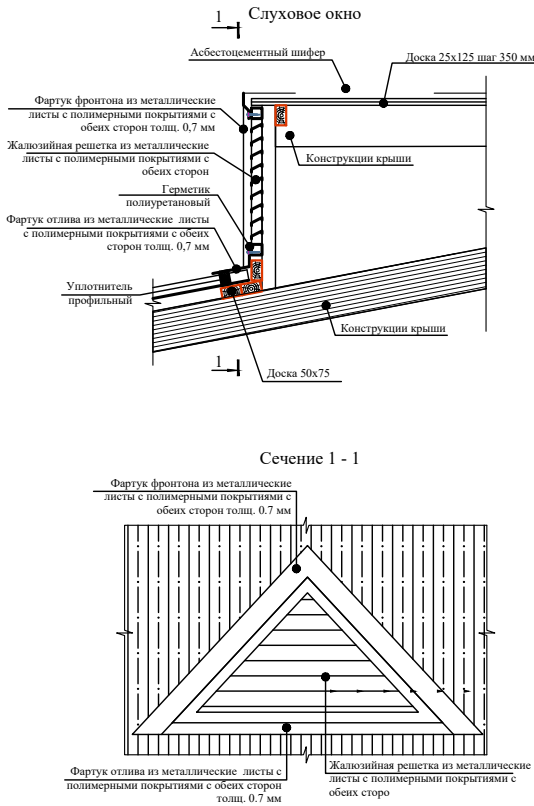

						Договор	АР		
						Капитальный ремонт школы №10 на 460 учащихся мест в СГМ "Пахтаобод" Китабского района Кашкадарьинской области			
Изм.	Колич.	Лист	Ндок.	Подпись	Дата	Существующий учебный корпус Блок 7	Стадия	Лист	Листов
ГИП		Собирова М					ТП	2	-
ГАП		Валижонов Х							
Разраб.		Пазиллов.К.М				План стен 1-го этажа после реконструкция. План кровля после реконструкция.	ГУ "QISHLOQ QURILISH LOYIHA" г. Фергана 2025 г.		
									


Ведомость рабочих чертежей НВК		
№пп	Наименование рабочих чертежей	Примечание
1	Общие данные	
2	Выкопировка из генплана с сетями ВиК	
3	Профиль В1. Схема В1. Детализовка водопроводных колодцев.	
4	Водопроводная камера 2600х2000	
5	Профиль К1.	
6	Профиль К1, КНЗ	
7	Таблица колодцев .	
8	Накопительная емкость с насосом	

Обозначение	Наименование	Примечание
	Ссылочные документы	
ТПР 901-09-11.84 альбом I,II,IV, V.	Колодцы водопроводные	
ТПР 902-09-22.84 альбом I,II	Колодцы канализационные	
	Прилагаемые документы	
НБК.С	Спецификация оборудования	
НБК.ВР	Ведомость объемов работ	

Наименование	Расчетные расходы по системам ВК			Мощность установленного эл.двигателя кВт	Примечание
	м3/сут	м3/час	л/с		
В1	11,50	5,50	2,10		
К1	11,50	5,50	2,10		
Наружное пожаротушение			15,00		

Собирова М.

Формат А3

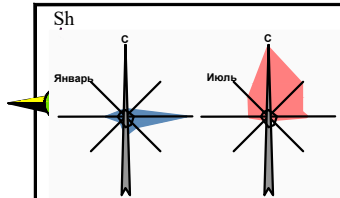

Выкопировка из генплана с сетями ВиК М1:500

Точка подключения
к поселковой сети
водопровода



УСЛОВНЫЕ ОБОЗНАЧЕНИЕ

- Существующие здания
- Озеленение
- Существующие дороги и тротуар

ВЕДЕМОСТЬ ЖИЛЫХ И ОБЩЕСТВЕННЫХ ЗДАНИЙ И СООРУЖЕНИЙ

№ по ГП	Наименование	Этажность	Количество	Показатели			Тип номер проекта
				Общ. площ. м2	Площ. застр. м2	Стр. объём. м3	
1	Существующий корпус капитальный ремонт (сущ.)	2	1				
2	Футбольное поле (сущ.)	1	2				
3	Котельная (сущ.)	1	1				
4	Склад хранения угля (сущ.)	1	1				
5	Уборная (сущ.)	1	1				
6	Склад (сущ.)	1	1				
7	Противопожарный хауз 80 м3 (сущ.) (снос.)	1	1				
8	Хауз (сущ.) (снос.)	1	1				
9	Ажурные ворота (проект.)	1	2				
10	Глухие ворота (сущ.)		1				
11	Ажурные металлические ограждения (проект.)						
12	Глухие ограждения (сущ.)						
13	Противопожарный шит (проект.)		2				
14	Автостоянка (проект.)		8				
15	Трансформатор (сущ. 250 кВт)						
16	Глухие корсетные ограждения (проект.)						
17	Выгребная яма (сущ.)						
18	Фанкойл, Чиллер (проект.)						
19	ЛЮС 12м3/сут (проект.)						
20	Накопительная емкость с насосом (проект.)						
21	Модульная котельная (проект.)	-	1				
22	Резервуар 25м3 (проект.)	-	1				
23							

1-ПГ Колодец с пожарным гидрантом

- В1 Проектируемый хозяйственный водопровод
- К1 Проектируемая хозяйственная канализация
- KH3 Проектируемая напорная хозяйственная канализация очищенных стоков

Договор:				НБК		
Капитальный ремонт школы №10 на 460 учащихся мест в СГМ "Пахтабод" Китабского района Кашкадарьинской области						
Внутриплощадочные сети водопровода и канализации				Стадия	Лист	Листов
				РП	2	
Выкопировка из генплана с сетями ВиК				"КИШЛОКУРИЛИШ ЛОЙИХА" ГУ город Фергана 2025 г.		
Изм.	Кол.	Лист	Док №	Подпись	Дата	
Гип	Собирова М.					
Исполнитель						

Ведомость рабочих чертежей основного комплекта марки ЭС		
Лист	Наименование	Примечание
1	Общие данные .	
2	Однолинейная схема, таблица подсчета нагрузок ТП.	
3	План низковольтных сетей 0,4 кВ. М1:500.	
4	Наружное освещение. Общий вид опоры восьмигранной Н=6,0м с солнечной панелью.	

Ведомость прилагаемых и ссылочных документов		
Обозначение	Наименование	Примечание
	<u>Ссылочные документы</u>	
Сер. 4.407- 251	Прокладка кабелей напряжением до 35 кВ	
выпуск - 1	в траншеях . Рабочие чертежи .	
	<u>Прилагаемые документы</u>	
ЭС.С.	Спецификация оборудования	3 - листа
ЭС.С-1	Спецификация оборудованияна АСКУЭ.	1 - лист
КЖ	Опоры восьмигранные конические	
	(по перечню чертежей на листе КЖ-1)	на 3 листах
	Технические условия	

Проект соответствует требованиям технологических, санитарно-гигиенических, противопожарных и других норм, действующих на территории Республики Узбекистан и обеспечивает безопасную для жизни и здоровья эксплуатацию объекта при соблюдении предусмотренных рабочими чертежами мероприятий.		
Главный инженер проекта		Собирова М

ОБЩИЕ УКАЗАНИЯ

Проект электроснабжения школы выполнен в соответствии с ПУЭ, КМК2.04.17-19, и на основании генплана.

Потребная мощность по проекту составляет =71 кВт

Категория электроснабжения школы - 3.

Проектом предусмотрена демонтаж сущ. силового трансформатора с мощностью 250кВА, и установка комплектной трасформаторной подстанции типа №773 Сущ ТП-250 кВА/10/0,4кВА и дизель-генератор на 250 кВт, включающий в комплект шкаф АВР (автоматический ввод резерва), устанавливаемые рядом с ТП.

Все оборудование: -ТП, дизель-генератор в комплекте с шкафом АВР, над ними необходимо предусмотреть навес (из металлоконструкций) от атмосферных осадков.

Кабели марки АВВГ- 1,0 кВ прокладываются в земляной траншее на глубине -0,7 кВ от поверхности земли.

Сечение кабелей выбраны по длительно - допустимому току и проверены на потерю напряжения и по условию отключения однофазных коротких замыканий.

Кабели в траншее укладываются на подсыпку из просеянного грунта толщиной -100мм.

При выходе из подстанции, на вводах в здания, при пересечении с инженерными коммуникациями и в местах частых вскрытий под дорогами, кабели в полиэтиленовых трубах защитить от механических повреждений кирпичом.


Для наружного освещения предусматриваются уличные светодиодные светильники типа GLIL-80W (в комплекте с оборудованием:- солнечными панелями 40W= 2шт,аккумулятором),работающие от солнечных панелей ,которые устанавливаются на металлических опорах Н =4м.

Монтаж электрооборудования выполнять в соответствии с ПУЭ и КМК 3.05.06. - 19.

						2025г	ЭС					
						Капитальный ремонт школы №10 на 460 учащихся мест в СГМ "Пахтаобод" Китабского района Кашкадарьинской области						
Изм.	Кол.	Лист	Н.док	Подпись	Дата							
ГИП		Собирова М				Низковольтные сети ~ 380/220 В		Стадия	Лист	Листов		
								РП	1			
Разраб.		Умарова Х				Общие данные		"КИШЛОҚҲУРИЛИШ ЛОЙИХА" ГУ город Ташкент 2025 г.				

Однолинейная схема трансформаторной подстанции типа №773 Сущ.ТП-250 кВА /10/0,4кВА

Силовой трансформатор , мощность , кВА напряжение , В
Тип и номинальный ток автомата , А
Номинальный ток трансформатора тока , А
Номинальный ток рубильника , А
Марка и сечение шин (фазных)
Тип автомата , номинальный ток , ток расцепителя , А
Марка и сечение шин (нулевой)

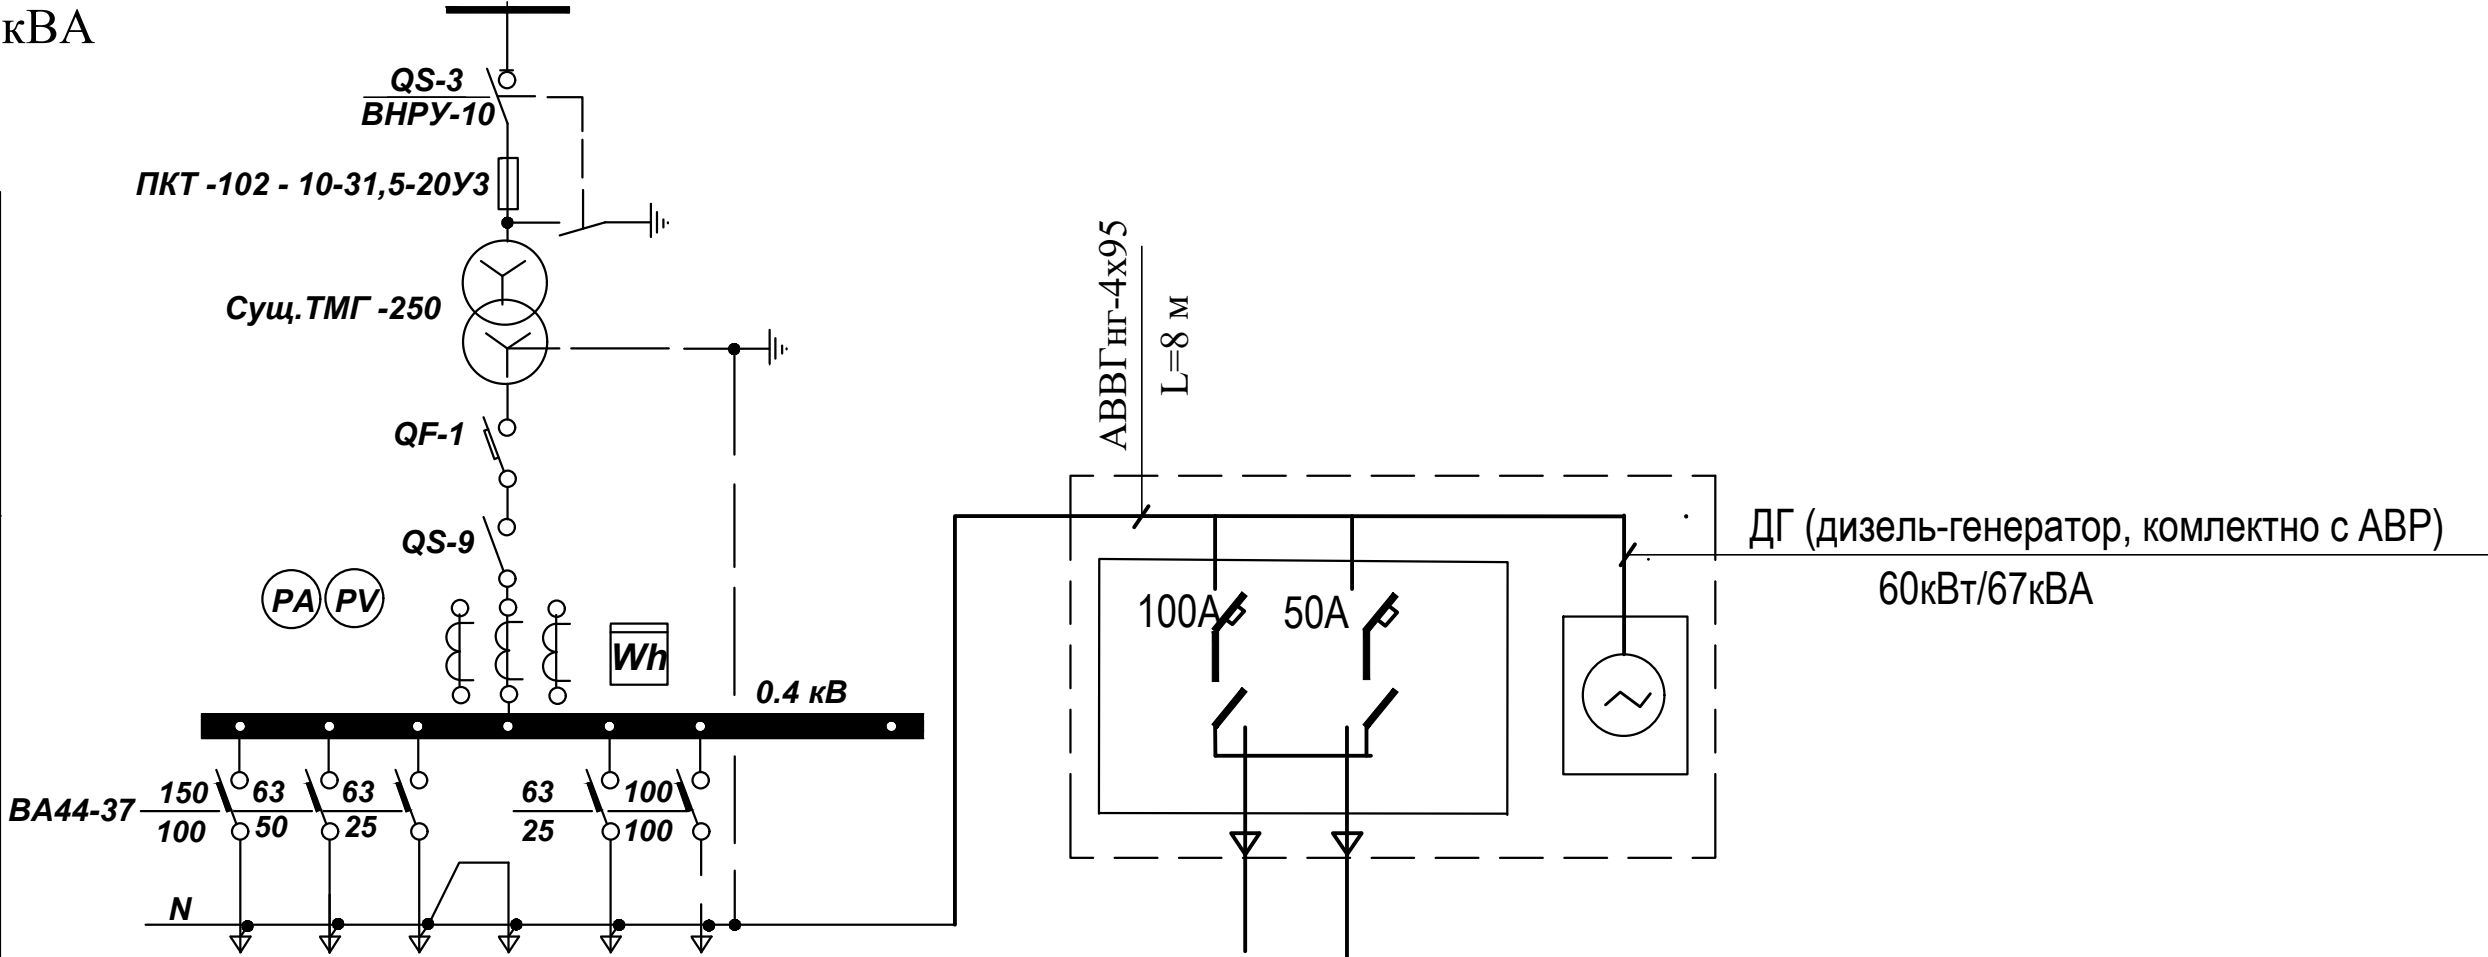


Назначение линии	Л 1	Л 2	Л 3	Л 3-1	Л 5	Л 6				Л 7	Л 8	
Расчетная мощность , кВт	42,835	20,82	2,2	1,55	3,5					42,835	20,82	
Расчетный ток , А	72,3	37,2	4,4	7,0	5,9					72,3	37,2	
Сечение отходящего кабеля , марки , кв. мм.	АВВГ-1000 4х50	АВВГ-1000 4х10	АВВГ-1000 4х6	АВВГ-1000 3х4	АВВГ-1000 4х6					АВВГ-1000 4х50	АВВГ-1000 4х10	
Длина отходящей линии ,м	124	20	59	42	115					124	20	
Потеря напряжения %	2,4	0,9	0,54	0,4	1,5					2,4	0,9	
Наименование объекта	ВРУ	Фанкойл, Чиллер	Насосная	ЛОС	Модульная катель					ВРУ	Фанкойл, Чиллер	

Потребность кабелей и проводов (длина-м)


Число и сече- ние жил, напряжение	Марка		
	АВВГ -1,0	АВВГ -0,66	
4х50мм 2	134		
4х10мм 2	22		
4х6мм 2	189		
3х4мм 2	46		
4х95мм 2	9		

КАБЕЛЬНЫЙ ЖУРНАЛ ДЛЯ ПИТАЮЩЕЙ СЕТИ

Марки - ровка кабеля	Трасса		Кабель			
	Начало	Конец	По проекту			Марка кабель
			Марка кабеля	Кол-во число жил и сечение напряжение	Длина траншей Длина кабеля	
Л 1	ТП-шины 0,4 кВ	ВРУ	АВВГ-1,0	4 х 50	124 / 134	
Л 2	ТП-шины 0,4 кВ	Фанкойл, Чиллер	АВВГ-1,0	4 х 10	20 / 22	
Л 3	ТП-шины 0,4 кВ	Насосная	АВВГ-1,0	4 х 6	59 / 64	
Л 3-1	Насосная	ЛОС	АВВГ-1,0	3х 4	42 / 46	
Л 4	ТП-шины 0,4 кВ	Модульная катель	АВВГ-1,0	4 х 6	115 / 125	

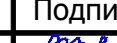						2025г	ЭС				
						Капитальный ремонт школы №10 на 460 учащихся мест в СГМ "Пахтаобод" Китабского района Кашкадарьинской области					
Изм.	Кол.	Лист	Н.док	Подпись	Дата	Внутриплощадочное электроснабжение 0,4 кВ			Стадия	Лист	Листов
ГИП		Собирова М							РП	2	
Разраб.		Умарова Х				Однолинейная схема и таблица подсчета ТП Кабельный журнал.			"КИШЛОҚҚУРИЛИШ ЛОЙИХА" ГУ город Ташкент 2025 г.		

Инв.№ подл.Подпись и дата.Взам.инв.№

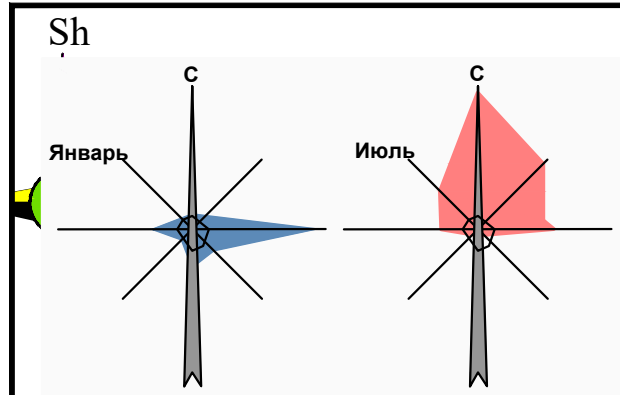

УСЛОВНЫЕ ОБОЗНАЧЕНИЕ

- Существующие здания
- Озеленение
- Существующие дороги и тротуар

ВЕДОМОСТЬ ЖИЛЫХ И ОБЩЕСТВЕННЫХ ЗДАНИЙ И СООРУЖЕНИЙ


№ по ГП	Наименование	Этажность	Количество	Показателей			Тип номер проекта	
				Общ. площ. м2	Площ. застр. м2	Стр. объём. м3		
1	Существующий корпус капитальный ремонт (сущ.)	2	1					
2	Футбольное поле (сущ.)	1	2					
3	Модульный котел (проект.) (сущ.)	1	1					
4	Склад хранения угля (сущ.)	1	1					
5	Уборная (сущ.)	1	1					
6	Склад (сущ.)	1	1					
7	Противопожарный хауз 80 м3 (сущ.)	1	1					
8	Хауз (сущ.)	1	1					
9	Ажурные ворота (сущ.)	1	2					
10	Глухие ворота (сущ.)		1					
11	Ажурные металлические ограждения (сущ.)							
12	Глухие ограждения (сущ.)							
13	Противопожарный щит (проект.)		2					
14	Автостоянка (проект.)		8					
15	Трансформатор (сущ. 250 кВт)							
16	Глухие корсетные ограждения (сущ.)							
17	Выгребная яма (сущ.)							
18	Фанкойл, Чиллер (проект.)	-	1					
19	ЛОС 12м3/сут (проект.)	-	1					
20	Насосная (проект.)	-	1					
21	Накопительная емкость с насосом (проект.)	-	1					
22	Модульная котельная (проект.)	-	1					



Сущ. №773 ТП250 kVA

ДЭС

						Договор:	ГП		
						Капитальный ремонт школы №10 на 460 учащихся мест в СГМ "Пахтаобод" Китабского района Кашкадарьинской области			
Изм.	Кол.уч.	Лист	Док №	Подпись	Дата				
ГИП	Собирова М					Низковольтные сети ~ 380/220 В	Стадия РП	Лист 3	Листов 4
Разраб.	Умарова Х					План низковольтных сетей 0,4 кВ.	"КИШЛОҚҚУРИЛИШ ЛОЙИХА" ГУ город Ташкент 2025 г.		
									

Общий вид. Опора восьмигранная Н=4,0м

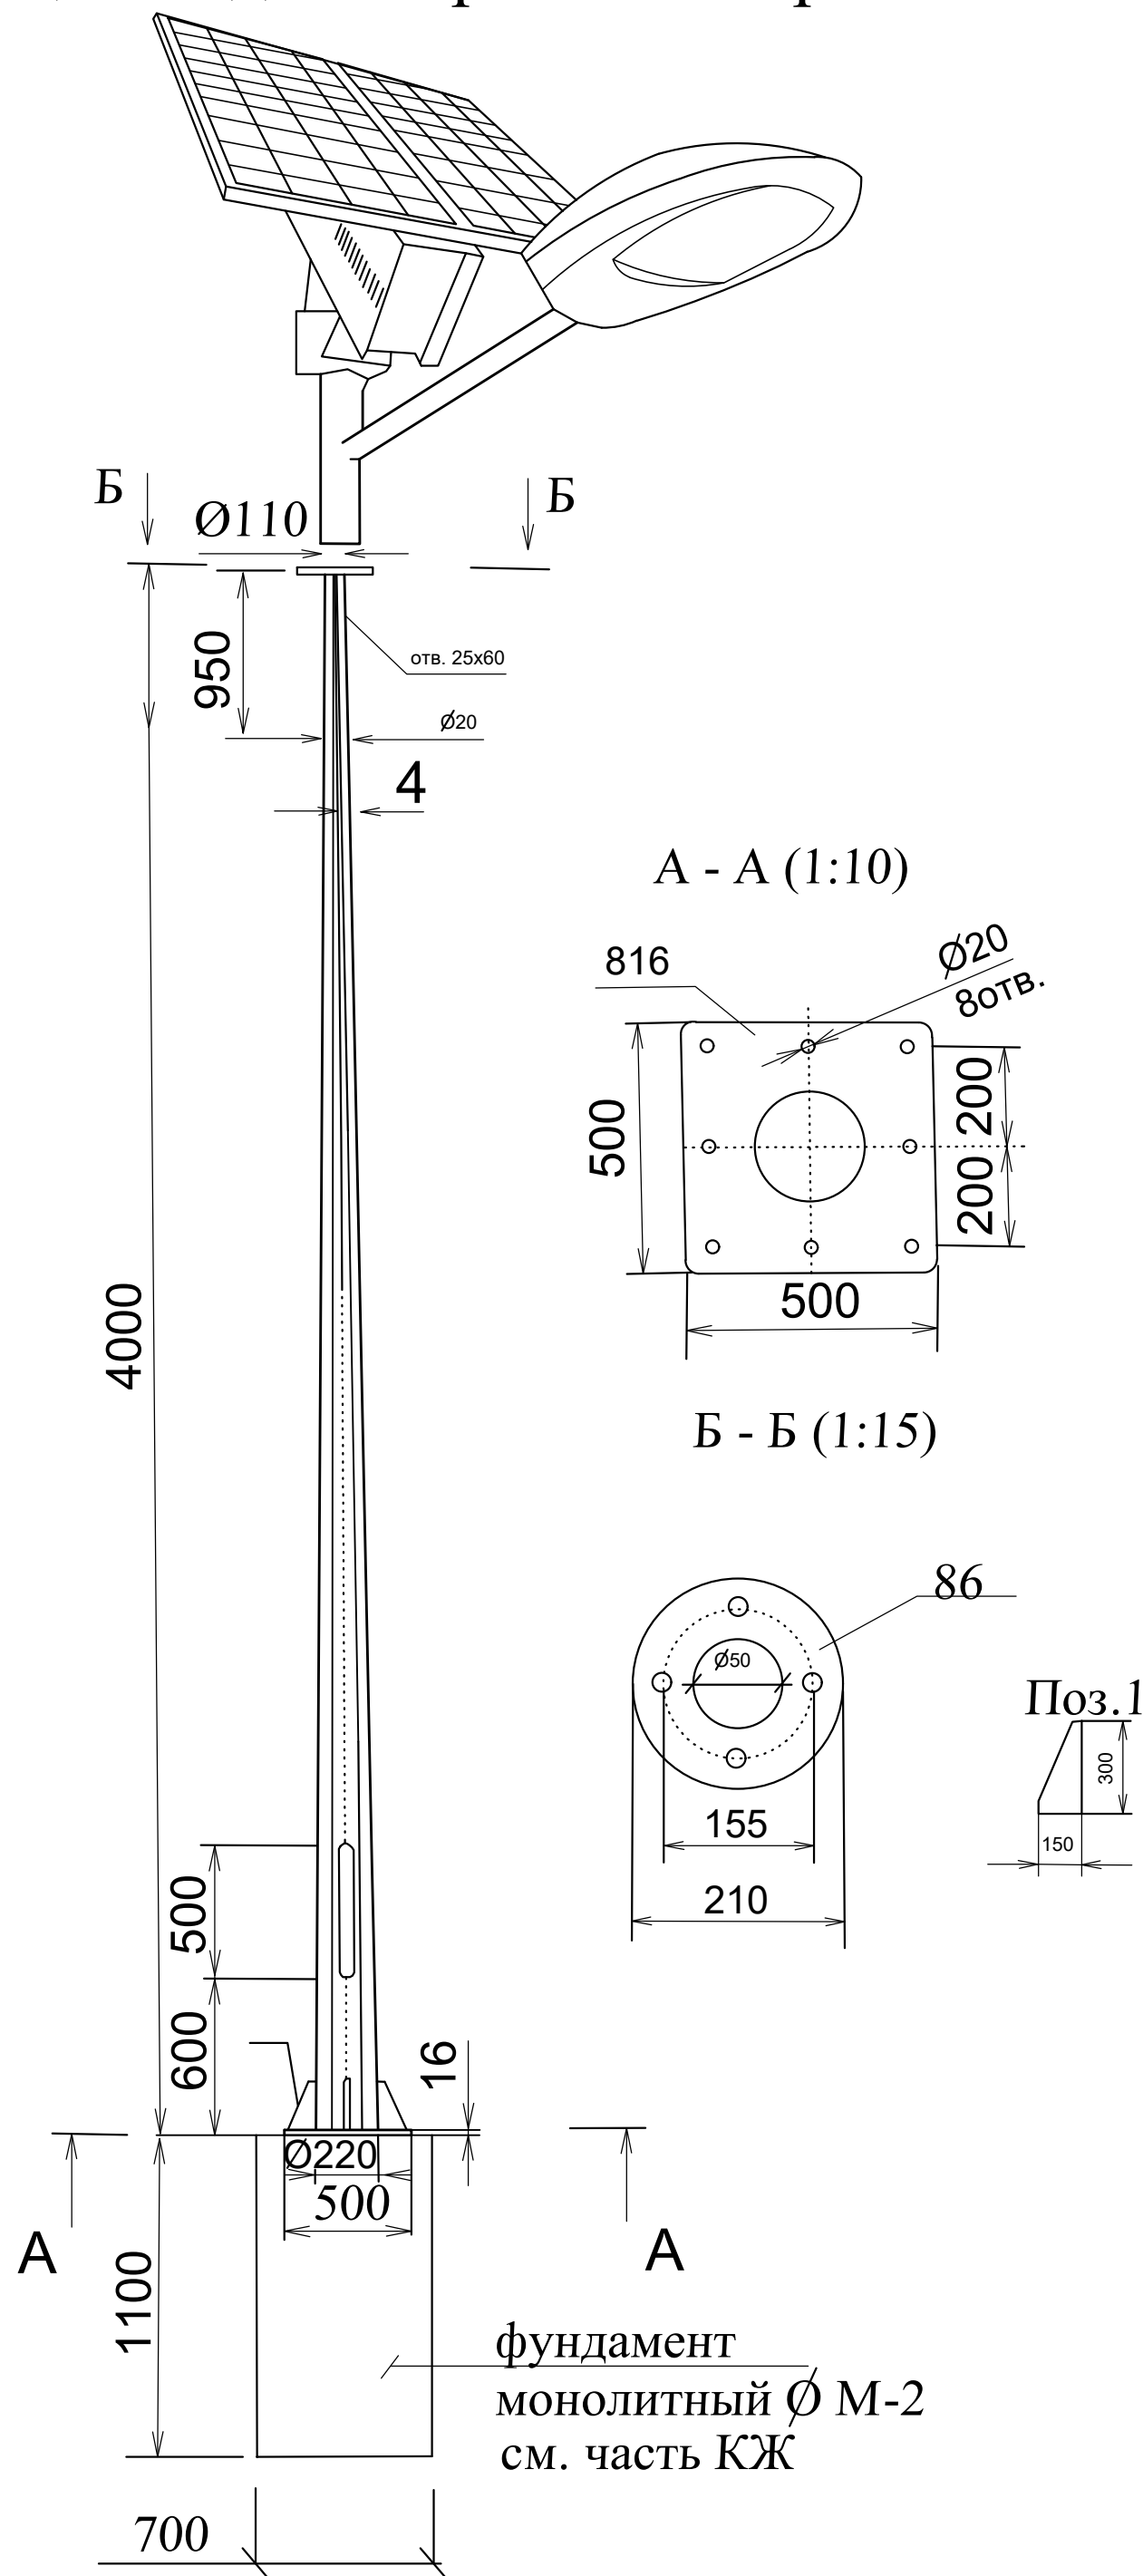

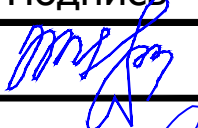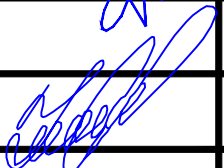						2025г	ЭС				
						Капитальный ремонт школы №10 на 460 учащихся мест в СГМ "Пахтаобод" Китабского района Кашкадарьинской области					
Изм.	Кол.	Лист	N.док	Подпись	Дата	Внутриплощадочное электроснабжение 0,4 кВ			Стадия	Лист	Листов
ГИП		Собирова М							РП	4	
Разраб.		Умарова Х				Наружное освещение. Общий вид опоры восьмигранной Н=4,0м с солнечной панелью.			"ҚИШЛОҚҚУРИЛИШ ЛОЙИХА" ГУ город Ташкент 2025 г.		

ВЕДОМОСТЬ РАБОЧИХ ЧЕРТЕЖЕЙ ОСНОВНОГО КОМПЛЕКТА "ТС"

Лист	Наименование	Примечание
ТС-1	Общие данные	
ТС-2	План инженерных сетей теплотрассы М1:500	
ТС-3	Схема теплосети.	
ТС-4	Продольный профиль теплосети, М вер 1:100, гор. 1:500	
	Сечение 1-1, М1:10.	
ТС-5	Монтажная схема железобетонных лотков теплотрассы. М1:100	
	Монтажная схема железобетонных плит теплотрассы. М1:100	
ТС-6	Деталь герметизации ввода трубопровода.	
СО-ТС	Спецификация изделий и материалов.	

ВЕДОМОСТЬ ССЫЛОЧНЫХ И ПРИЛАГАЕМЫХ ДОКУМЕНТОВ

Обозначение	Наименование	Примечание
	Ссылочные документы	
КМК 2.04.07-99	"Тепловые сети"	
КМК 3.01.02-00	"Техника безопасности в строительстве"	
Серия 3.006	Сборные железобетонные каналы и тоннели	
	из лотковых элементов.	
	Прилагаемые документы	
СО-ТС	Спецификация материалов.	

Проектно-сметная документация разработана в соответствии с утвержденным рабочим проектом, с нормами, правилами, инструкциями, государственными стандартами, а также в соответствии с техническими заданиями на присоединение проектируемого объекта к инженерным сетям и коммуникациям.

Гл. инженер проекта

УМУМИЙ МА'ЛУМОТ

Issiqlik tizimi loyihasi quyidagi dastlabki ma'lumotlar asosida amalga oshirildi:

1. Toposiyomka

2. Arxitektura-rejalashtirish yechimi

3. Dizayn vazifalari

4. Texnik xususiyatlar

5. Muhandislik-geologik tadqiqotlar bo'yicha hisobot

Issiqlik ta'minoti manbai qozonxona(200 kVt modul qozonxona). Issiqlik tizimi yer ostida temir betton kanallar ichida ketedi. Issiqli tashuvchi suv parametrlari: T1/T2= 80/60; P1/P2=10.0/8.0 kPa; Issiqlik tarmoqlarining ishlash sxemasi yopiq. Loyiha KMK 3.05.03-85 "Issiqlik tarmoqlari", KMK 3.01.02-00 "Qurilishda xavfsizlik" asosida amalga oshirildi.

Quvurlar

Magistral isitish quvurlari er osti yotqizish uchun issiqlik izolatsiyasiga ega po'lat quvurlardan mo'ljallangan. Quvurning diametri Ø89x3.0. Quvurlarni yotqizish er ostida amalga oshiriladi. Issiqlik cho'zilishining kompensatsiyasi P(П) ko'rinishidagi kompensatordan foydalaniladi.

KMK 2.04.07-99 ga muofiq issiqlik magistralini qurishda quyidagi ishlar bo'yicha tekshirish guvochnomalarini rasmiylashtirish kerak:

1. Qo'zg'aluvchi va qo'zg'almas quvur liniyasi tayanchlarini bajarish.

2. Quvurlarni tozalash va dezinfeksiya qilish

3. Payvand choklarining sifatini tekshirish.


4. Zadvijkalarni qayta ko'rib chiqish va sinovdan o'tkazish.

5. Quvurlarni gidravlik sinovdan o'tkazish.

Поз. по Ген-плану	Наименование потребителя	Расчетный тепловой поток; кВт (Гкал/ч)				
		Отопление	Вентиляция	Горячее водоснаб-жение	Технологи-ческие нужды	В С Е Г О
1	Учебный корпус	200,45	-	-	-	200,45
1			-	-	-	

Общая потребность тепла: 200.45 кВт (172.387) Гкал/ч

							Дог.№ _____ от _____ 2025г.	ТС
							Капитальный ремонт школы №10 на 460 учащихся мест в СГМ "Пахтаобод" Китабского района Кашкадарьинской области	
Изм.	Кол. уч.	Лист	№ док.	Подп.	Дата			
ГИП	Собирова М						Теплоснабжения	Стадия
Испол.	Нишонов Т							Лист
								Листов
							РП	1
							6	
							Общие данные	
							"КИШЛОККУРИЛИШ ЛОЙИХА" ГУ город Ташкент 2025	

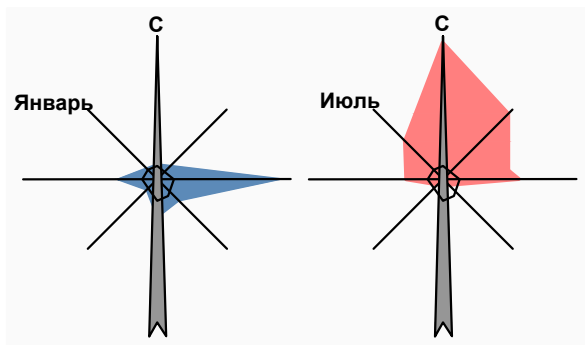

План инженерных сетей теплоотрасли М1:500




- УСЛОВНЫЕ
ОБОЗНАЧЕНИЕ**
- Существующие здания
 - Озеленение
 - Существующие дороги

ВЕДЕМОСТЬ ЖИЛЫХ И ОБЩЕСТВЕННЫХ ЗДАНИЙ И СООРУЖЕНИЙ

№ по ГП	Наименование	Этажность	Количество	Показателей			Тип номер проекта	
				Общ. площ. м2	Площ. застр. м2	Стр. объём. м3		
1	Существующий корпус капитальный ремонт (сущ.)	2	1					
2	Футбольное поле (сущ.)	1	2					
3	Модульный котел (проект.) (сущ.)	1	1					
4	Склад хранения угля (сущ.)	1	1					
5	Уборная (сущ.)	1	1					
6	Склад (сущ.)	1	1					
7	Противопожарный хауз 80 м3 (сущ.)	1	1					
8	Хауз (сущ.)	1	1					
9	Ажурные ворота (сущ.)	1	2					
10	Глухие ворота (сущ.)		1					
11	Ажурные металлические ограждения (сущ.)							
12	Глухие ограждения (сущ.)							
13	Противопожарный щит (проект.)		2					
14	Автостоянка (проект.)		8					
15	Трансформатор (сущ. 250 кВт)							
16	Глухие корсетные ограждения (сущ.)							
17	Выгребная яма (сущ.)							
18	Теплонасос (проект.)	-	1					
19	ЛОС 12м3/сут (проект.)	-	1					
20	Насосная (проект.)	-	1					
21	Накопительная емкость с насосом (проект.)	-	1					
22	Модульная котельная (проект.)	-	1					
23	Резервуар питьевой воды 25 м³ (проект.)	-	1					

Дог.№ _____ от _____ 2025г. ТС					
Капитальный ремонт школы №10 на 460 учащихся мест в СГМ "Пахтаобод" Китабского района Кашкадарьинской области					
Изм. Кол.уч	Лист	Док №	Подпись	Дата	
ГИП	Собирова М				Теплоснабжения
Исполнитель	Нишонов Т				РП
					2
					Листов
					6
План инженерных сетей теплоотрасли М1:500					"КИШЛОККУРИЛИШ ЛОЙИХА" ГУ город Ташкент 2025

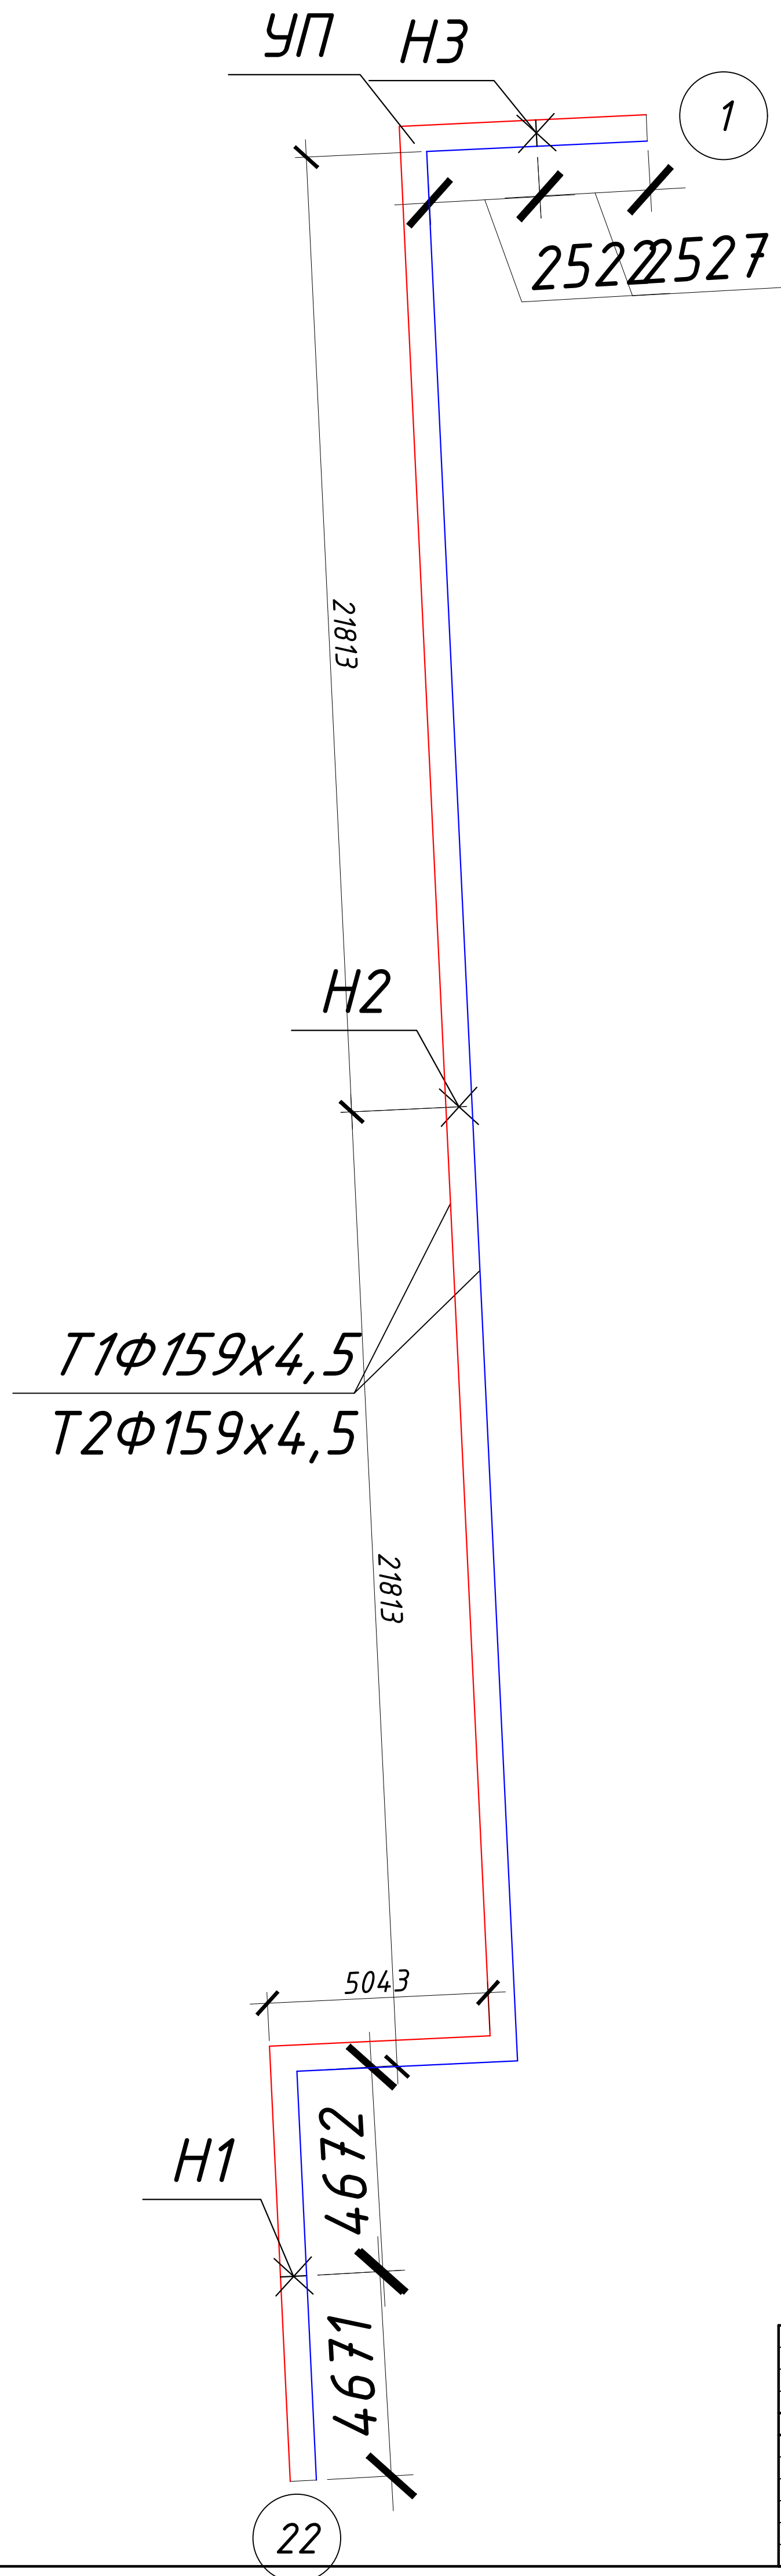

						Доз.№ _____ от _____ 2025г. ТС
						Капитальный ремонт школы №10 на 460 учащихся мест в СГМ "Пахтаобод" Китабского района Кашкадарьинской области
Изм.	Кол. уч.	Лист	№ док.	Подп.	Дата	
ГИП	Собирова М					Теплоснабжения
Испол.-ТС	Нишинов Т					
						</