

РЕСПУБЛИКА КАЗАХСТАН
ЗАПАДНО-КАЗАХСТАНСКАЯ ОБЛАСТЬ

ТОО ТАТПРОЕКТ
Лицензия:ГЛС 14018895
Заказ:654-24

Заказчик: ТОО «Приуральная Металлоломная компания»

Строительство пункта приема по адресу:
ЗКО, г.Уральск, Промзона Желаетов,строение 39/2

Директор



Махметов А.Б.

Уральск 2025 год


					стадия	лист	листо́в
ГИП	Кажиахметов				ЭП	1	13
Исполнитель	Жунусов						
				Общие данные		ТОО ТАТПРОЕКТ г. Уральск	

Согласовано			

Ситуационная схема




Земельный участок S=0.6028 га.
право частной собственности
ЗКО, г. Уральск, промзона Желаетово строение 39/2

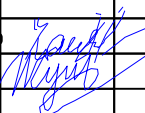				стадия	лист	листов
ГИП	Кажиахметов			ЭП	2	13
Исполнитель	Жунусов			Ситуационная схема		
				ТОО ТАТПРОЕКТ г. Уральск		

ЭКСПЛИКАЦИЯ

Генеральный план М 1:500

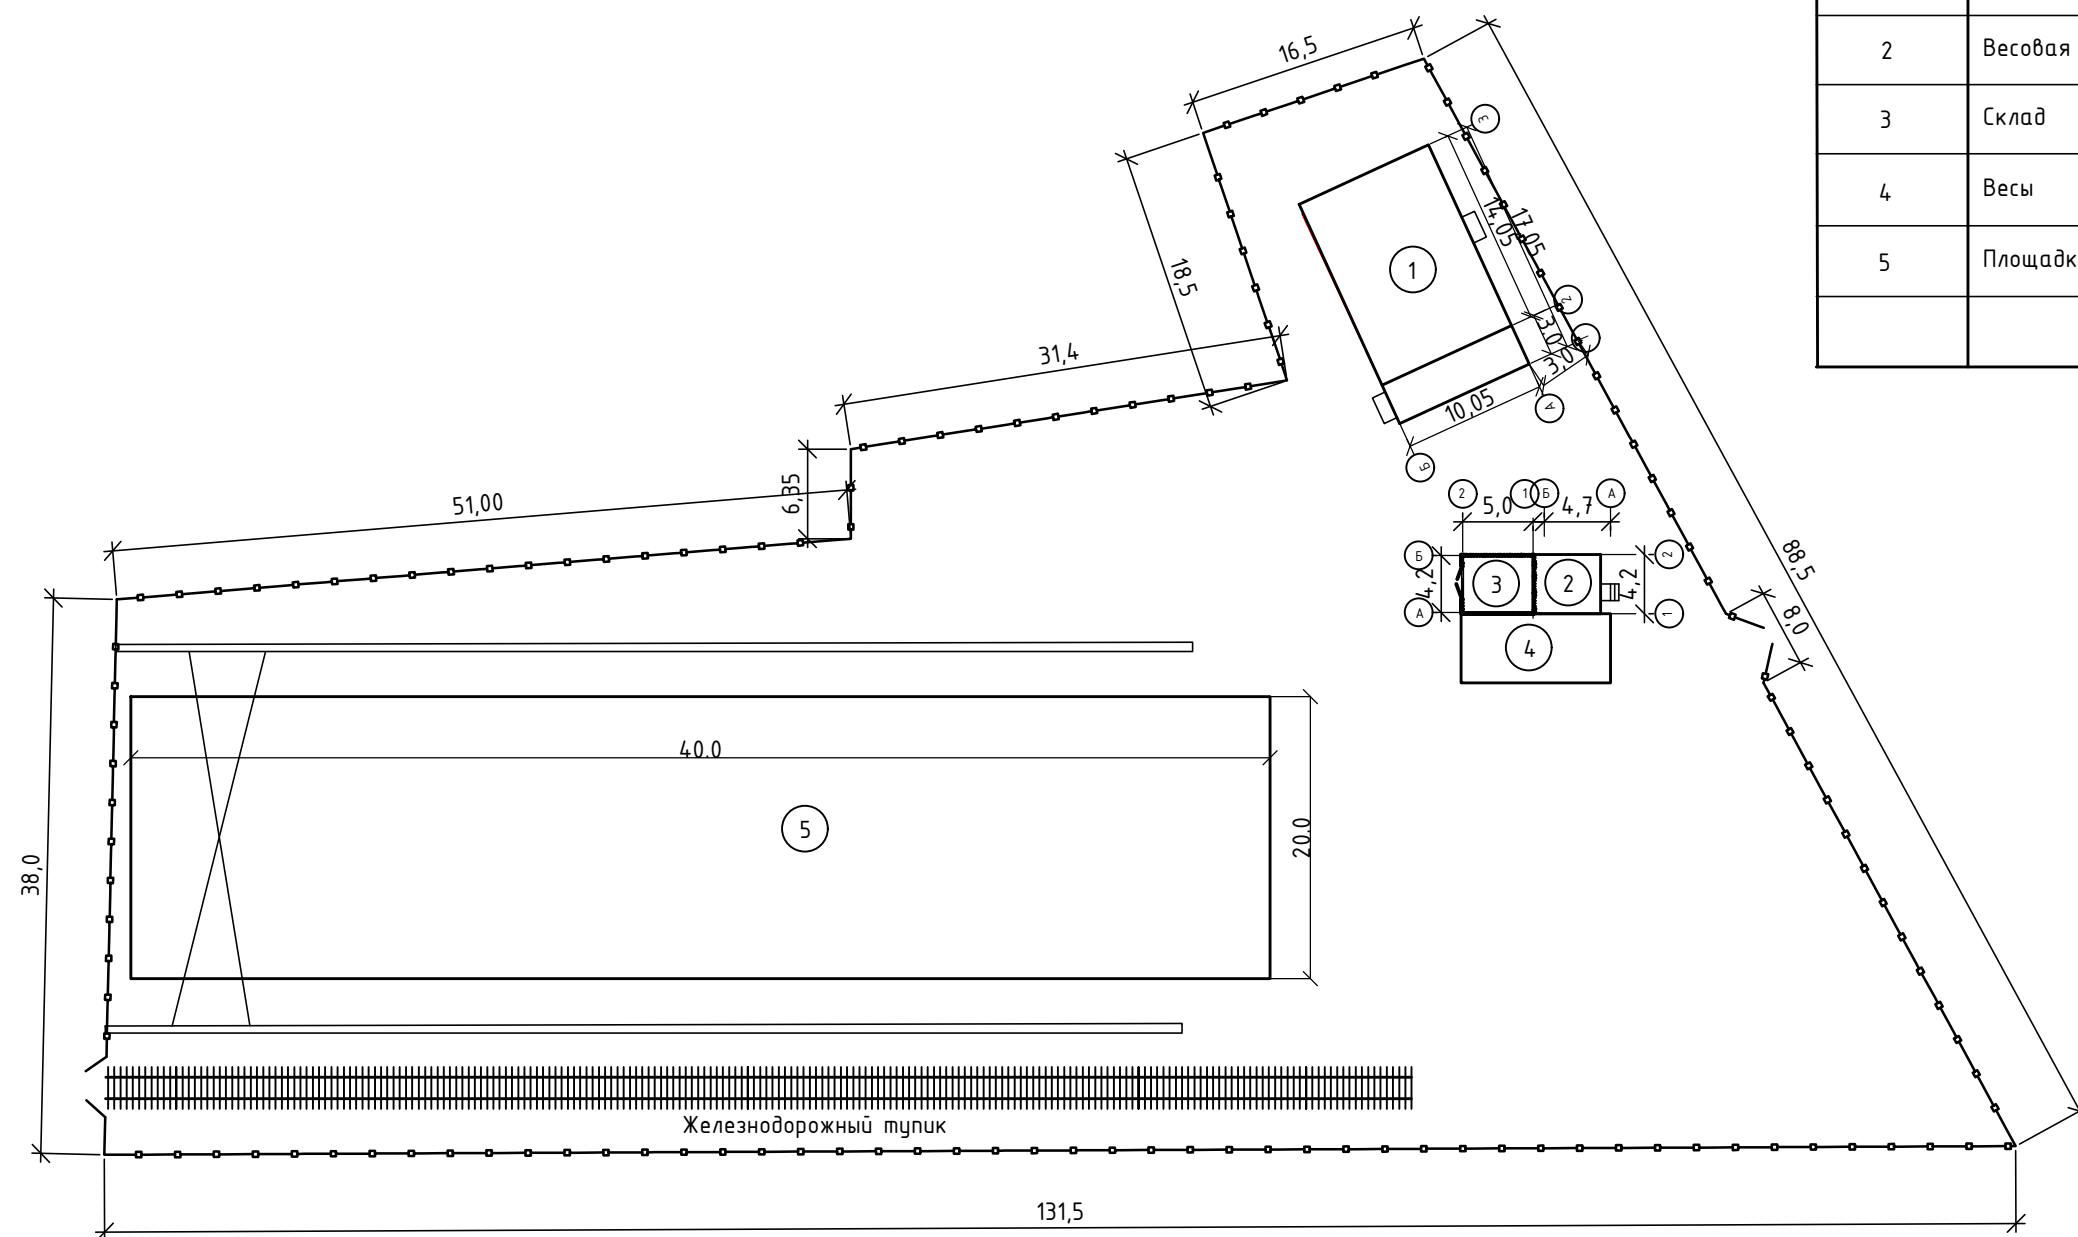


номер на плане	Наименование
1	2
1	Административное здание
2	Весовая
3	Склад
4	Весы
5	Площадка для складирования груза

Согласовано


					стадия	лист	листов
ГИП	Кажиахметов				ЭП	3	13
Исполнитель	Жунусов						
				Генеральный план М 1:500		ТОО ТАТПРОЕКТ	г. Уральск

Согласовано

Фасад в осях 1-3 М 1:100

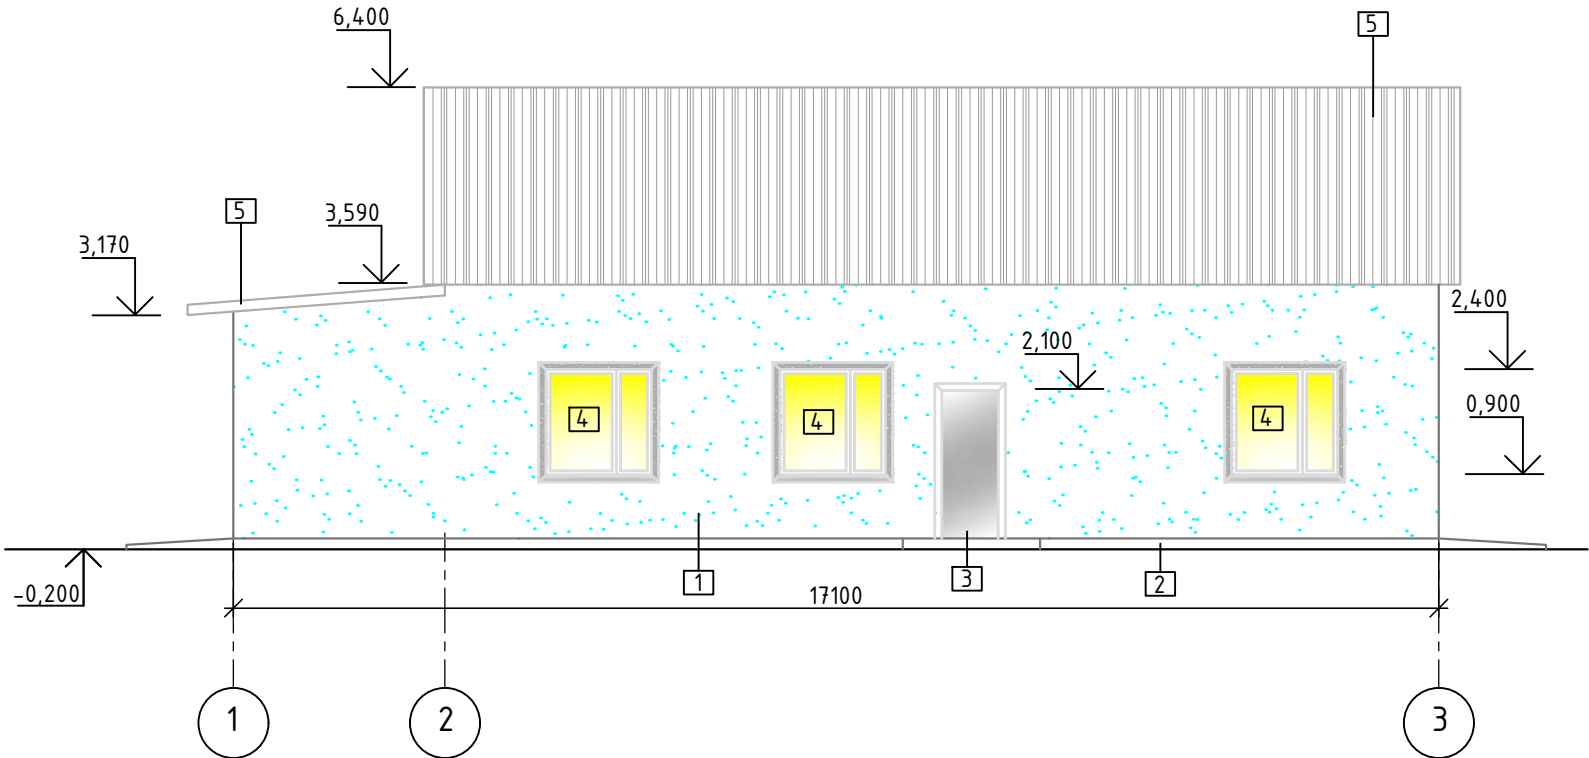


Фасад в осях 3-1 М 1:100

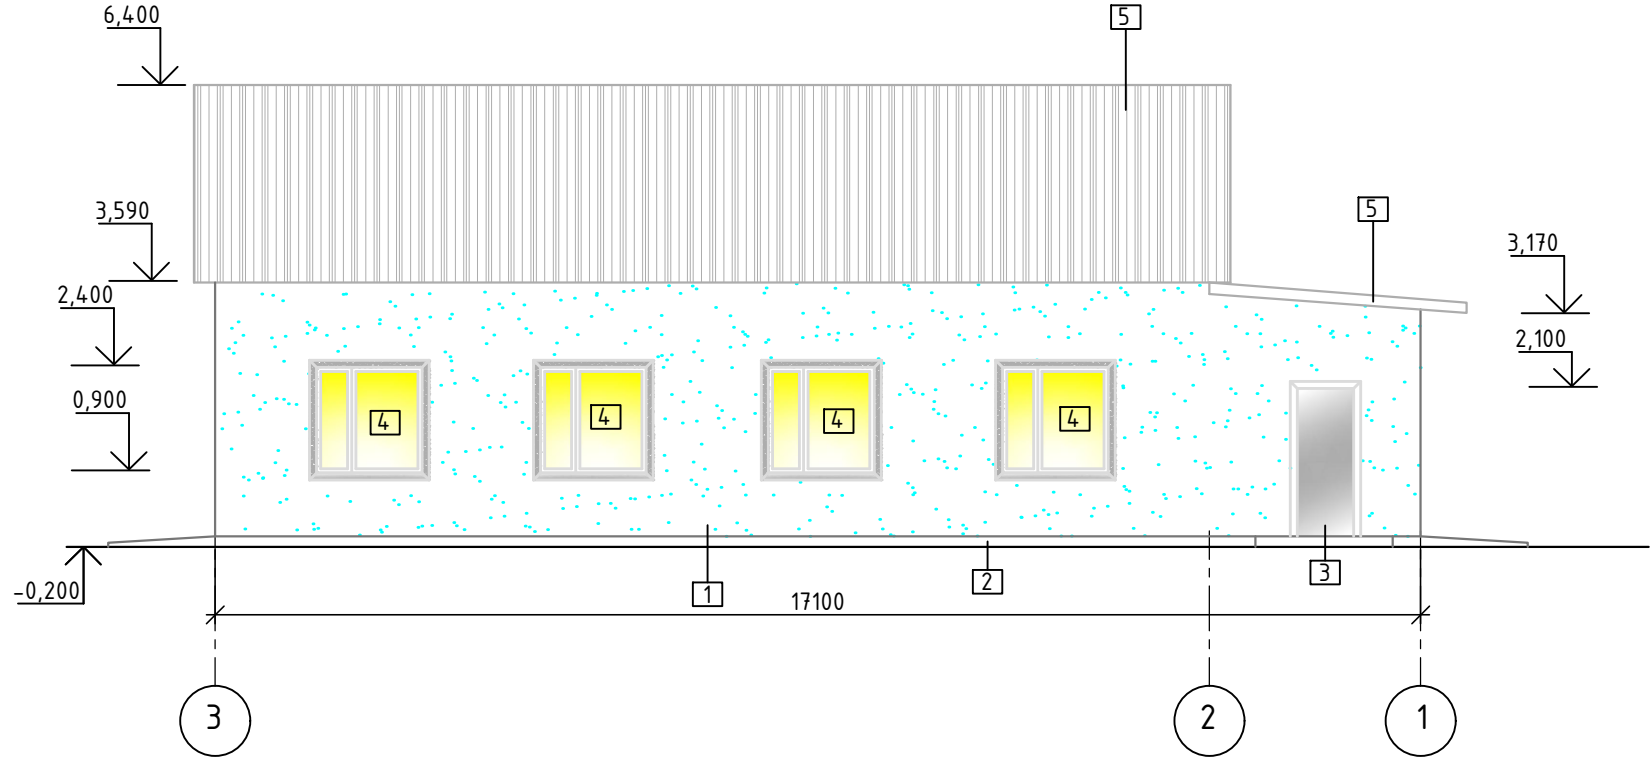


ГИП	Кажиахметов			стадия	лист	листов
Исполнитель	Жунусов			ЭП	4	13
				Административное здание		
				Фасад 1-3, 3-1. М 1:100.		
				ТОО ТАТПРОЕКТ		
				г. Уральск		

Согласовано

Фасад в осях А-Б М 1:100

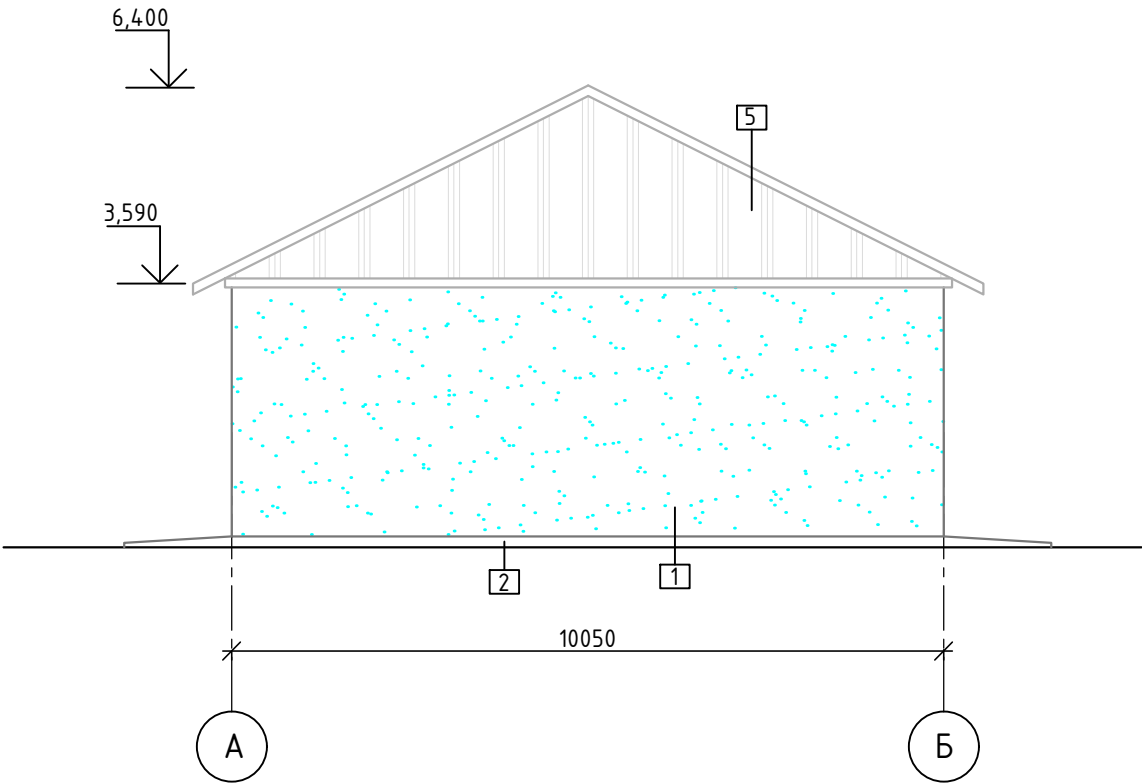

Фасад в осях Б-А М 1:100

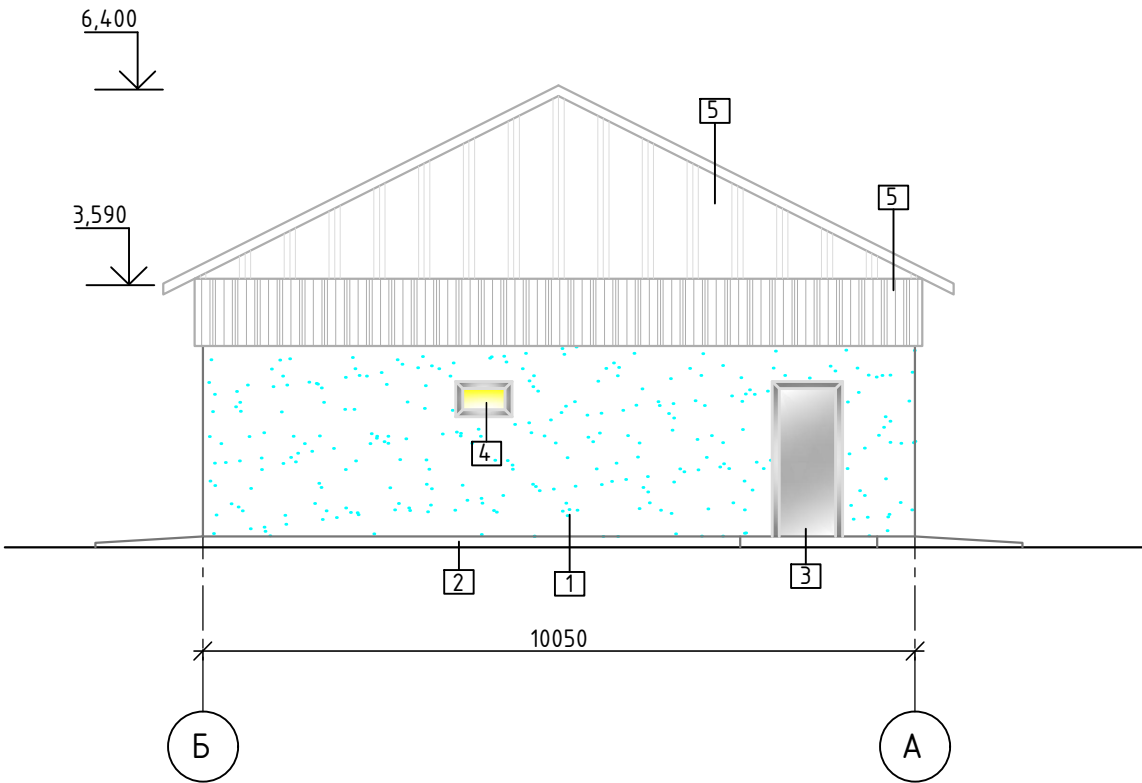


Ведомость отделки фасадов

Тип отделки	Элемент фасада	Отделка	Цвет	Примечания
1	Основные плоскости наружных стен	Декоративная штукатурка "Alinexs" Силикатный кирпич толщ.510мм	Голубой	RAL-5012
2	Цоколь здания	Штукатурка Шуба	Жемчужный темно-серый	RAL-9023
3	Дверные б/локи	Металлические, эмаль для наружных работ	Антрацитово-серый	RAL-7016
4	Окна	ПВХ профили, заполнение 2-х камерный стеклопакет	Белый	RAL-9003
5	Покрытие кровли	Профнастил НС44-1000-07	Оцинкованный	

ГИП	Кажиахметов			стадия	лист	листов
Исполнитель	Жунусов			ЭП	5	13
				Административное здание Фасад А-Б, Б-А. М 1:100.		
				ТОО ТАТПРОЕКТ г. Уральск		

План на отм. 0.000 М 1:100

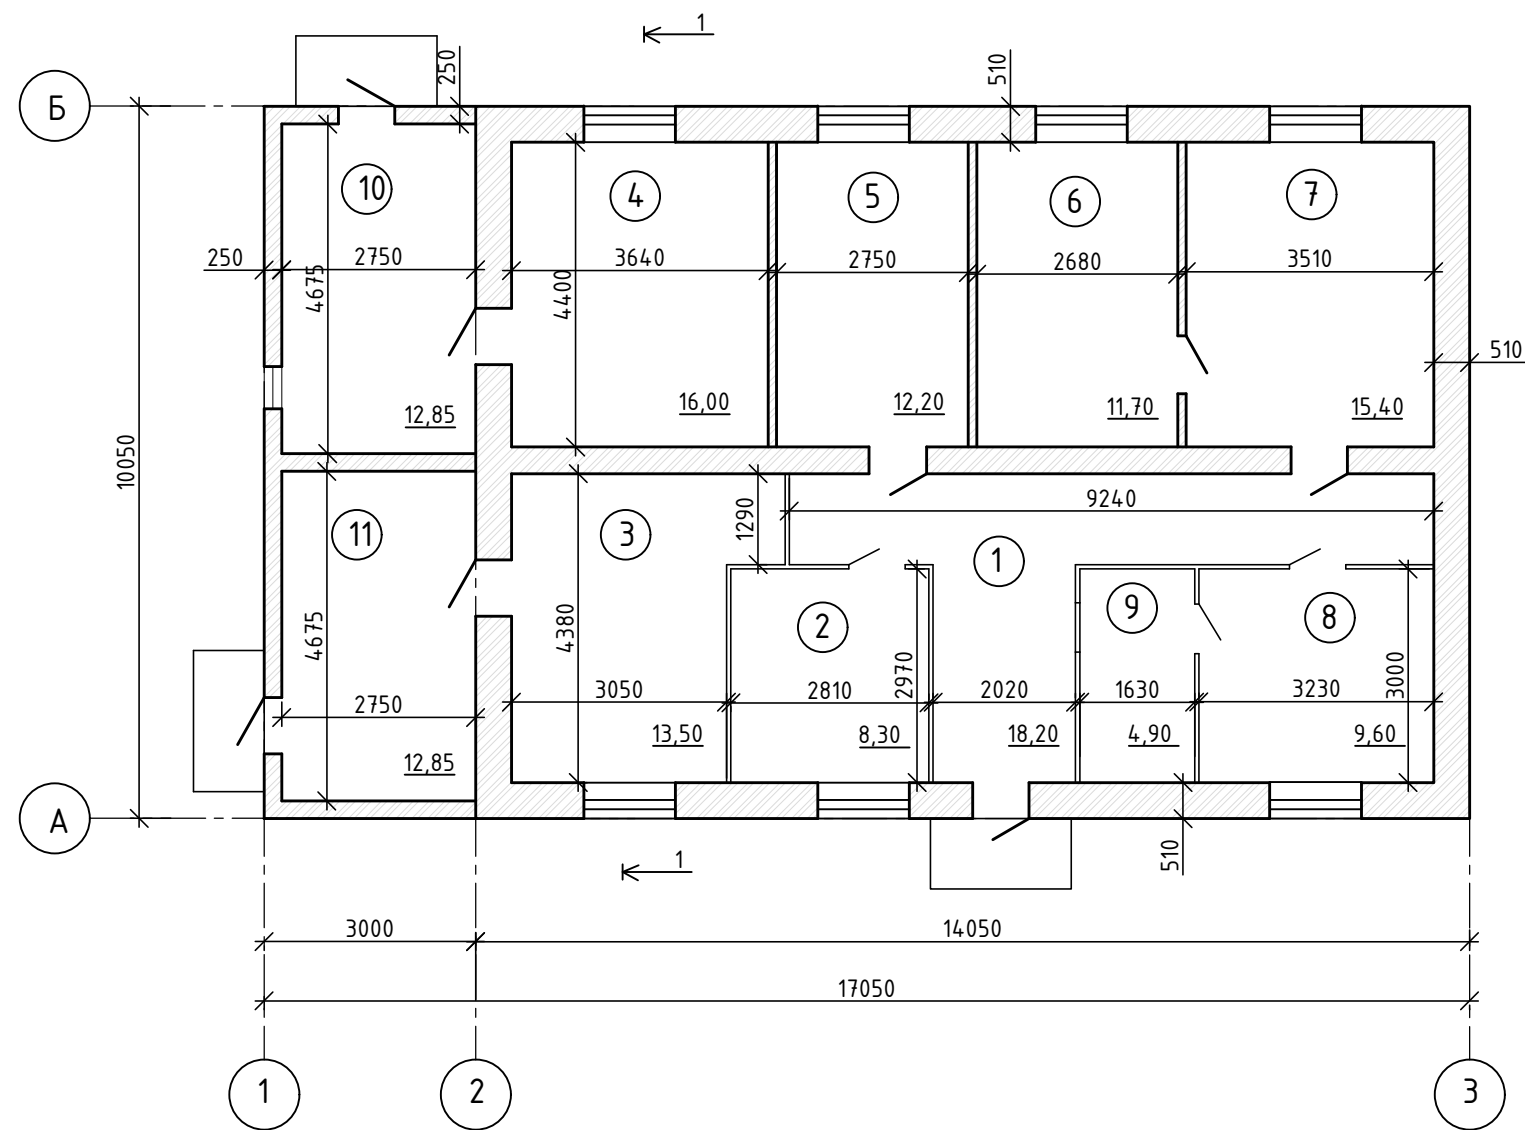


Экспликация помещений

№ помещ.	Наименование	Площадь м2
1	Коридор	18,20
2	Кабинет	8,30
3	Кабинет	13,50
4	Кабинет	16,00
5	Кабинет	12,20
6	Кабинет	11,70
7	Кабинет	15,40
8	Кабинет	9,60
9	Кабинет	4,90
10	Тамбур	12,85
11	Тамбур	12,85
Итого:		135,50

Согласовано

ГИП	Кажиахметов	ЭП	стадия	лист	листов
Исполнитель	Жунусов	ЭП	ЭП	6	13
Административное здание			ТОО ТАТПРОЕКТ		
План на отм. 0.000, Экспликация помещений.			г. Уральск		

Разрез 1-1 М 1:100

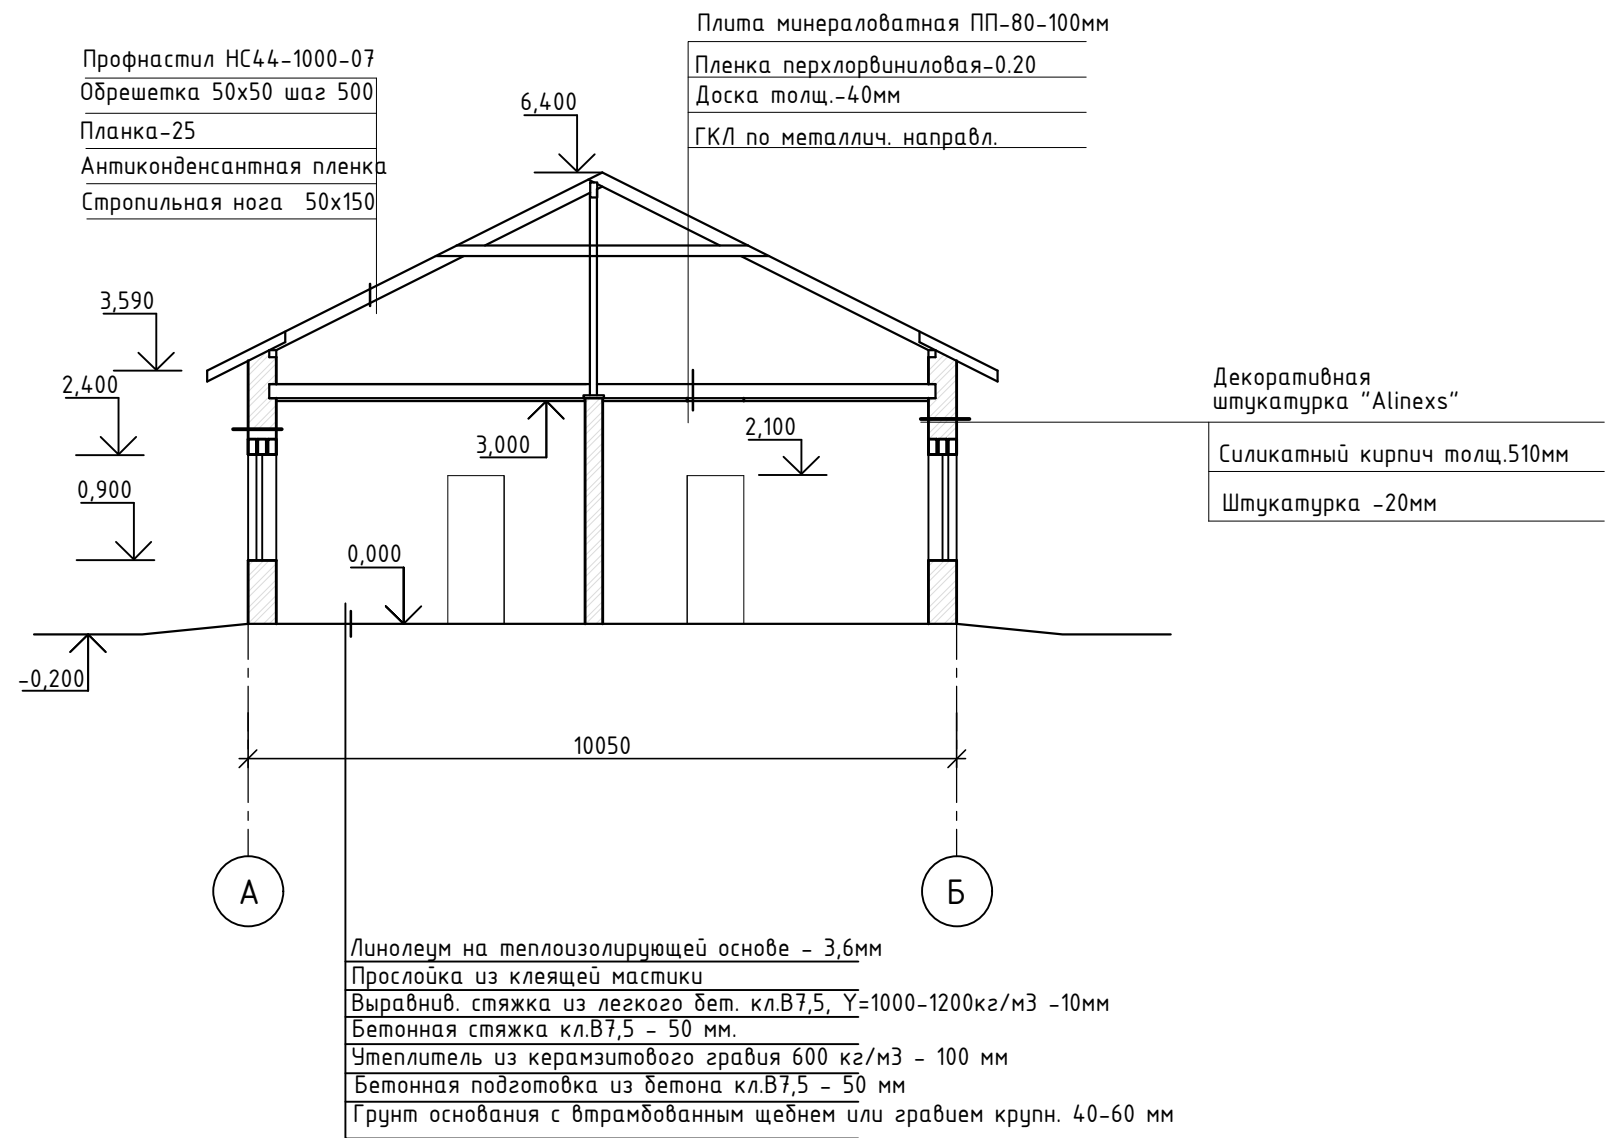


Согласовано

				стадия	лист	листов
ГИП	Кажиахметов			ЭП	7	13
Исполнитель	Жунусов			Административное здание Разрез 1-1 М 1:100		
				ТОО ТАТПРОЕКТ г. Уральск		

Согласовано			


План кровли М 1:100

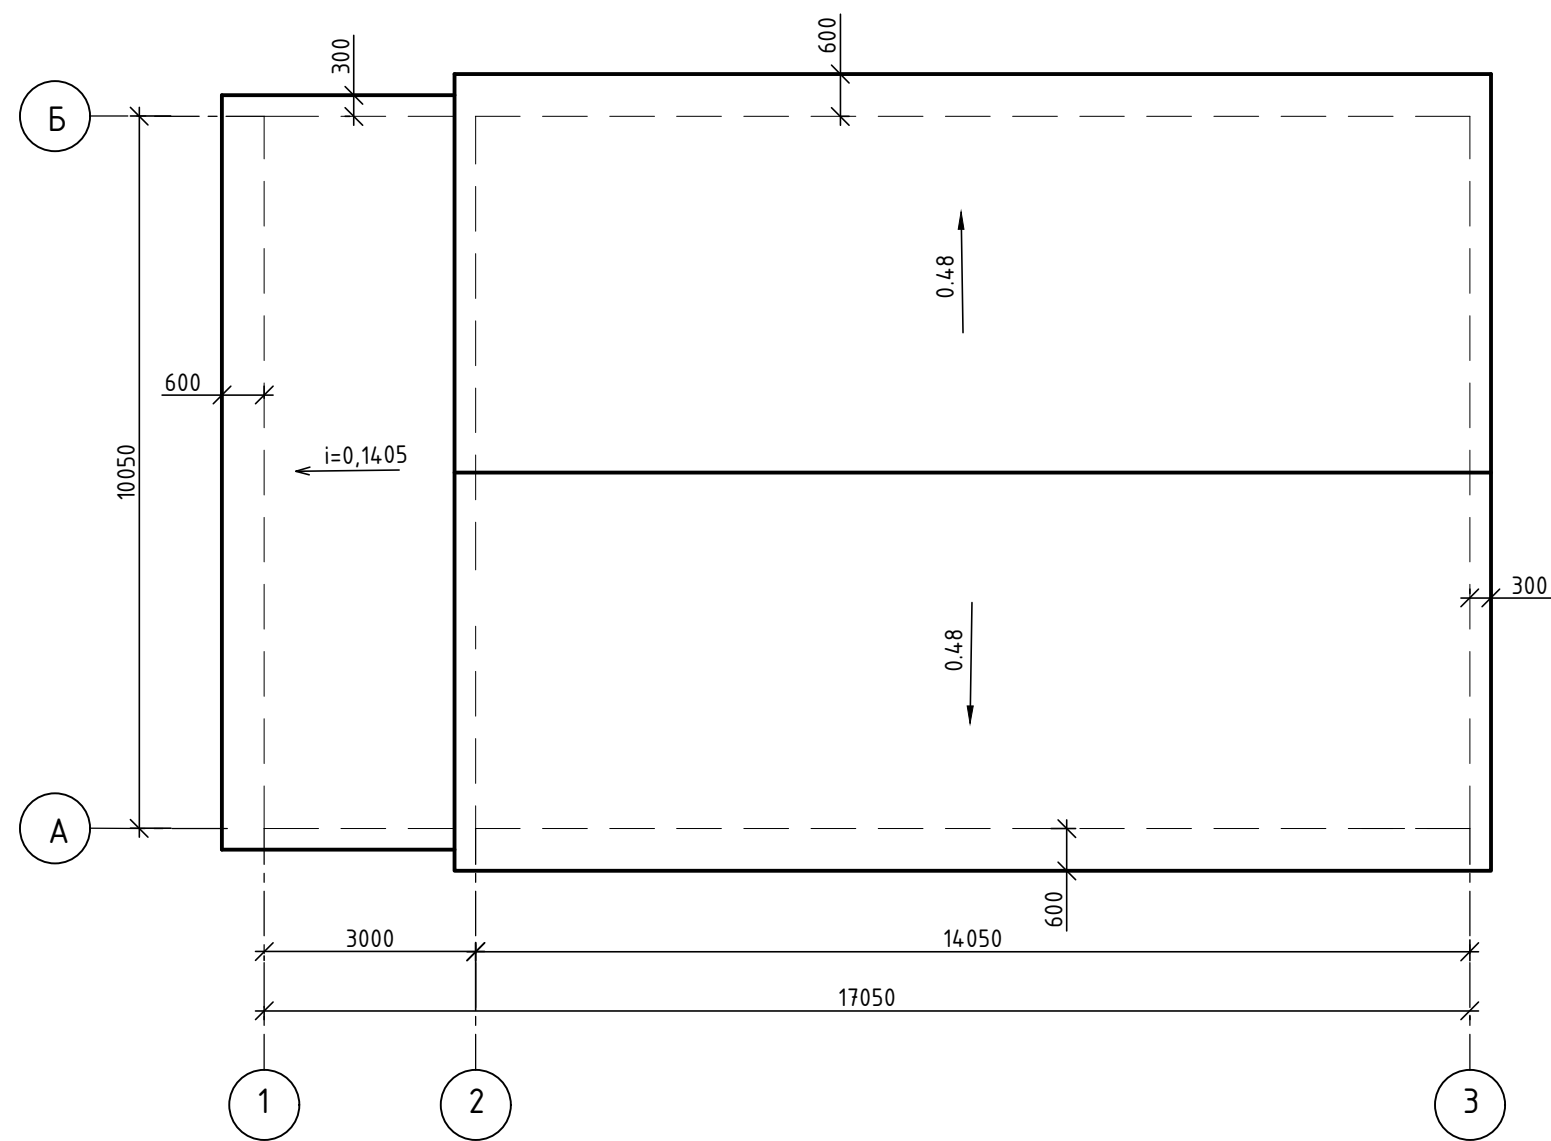


Кровля из профнастила НС44-1000-07 по деревянной обрешетке.

				стадия	лист	листов
ГИП	Кажиахметов			ЭП	8	13
Исполнитель	Жунусов			Административное здание План кровли М 1:100		
				ТОО ТАТПРОЕКТ г. Уральск		

План на отм. 0.000 М 1:100

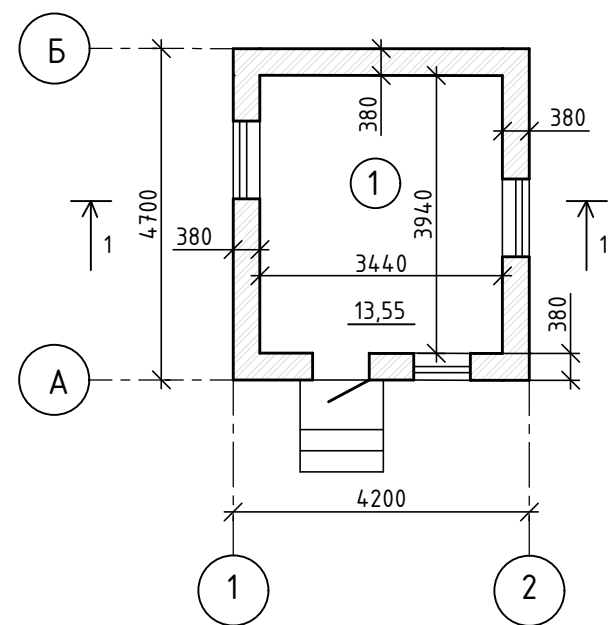


План кровли М 1:100

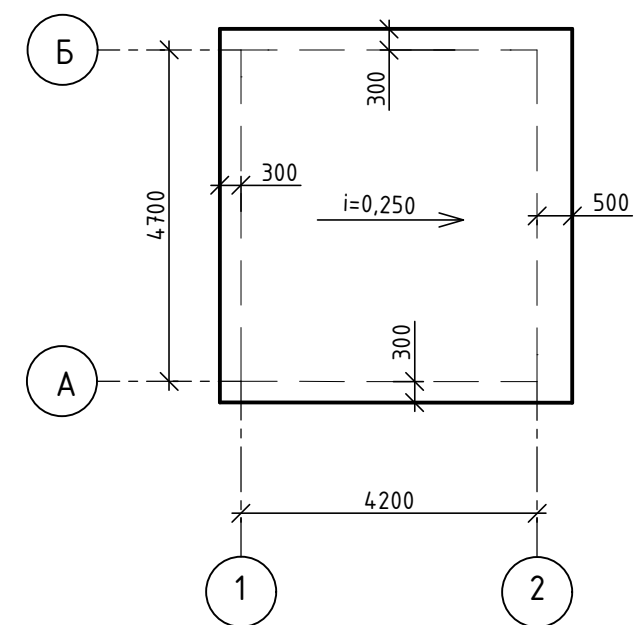

Разрез 1-1 М 1:100

Профнастил НС44-1000-07
Обрешетка 50х50 шаг 500
Планка-25
Антиконденсатная пленка
Стропильная нога 50х150
ГКЛ по металлич. направл.

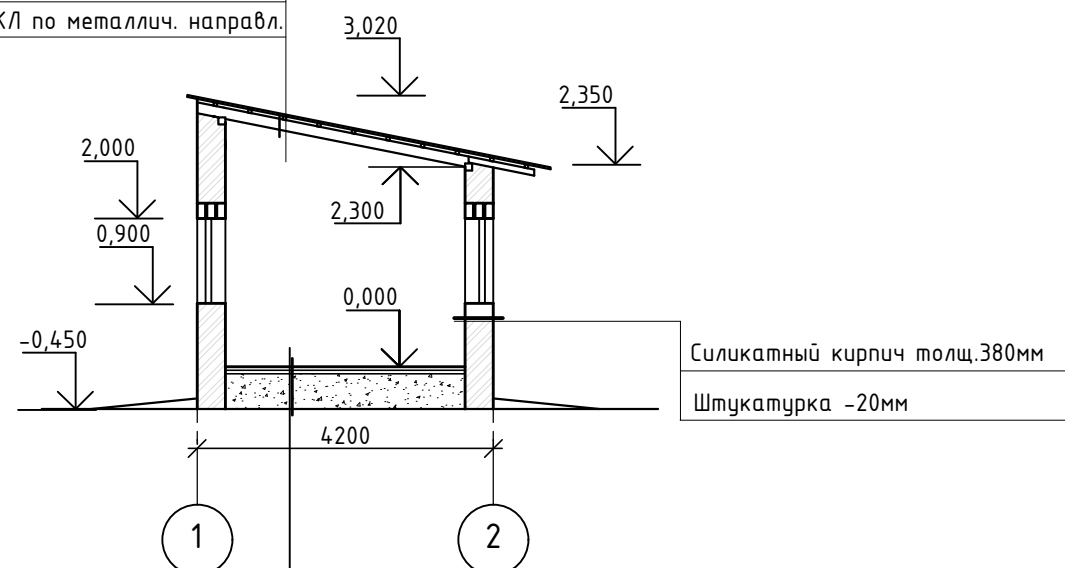




Линолеум на теплоизолирующей основе - 3,6мм
Прослойка из клеящей мастики
Выравнив. стяжка из легкого бет. кл.В7,5, Y=1000-1200кг/м3 - 10мм
Бетонная стяжка кл.В7,5 - 50 мм.
Утеплитель из керамзитового гравия 600 кг/м3 - 100 мм
Бетонная подготовка из бетона кл.В7,5 - 50 мм
Грунт основания с втрамбованным щебнем или гравием крупн. 40-60 мм

Экспликация помещений

№ помещ.	Наименование	Площадь м2
1	Весовая	13,55


					стадия	лист	листов
ГИП	Кажиахметов				ЭП	9	13
Исполнитель	Жунусов						
				Весовая	ТОО ТАТПРОЕКТ г. Уральск		
				План на отм. 0.000, Экспликация помещений.			
				Разрез 1-1, план кровли М 1:100			

Согласовано			

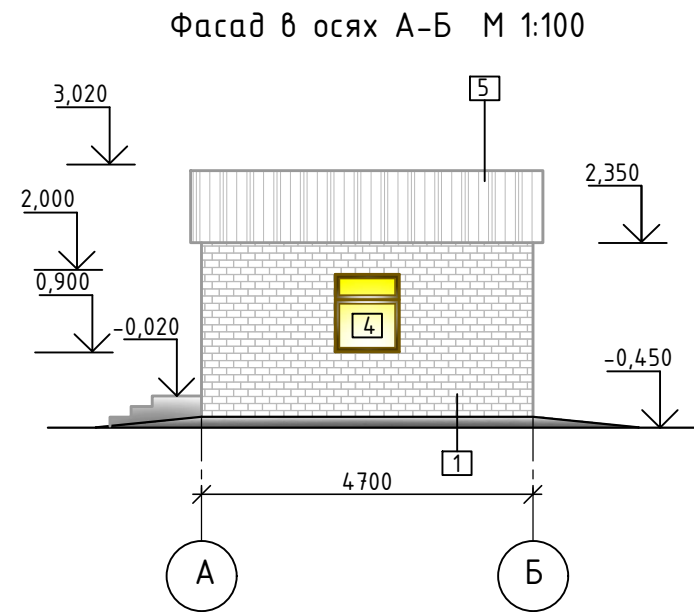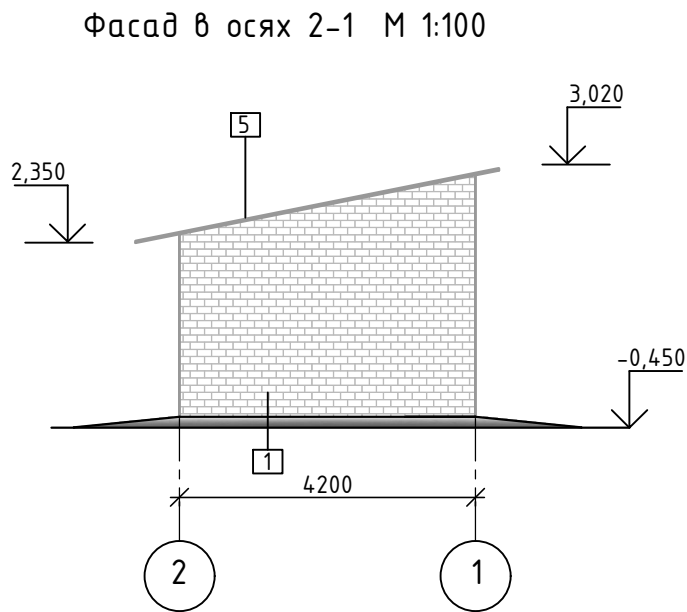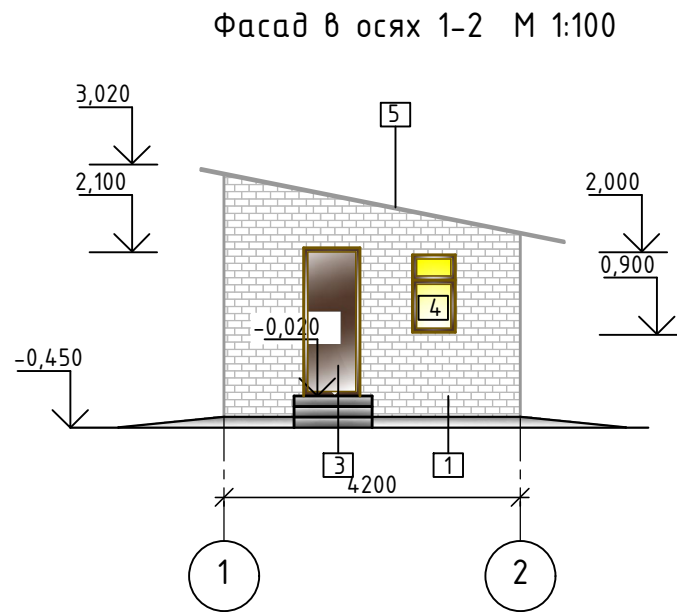

Ведомость отделки фасадов

Тип отделки	Элемент фасада	Отделка	Цвет	Примечания
1	Основные плоскости наружных стен	Кладка из силикатного лицевого кирпича С0Л-100/25	Бело-алюминиевый	RAL-9006
3	Дверные блоки	Металлические, эмаль для наружных работ	Коричнево-бежевый	RAL-1011
4	Окна	Деревянные, заполнение 2-х камерный стеклопакет	Орех	RAL-8001
5	Покрытие кровли	Профнастил НС44-1000-07	Оцинкованный	

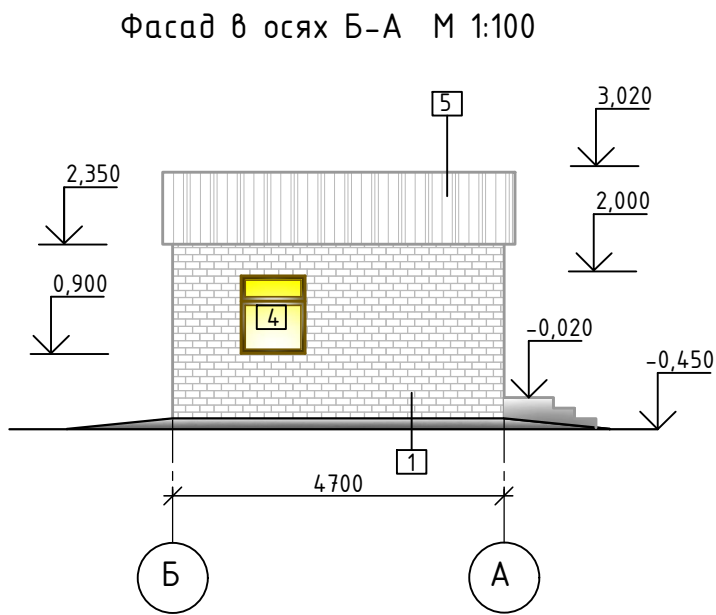

				стадия	лист	листов
ГИП	Кажиахметов			ЭП	10	13
Исполнитель	Жунусов					
				Весовая		
				Фасад в осях 1-2, 2-1, А-Б, Б-А М 1:100		
					ТОО ТАТПРОЕКТ	
					г. Уральск	

Technical drawing of a rectangular room. The overall dimensions are 5000 (width) and 4200 (height). The room is divided into four quadrants by a vertical line at 2190 from the right edge and a horizontal line at 2300 from the bottom edge. The left wall has a decorative wavy pattern. The top and bottom walls have a dashed line with a dimension of 1. The room is labeled with grid lines 1 and 2 horizontally, and A and B vertically.

Technical drawing of a rectangular structure, likely a foundation or slab, showing dimensions and labels.

The overall width is 5000 units. The overall height is 4200 units.

The structure is divided into two horizontal sections, each 500 units high. The top section is labeled with a downward arrow and $i=0,1405$. The bottom section is labeled with an upward arrow and $i=0,1405$.

Labels A and Б are positioned on the left side, corresponding to the bottom and top sections respectively. Labels 1 and 2 are positioned at the bottom corners, corresponding to the left and right sides respectively.

Dimensions 200 and 500 are indicated for the top section, and 200 and 500 are indicated for the bottom section.

Разрез 1-1 М 1:100

3,100

2,400

-0.200.

-0.000

4,200

А Б

-Профнастил оцинкованный Н44-1100-0.7

-Прогон квадратная труба 50х50х3

-ФМ-1


-Профнастил оцинкованный с полимерным покрытием С10-1100-0.7

№ помещ.	Наименование	Площадь, м2
1	Холодный склад	21,90


				стадия	лист	листо́в
ГИП	Кажирахметов			ЭП	11	13
Исполнитель	Жунусов					
				Склад		
				План на отм. 0.000 М 1:100, разрез 1-1,		
				план кровли М 1:100.		
				ТОО ТАТПРОЕКТ		
				г. Уральск		

Согласовано


Фасад в осях 1-2, 2-1 М 1:50

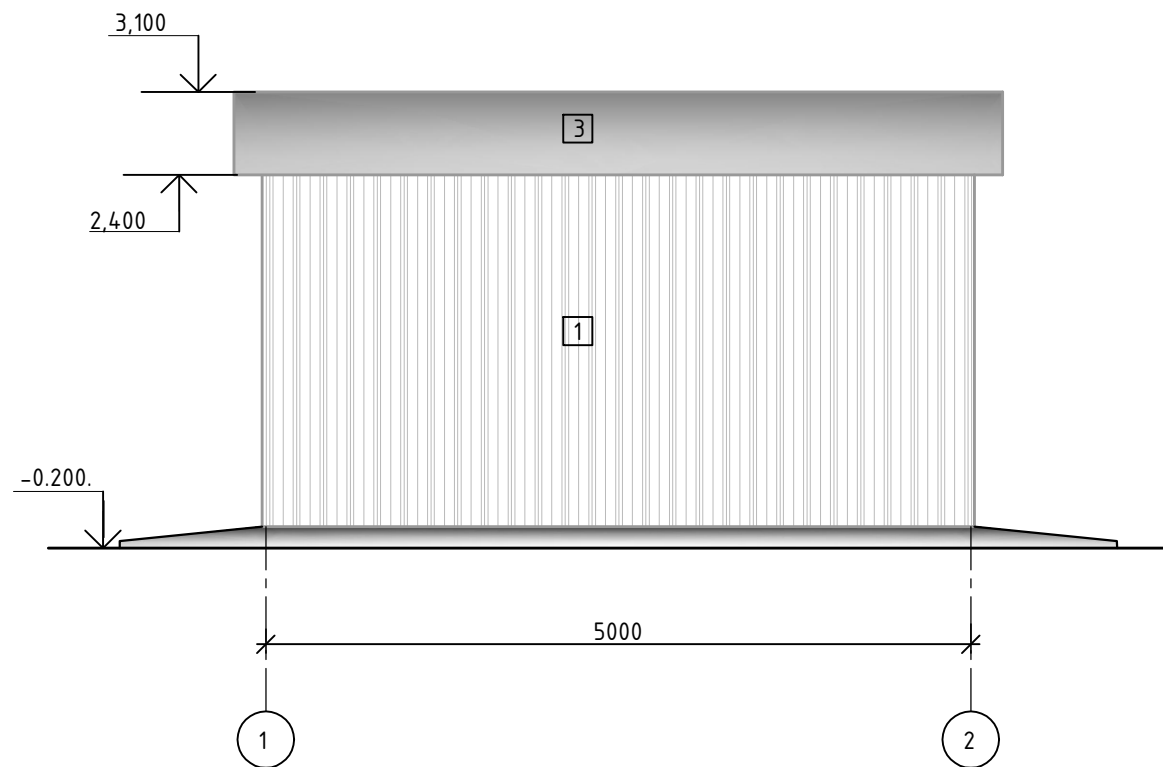

Фасад в осях А-Б М 1:50

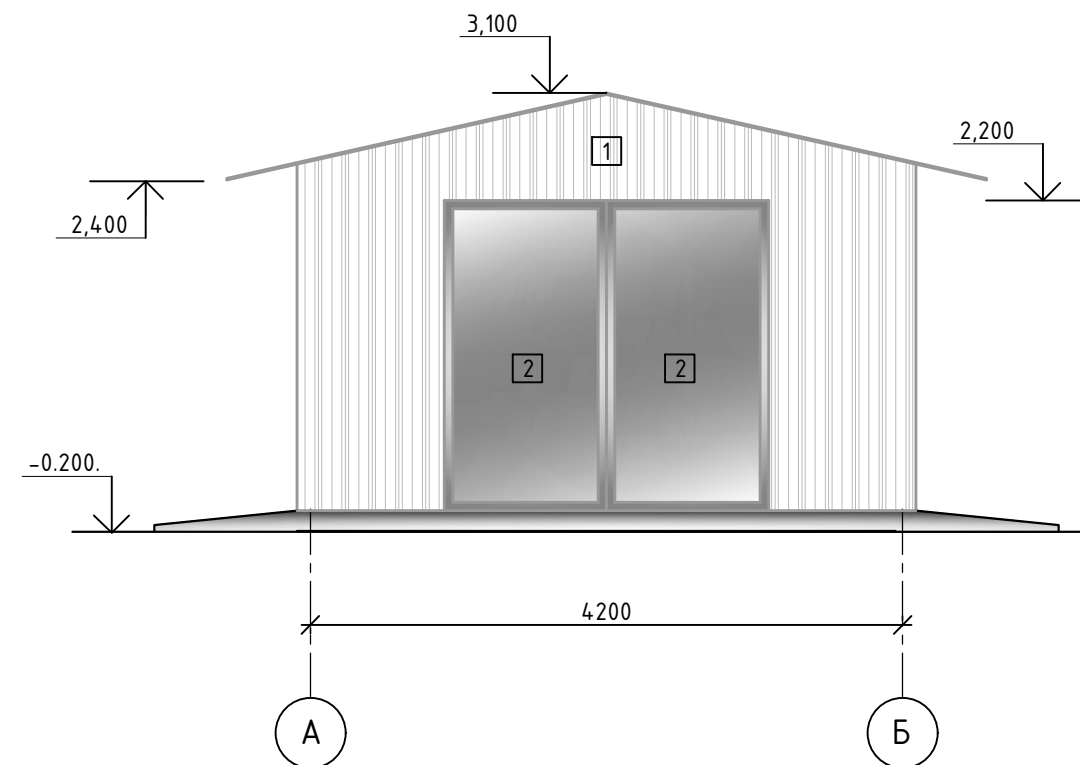

Фасад в осях Б-А М 1:50

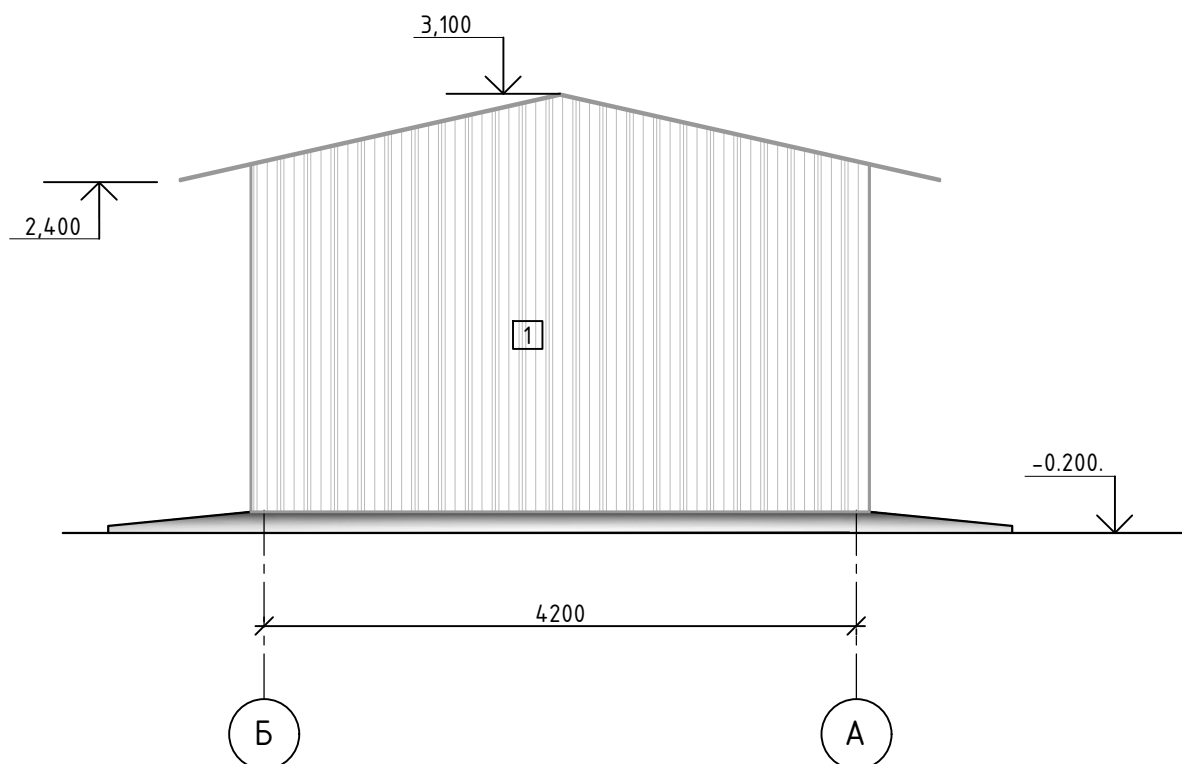


Ведомость отделки фасадов

Тип отделки	Элемент фасада	Отделка	Цвет	Примечания
1	Основные плоскости наружных стен	Профлист С 21-1000-0.7	Алюминиевый	RAL-9006
2	Ворота	Металлические, эмаль для наружных работ	Алюминиевый	RAL-9006
3	Покрытие кровли	Профнастил НС44-1000-07	Алюминиевый	RAL-9006


ГИП	Кажиахметов	ЭП	стадия	лист	листов
Исполнитель	Жунусов	ЭП	12	13	
Склад	Фасад в осях 1-2, 2-1 М 1:50 Фасад в осях А-Б, Б-А М 1:50	ТОО ТАТПРОЕКТ г. Уральск			

Согласовано				


План площадки М 1:500

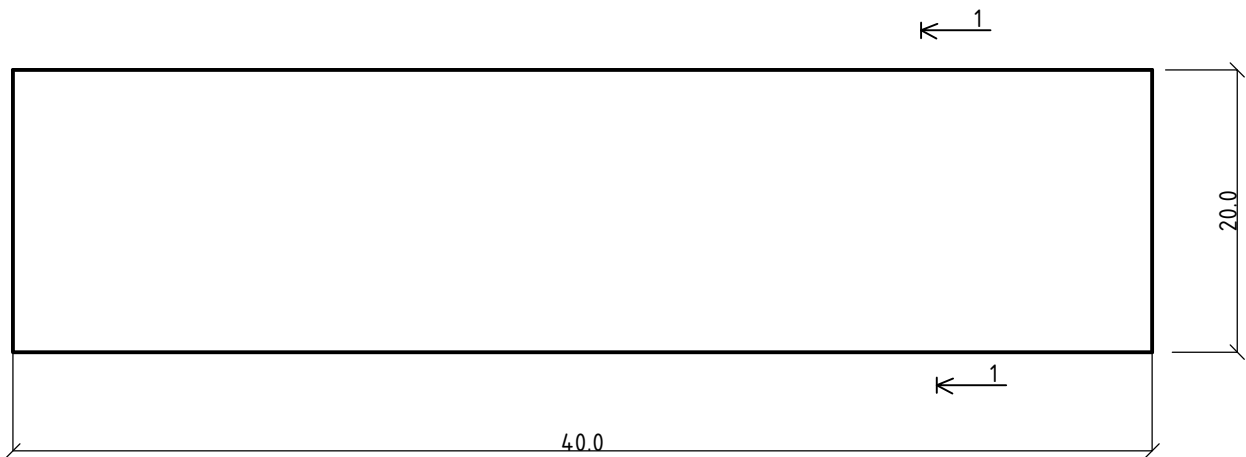

УЗЕЛ 1

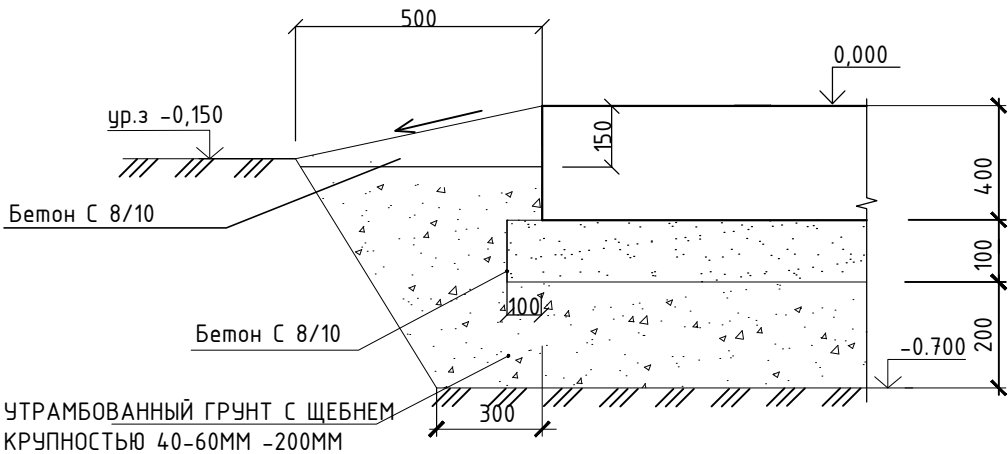

РАЗРЕЗ 1-1 М 1:50

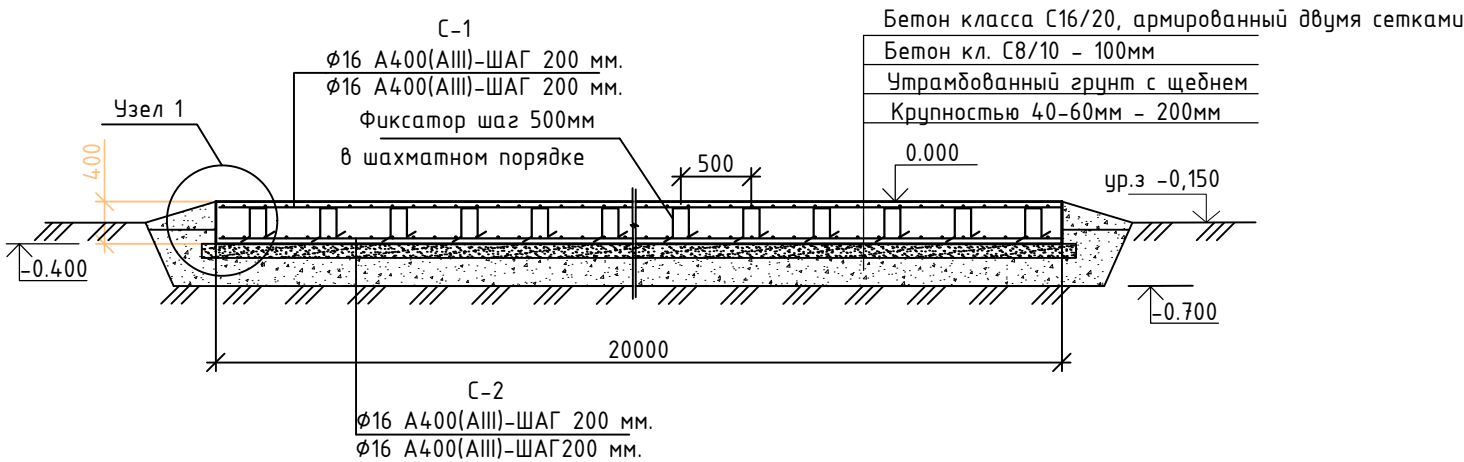

					стадия	лист	листов
ГИП	Кажиахметов				ЭП	13	13
Исполнитель	Жунусов						
				План площадки М 1:500, разрез 1-1 М1:50	ТОО ТАТПРОЕКТ г. Уральск		