

**Строительство двухэтажного административного
здания с подвалом и открытой террасой,
расположенного на земельном участке
по адресу РК, г.Усть-Каменогорск,
набережная им.Е.П.Славского, гараж №40Г**

Стадия проектирования: П
Раздел: АР

Заказчик:

 Рябенко Надежда Анатольевна

Местонахождения:

РК, г.Усть-Каменогорск, набережная им.Е.П.Славского,
гараж №40Г

ГИП



Косолапова В.А.

г.Усть-Каменогорск
2025 г.

СИТУАЦИОННАЯ СХЕМА



Отведенный земельный участок под строительство
кадастровый номер 05-085-072-945; 05-085-072-1527

Технические решения, принятые в проекте, соответствуют требованиям экологических, санитарно-гигиенических, противопожарных и других действующих норм и правил, и обеспечивают безопасную для жизни и здоровья людей эксплуатацию объекта при соблюдении предусмотренных рабочими чертежами мероприятий.

Главный инженер проекта

Косолапова В.А.

Общие данные

Архитектурно-строительная часть рабочего проекта «Строительство двухэтажного административного здания общей площадью 702,34м.кв, расположенного на земельном участке по адресу: РК, г.Усть-Каменогорск, набережная им.Е.П.Славского, гараж №40 разработан в соответствии со СН РК 1.02-03-2011 "Порядок разработки, согласования, утверждения и состав проектной документации на строительство", архитектурно-планировочным заданием, договора с заказчиком и заданием на проектирование, утвержденным заказчиком. Проект разработан г.Усть-Каменогорск, ВКО, Проект разработан для IV климатического подрайона, с расчетной зимней температурой наружного воздуха $t = -37^{\circ}\text{C}$, в сухой зоне влажности. За условную отметку 0,000 принят уровень чистого пола помещений 1-го этажа, соответствующую абсолютной отметке на местности 419.60

ОСНОВНЫЕ ПОКАЗАТЕЛИ ПО ГЕНПЛАНУ

Наименование	Количество м ²	%
Площадь отведенного земельного участка по Акту кадастровый номер 05-085-072-945; -0,0350 га 05-085-072-1527; -0,0224 га	574	100
а) площадь застройки	203,58	36
б) площадь покрытия	323,0	56
в) площадь озеленения	28,0	5
г) прочие площади	19,42	3
Площадь покрытия по прилегающей территории	291,0	-

						АР			
						Строительство двухэтажного административного здания с подвалом и открытой террасой, расположенного на земельном участке по адресу РК, г.Усть-Каменогорск, набережная им.Е.П.Славского, гараж №40Г			
Изм.	Кол.уч.	Лист	№ док.	Подпись	Дата	Административное здание	Стадия	Лист	Листов
ГИП		Косолапова В.А.					П	1	18
Архитектор									
						Общие данные. Схема размещения.	ООО "СемСтройтехнаб"		
							Государственная		
							лицензия ГС/Л №18016321		


Перед входами в здание предусмотрены крыльцо, с защищенное от осадков, Крыша - скатная чердачная с наружным организованным водостокам по системе "Металлпрофиль". Для прокладки инженерных сетей в здании предусмотрены технические помещения. Эвакуация людей из помещений осуществляется: - из помещений подвала по лестнице непосредственно наружу - из помещений первого этажа - непосредственно наружу; - из помещений второго этажа по лестнице Л1 в лестничной клетке 1 типа Шумоизоляция помещений достигается посредством планировочных мероприятий, применением металлопластиковых окон со стеклопакетом и эффективных шумоизолирующих материалов в конструкциях стен и полов. Теплотехнический расчет ограждающих конструкций зданий выполнен на основании проектных решений с использованием эффективных теплоизоляционных материалов с соблюдением нормативных требований, согласно СН РК 2.04-21-2004 «Энергопотребление и тепловая защита гражданских зданий».

Наружная отделка Отделка фасадов предусмотрена из долговечных материалов, не требующих ремонта в процессе длительной эксплуатации. Стены - Облицовочный кирпич, Навесной вентилируемый фасад с фибропанелями типа "Латонит", окраска фасадной акриловой краской Окна - ПВХ, Витражи - ПВХ, алюминиевые Двери - ПВХ по ГОСТ 30970-2014; стальные по ГОСТ 31173-2016, деревянные по ГОСТ ; стальные по ГОСТ 31173-2016, деревянные по ГОСТ 31173-2016, деревянные по ГОСТ 31173-2016, деревянные по ГОСТ ГОСТ 475-2016 Цоколь - экструдированный пенополистирол 50мм, сплитерная плитка . Кровля -металлочерепица

Внутренняя отделка Внутренняя отделка Внутренняя отделка помещений предусмотрена в соответствии с их назначением. Стены и перегородки окрашиваются водно-дисперсионной, акриловой краской, облицовываются глазурованной прямоугольной плиткой гладкой с завалом. Полы - керамическая плитка с рельефной поверхностью, бетонные, линолиум, ламинат 33 класс. Полы запроектированы в соответствии со СП РК 3.02-136-2013 "Полы". Откосы дверных и оконных проемов оштукатурить цементным раствором, выровнять шпатлевкой с последующей окраской в цвет стен. Столярные изделия должны быть окрашены масляной краской за два раза по заводской грунтовке.

Планировка участка обеспечивает свободный проезд к зданию. Противопожарные мероприятия назначены согласно - СП РК 2.02-101-2014 - "Пожарная безопасность зданий и сооружений". По конструктивным решениям здание относится ко 1-ой степени огнестойкости. Класс по конструктивной пожарной опасности - С0. Стены и перегородки имеют предел огнестойкости не менее 0,75 часа и класс пожарной опасности К0.

Главный инженер проекта  В.А.Косолапова

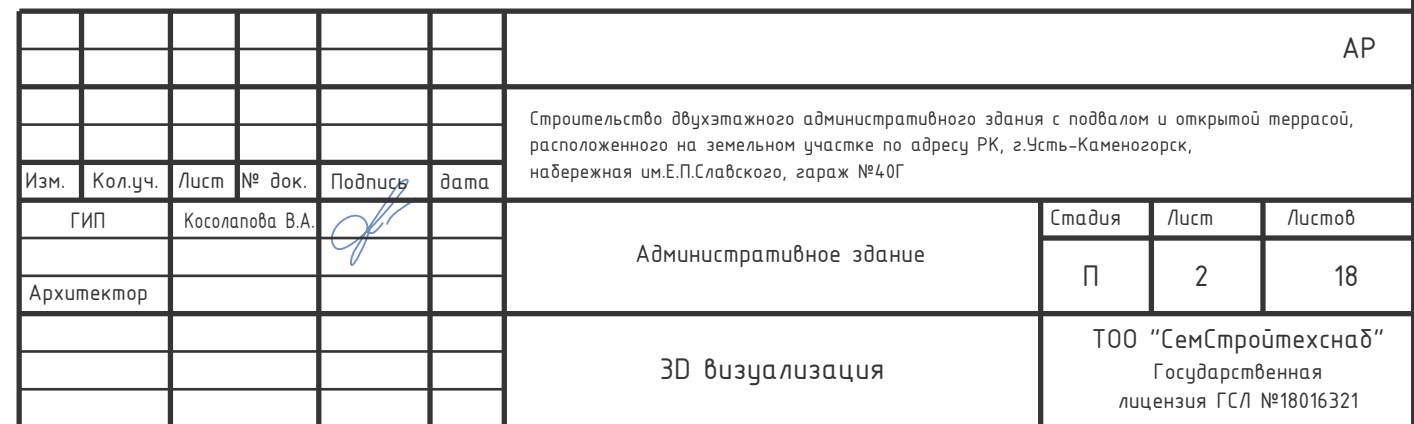

- Инженерные сети: водоснабжение - центральное; канализация - центральная; отопление местное - электродотел; электричество - центральное, согласно ТУ. Подключение объекта к сетям производится в соответствии с ТУ. Проекты подключения к сетям разрабатываются и согласовываются отдельно по каждому сетям.

Ведомость жилых и общественных зданий и сооружений

Номер на плане	Наименование и обозначение	Этаж-ность	Количество зданий	Площадь, м ²				Строительный м ³	
				застройки		общая			
				здания	всего	здания	всего	здания	всего
1	Административное здание	2	1		203,58				
2	Площадка для мусороконтейнеров, на 2 контейнера	-	1		3,0				
3	Стоянка на 6 автомашин в том числе 1 маш./мест для МГН	-	1		323,0				
4	Гараж (существующий)	1	1		-				
	итого				203,58				


Условное обозначение

- Граница отведенного земельного участка
- Проектируемое здание
- Существующее здание
- Скважина

1. Разбивку здания в плане производить от угла сужающегося здания гаража поз.4.
2. Все размеры на чертеже даны в метрах.
3. Размеры зданий и сооружений даны в осях.
4. Радиус закругления проездов $R=6$ метров.
5. Привязка площадок и дорожек в плане выполнены на листе ГП-6.

						АР			
						Строительство двухэтажного административного здания с подвалом и открытой террасой, расположенного на земельном участке по адресу РК, г.Усть-Каменогорск, набережная им.Е.П.Славского, гараж №40Г			
Изм.	Кол.уч.	Лист	№ док.	Подпись	дата	Административное здание	Стадия	Лист	Листов
ГИП		Косолапова В.А.					П	3	18
Архитектор									
						Разбивочный план. М1:500	ТОО "СемСтройтехснаб" Государственная лицензия ГСЛ №18016321		

ВЕДОМОСТЬ ОБЪЕМОВ ЗЕМЛЯНЫХ МАСС

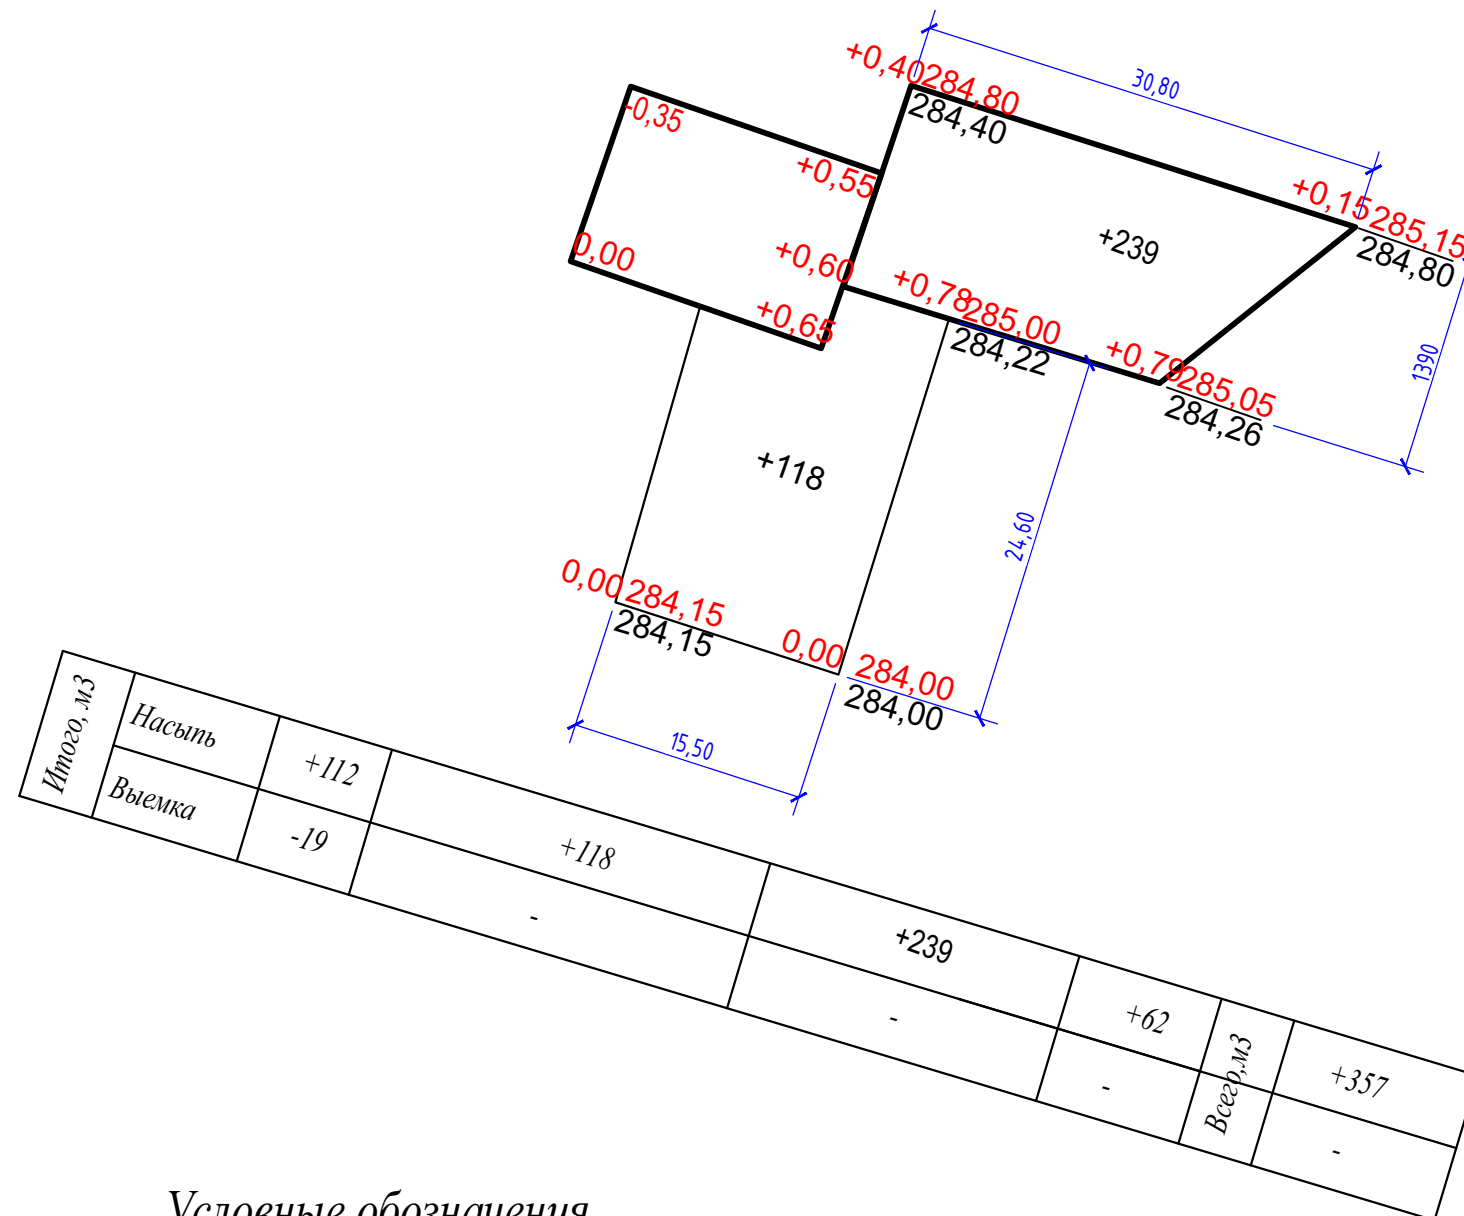

Условные обозначения


+0,60	424,70	Рабочая отметка	Проектная отметка
	424,10		Факт.отметка рельефа
$\frac{4}{32,0}$		Уклон в % ° расстояние	

Наименование грунта	Количество,м.З				Примеч.
	Насыпь	Выемка	Насыпь	Выемка	
1. Грунт планировки территории	357	-			
2. Вытесненный грунт,					
в том числе при устройстве:					
а) подземных частей зданий (сооружений)					
б)автодорожных покрытий		192,04			
в) срезка насыпи					
г) подземных сетей					
д) водоотводных сооружений					
е) под озеленение		6,15			
3. Грунт для устройства земляного полотна автодорог					
4. Грунт для устройства земляного полотна ж/д путей					
5. Грунт для устройства высоких полов зданий и сооружений					
6. Поправка на уплотнение	35,7				
7. Всего пригодного грунта	392,7	198,19			
8.Недостаток пригодного грунта		194,51			
9. Грунт непригодный для устройства насыпи оснований зданий, сооружений и подлежащий удалению с территории (торф)					
10. Плодородный грунт, всего,	-	-			
в том числе:					
а) используемый для озеленения территории	6,15				
б) недостаток плодородного грунта		6,15			
11. Итого перерабатываемого грунта	398,85	398,85			

1. Данный лист разработан на основании листа ГП-4.

						АР			
						Строительство двухэтажного административного здания с подвалом и открытой террасой, расположенного на земельном участке по адресу РК, г.Усть-Каменогорск, набережная им.Е.П.Славского, гараж №40Г			
Изм.	Кол.уч.	Лист	№ док.	Подпись	дата	Административное здание	Стадия	Лист	Листов
ГИП		Косолапова В.А.					П	5	18
Архитектор									
						План организации рельефа М1:500	ТОО "СемСтройтехнад"		
							Государственная		
							лицензия ГС/Л №18016321		

	Бортовой камень Бр 100.30.15; БК100.30.18.8
	Бортовой камень Бр 100.20.8.
	Резиновый бордюр
	Асфальтобетонное покрытие проездов тип 1

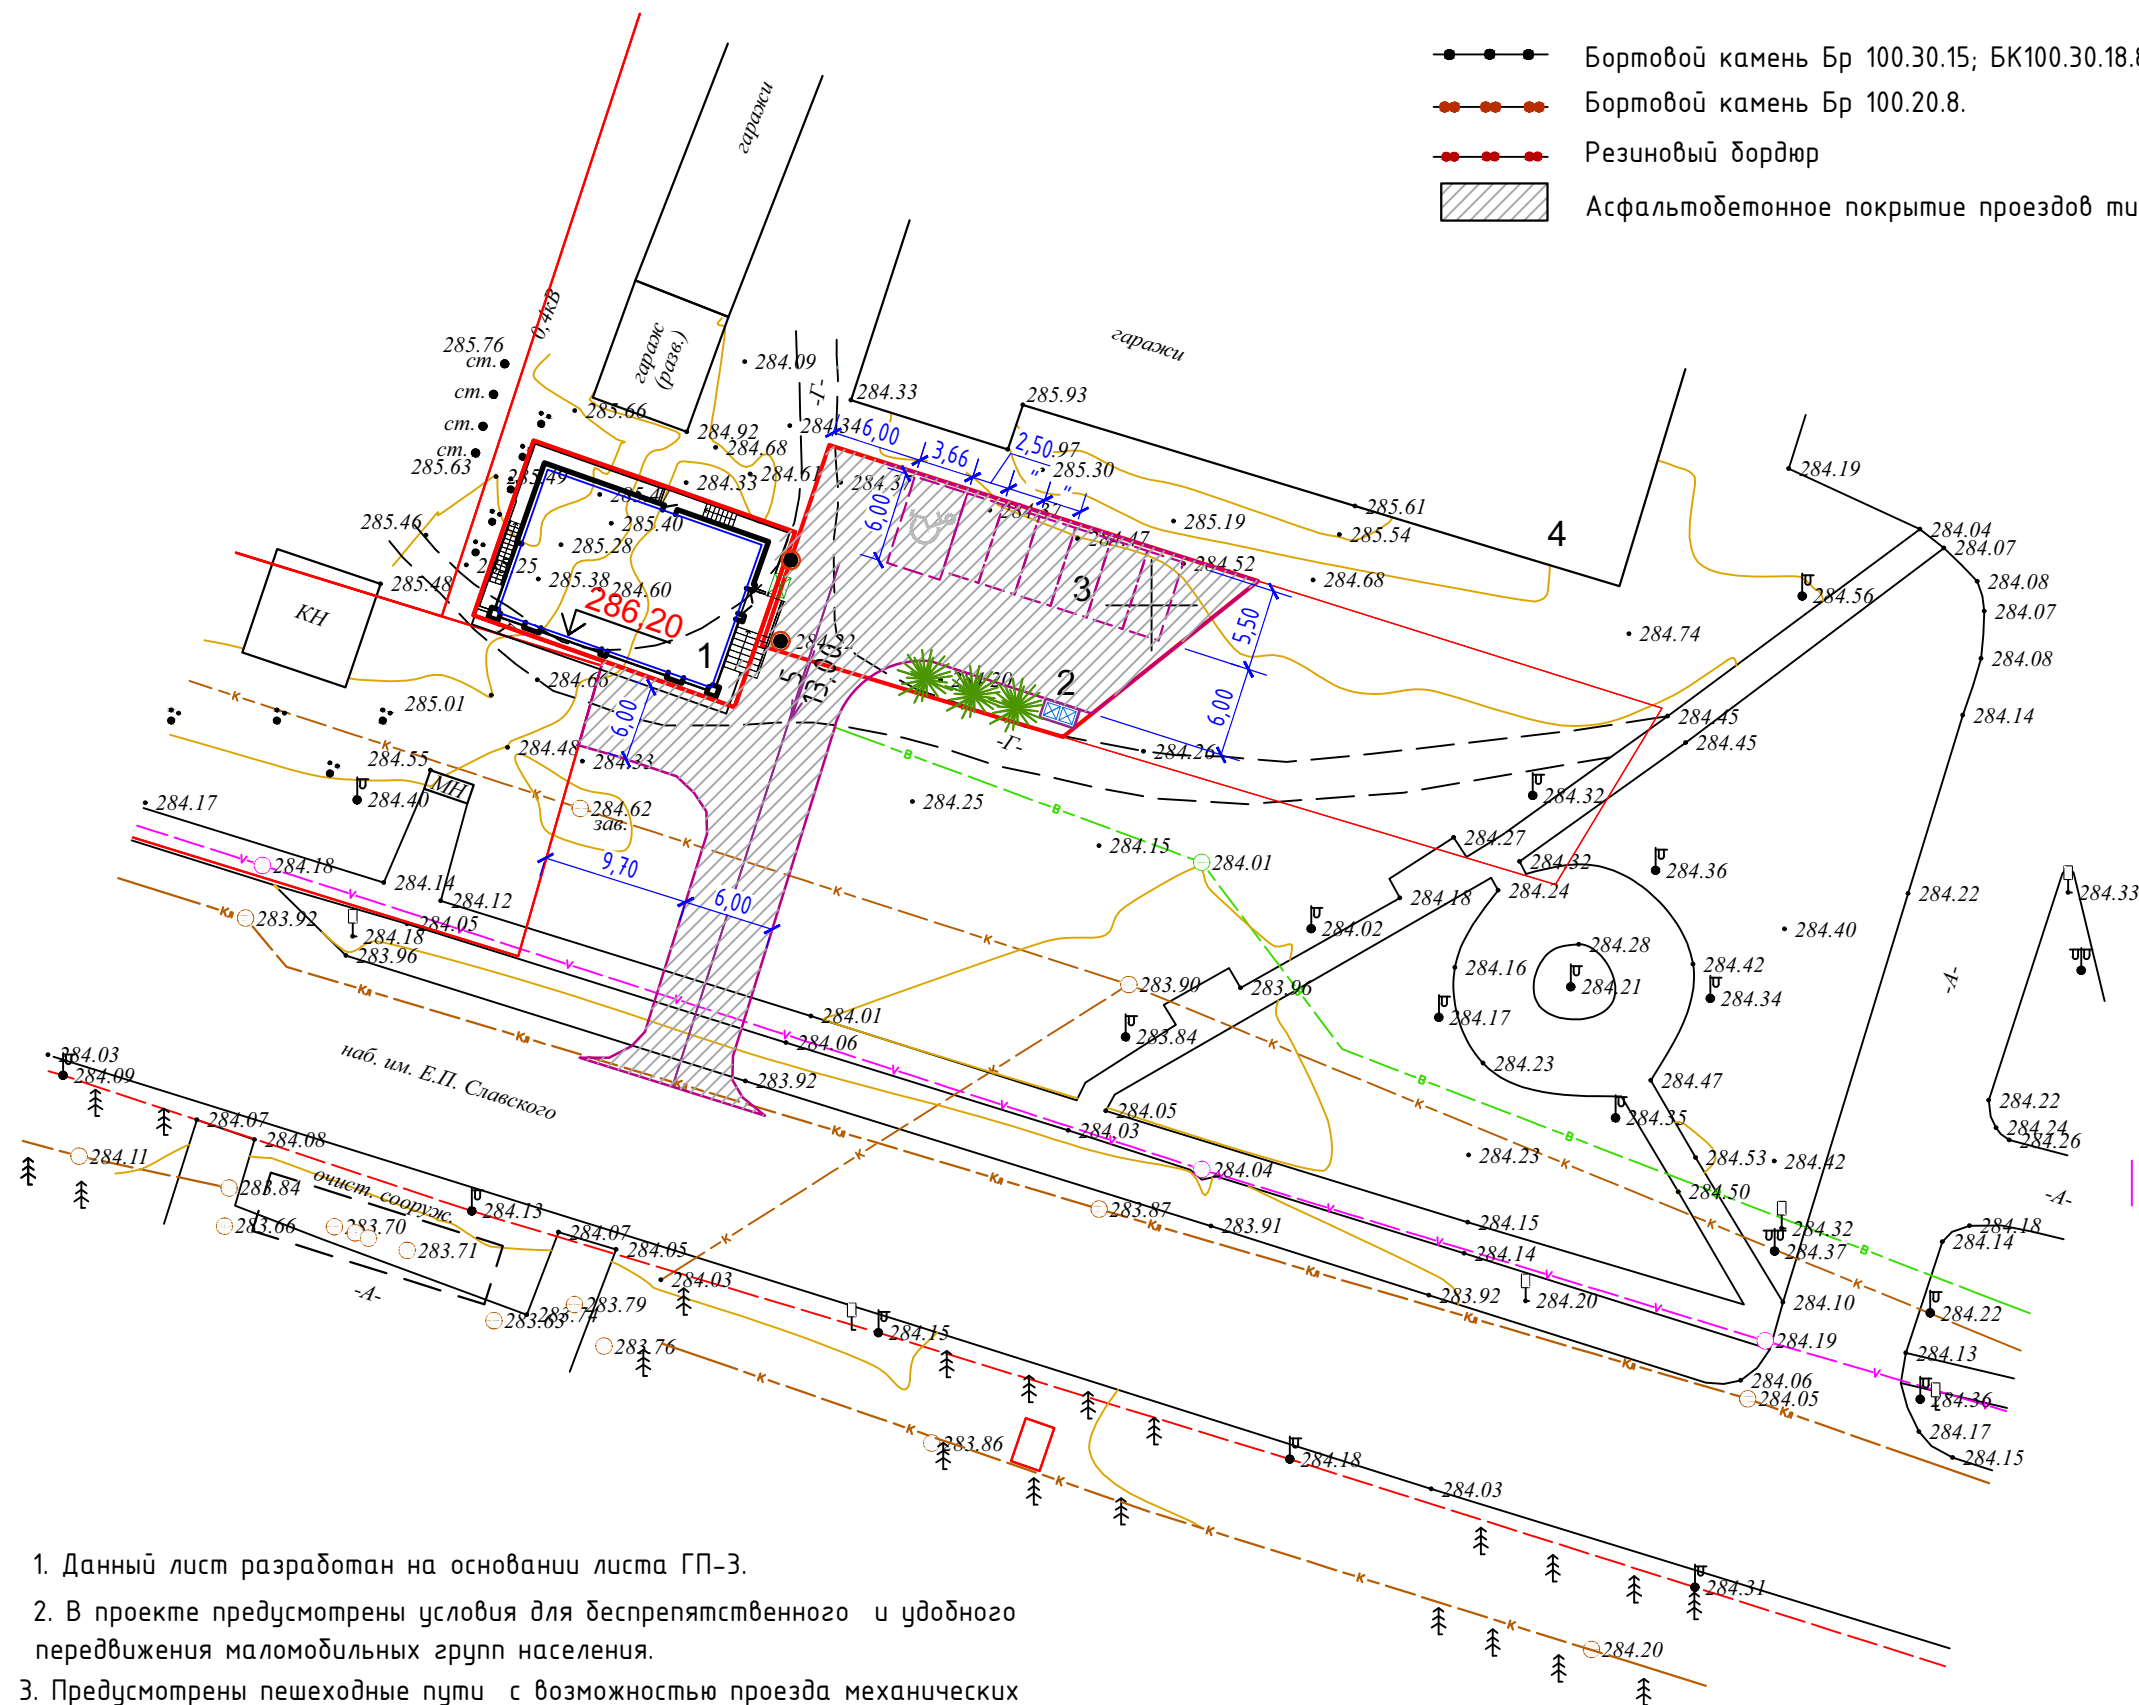

1. Данный лист разработан на основании листа ГП-3.
2. В проекте предусмотрены условия для беспрепятственного и удобного передвижения маломобильных групп населения.
3. Предусмотрены пешеходные пути с возможностью проезда механических инвалидных колясок(1,50м). Высота вертикальных препятствий (бортовые камни, поребрики в местах пересечения тротуаров с проезжей частью) на пути следования не превышают 2см. Уклоны в пределах 4...6 промилле, поручней не требуется.
4. *Посадку деревьев выполнять с добавлением*
плодородной почвы до 100% объема лунки, травосеяние с подготовкой почвы и замены грунта на растительную землю до 20 см.
5. В скобке даны объемы по прилегающей территории.

Поз.	Условн. изобр.	Наименование	Тип	Количество	Примечание
1		Асфальтобетонное покрытие проездов, м2 с бортовым камнем: Бр100.30.15 L= 51 (55),мм. БК100.30.18.8 L=6 (57),мм.	1	323 (291)	в скобках даны объемы по прилегающей территории

Поз.	Условн. изобр.	Наименование породы и вида насаждений	Возраст, лет	Количество шт.	Примечание
1		Тополь пирамидальный	3-5	3	Саженцы (1,0х1,0х0,8)
2		Газон , м2	-	25	семена многолетних трав (40г./м.2)

N п/п	Обозначение	Наименование	Количество, шт.	Примечание
●	8601-0303-0204	Чрна Сатурн	2	УСН РК 8.02-03-2024

ТИП-1

Бордюрный камень
БР-15.30.100

Засыпка пазух
грунтом

Бетон В15

150

120

50

300

200

350

150

Мелкозернистый асфальтобетон
СТ РК 1225-2013, тип Б, марка II, $H=0.04\text{ м}$;
Подгрунтовка битумом с расходом $0,2\text{ л/м}^2$;

Крупнозернистый асфальтобетон
СТ РК 1225-2013, тип Б, марка II, $H=0.06\text{ м}$;
Подгрунтовка битумом с расходом $0,7\text{ л/м}^2$;

Щебень по ГОСТ 8267-93* фракции 20-40, марка 600, $H=0,1\text{ м}$;
Уплотненный грунт К упл.=0.95

							АР		
							Строительство двухэтажного административного здания с подвалом и открытой террасой, расположенного на земельном участке по адресу РК, г.Усть-Каменогорск, набережная им.Е.П.Славского, гараж №40Г		
Изм.	Кол.уч.	Лист	№ док.	Подпись	дата		Стадия	Лист	Листов
	ГИП	Косолапова В.А.				Административное здание	П	6	18
	Архитектор								
						План благоустройства территории М1:500	ООО "СемСтройтехснаб" Государственная лицензия ГСЛ №18016321		

Общие данные:

Раздел наружные сети водоснабжения и канализации проекта выполнен на основании: задания на проектирование и технических условий. В соответствии с главами СНиП РК 4.01-02-2009, СН РК 4.01-03-2011, СП РК 4.01-103-2013, СН РК 4.01-05-2002, СП РК 3.01-101-2013.

Запроектированы следующие системы водопровода и канализации:

- бытовая канализация;
- хозяйственно-питьевой водопровод.

Климатические природные условия характеризуются следующими показателями:

- расчетная температура воздуха наиболее холодной пятидневки - 37.3° С;
- сейсмичность района строительства - 7 баллов;

Примечания:

1.Пересечение проектируемых сетей с подземными коммуникациями, дорогами производить по СН РК 5.01-01-2013.

2.Перед началом производства работ уточнить все подземные кабели и коммуникации.

3.Производство работ вести согласно СП РК 4.01-103-2013.

4. Перед началом производства работ уточнить отметки в местах подключений и пересечений, материал существующих коммуникаций, их назначение.

5.При пересечении проектируемых трубопроводов с действующими подземными коммуникациями земляные работы производить вручную по 2 м от боковых стенок траншеи и до 1 м над верхом трубы.

6.Обратную засыпку под дорогами производить песчаным грунтом с послойным уплотнением на всю глубину траншеи до низа дорожной одежды.

7.При производстве земляных работ для труб предусмотреть песчаное основание толщиной 10 см, при обратной засыпке предусмотреть подсыпку мягким местным грунтом толщиной 30 см над верхом трубы, согласно СН РК 4.01-05-2002, п.9.10.2, п.9.10.4.

8.Гидроизоляция. Поверхности ж/б конструкций, соприкасающихся с грунтом, обмазать горячим битумом в 2 слоя, по битуму оклейка наплавляемым рулонным материалом техноэласт.




Настоящий проект выполнен в соответствии с экологическими, санитарно-гигиеническими, противопожарными требованиями и другими нормами и правилами и обеспечивает безопасную для жизни и здоровья людей эксплуатацию объекта при соблюдении предусмотренных рабочими чертежами мероприятий.
Главный инженер проекта _____ Косолапова В.А.




						АР			
						Строительство двухэтажного административного здания с подвалом и открытой террасой, расположенного на земельном участке по адресу РК, г.Усть-Каменогорск, набережная им.Е.П.Славского, гараж №40Г			
Изм.	Кол.уч.	Лист	№ док.	Подпись	дата	Административное здание	Стадия	Лист	Листов
ГИП		Косолапова В.А.					П	7	18
Архитектор									
						Общие данные.Сети В1 и К1.	ТОО "СемСтройтехснаб"		
							Государственная лицензия ГСЛ №18016321		

Экспликация помещений

Номер помеще-ния	Наименование	Площадь, м ²	Кат помеще-ния
21	Комерческое помещение	108,71	
22	Санузел МГН	5,10	
23	Шлюз	5,49	
24	ПЧИ	4,02	
25	Санузел	1,93	
27	Санузел	1,93	
Общий итог: 6		127,18	

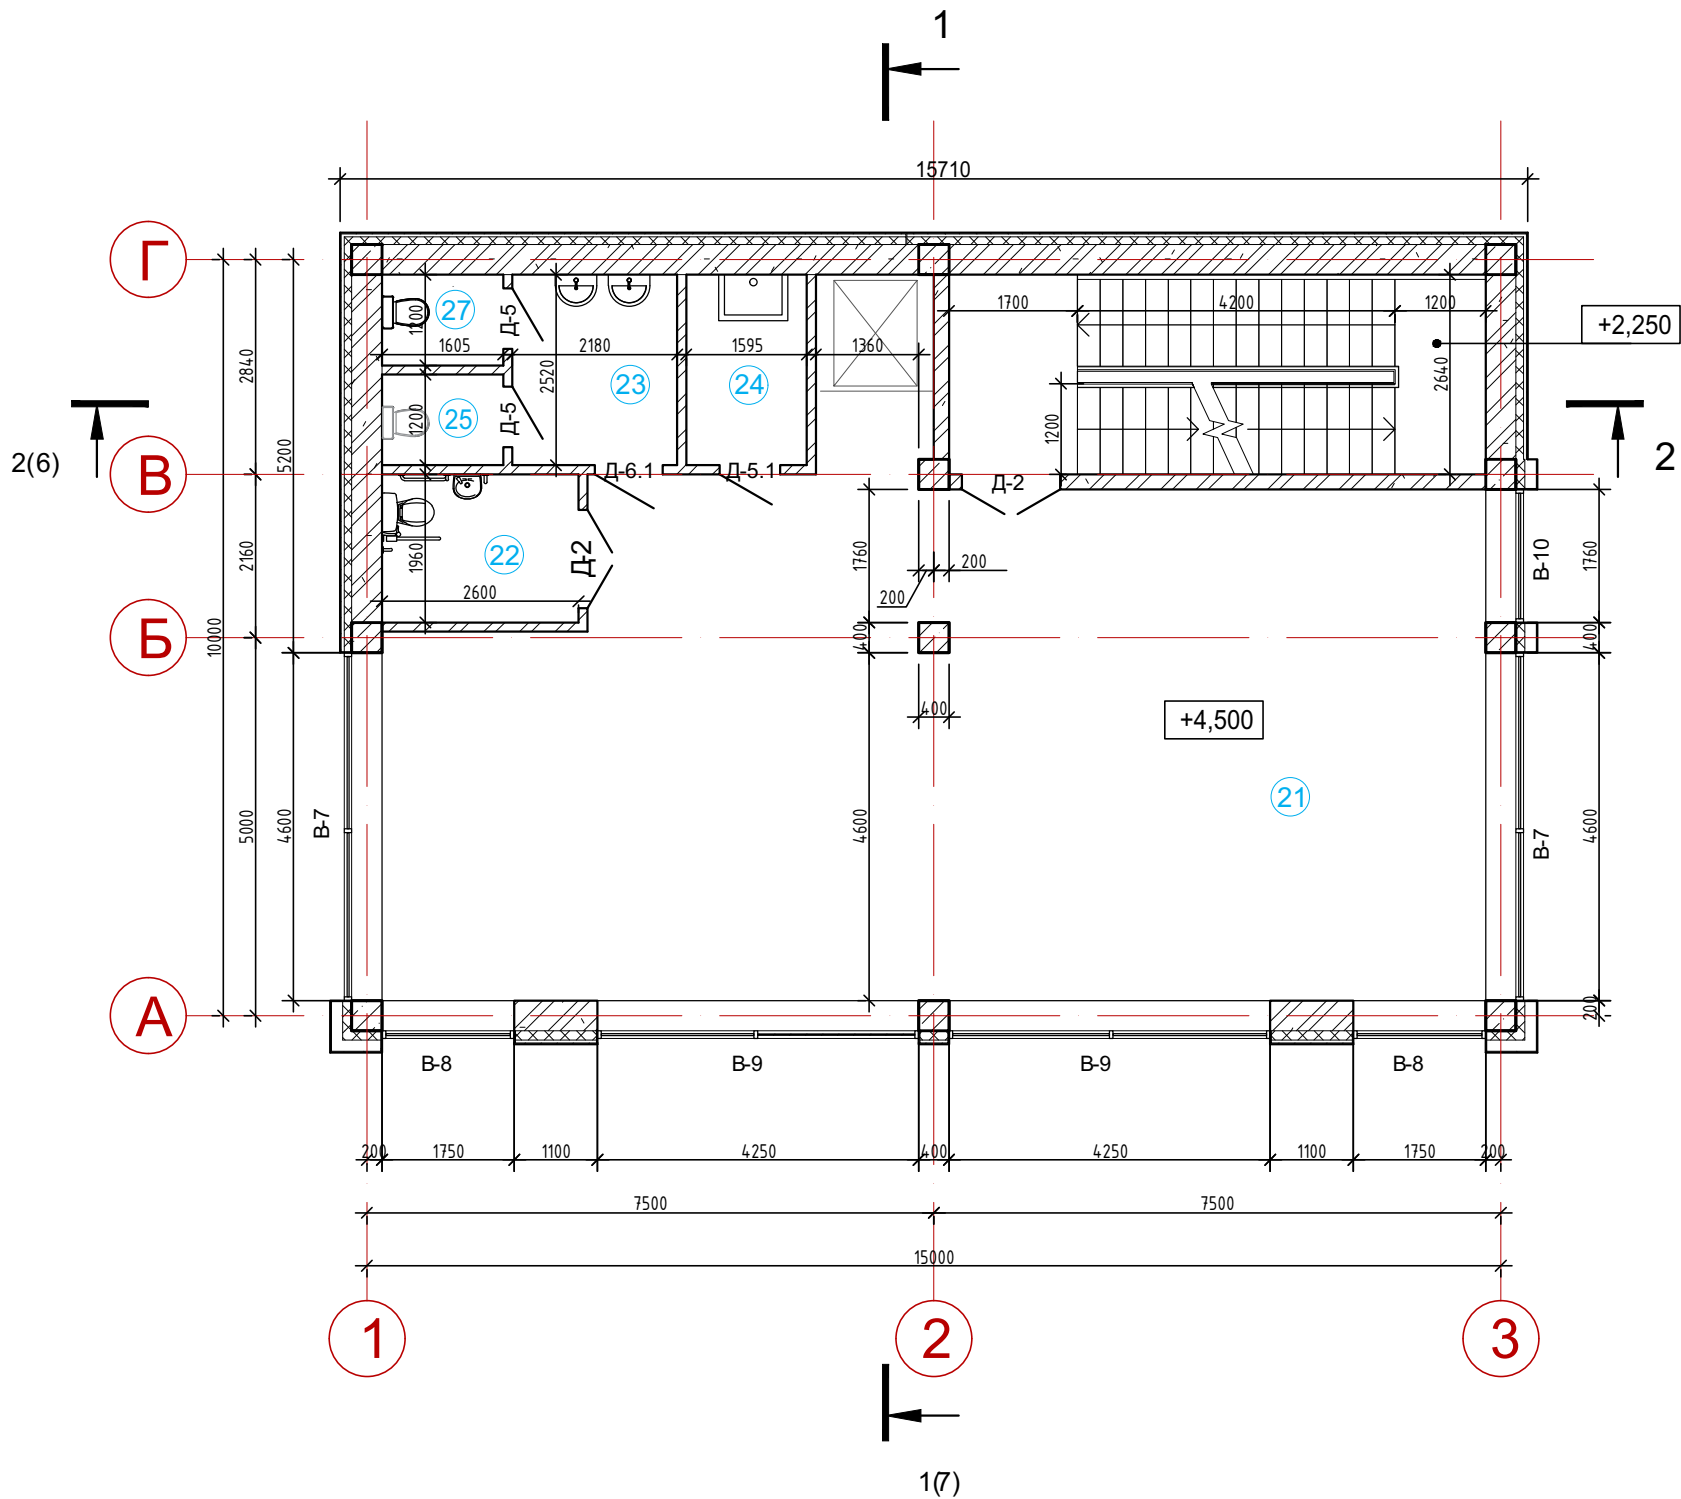

						АР			
						Строительство двухэтажного административного здания с подвалом и открытой террасой, расположенного на земельном участке по адресу РК, г.Усть-Каменогорск, набережная им.Е.П.Славского, гараж №40Г			
Изм.	Кол.уч.	Лист	№ док.	Подпись	дата	Административное здание	Стадия	Лист	Листов
ГИП		Косолапова В.А.					П	8	18
Архитектор						План подвального этажа на отм. -4,500	ООО "СемСтройтехснаб" Государственная лицензия ГСЛ №18016321		

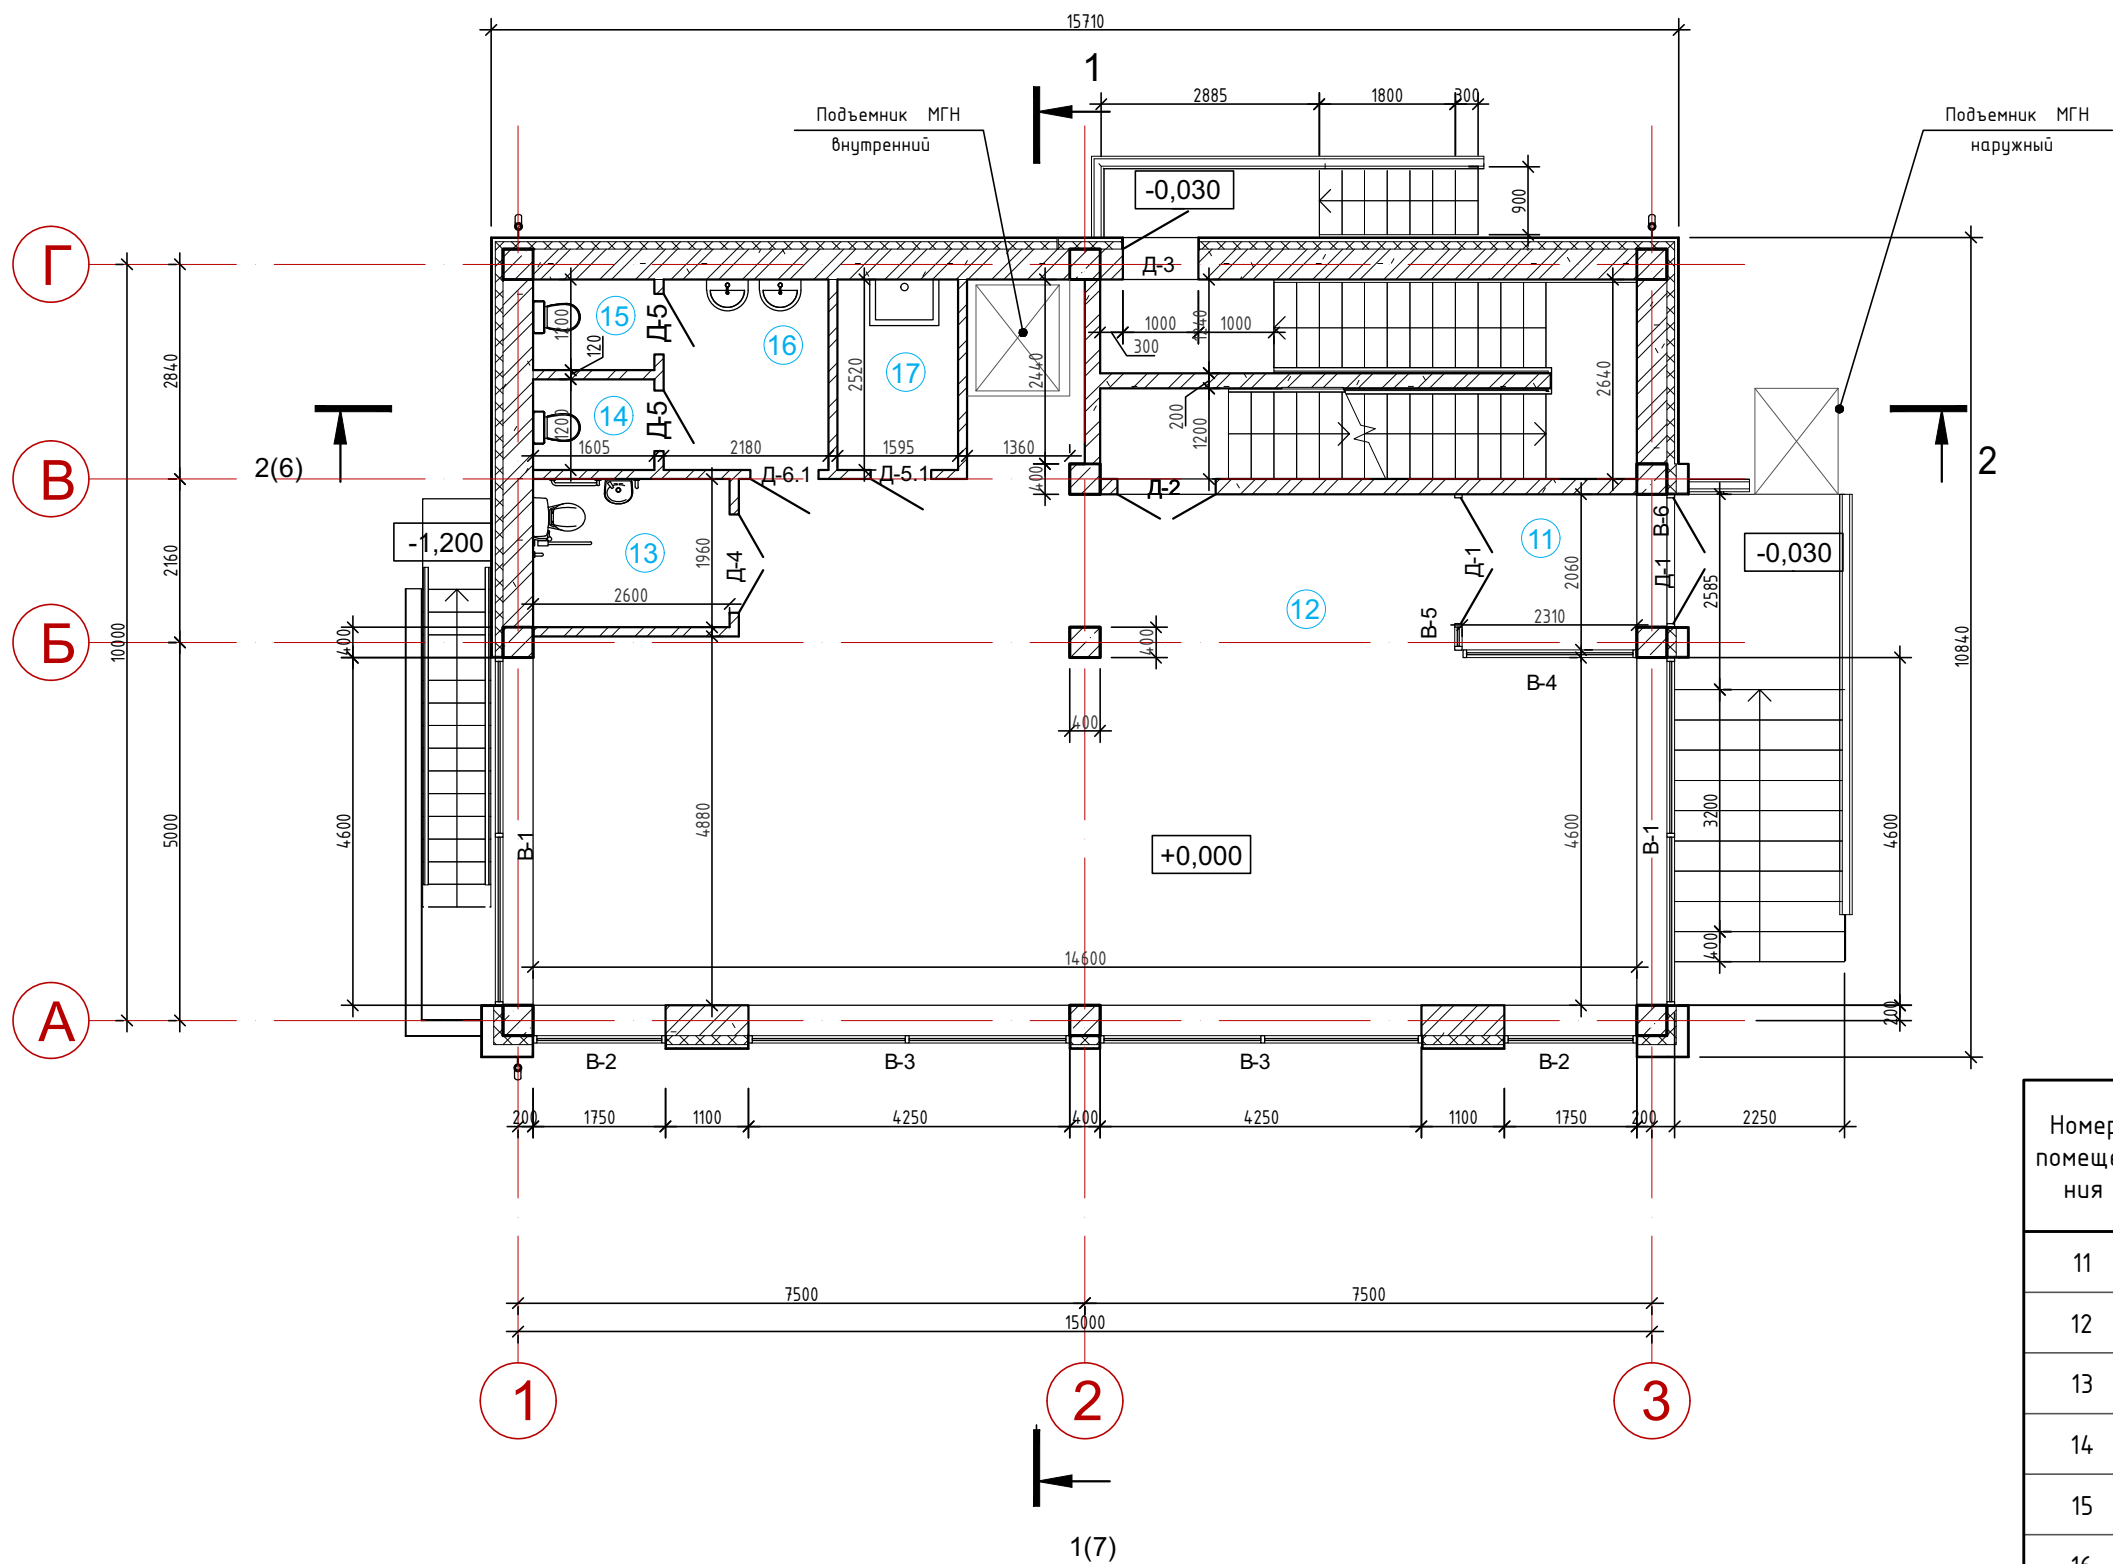


Экспликация помещений

Номер помеще-ния	Наименование	Площадь, м²	Кат помеще-ния
11	Тамбур	5,77	
12	Комерческое помещение	102,94	
13	Санузел МНГ	5,10	
14	Санузел	1,93	
15	Санузел	1,93	
16	Шлюз	5,49	
17	ПУИ	4,02	
Общий итог 7		127,18	


						АР			
						Строительство двухэтажного административного здания с подвалом и открытой террасой, расположенного на земельном участке по адресу РК, г.Усть-Каменогорск, набережная им.Е.П.Славского, гараж №40Г			
Изм.	Кол.уч.	Лист	№ док.	Подпись	дата	Административное здание	Стадия	Лист	Листов
ГИП		Косолапова В.А.					П	9	18
Архитектор						План 1-го этажа на отм. ±0,000	ООО "СемСтройтехснаб" Государственная лицензия ГСЛ №18016321		

Экспликация помещений

Номер помеще-ния	Наименование	Площадь, м²	Кат. помеще-ния
01	Тамбур	3,55	
02	Санузел	2,50	
03	ПУИ	4,34	
04	Санузел	2,14	
05	Шлюз	5,94	
06	Коммерческое помещение	101,74	
07	Лестничная клетка	19,46	
08	Техническое помещение	3,53	
Общий итог 8		143,20	

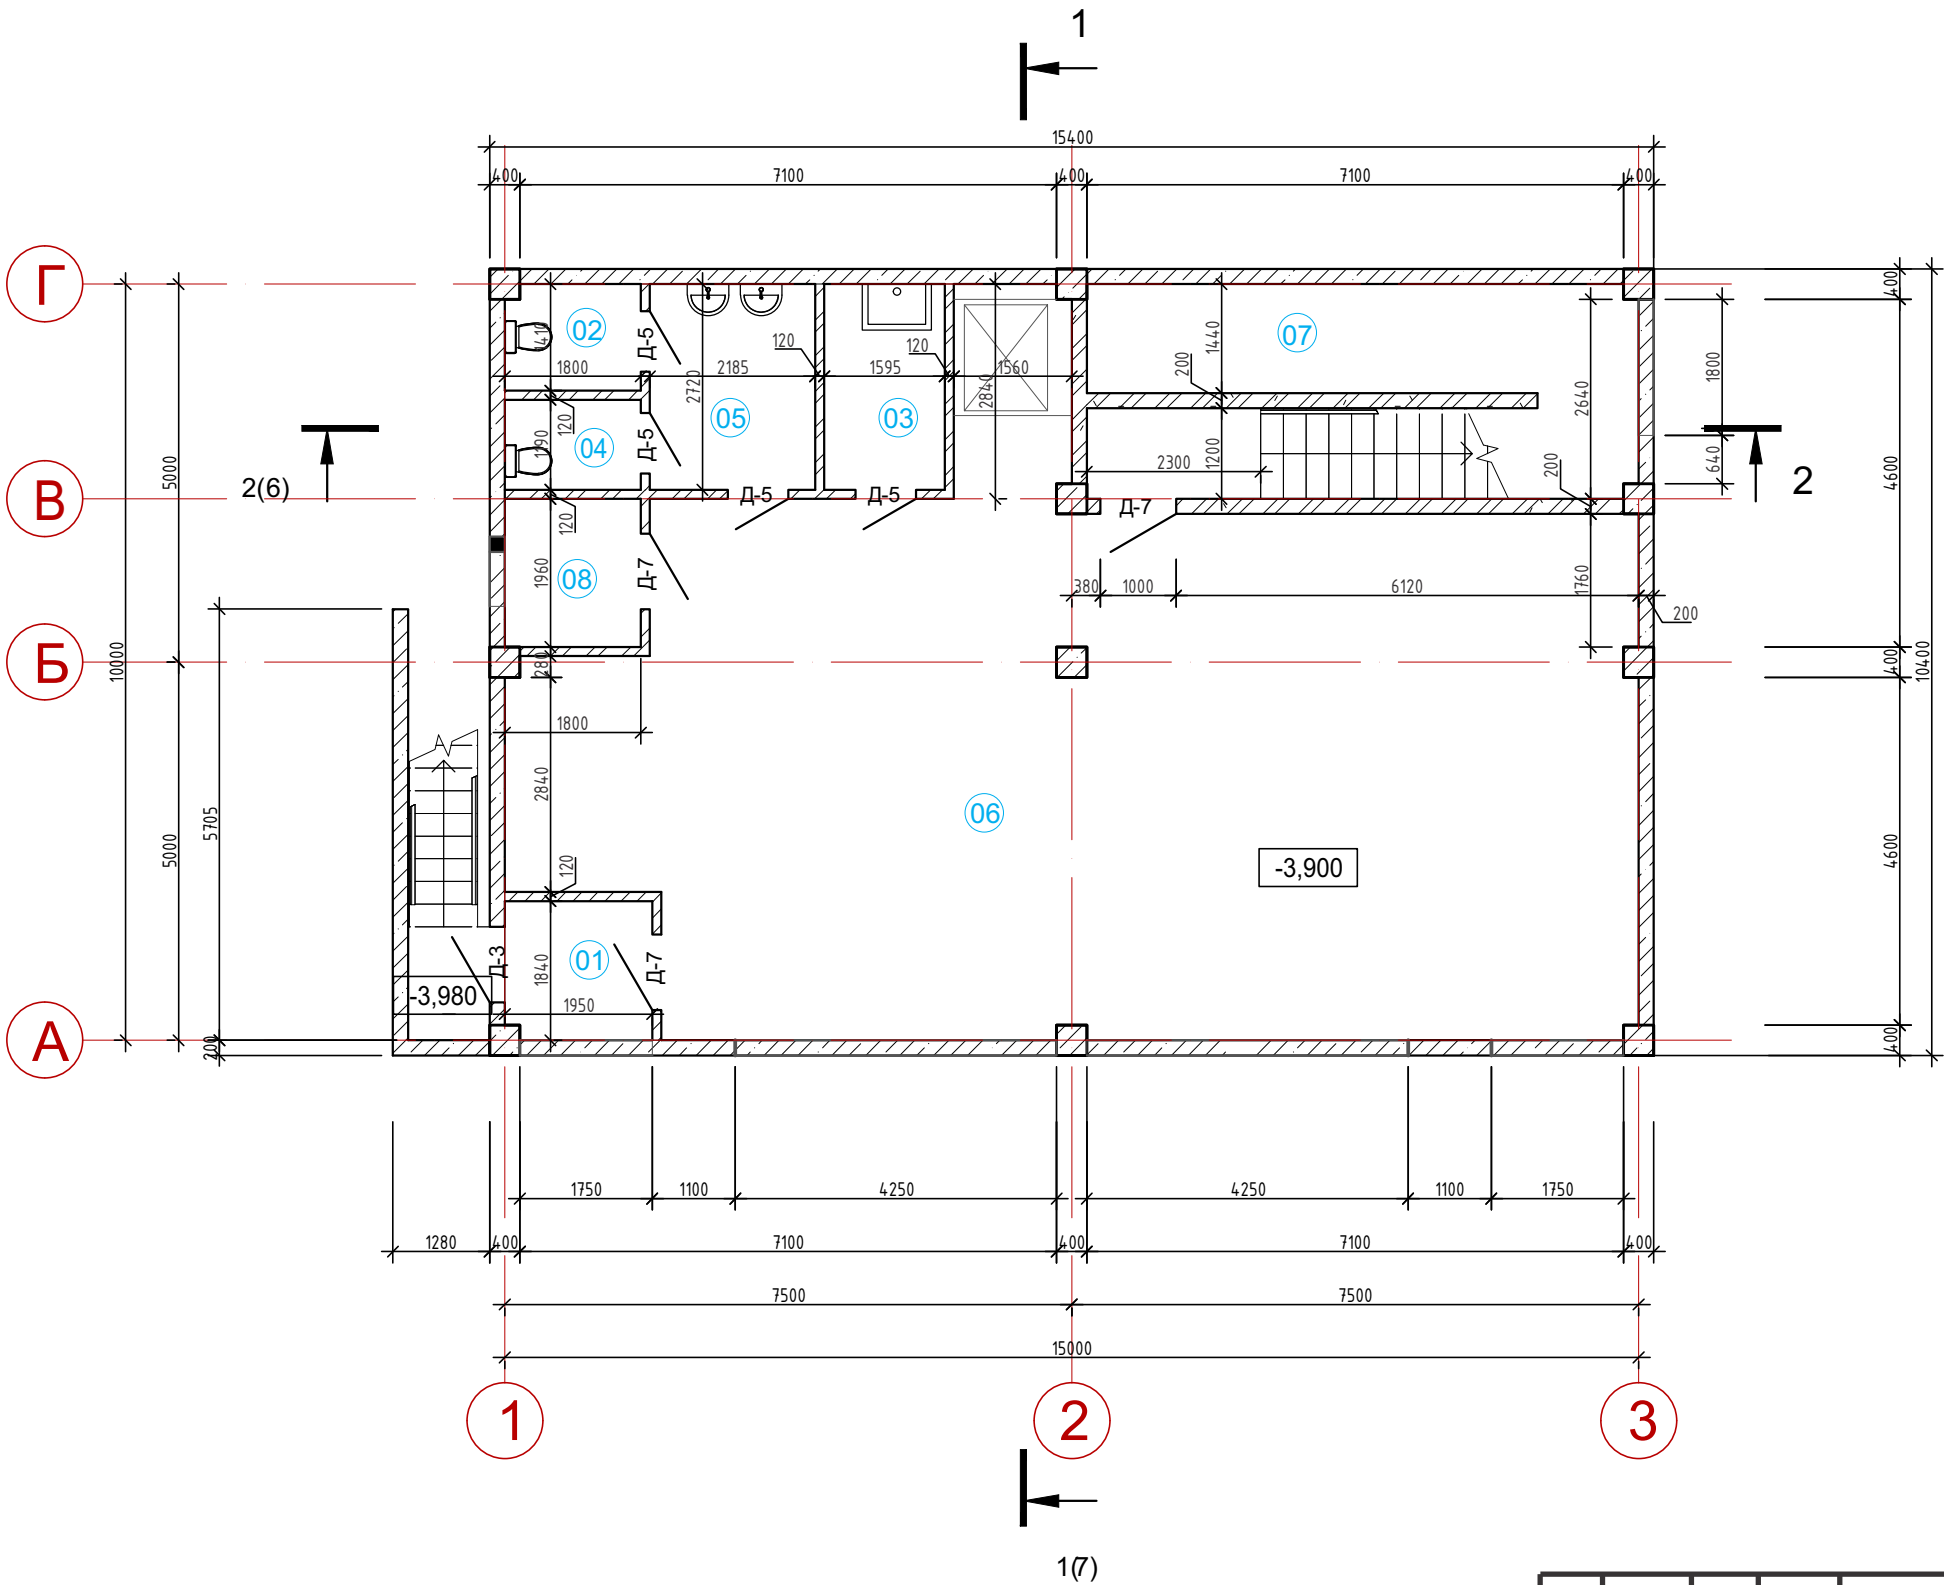


						АР			
						Строительство двухэтажного административного здания с подвалом и открытой террасой, расположенного на земельном участке по адресу РК, г.Усть-Каменогорск, набережная им.Е.П.Славского, гараж №40Г			
Изм.	Кол.уч.	Лист	№ док.	Подпись	дата	Административное здание	Стадия	Лист	Листов
ГИП		Косолапова В.А.					П	10	18
Архитектор						План 2-го этажа на отм. +3,900	ООО "СемСтройтехснаб" Государственная лицензия ГСЛ №18016321		

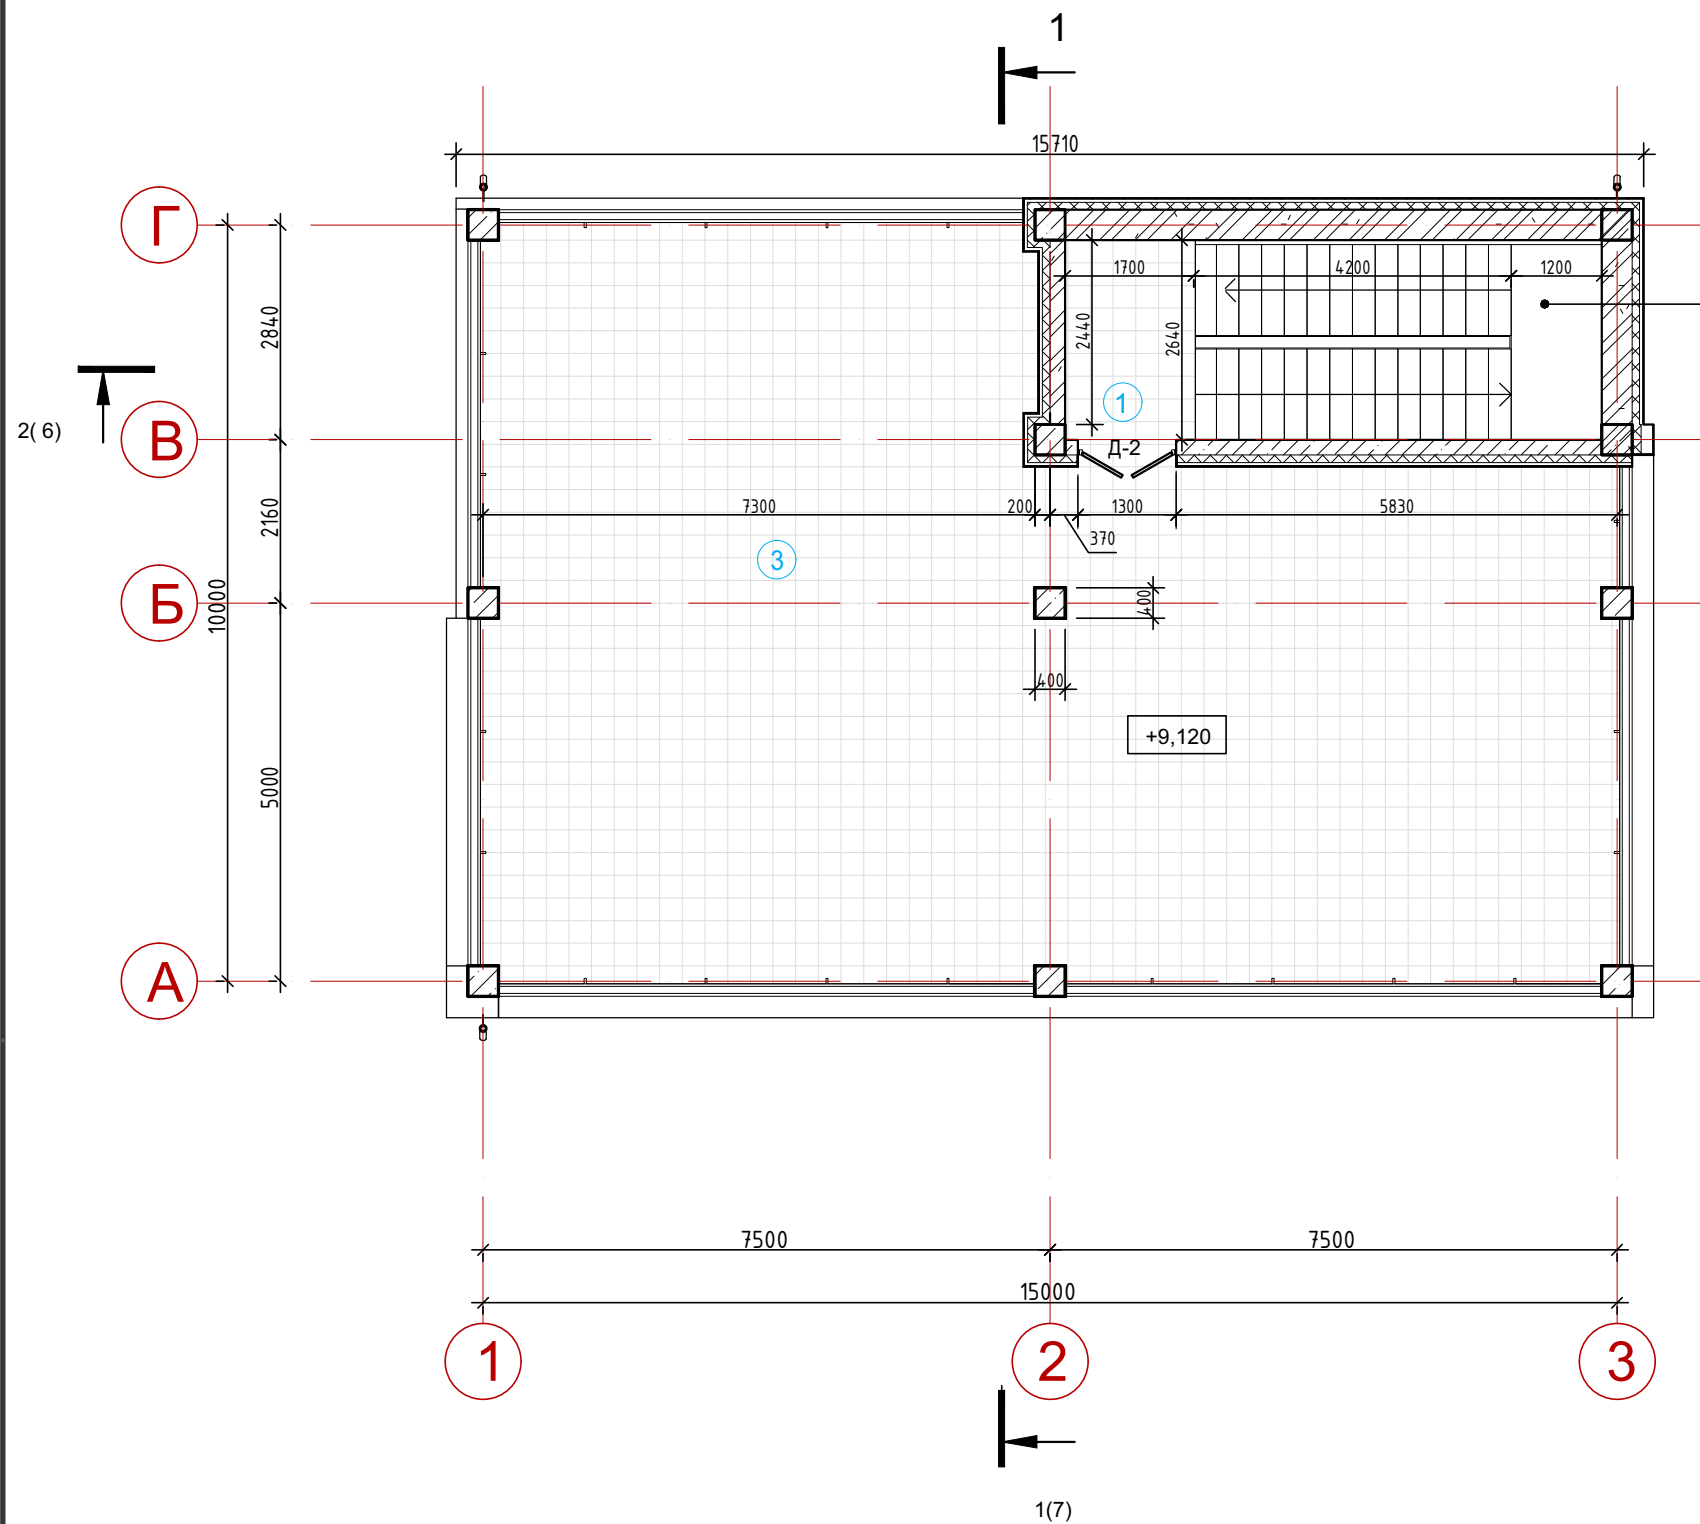


Экспликация кровли		
Тип кровли по проекту	Элементы кровли и их толщина (S) в мм.	Площадь, м²
1	1. Металлочерепица 2. Контрорешетка 50х50мм 3. Обрешетка 50х50 мм 4. Гидрозащитная паропроницаемая мембрана "Изоспан АМ" 5. Стропило 75х200мм	235,87
2 чердак	1. Гидрозащитная паропроницаемая мембрана "Изоспан АМ", (СТ 5774-003-18603495-2004, изм. №1) насухо 2. Эффективный утеплитель , группы НГ из минераловатных плит "Izoterm П150" (СТ ТОО 30405390-01-2008 с изм. 1,2) -200 мм 3. Пароизоляция - полиэтиленовая стабилизированная пленка марки Тс , типа "Тайвек " (ГОСТ 10354-82 (1 слой)) наклеенная на битумно -кукресольной мастике (насухо) -200 мкм 4. Грунтовка в один слой раствором битума марки БН 90/10 в керосине в соотношении 1:3 5. Затирка выравнивающая из цементно -песчаного раствора марки 50 -5 мм 6. Железобетонная плита покрытия -200 мм	24,96
3 терраса	1. Тротуарная плитка на регулируемых опорах -100 мм 2. Излопробивной геотекстиль ТехноНИКОЛЬ 300 г/ м2 3. Кровельная ПВХ мембрана LOGICROOF V-GR 4. Стеклохолст 100 г/ м2 5. Экструзионный пенополистирол -100 мм 6. Технобарьер 7. Железобетонная плита покрытия -200 мм	141,44


						АР			
						Строительство двухэтажного административного здания с подвалом и открытой террасой, расположенного на земельном участке по адресу РК, г.Усть-Каменогорск, набережная им.Е.П.Славского, гараж №40Г			
Изм.	Кол.уч.	Лист	№ док.	Подпись	дата	Административное здание	Стадия	Лист	Листов
ГИП		Косолапова В.А.					П	11	18
Архитектор									
						План террасы на отм. +9,120		ТОО "СемСтройтехснаб" Государственная лицензия ГСЛ №18016321	

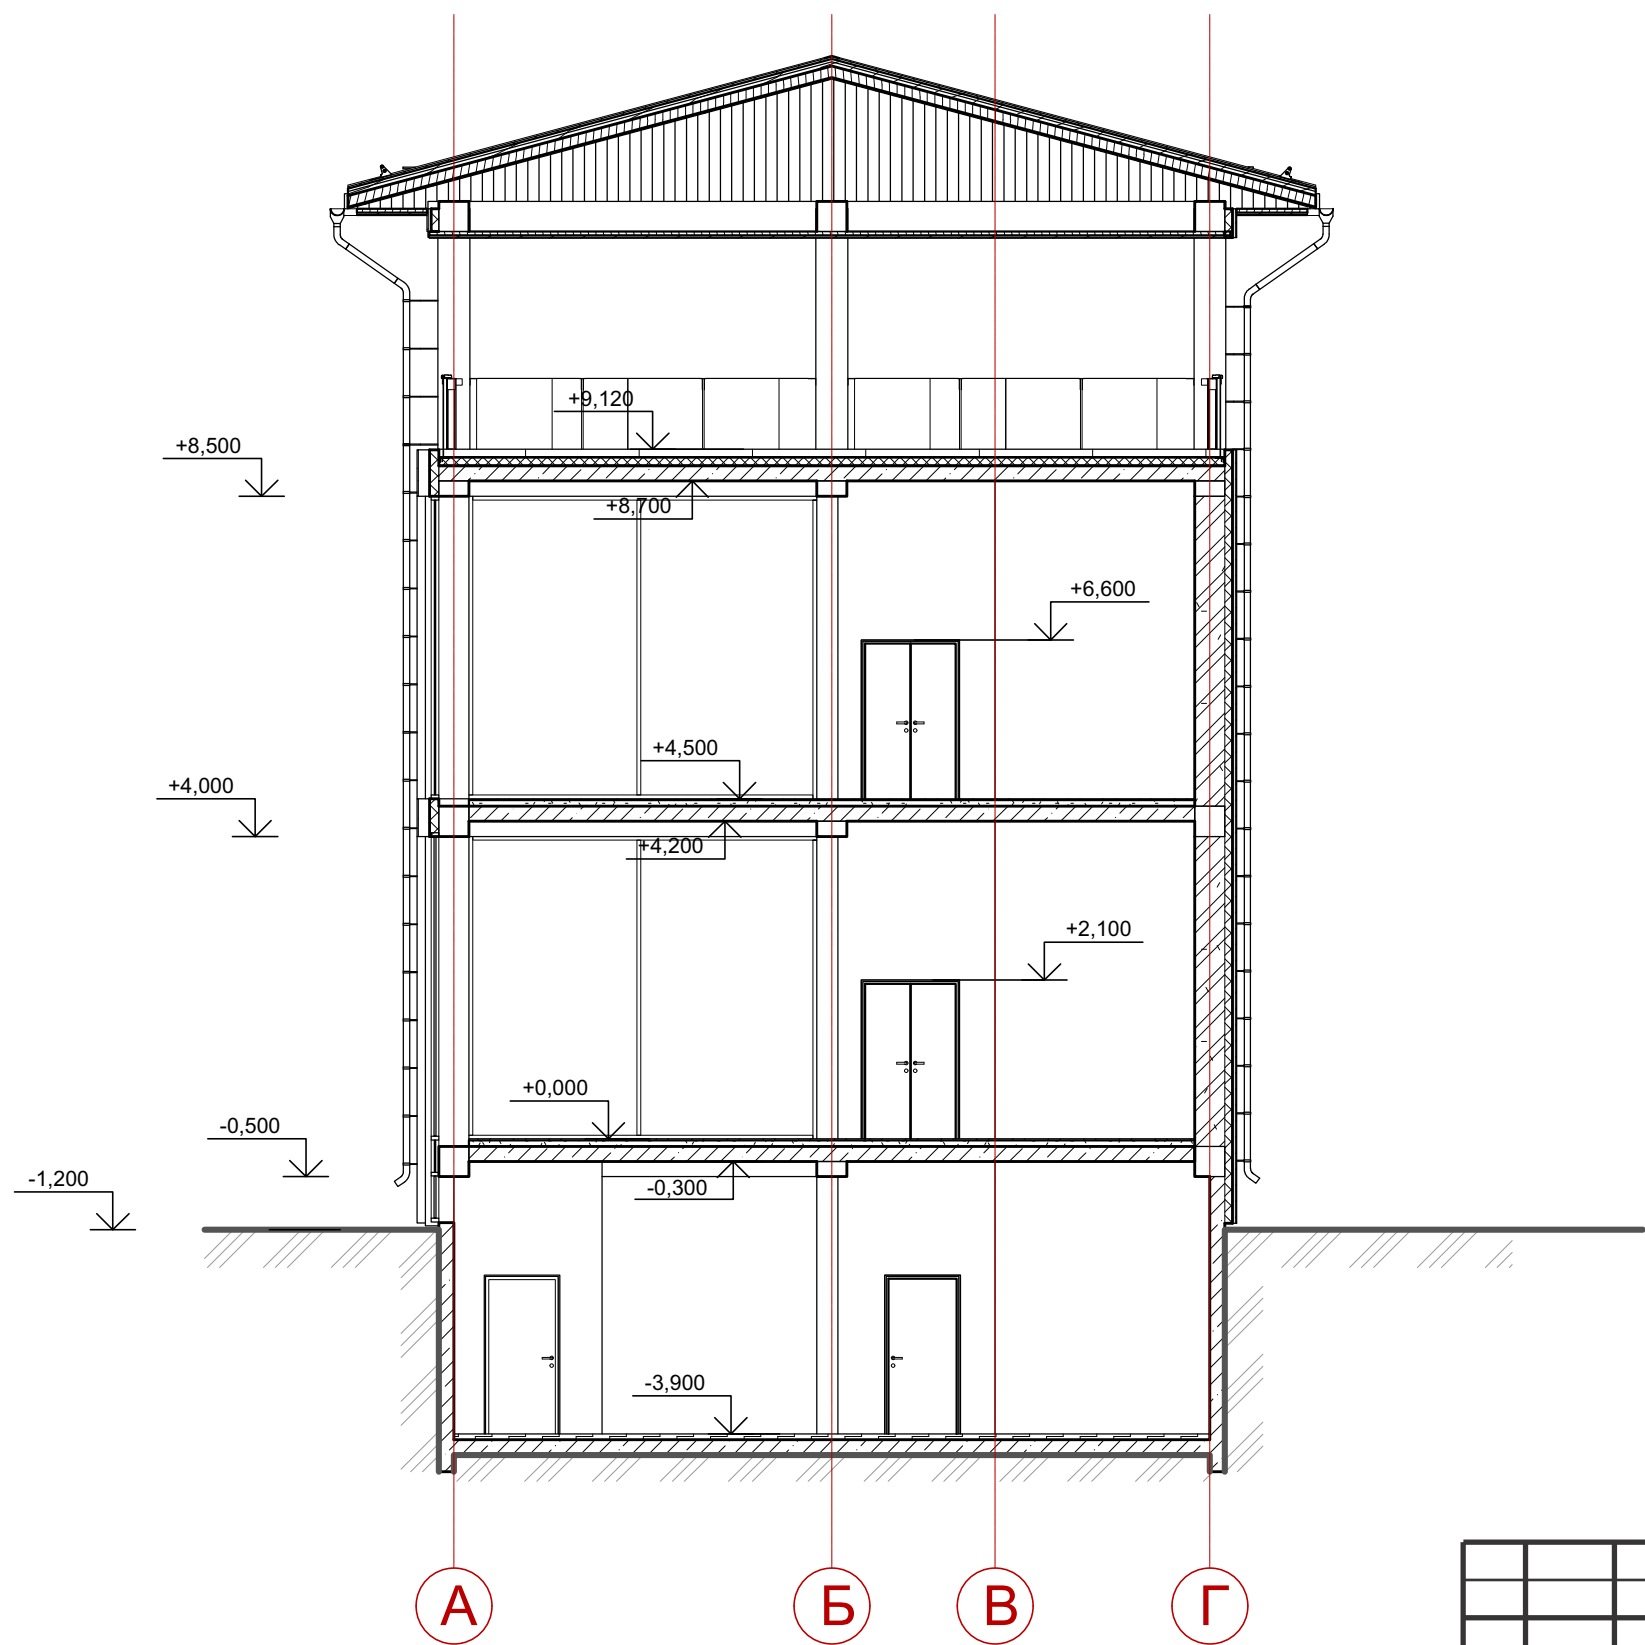

						АР			
						Строительство двухэтажного административного здания с подвалом и открытой террасой, расположенного на земельном участке по адресу РК, г.Усть-Каменогорск, набережная им.Е.П.Славского, гараж №40Г			
Изм.	Кол.уч.	Лист	№ док.	Подпись	дата	Административное здание	Стадия	Лист	Листов
ГИП		Косолапова В.А.					П	12	18
Архитектор						Разрез 1-1	ТОО "СемСтройтехснаб" Государственная лицензия ГСЛ №18016321		

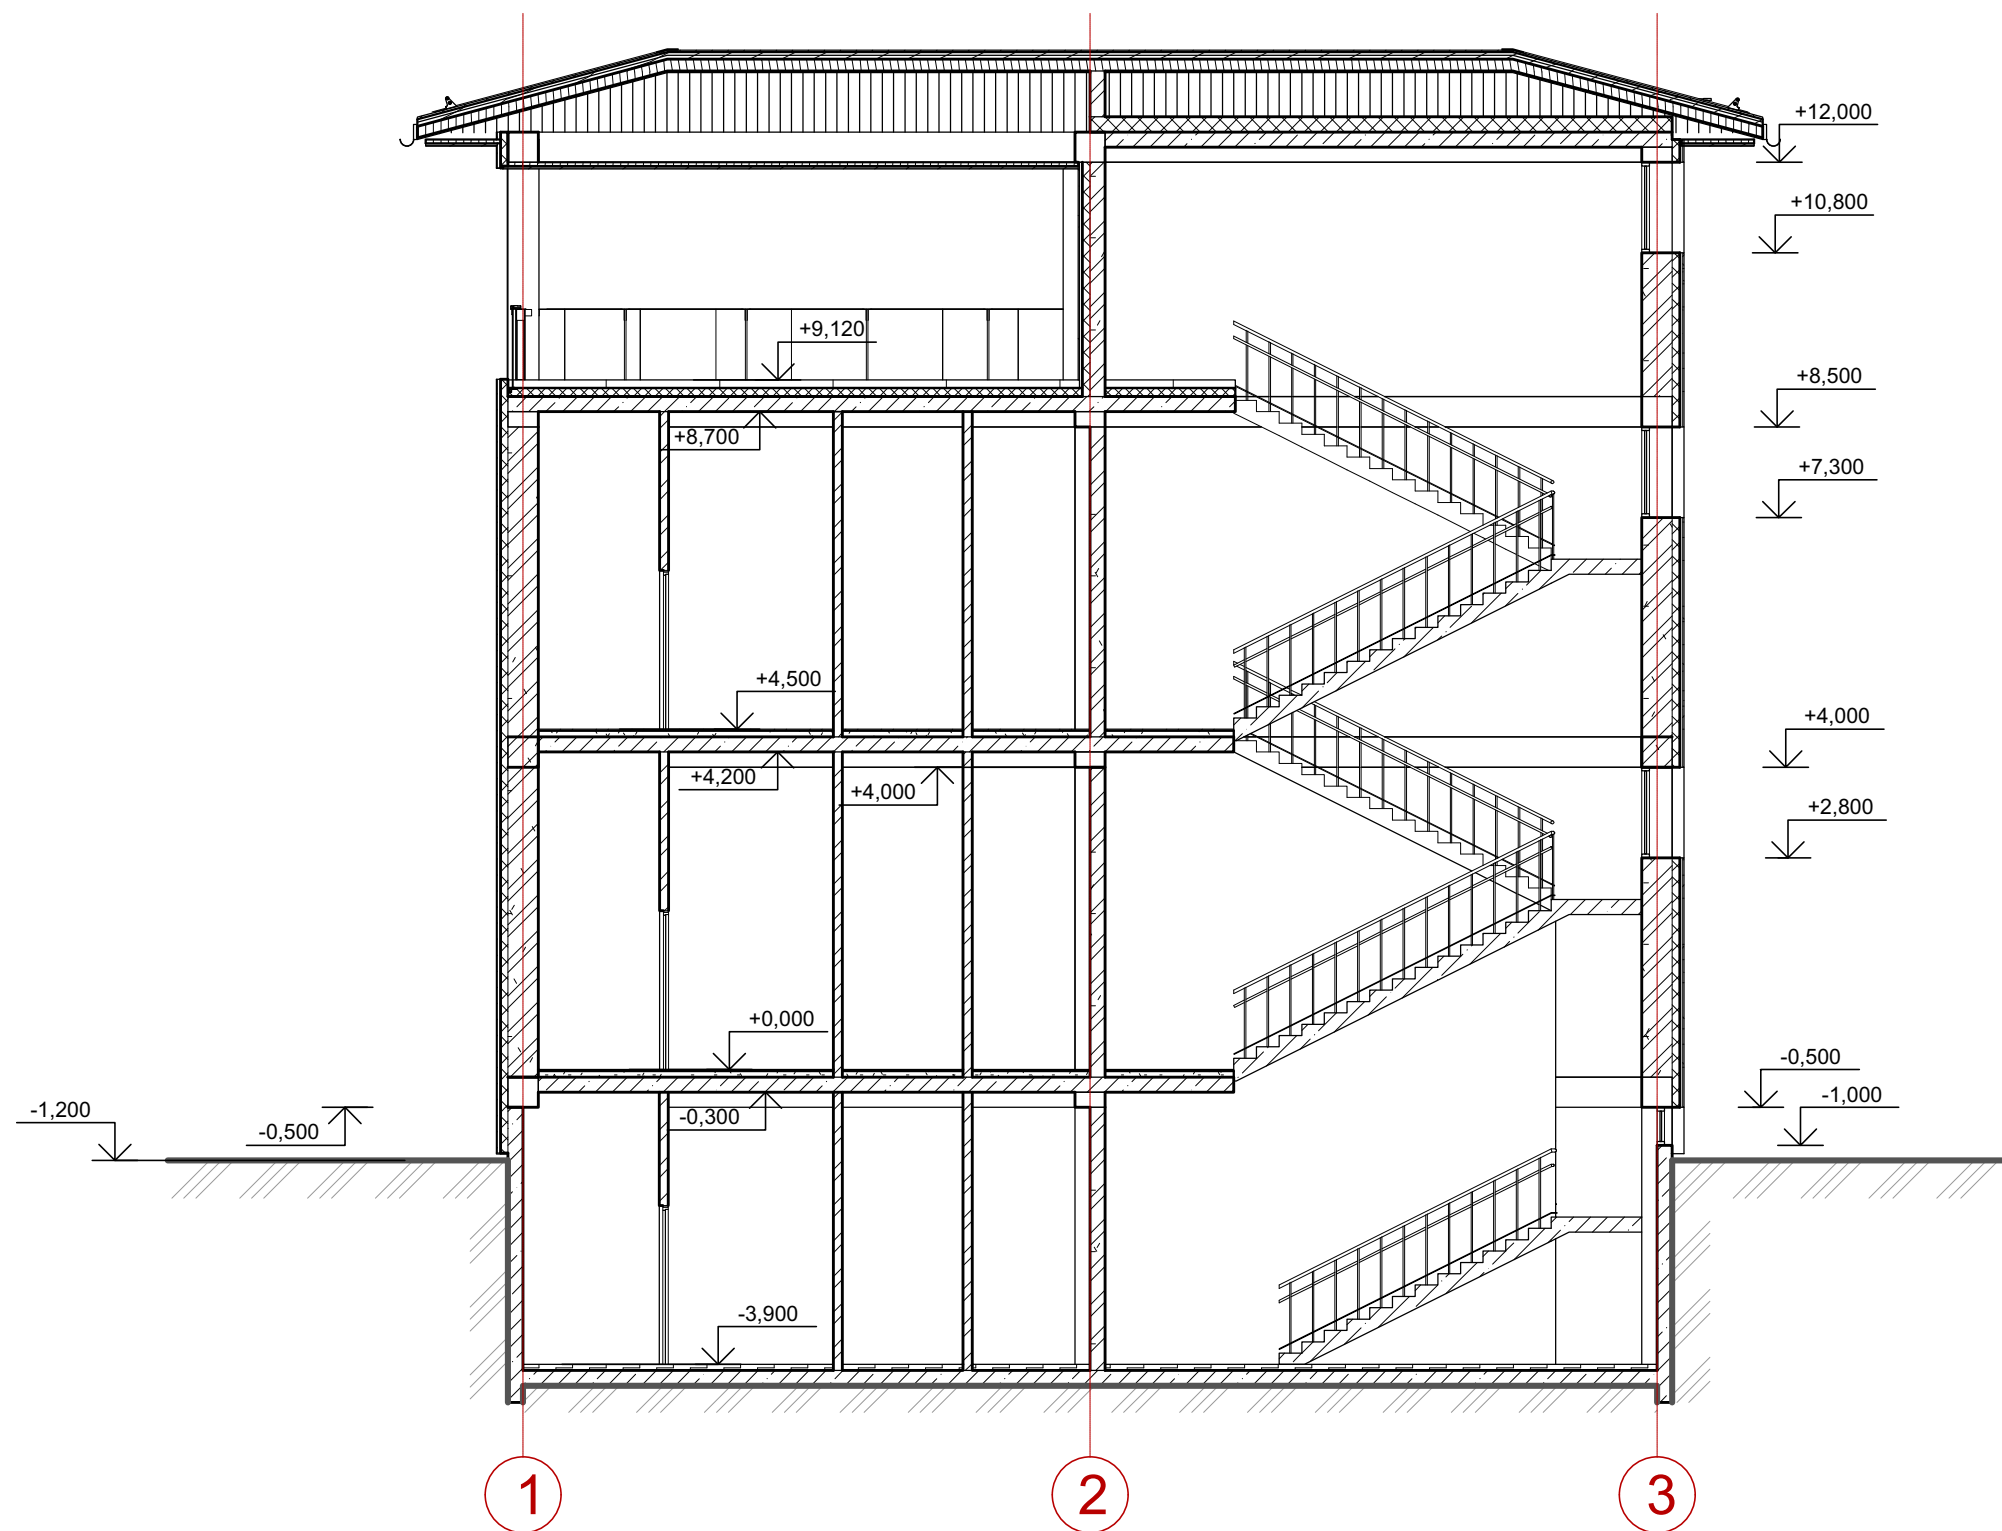


						АР			
						Строительство двухэтажного административного здания с подвалом и открытой террасой, расположенного на земельном участке по адресу РК, г.Усть-Каменогорск, набережная им.Е.П.Славского, гараж №40Г			
Изм.	Кол.уч.	Лист	№ док.	Подпись	дата	Административное здание	Стадия	Лист	Листов
ГИП		Косолапова В.А.					П	13	18
Архитектор						Разрез 2-2	ТОО "СемСтройтехснаб" Государственная лицензия ГСЛ №18016321		

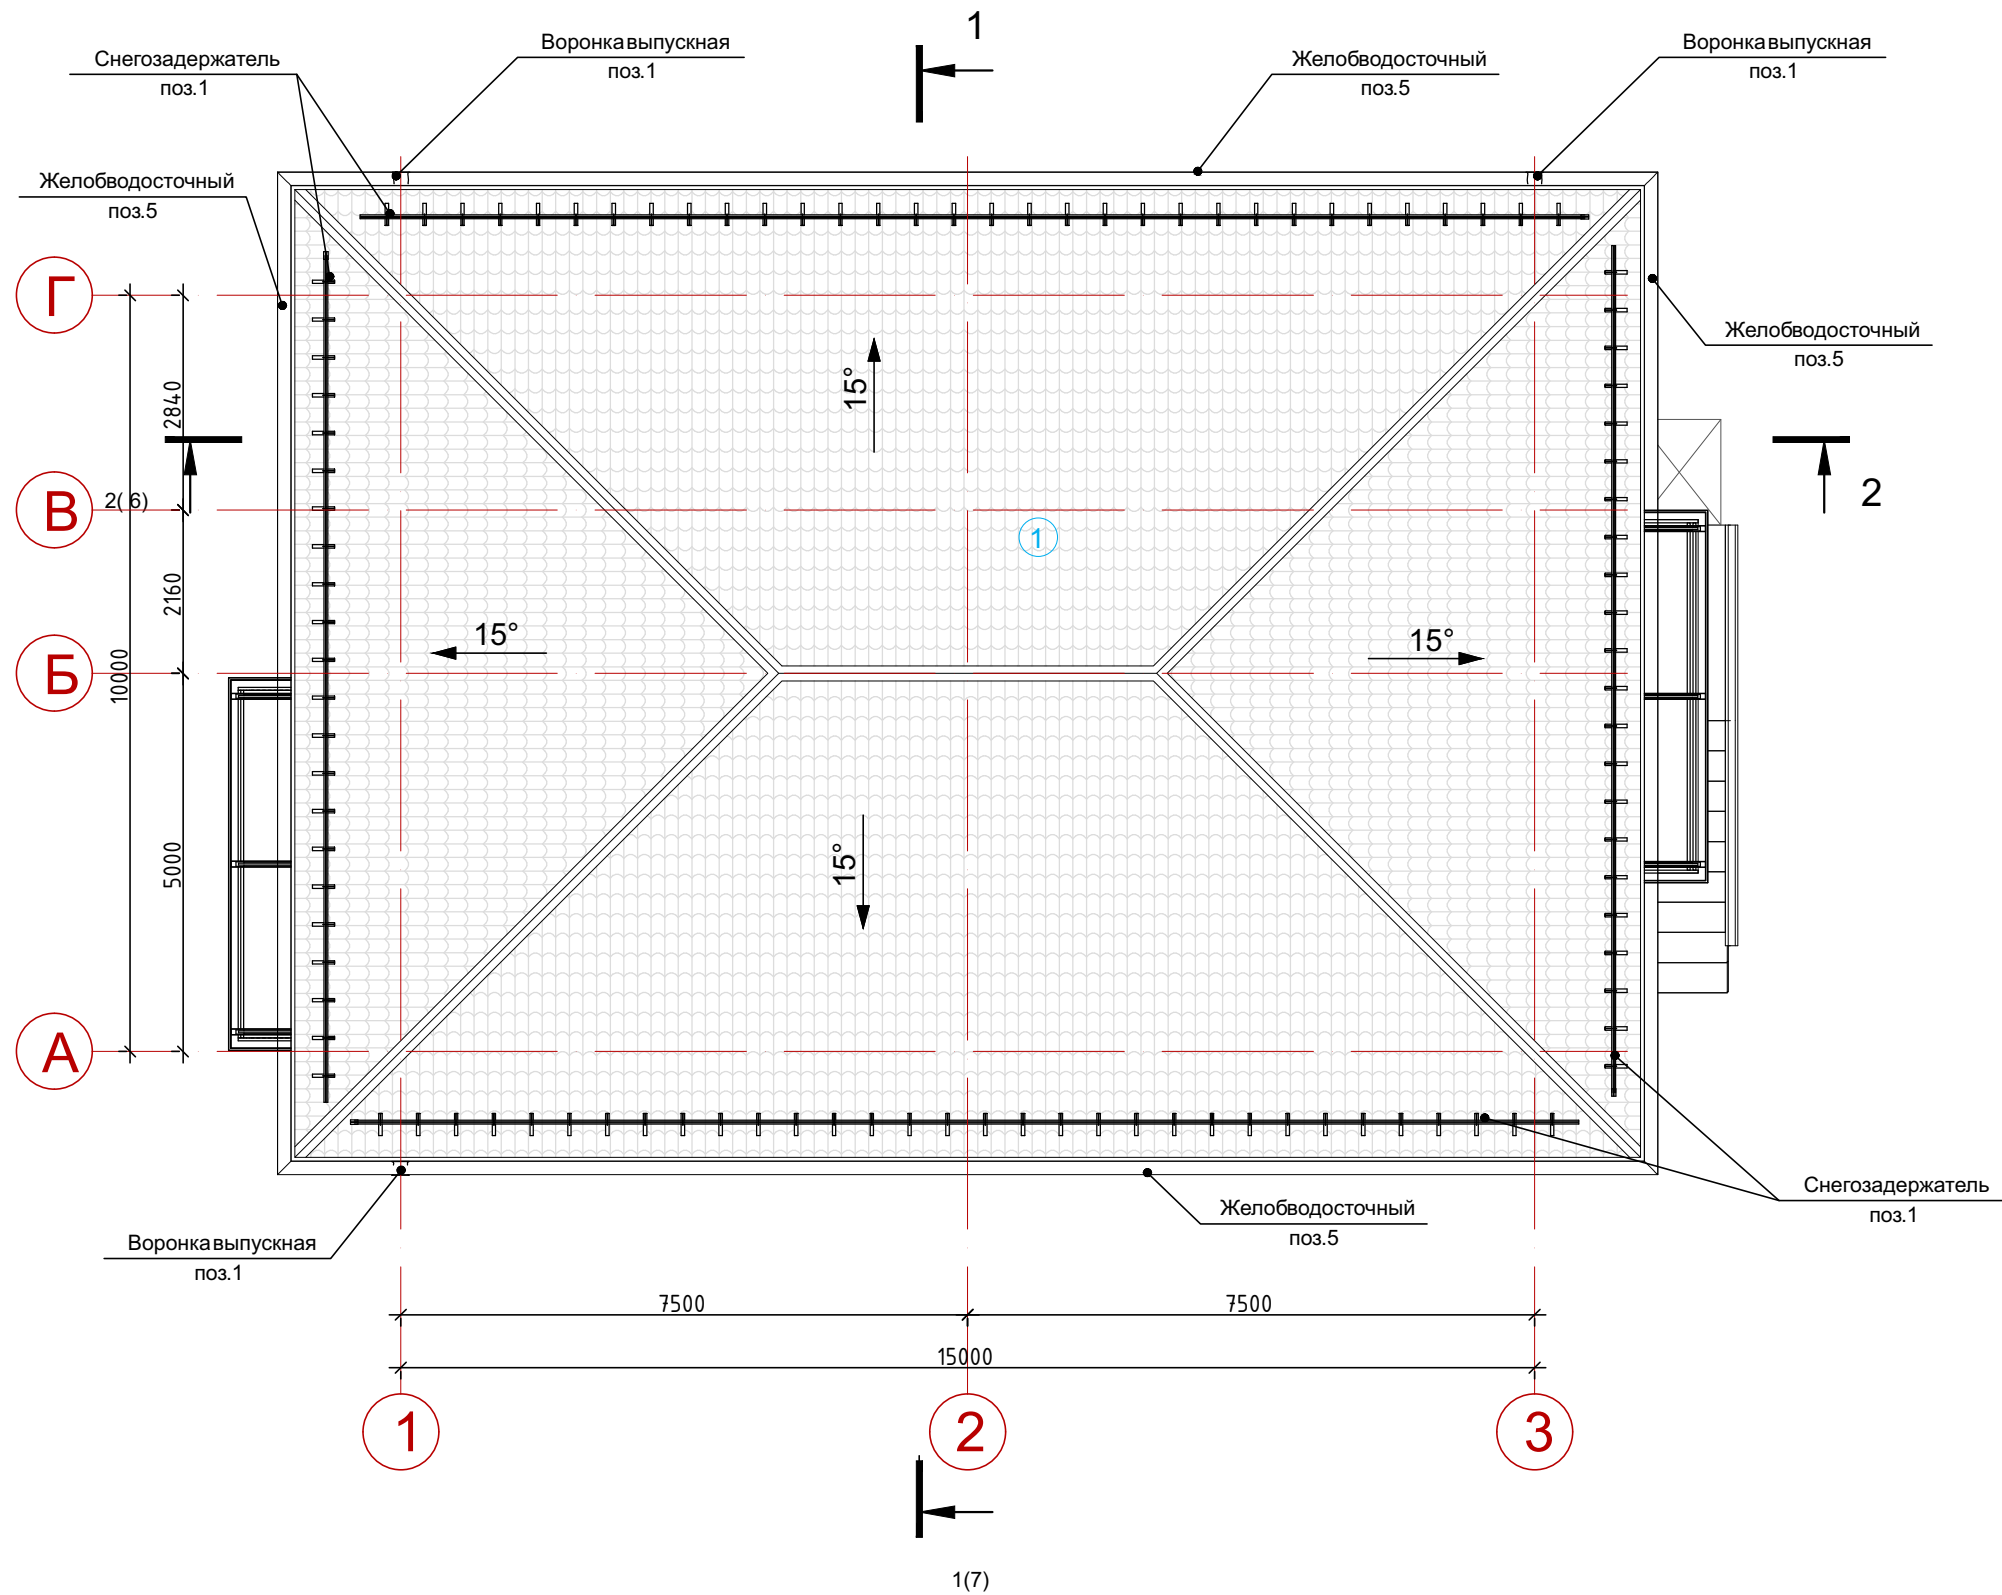


						АР			
						Строительство двухэтажного административного здания с подвалом и открытой террасой, расположенного на земельном участке по адресу РК, г.Усть-Каменогорск, набережная им.Е.П.Славского, гараж №40Г			
Изм.	Кол.уч.	Лист	№ док.	Подпись	дата	Административное здание	Стадия	Лист	Листов
ГИП		Косолапова В.А.					П	14	18
Архитектор						План кровли	ТОО "СемСтройтехнаб" Государственная лицензия ГСЛ №18016321		

Фасад А-Г

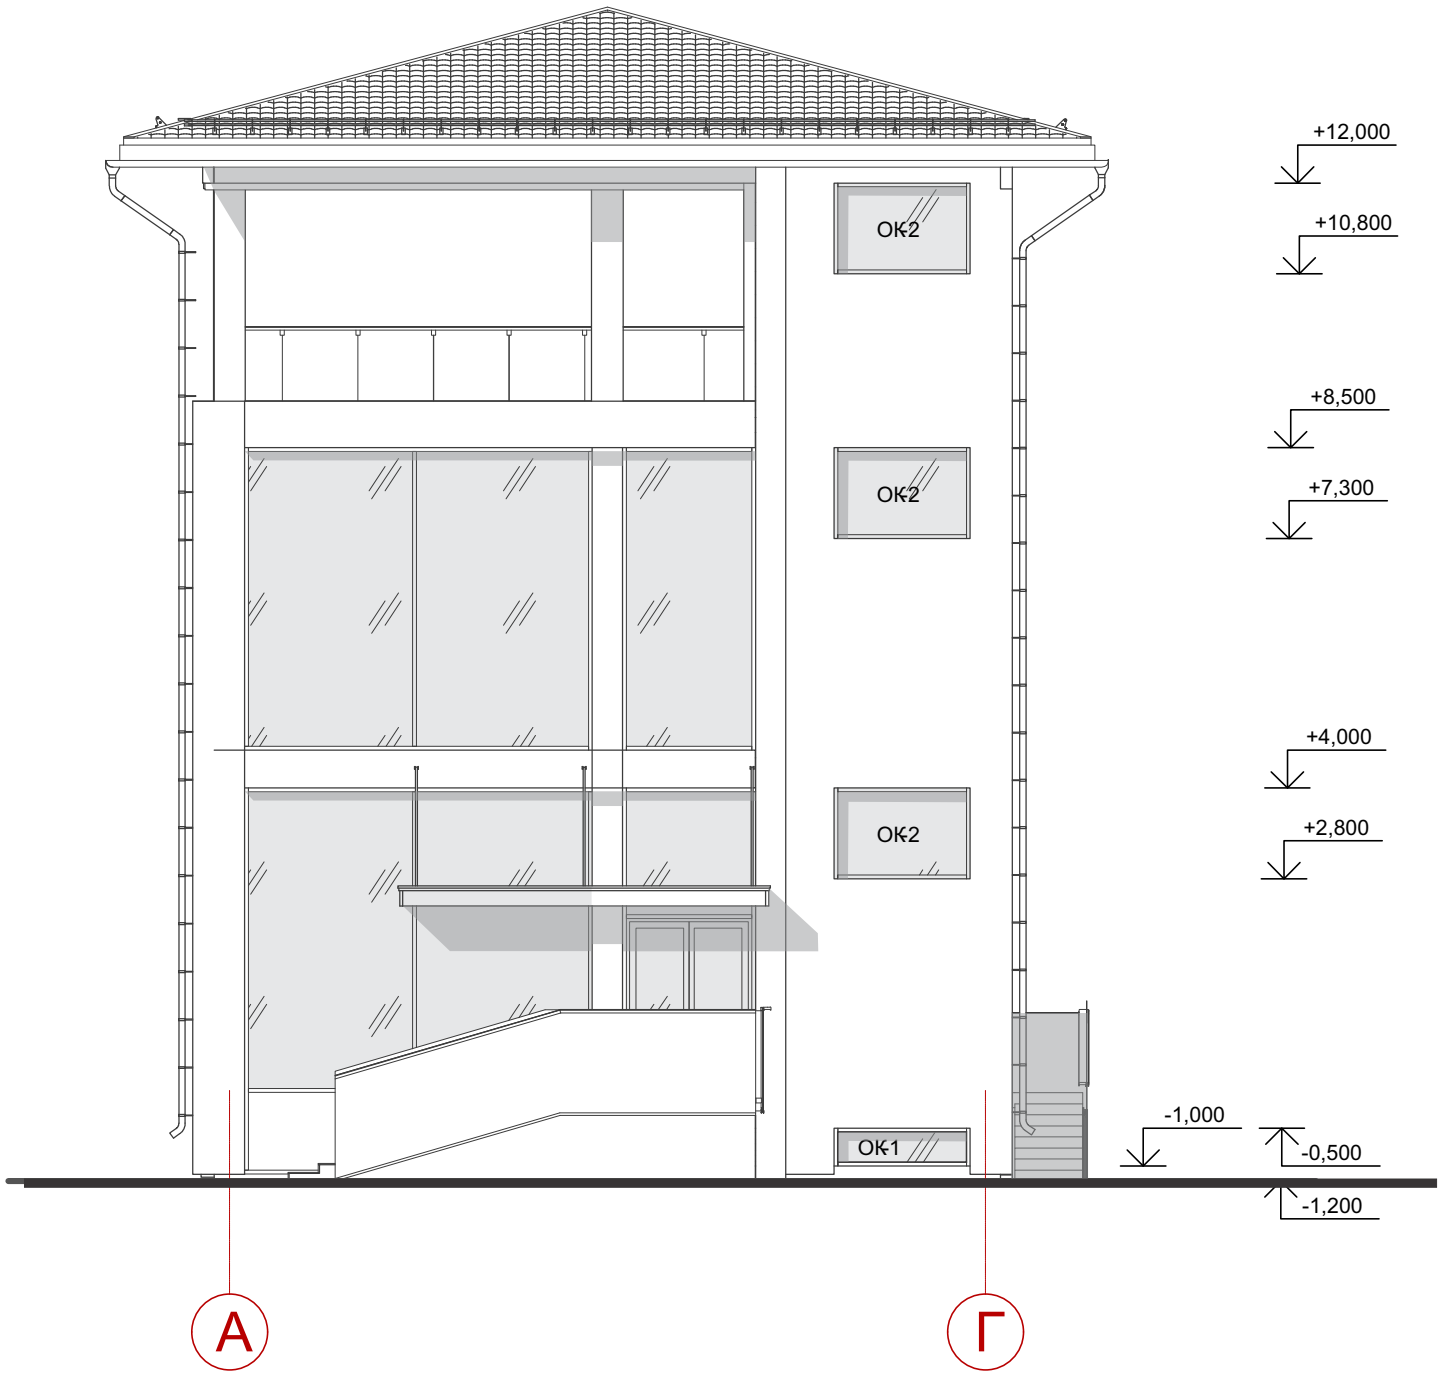


Фасад Г-А

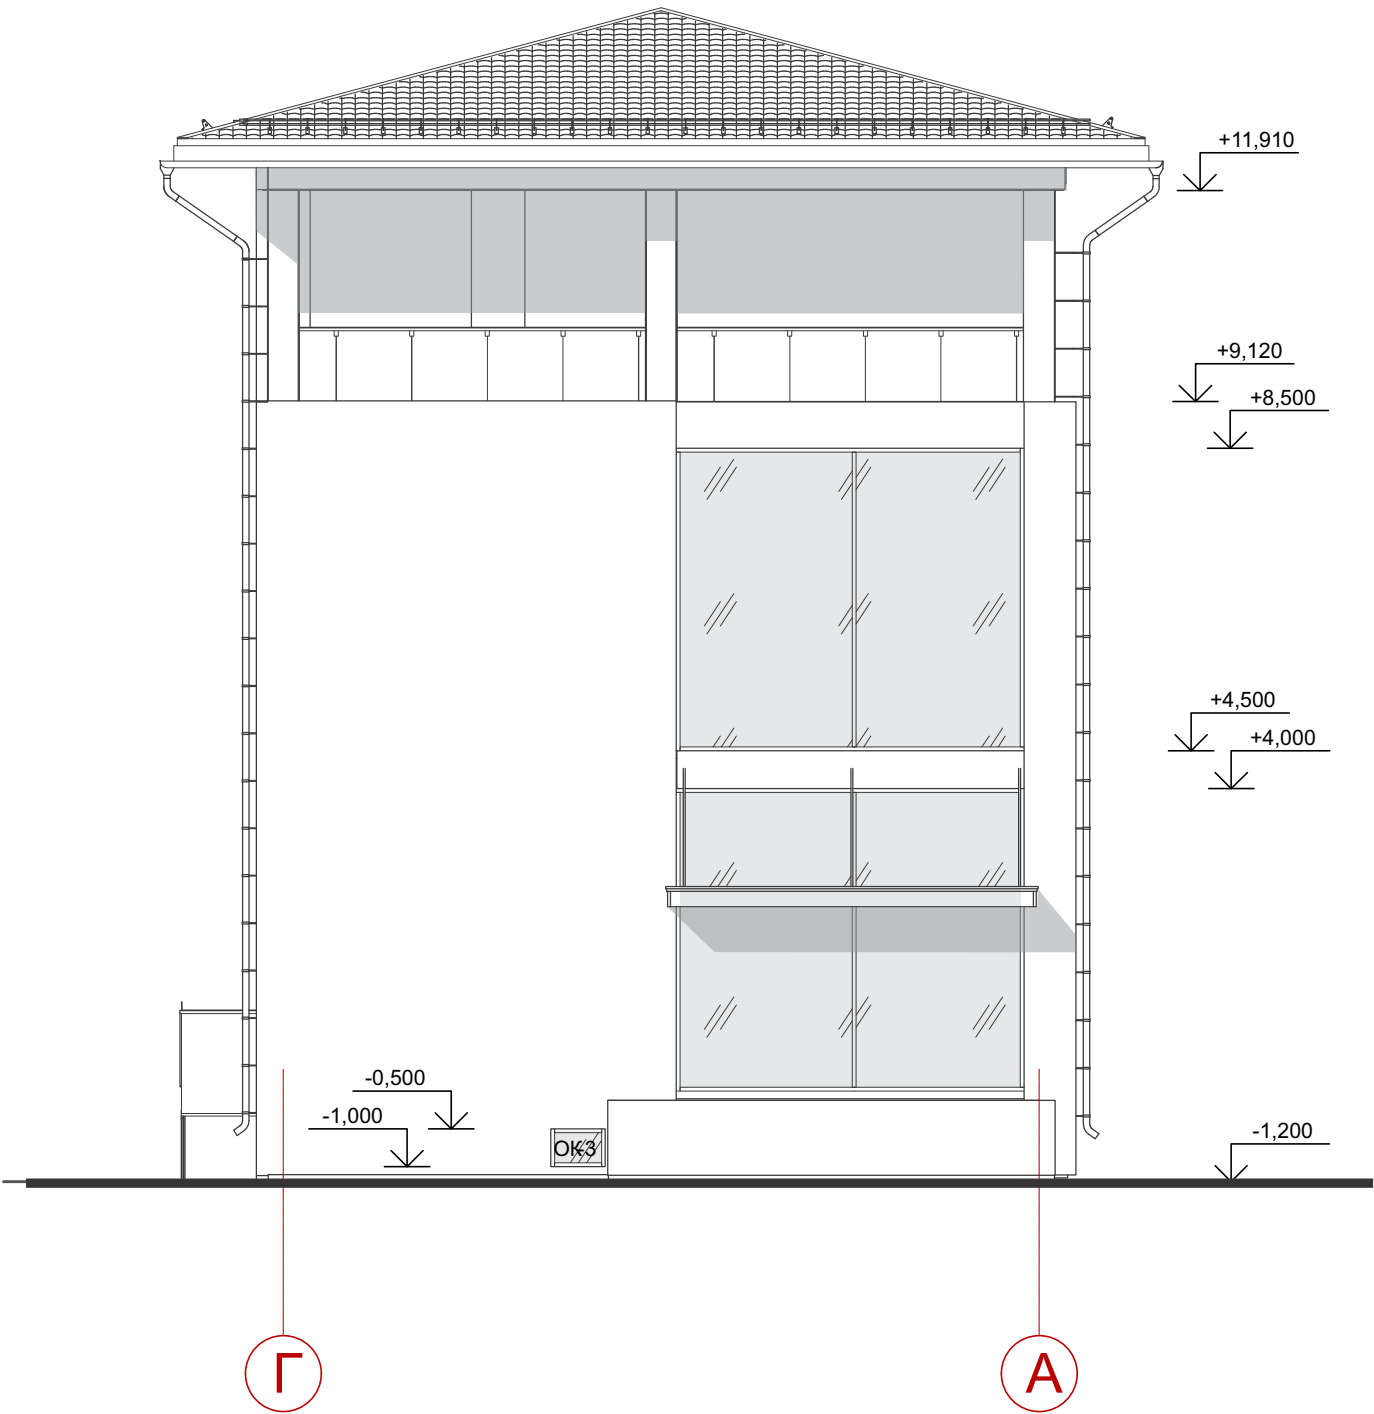


						АР			
						Строительство двухэтажного административного здания с подвалом и открытой террасой, расположенного на земельном участке по адресу РК, г.Усть-Каменогорск, набережная им.Е.П.Славского, гараж №40Г			
Изм.	Кол.уч.	Лист	№ док.	Подпись	дата	Административное здание	Стадия	Лист	Листов
ГИП		Косолапова В.А.					П	15	18
Архитектор						Фасады	ООО "СемСтройтехснаб" Государственная лицензия ГСЛ №18016321		

Фасада 1-3

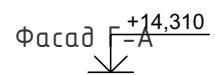

Фасад 3-1

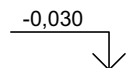

						АР			
						Строительство двухэтажного административного здания с подвалом и открытой террасой, расположенного на земельном участке по адресу РК, г.Усть-Каменогорск, набережная им.Е.П.Славского, гараж №40Г			
Изм.	Кол.уч.	Лист	№ док.	Подпись	Дата	Административное здание	Стадия	Лист	Листов
ГИП		Косолапова В.А.					П	16	18
Архитектор						Фасады	ТОО "СемСтройтехснаб"		
							Государственная		
							лицензия ГСЛ №18016321		

Ведомость отделки фасада					Ведомость отделки фасада				
Поз. отделки	Наименование элемента фасада	Наименование материала отделки	Номер эталона цвета, RAL	Площадь	Поз. отделки	Наименование элемента фасада	Наименование материала отделки	Номер эталона цвета, RAL	Площадь
Тип 1	Цоколь, стены подвала	Экструдированный пенополистеролл "пеноплекс" 50мм, Отделка сплитерная плитка	Рваный камень	159,71 39,26	Тип 15	Кровля	Фасонные элементы планка конька	Темно-серый RAL 7016	94,58
Тип 2	Стены	Кирпич отделочный КР-р-пу 250x120x65 Мин. вата "Izoterm -150" -130мм	Серый	557,93 327,16					
Тип 3	Стены	Фиброцементные панели типа "Латонит" на металл.каркасе. Мин. вата "Izoterm -150" -130мм	Темно-серый RAL 7016	19,38					
Тип 4	Стены	Фиброцементные панели типа "Латонит" на металл.каркасе. Мин. вата "Izoterm -150" -130мм	Светло-бежевый RAL 1013	54,87					
Тип 5	Стены, Элементы фасада	Кирпич отделочный	Серый	29,28					
Тип 6	Кровля	Металлочерепица	Темно-серый RAL 7016	428,21					
Тип 7	Кровля	Фасонные элементы Карнизная планка	Темно-серый RAL 7016	86,0 м.п.					
Тип 8	Кровля	Фасонные элементы Торцевая ветровая планка	Темно-серый RAL 7016	4,49 м.п.					
Тип 9	Кровля	Фасонные элементы Софит перфорированный	Темно-серый RAL 7016	86,0 м.п. 68,8 м2					
Тип 10	Кровля	Фасонные элементы планка ендовы нижняя	Темно-серый RAL 7016	32,82					
Тип 11	Кровля	Фасонные элементы планка ендовы верхняя	Темно-серый RAL 7016	32,82					
Тип 12	Окна	Фасонные элементы Отливы окон: сталь с полимерным покрытием	Темно-серый RAL 7016	82,56 м.п.					
Тип 13	Крыльцо, вход в подвал, пандус	Отделка сплитерная плитка	Рваный камень	26,17					
Тип 14	Крыльцо, вход в подвал, пандус	Керамогранит с шероховатой поверхностью	Серый	117,47					

Изм.	Кол.уч.	Лист	№ док.	Подпись	дата	АР
ГИП		Косолапова В.А.				Строительство двухэтажного административного здания с подвалом и открытой террасой, расположенного на земельном участке по адресу РК, г.Усть-Каменогорск, набережная им.Е.П.Славского, гараж №40Г
Архитектор						Административное здание
						П
						17
						18
						ТОО "СемСтройтехнаб"
						Государственная лицензия ГСЛ №18016321



						АР			
						Строительство двухэтажного административного здания с подвалом и открытой террасой, расположенного на земельном участке по адресу РК, г.Усть-Каменогорск, набережная им.Е.П.Славского, гараж №40Г			
Изм.	Кол.уч.	Лист	№ док.	Подпись	дата	Административное здание	Стадия	Лист	Листов
	ГИП		Косолапова В.А.				П	18	18
Архитектор						3D визуализация	ТОО "СемСтройтехснаб" Государственная лицензия ГСЛ №18016321		