

Общество с ограниченной ответственностью



Свидетельство о допуске СРО № 2002.00-2016-7733899110-П-186

Рабочая документация.

Интерьерные решения. Гостиница "Приморская", корпус 1, 4 этаж, N410. Тип "Стандарт".

Развитие гостиницы «Приморская» в г. Сочи. Приспособление и сохранение объекта культурного наследия «Здание, где в годы Великой Отечественной войны размещались госпитали N 2095, 2120, 1941–1945 годы», расположенного по адресу: г. Сочи, Центральный район, ул. Соколова, д. 1.

Шифр: ПриМ-0001/2024-АИ.02-410

Общество с ограниченной ответственностью



Свидетельство о допуске СРО № 2002.00-2016-7733899110-П-186

Рабочая документация.

Интерьерные решения. Гостиница "Приморская", корпус 1, 4 этаж, N410. Тип "Делюкс".

Развитие гостиницы «Приморская» в г. Сочи. Приспособление и сохранение объекта культурного наследия «Здание, где в годы Великой Отечественной войны размещались госпитали N 2095, 2120, 1941–1945 годы», расположенного по адресу: г. Сочи, Центральный район, ул. Соколова, д. 1.

Генеральный директор

Главный архитектор проекта



Е.А. Сафронова Е.А. Сафронова


Е.А. Сафронова Е.А. Сафронова

г. Москва, 2026 г.

Согласовано				
Взам. инв. №				
Подп. и дата				
Инв. № подл.				


Ведомость чертежей		
Лист	Наименование	Масштаб
1.	– Ведомость чертежей.	150
2.	– План с расстановкой мебели.	150
3.	– План гидроизоляции мокрых зон.	150
4.	– План раскладки напольного покрытия. Деталь устройства дверного порожка.	150
5.	– План с указанием плинтусов.	150
6.	– Детализованный чертеж к плану раскладки напольных покрытий. Детали и узлы облицовки. Узел 4, 5, 6. Разрез 7–7, 8–8.	1:25
7.	– План теплого пола. Узел 7.	150
8.	– План заполнения дверных проемов.	150
9.	– Детализованный чертеж к плану заполнения дверных проемов.	150
10.	– Детализованный чертеж к плану заполнения дверных проемов.	1:25
11.	– План расположения розеток и выключателей. Лист 1.	150
12.	– План расположения розеток и выключателей. Лист 2.	150
13.	– План расположения электрических выводов. Деталь устройства встр. подсветки прикроватной тумбочки.	150
14.	– План с привязкой светильников и указанием групп освещения.	150
15.	– План с расположением и маркировкой светильников.	150
16.	– План потолков.	150
17.	– План с маркировкой карнизов.	150
18.	– Детализованный чертеж к плану потолка. Узлы и детали потолка. Разрез 1–1, 2–2, 3–3, 4–4, 5–5, 6–6, 7–7. Узел 8.	1:25
19.	– План с привязкой сантехники.	150
20.	– Помещение N1 (прихожая). Развертка стен А–А.	1:25

Лист	Наименование	Масштаб
21.	– Помещение №2 (гардеробная комната). Маркировочный план.	1:25
22.	– Помещение №2 (гардеробная комната). Развертка стен А–А.	1:25
23.	– Помещение №3 (ванная комната). План с привязкой сантехники и маркировкой оборудования.	1:25
24.	– Помещение №3 (ванная комната). План раскладки напольных покрытий.	1:25
25.	– Помещение №3 (ванная комната). Схема привязки сантехники. Развертка стен А–В. Лист 1	1:25
26.	– Помещение №3 (ванная комната). Схема привязки сантехники. Развертка стен В–А. Лист 2	1:25
27.	– Помещение №3 (ванная комната). Развертка стен А–В.	1:25
28.	– Помещение №3 (ванная комната). Развертка стен В–А.	1:25
29.	– Помещение N4 (санузел). Схема и план с привязкой сантехники. Развертка стен А–А.	1:25
30.	– Помещение N4 (санузел). Развертка стен А–А. План с раскладкой напольных покрытий.	1:25
31.	– Помещение N5 (душевая). Схема и план с привязкой сантехники. Развертка стен А–А.	1:25
32.	– Помещение N5 (душевая). Развертка стен А–А. План с раскладкой напольных покрытий.	1:25
33.	– Помещение №6 (спальная комната). Маркировочный план.	1:25
34.	– Помещение №6 (спальная комната). Развертка стен А–В. План с маркировкой разверток.	1:25
35.	– Помещение №6 (спальная комната). Развертка стен В–А. План с маркировкой разверток.	1:25
36.	– Помещение №7 (гостиная комната). Маркировочный план.	1:25
37.	– Помещение №7 (гостиная комната). Развертка стен А–Б.	1:25
38.	– Помещение №7 (гостиная комната). Развертка стен Б–Ж. План с маркировкой разверток.	1:25
39.	– Помещение №7 (гостиная комната). Развертка стен Ж–З. План с маркировкой разверток.	1:25
40.	– Помещение №7 (гостиная комната). Развертка стен З–А. План с маркировкой разверток.	1:25

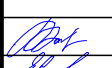						Заказчик: ООО «Приморская» Технический заказчик: АО «СЗ «ЛСР. Недвижимость – М»							
						ПриМ-0001/2024-АИ.01-410							
						Развитие гостиницы «Приморская» в г. Сочи. Приспособление и сохранение объекта культурного наследия «Здание, где в годы Великой Отечественной войны размещались госпитали № 2095, 2120, 1941-1945 годы», расположенного по адресу: г. Сочи, Центральный район, ул. Саколова, д. 1.							
Изм.	Кол.уч.	Лист	№ док.	Подпись	Дата	Интерьерные решения. Гостиница “Приморская”, корпус 1, 4 этаж, N 410. Тип “Делюкс”			Стадия	Лист	Листов		
Разработал		Казыева А.Р.			02.02.26				РД	1	40		
Проверил		Новикова Е.			02.02.26								
						Ведомость чертежей.			ООО “Арх-И-Арм”				
Н.контр.		Бахвалова Л.В.			02.02.26								
ГАП		Сафронова Е.			02.02.26								


План с расстановкой мебели.
Корпус 1, 4 этаж, N 410. Тип "Делюкс"

Экспликация помещений		
№	Наименование	Площадь м2
1	Прихожая	3,74
2	Гардеробная комната	4,18
3	Ванная комната	6,77
4	Санузел	1,2
5	Душевая	1,56
6	Спальная комната	10,45
7	Гостиная комната	19,37
5	общая	47,3

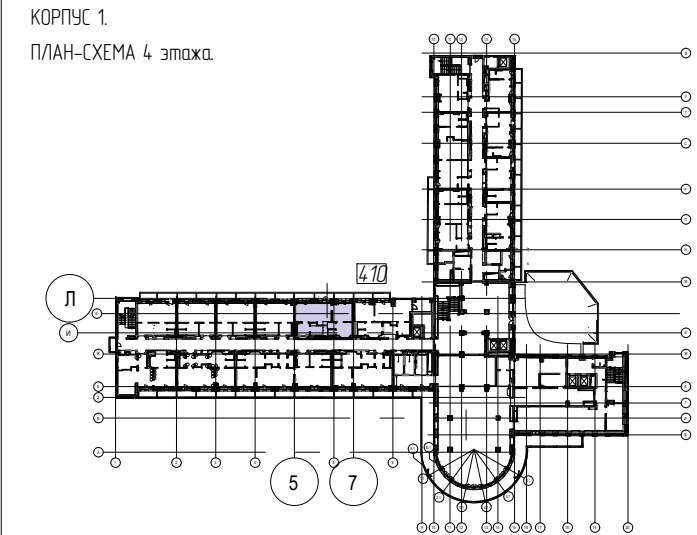

- Условные обозначения
- 1 - Номер помещения
 - Р - Радиатор

Согласовано					
Взам. инв. №					
Подп. и дата					
Инв. № подл.					

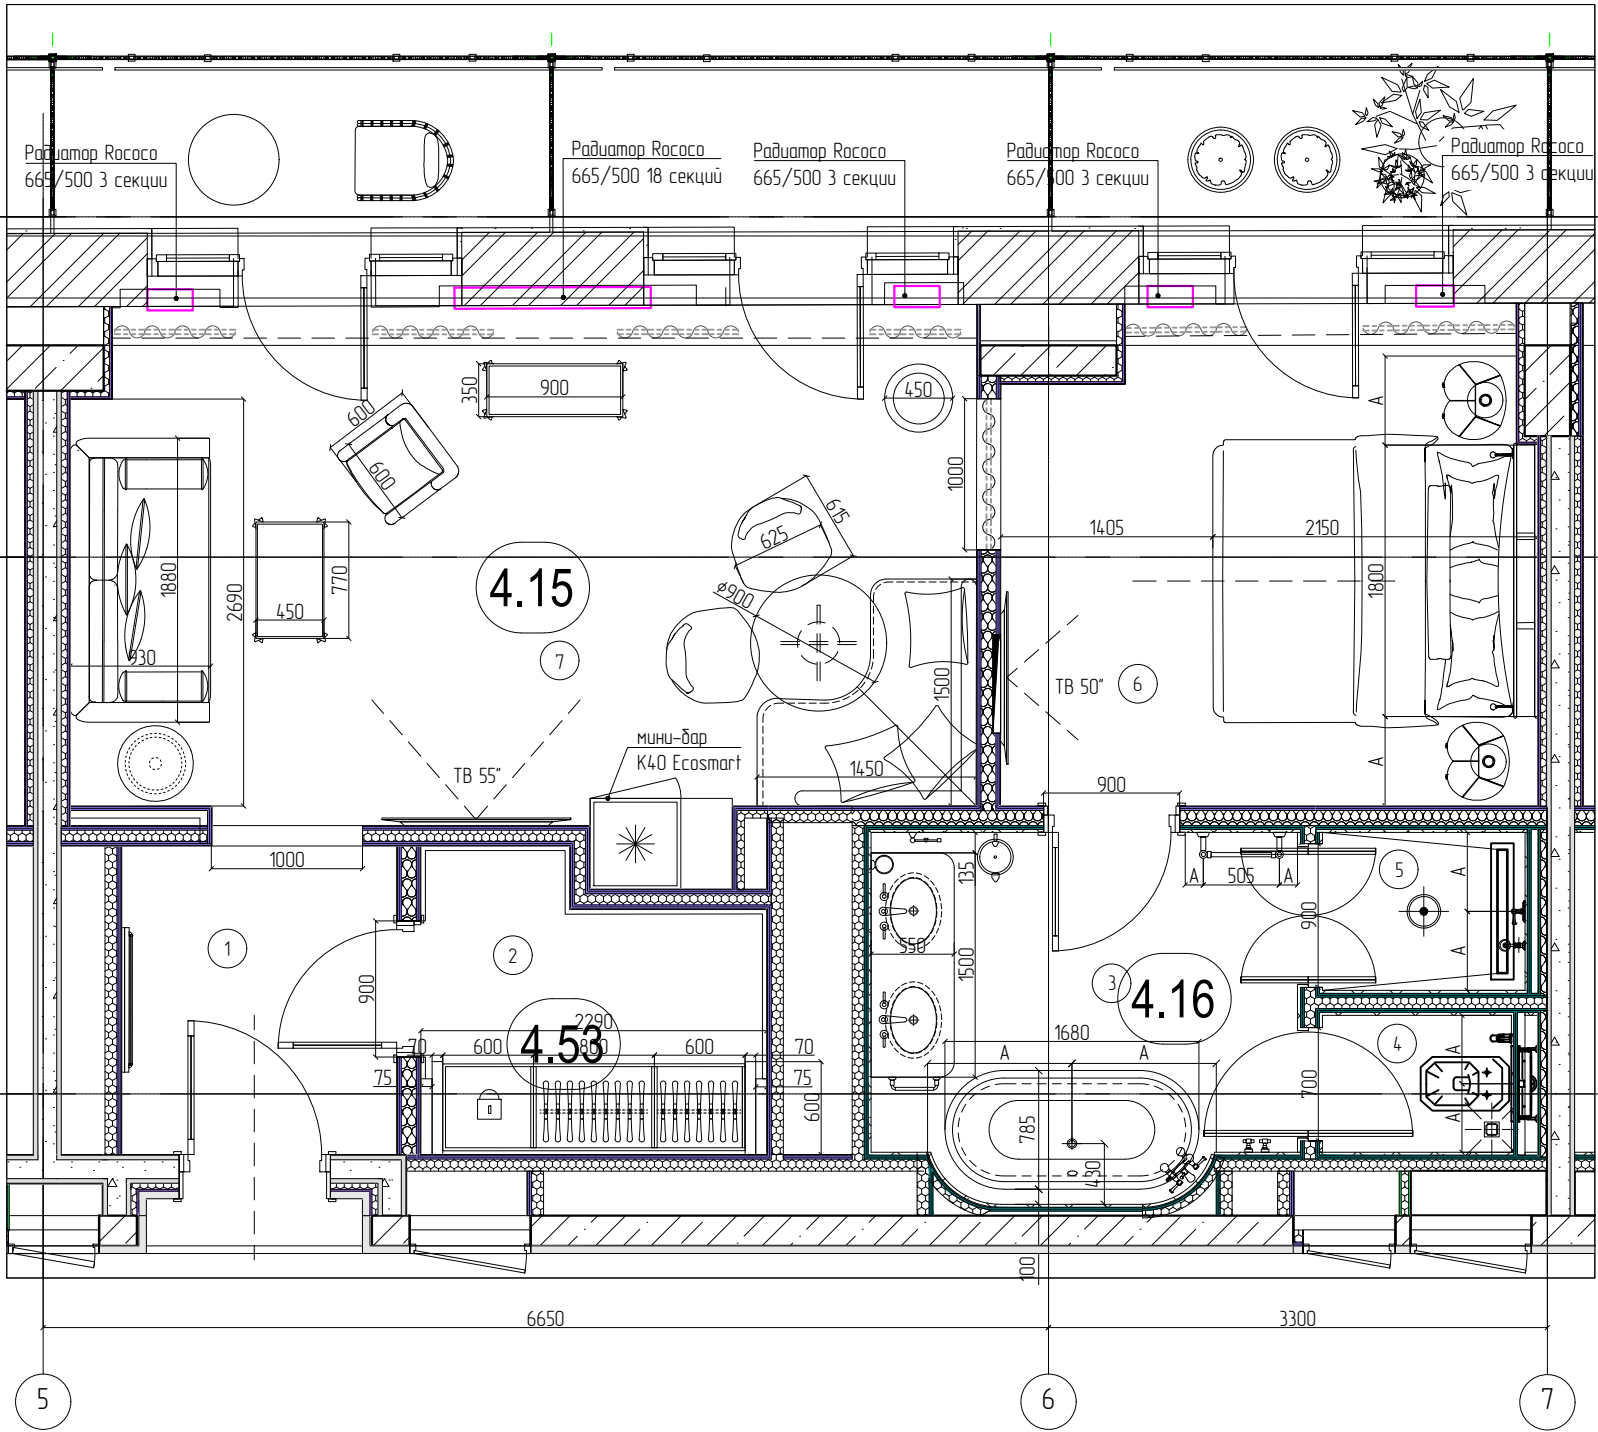

Заказчик: ООО «Приморская»						ПриМ-0001/2024-АИ.01-410		
Технический заказчик: АО «СЗ «ЛСР. Недвижимость – М»								
Развитие гостиницы «Приморская» в г. Сочи. Приспособление и сохранение объекта культурного наследия «Здание, где в годы Великой Отечественной войны размещались госпитали № 2095, 2120, 1941-1945 годы», расположенного по адресу: г. Сочи, Центральный район, ул. Саколова, д. 1.								
Изм.	Кол.уч.	Лист	№ док.	Подпись	Дата	Интерьерные решения. Гостиница "Приморская", корпус 1, 4 этаж, N 410. Тип "Делюкс"	Стадия	Лист
Разработал	Казыева А.Р.			Р. Казыева	02.02.26		РД	2
Проверил	Нобикова Е.			Е. Нобикова	02.02.26			40
						План с расстановкой мебели.	ООО "Арх-И-Арм"	
Н.контр.	Бахвалова Л.В.			Л.В. Бахвалова	02.02.26			
ГАП	Сафронова Е.			Е. Сафронова	02.02.26		Формат А3	

Примечания

1. Планировочное решение выполнено на основании чертежей раздела АР, ТЗ и концепции, утвержденной Заказчиком.

2. При расхождении размеров на строительной площадке, превышающих ± 40 мм, их необходимо согласовать с Архитектором. В случае расхождения размеров между мелко масштабными чертежами и детализированными необходимо руководствоваться только размерами детализированного чертежа. Не использовать фрагменты плана как шаблон.


3. Высоты даны от уровня чистого пола этажа. За отм. чистого пола принять верх чистового покрытия коридора.

План гидроизоляции мокрых зон.
Корпус 1, 4 этаж, N 410. Тип "Делюкс"

Экспликация помещений		
№	Наименование	Площадь м2
1	Прихожая	3,74
2	Гардеробная комната	4,18
3	Ванная комната	6,77
4	Санузел	12
5	Душевая	1,56
6	Спальная комната	10,45
7	Гостиная комната	19,37
S общая		47,3

Условные обозначения:	
1	- Номер помещения
	- Зона устройства гидроизоляции. Для плоскостей применить Аквупласт или аналог
	- Гидроизоляцию завести на стены на 1050 мм
	- Гидроизоляцию завести на стены на 2700 мм


Согласовано					
Взам. инв. №					
Подп. и дата					
Инв. № подл.					

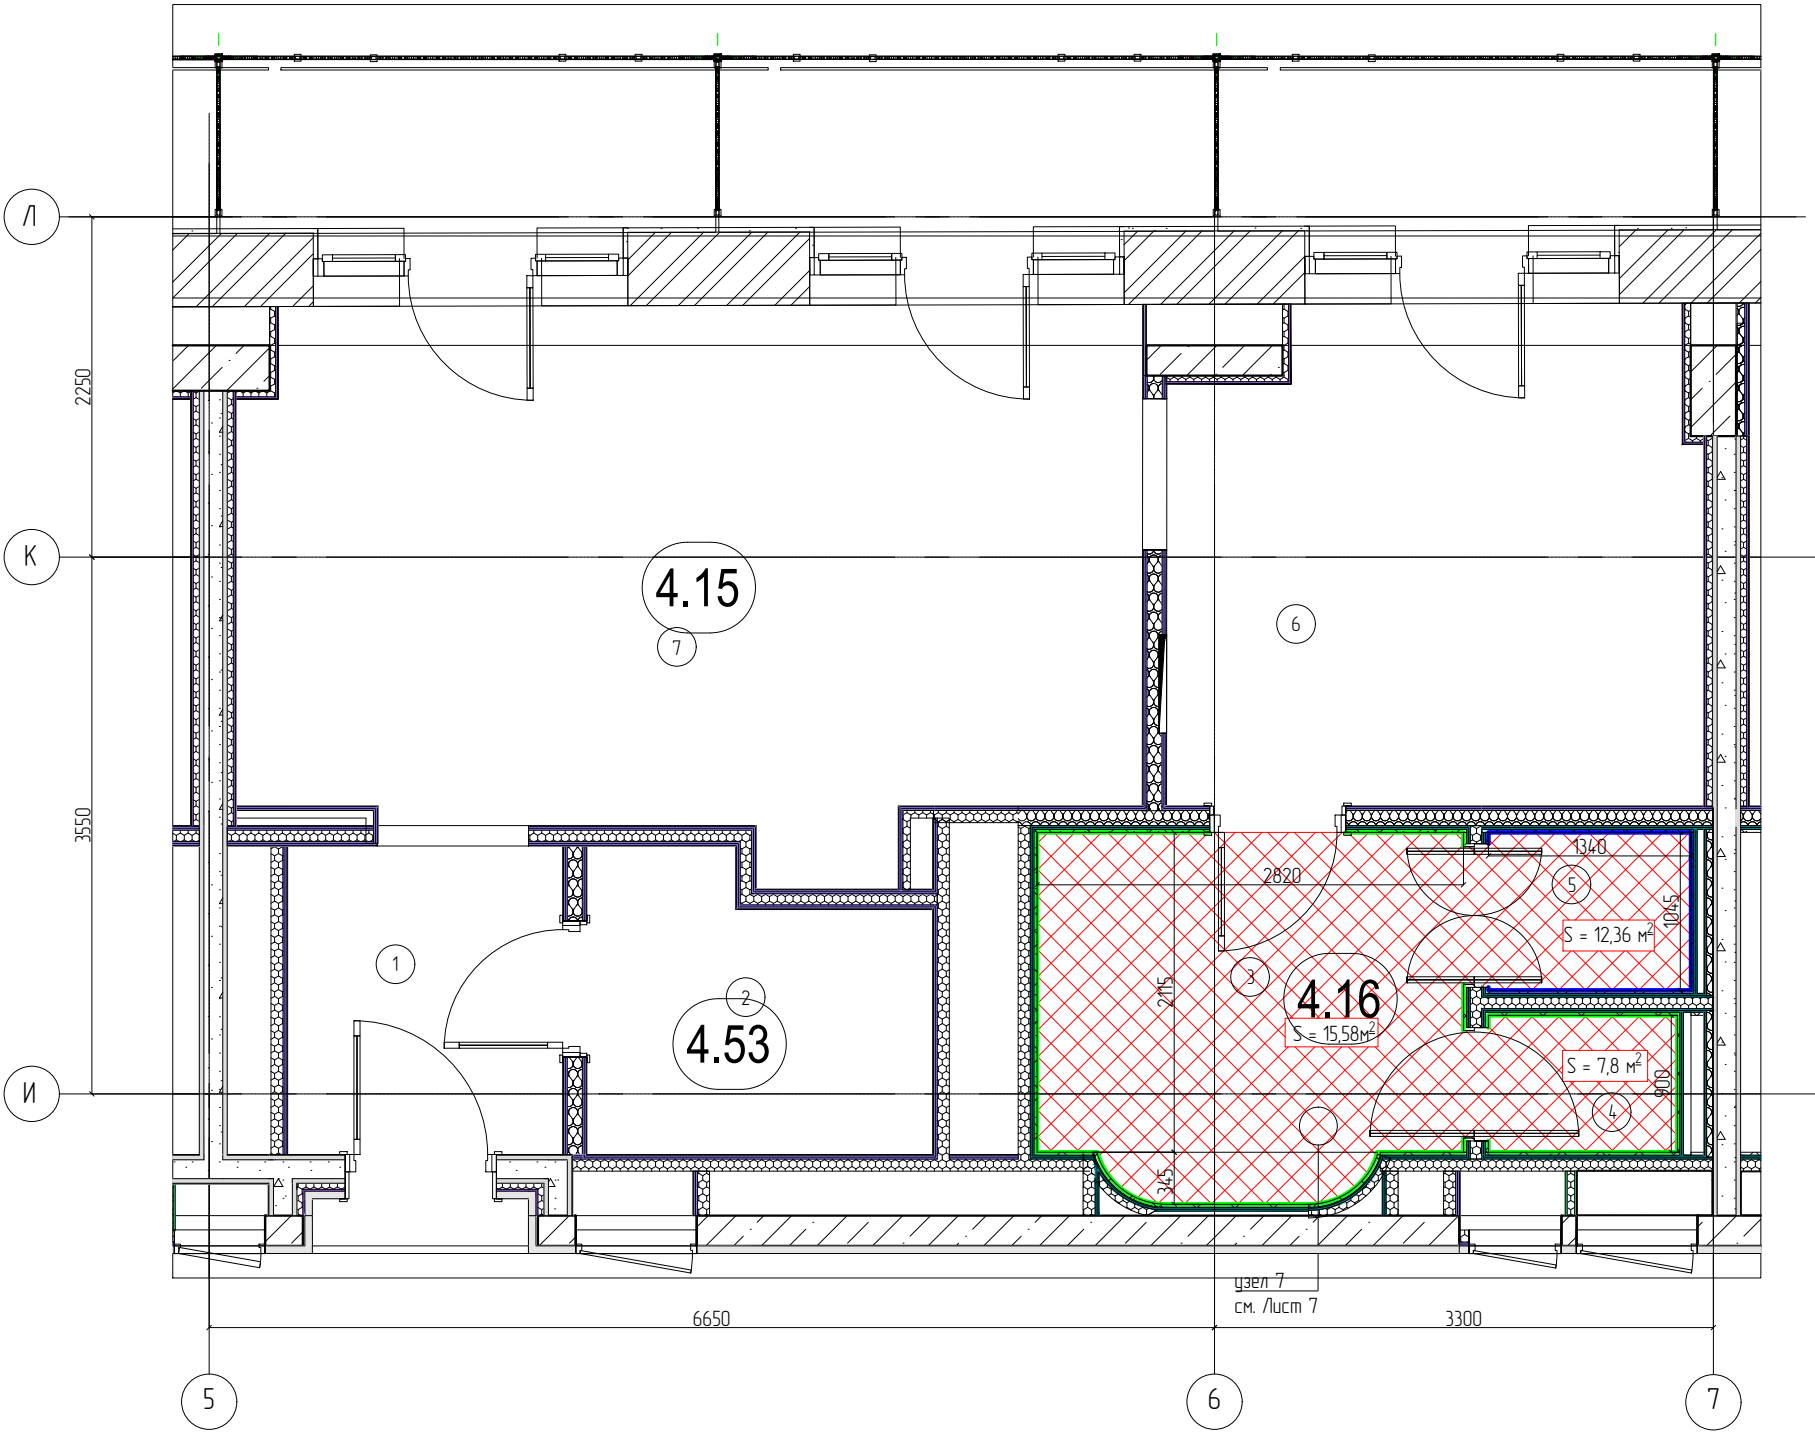

Заказчик: ООО «Приморская»						ПриМ-0001/2024-АИ.01-410		
Технический заказчик: АО «СЗ «ЛСР. Недвижимость – М»								
Развитие гостиницы «Приморская» в г. Сочи. Приспособление и сохранение объекта культурного наследия «Здание, где в годы Великой Отечественной войны размещались госпитали № 2095, 2120, 1941-1945 годы», расположенного по адресу: г. Сочи, Центральный район, ул. Саколова, д. 1.								
Изм.	Кол.уч.	Лист	№ док.	Подпись	Дата	Интерьерные решения. Гостиница "Приморская", корпус 1, 4 этаж, N 410. Тип "Делюкс"	Стадия	Лист
Разработал	Казыева А.Р.				02.02.26		РД	3
Проверил	Нобикова Е.				02.02.26			40
						План гидроизоляции мокрых зон. М 1:50	ООО "Арх-И-Арм"	
Н.контр.	Бахвалова Л.В.				02.02.26			
ГАП	Сафронова Е.				02.02.26			

План раскладки напольных покрытий.
Корпус 1, 4 этаж, N 410. Тип "Делюкс"


Экспликация помещений		
№	Наименование	Площадь м2
1	Прихожая	3,74
2	Гардеробная комната	4,18
3	Ванная комната	6,77
4	Санузел	12
5	Душевая	1,56
6	Спальная комната	10,45
7	Гостиная комната	19,37
Σ общая		47,3

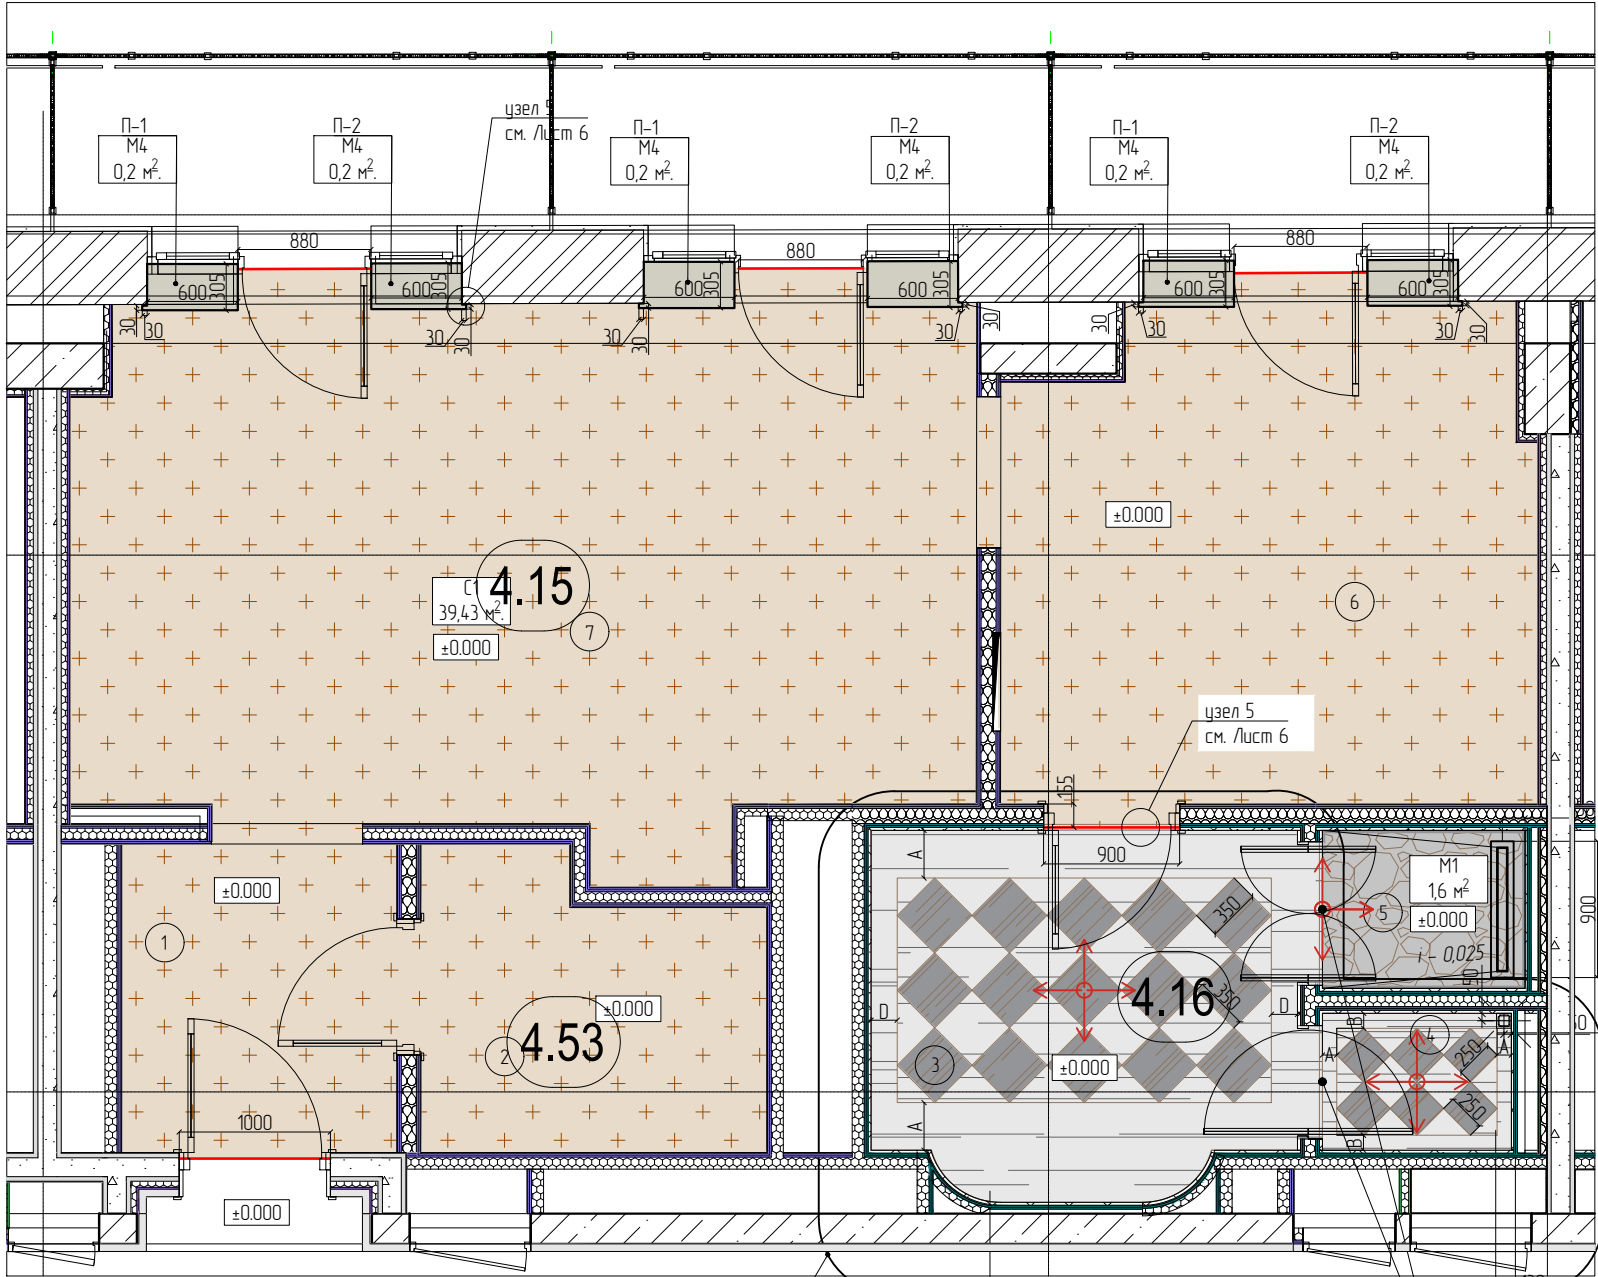

Спецификация напольных покрытий номера Deluxe				
Тип	Изображение типоразмера	Описание	Вид	Кол-во
- C1 -		- ковролин Bespoke Carpet Flooring, 80% wool and 20% nylon, arm. ivory with print, толщина		39,43 + 10% = 43,37 м²
- M1 -		- натуральный камень Breccia Capraia marble, матовый, толщина 20мм		1,6 + 10% = 2,76 м²
- M2 -		- натуральный камень Corteccia marble, матовый, толщина 20мм		2,22 + 10% = 2,44 м²
- M3 -		- натуральный камень Calacata Borghini marble, матовый, толщина 20мм		5,9 + 10% = 6,5 м²
- M4 -		- натуральный камень Botticino stone, матовый, толщина 20мм		1,2 + 10% = 1,32 м²
		- Металлический профиль, L = 880мм, 880мм, 880мм, 900мм, 1000мм, ширина 13мм, цвет: брашированная бронза		3 поз.м. + 10% = 4,4 поз.м.

Условные обозначения:

- 1 - Номер помещения
- ±0.000 - Уровень чистого пола этажа
- M1 - Маркировка напольного покрытия
- 0,62 м² - Площадь напольного покрытия
- Устройство порога арт. TECEDrainline 650800/650900
- Устройство порога 100x100мм
- Направление укладки

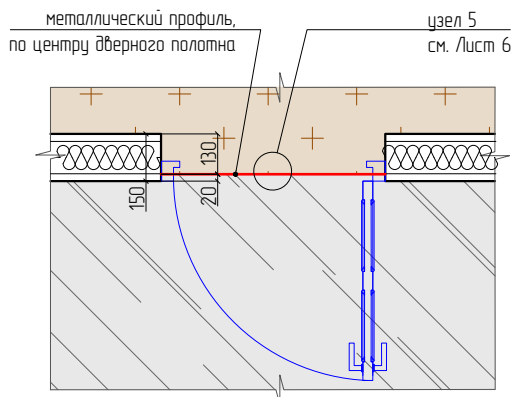

Раскладка напольного покрытия:
см. Детализированный чертеж, лист 24,30

M2
1,84 м²
M3
5,1 м²

Устройство порога из натурального
камня, мрамор 20мм. см. узел 6, лист 6

Примечания

1. Планировочное решение выполнено на основании чертежей раздела АР, ТЗ и концепции, утвержденной Заказчиком.
2. При расхождении размеров на строительной площадке, превышающих ± 40 мм, их необходимо согласовать с Архитектором. В случае расхождения размеров между мелко масштабными чертежами и детализированными необходимо руководствоваться только размерами детализированного чертежа. Не использовать фрагменты плана как шаблон.
3. За отм. чистого пола принять верх чистового покрытия коридора этажа. Полы во всех помещениях должны быть в одном уровне на отм. 0.000 (чистый пол этажа).
4. На границе разных напольных покрытий переходной шов закрыть металлическим порогом. Шов выполнить по центру дверного полотна см. План заполнения дверных проемов.
5. Подсчет материалов указан с 10% запасом, расчет скорректировать согласно раскроя поставщика.
6. В помещениях: N3(ванная), N4(душевая), N5(су), перед укладкой напольного покрытия произвести гидроизоляцию, см. План гидроизоляции мокрых зон.
7. Начало раскладки на чертеже указано стрелками.
8. Весь натуральный камень выкладывать с минимальным швом, образовавшиеся зазоры обрабатывать затиркой в цвет камня.
9. В зоне су и душевой выполнить разуклонку в сторону сливного лотка.


						Заказчик: ООО «Приморская» Технический заказчик: АО «СЗ «ЛСР. Недвижимость – М»			ПриМ-0001/2024-АИ.01-410			
						Развитие гостиницы «Приморская» в г. Сочи. Приспособление и сохранение объекта культурного наследия «Здание, где в годы Великой Отечественной войны размещались госпитали № 2095, 2120, 1941-1945 годы», расположенного по адресу: г. Сочи, Центральный район, ул. Соколова, д. 1.						
Изм.	Кол.уч.	Лист	№ док.	Подпись	Дата	Интерьерные решения. Гостиница "Приморская", корпус 1, 4 этаж, N 410. Тип "Делюкс"			Стадия	Лист	Листов	
Разработал	Казыева А.Р.				02.02.26				РД	4	40	
Проверил	Новикова Е.				02.02.26							
Н.контр.	Бахвалова Л.В.				02.02.26	План раскладки напольных покрытий. Деталь устройства дверного порога. М 1:50			ООО "Арх-И-Арм"			
ГАП	Сафронова Е.				02.02.26							

План с указанием плинтусов
Корпус 1, 4 этаж, N 410. Тип "Делюкс"


Экспликация помещений		
№	Наименование	Площадь м2
1	Прихожая	3,74
2	Гардеробная комната	4,18
3	Ванная комната	6,77
4	Санузел	12
5	Душевая	1,56
6	Спальная комната	10,45
7	Гостиная комната	19,37
S общая		47,3

Спецификация плинтусов номера Deluxe:				
Тип	Изображение типоразмера	Описание	Вид	Кол-во
-S1-		- Плинтус из массива натурального дерева, Ash Wood (ясень), покрытие матовым бесцветным лаком. Н-150мм, толщина 17мм		31,1 поз.м. + 10% = 34,2 поз.м.
-S3-		- Плинтус из мрамора -M2a- Carreccia marble, толщина 20мм, Н - 120мм, полированный		7,5 поз.м. + 10% = 8,25 поз.м.
-S4-		- Плинтус из мрамора -M3a- Calacata Barghini marble, толщина 20мм, Н - 100мм, полированный		3,6 поз.м. + 10% = 3,96 поз.м.


Плинтус S1
из массива натурального дерева
Ash Wood (ясень)
150мм x 17мм

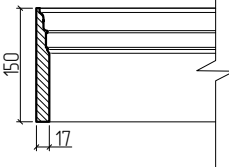

Плинтус S3
из полированного мрамора -M2a-
Carreccia Marble
120мм x 20мм

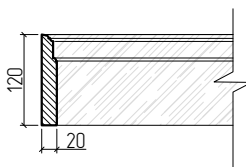


Плинтус S4
из полированного мрамора -M3a-
Calacata Barghini
100мм x 20мм

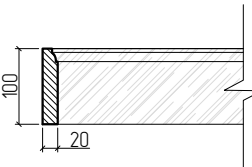

Условные обозначения:

- 1 - Номер помещения
S1 - Маркировка плинтуса

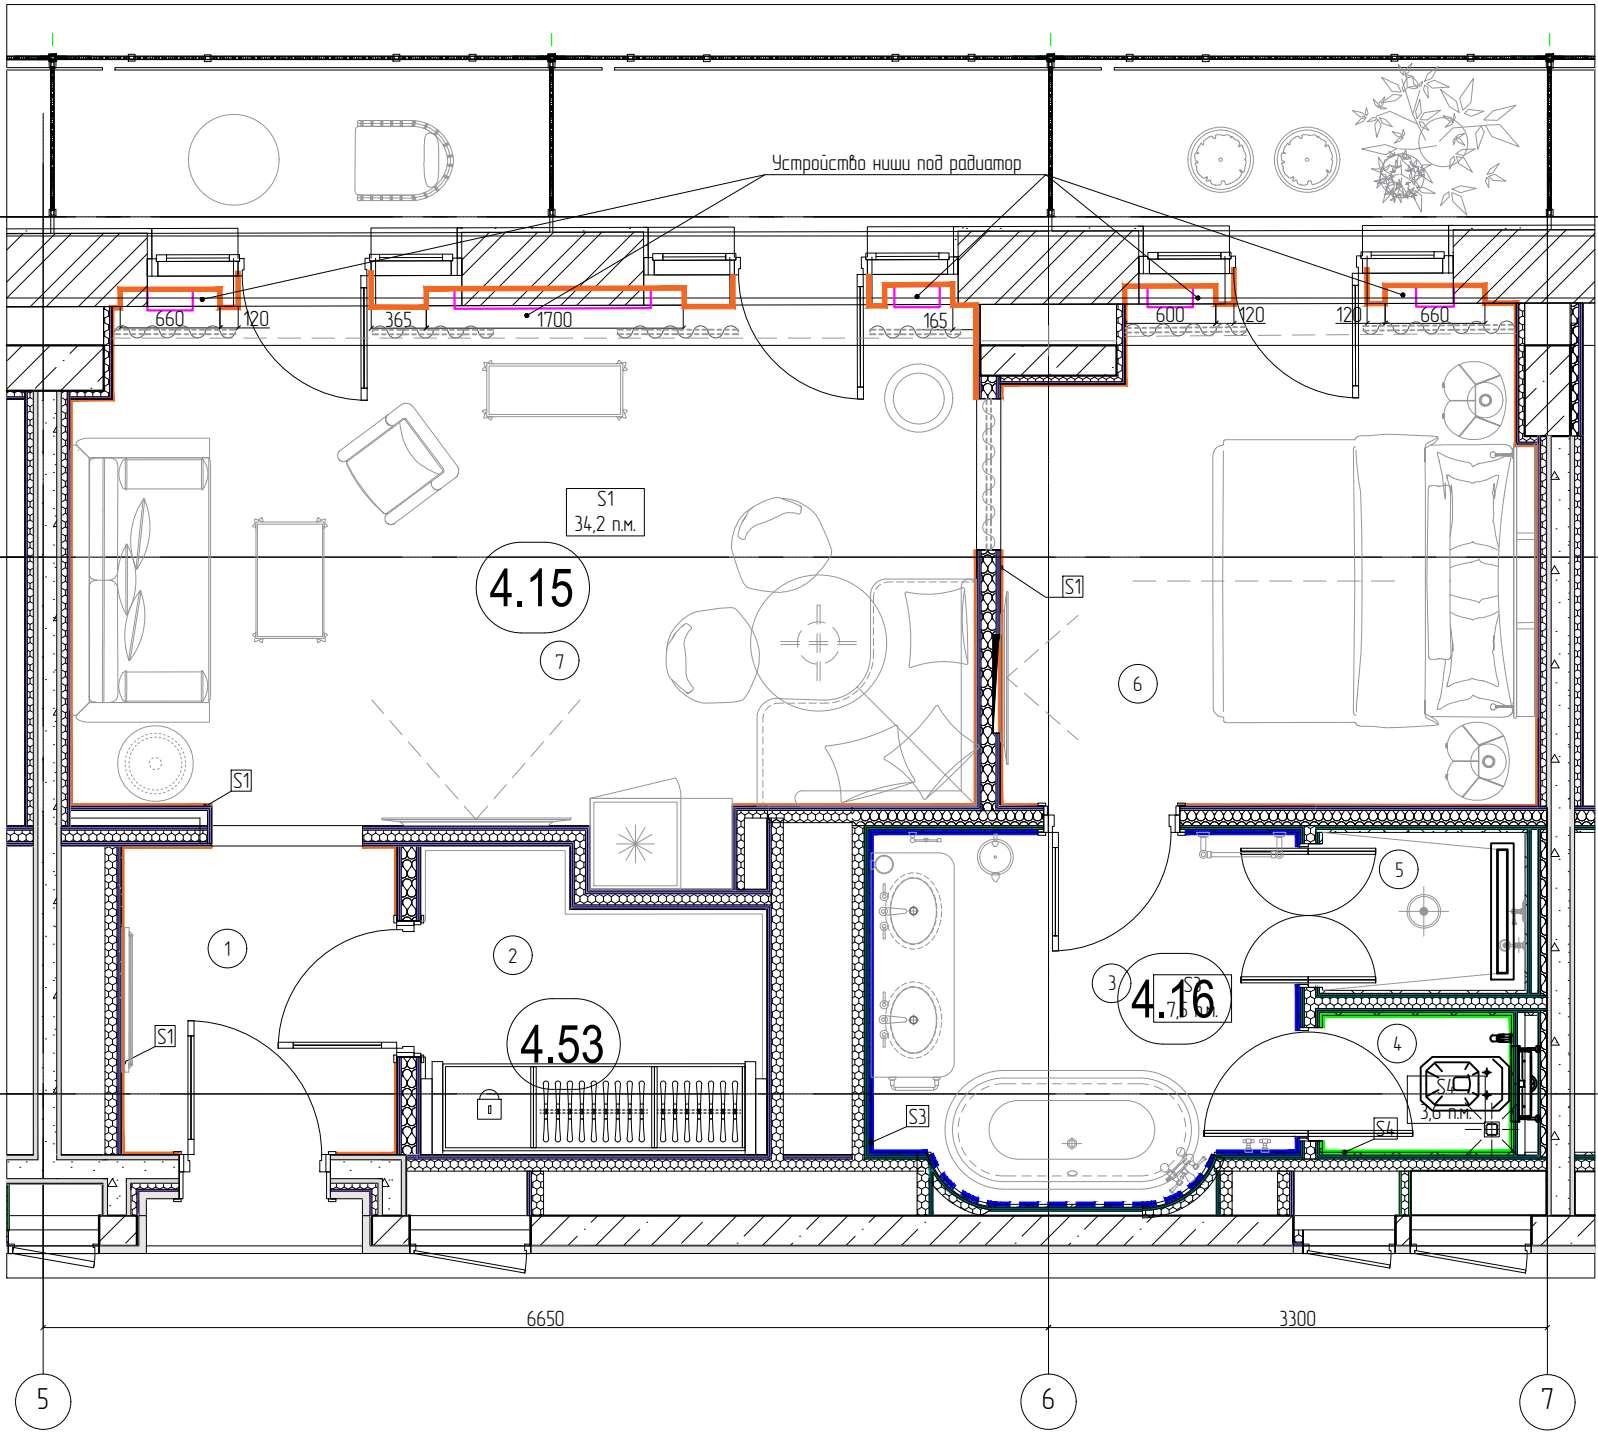

Согласовано					
Взам. инв. №					
Подп. и дата					
Инв. № подл.					


Заказчик: ООО «Приморская» Технический заказчик: АО «СЗ «ЛСР. Недвижимость – М»						ПриМ-0001/2024-АИ.01-410		
Развитие гостиницы «Приморская» в г. Сочи. Приспособление и сохранение объекта культурного наследия «Здание, где в годы Великой Отечественной войны размещались госпитали № 2095, 2120, 1941-1945 годы», расположенного по адресу: г. Сочи, Центральный район, ул. Саколова, д. 1.								
Изм.	Кол.уч.	Лист	№ док.	Подпись	Дата	Интерьерные решения. Гостиница "Приморская", корпус 1, 4 этаж, N 410. Тип "Делюкс"	Стадия	Лист
Разработал	Казыева А.Р.				02.02.26		РД	5
Проверил	Новикова Е.				02.02.26			Листов
								40
Н.контр.	Бахвалова Л.В.				02.02.26	План с указанием плинтусов. М 1:50	ООО "Арх-И-Арм"	
ГАП	Сафронова Е.				02.02.26			

- Примечания
1. Планировочное решение выполнено на основании чертежей раздела АР, ТЗ и концепции, утвержденной Заказчиком.
2. При расхождении размеров на строительной площадке, превышающих ± 40 мм, их необходимо согласовать с Архитектором. В случае расхождения размеров между мелко масштабными чертежами и детализированными необходимо руководствоваться только размерами детализированного чертежа. Не использовать фрагменты плана как шаблон.
3. За отм. чистого пола принять верх чистового покрытия коридора этажа. Палы во всех помещениях должны быть в одном уровне на отм. 0.000 (чистый пол этажа).


Лист дополнительной информации. Детализированный чертеж к плану раскладки напольных покрытий.
Детали и узлы облицовки.

4
6, 10

Деталь. ПЛАН
Подоконники

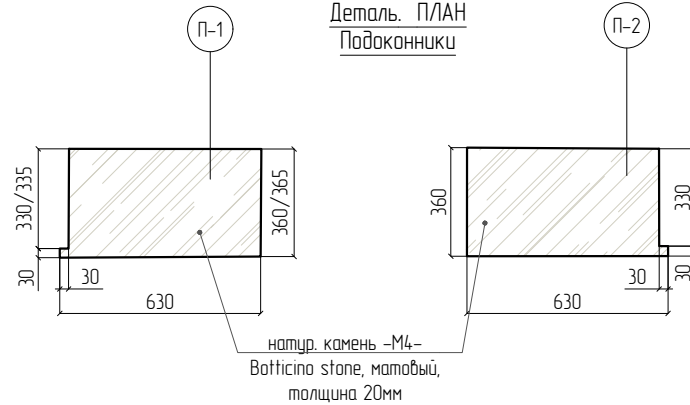


Деталь к узлу 4.
Профиль подоконника. П-1, П-2.

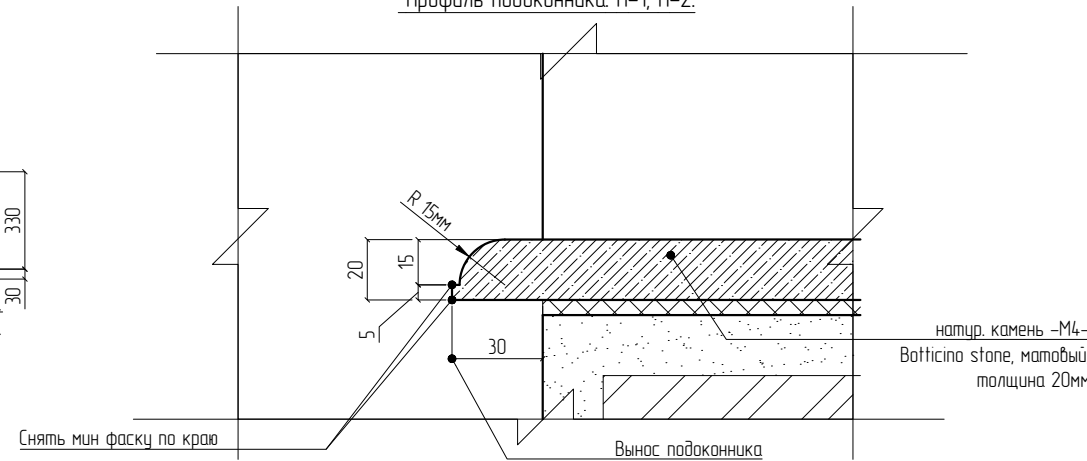


5
6


Стык напольного покрытия. Вар. профиль 1

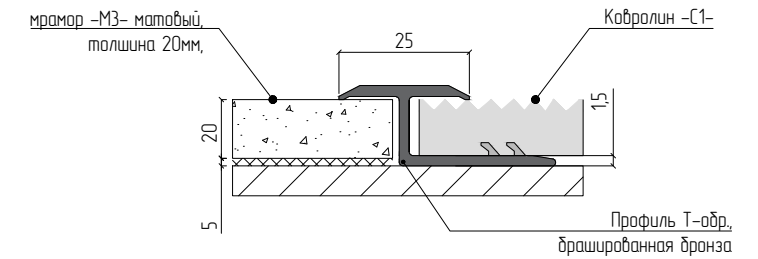


Стык напольного покрытия. Вар. профиль 2

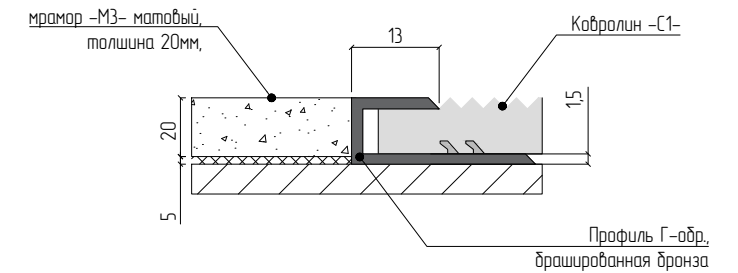

Деталь облицовки верха портала пом. N5 (душевая)
Разрез 8-8

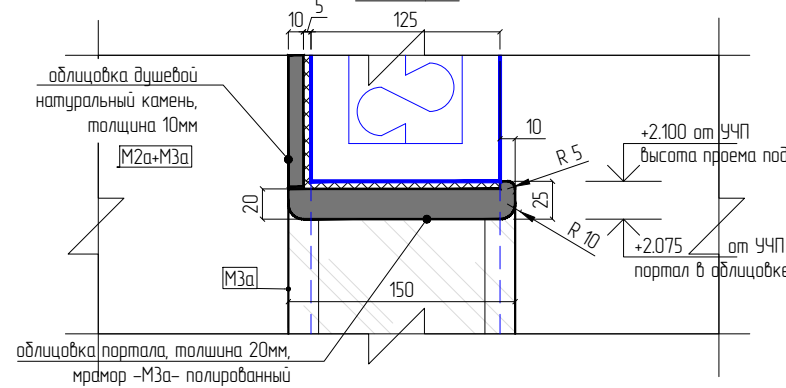


Деталь. ПЛАН
Порожек в пом. N5 (душевая)

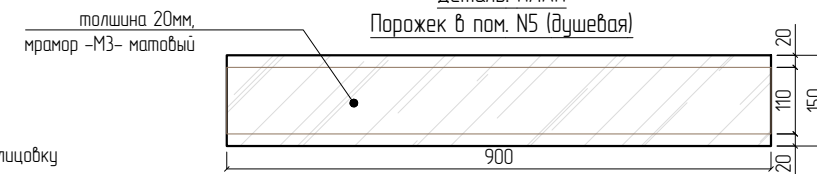


Деталь. ПЛАН
Порожек в пом. N4 (су)




Деталь облицовки портала и порожек пом. N4 (су)
Разрез 7-7

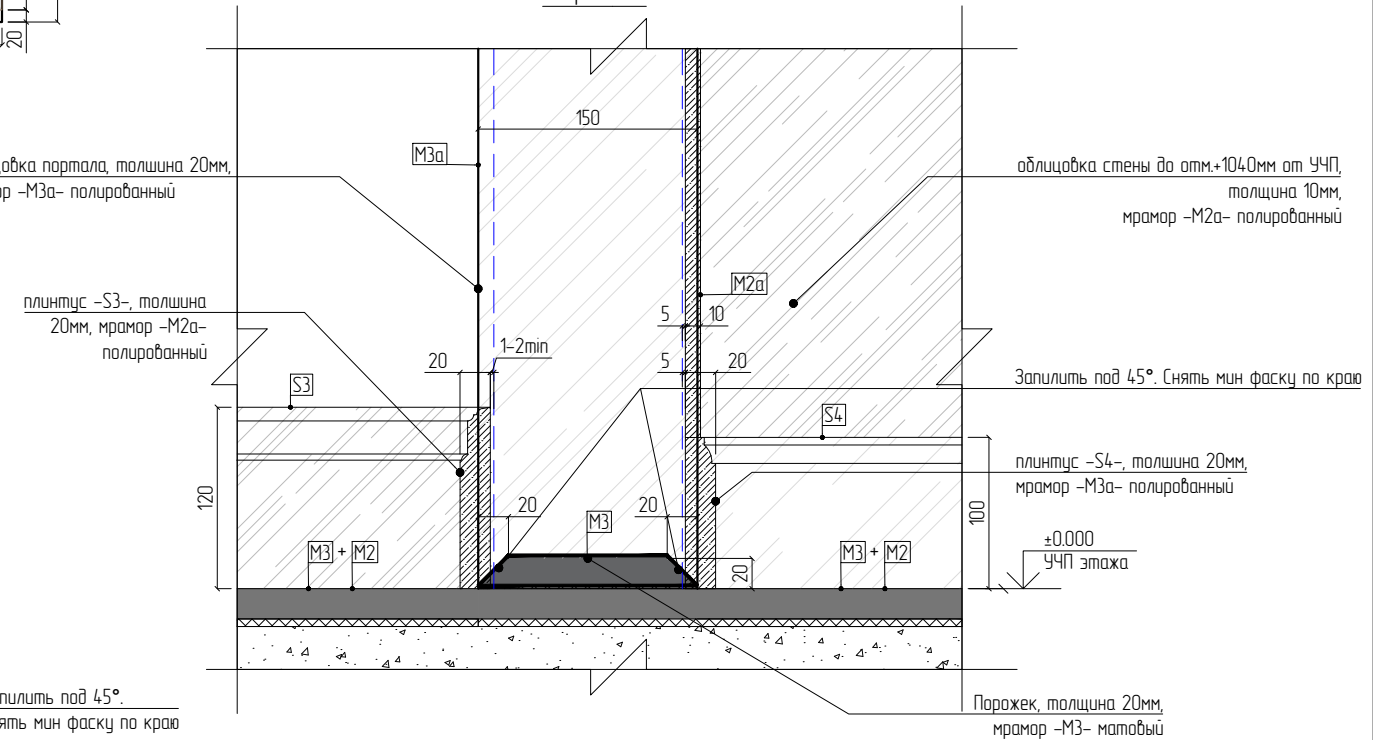

Деталь облицовки портала и порожек пом. N5 (душевая)
ПЛАН

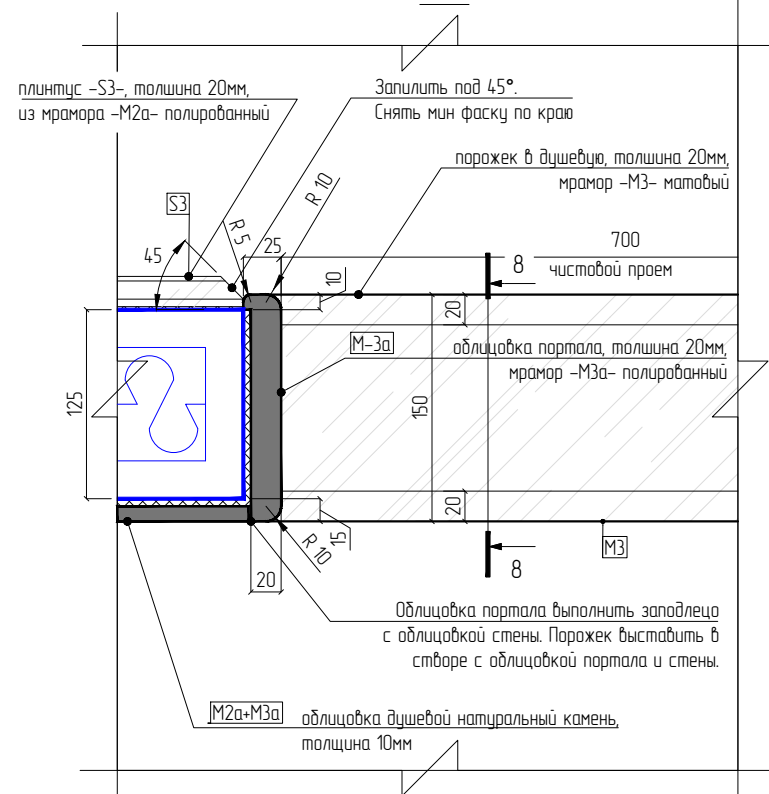



Деталь облицовки портала и порожек пом. N4 (су)
ПЛАН

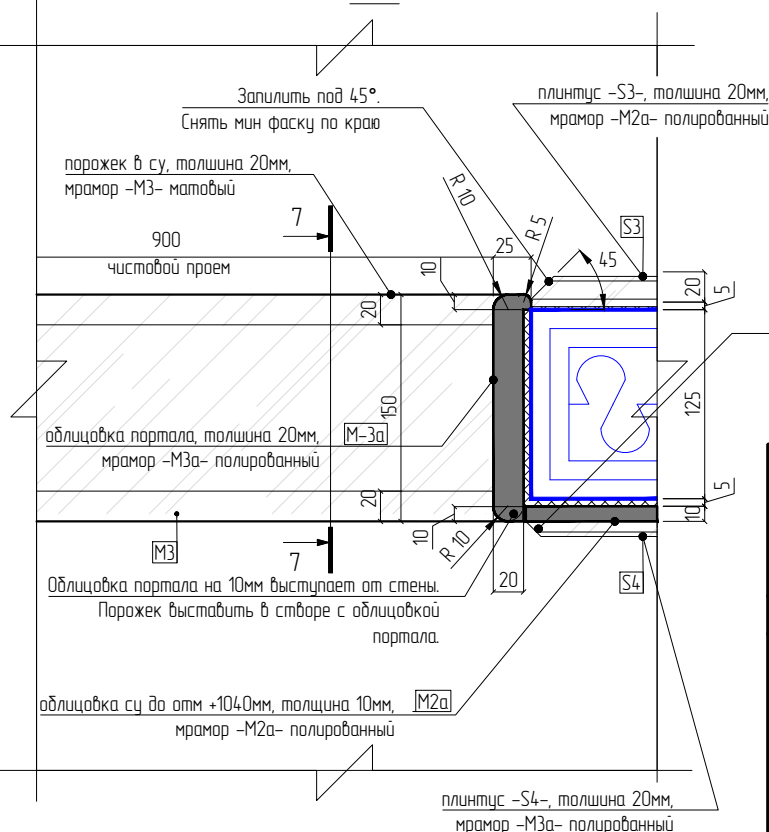

Заказчик: ООО «Приморская» Технический заказчик: АО «СЗ «ЛСР. Недвижимость – М»						ПриМ-0001/2024-АИ.01-410		
Развитие гостиницы «Приморская» в г. Сочи. Приспособление и сохранение объекта культурного наследия «Здание, где в годы Великой Отечественной войны размещались госпитали № 2095, 2120, 1941-1945 годы», расположенного по адресу: г. Сочи, Центральный район, ул. Саколова, д. 1.						Интерьерные решения. Гостиница «Приморская», корпус 1, 4 этаж, N 410. Тип «Делюкс»		
Изм.	Кол.уч.	Лист	№ док.	Подпись	Дата	РД	6	40
Разработал	Казыева А.Р.	02.02.26				ООО «Арх-И-Арт»		
Проверил	Нобикова Е.	02.02.26						
Н.контр.	Бахвалова Л.В.	02.02.26				Детализированный чертеж к плану раскладки напольных покрытий. Детали и узлы облицовки. Узел 4, 5, 6 М 1:25		
ГАП	Сафронова Е.	02.02.26						

План теплого пола.
Корпус 1, 4 этаж, N 410. Тип "Делюкс"

Экспликация помещений		
№	Наименование	Площадь м2
1	Прихожая	3,74
2	Гардеробная комната	4,18
3	Ванная комната	6,77
4	Санузел	12
5	Душевая	1,56
6	Спальная комната	10,45
7	Гостиная комната	19,37
S общая		47,3

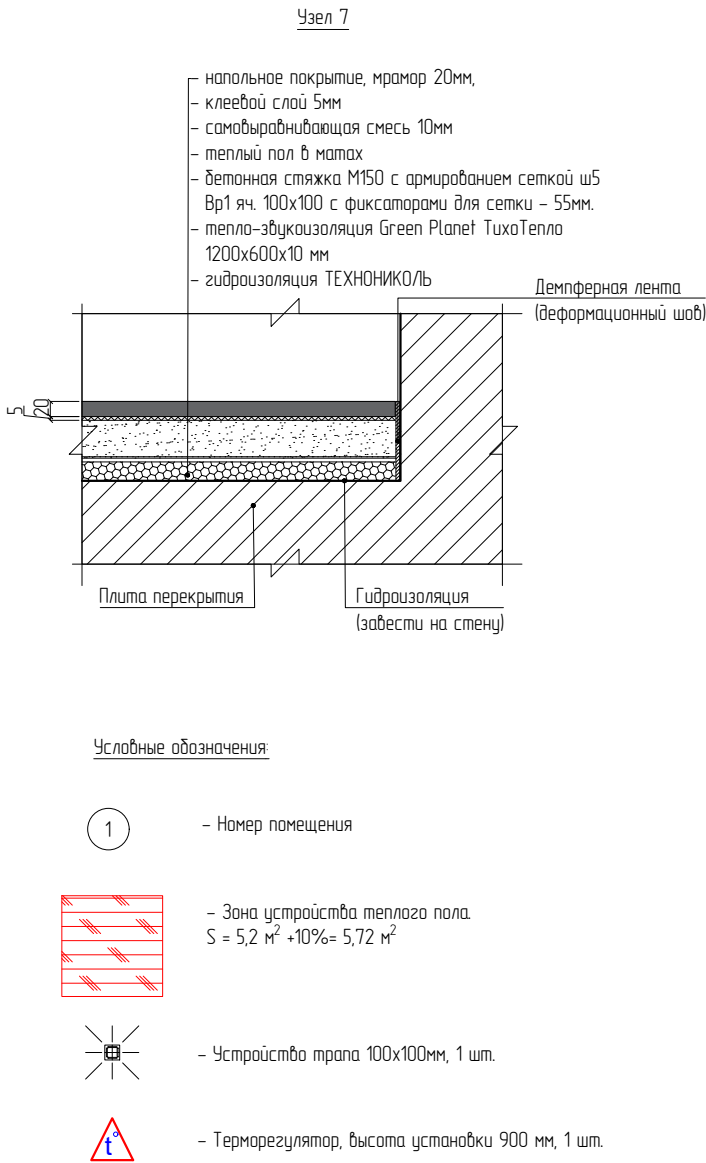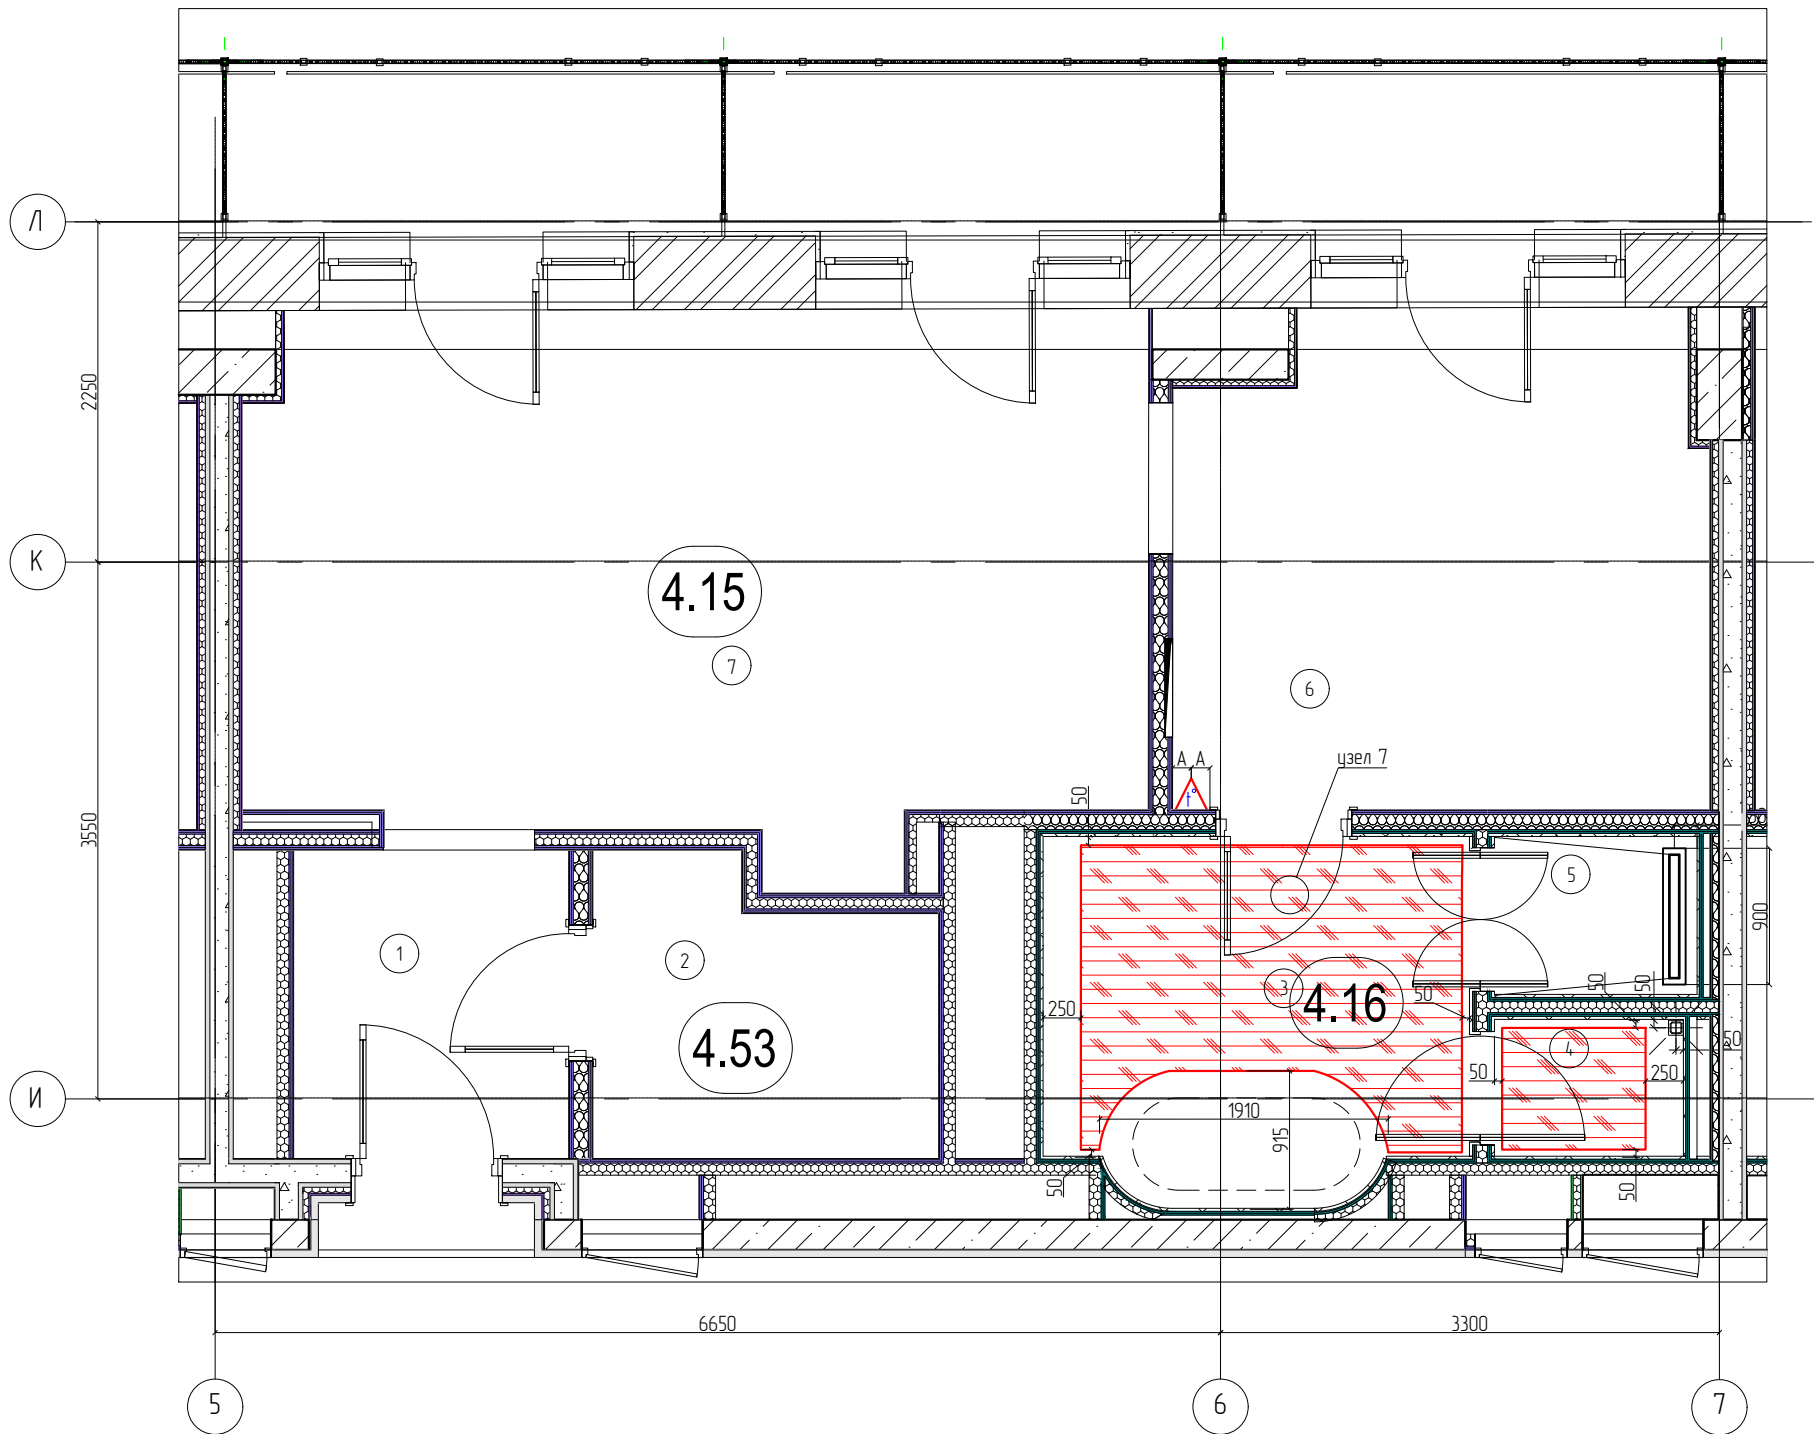

Согласовано					
Взам. инв. №					
Подп. и дата					
Инв. № подл.					

Заказчик: ООО «Приморская»						ПриМ-0001/2024-АИ.01-410		
Технический заказчик: АО «СЗ «ЛСР. Недвижимость – М»								
Развитие гостиницы «Приморская» в г. Сочи. Приспособление и сохранение объекта культурного наследия «Здание, где в годы Великой Отечественной войны размещались госпитали № 2095, 2120, 1941-1945 годы», расположенного по адресу: г. Сочи, Центральный район, ул. Соколова, д. 1.								
Изм.	Кол.уч.	Лист	№ док.	Подпись	Дата	Интерьерные решения. Гостиница "Приморская", корпус 1, 4 этаж, N 410. Тип "Делюкс"	Стадия	Лист
Разработал	Казыева А.Р.				02.02.26		РД	7
Проверил	Нобикова Е.				02.02.26			Листов
								40
Н.контр.	Бахвалова Л.В.				02.02.26	План теплого пола. Узел 7. М 1:50	ООО "Арх-И-Арм"	
ГАП	Сафронова Е.				02.02.26			


- Примечания
1. Планировочное решение выполнено на основании чертежей раздела АР, ТЗ и концепции, утвержденной Заказчиком.
 2. При расхождении размеров на строительной площадке, превышающих ± 40 мм, их необходимо согласовать с Архитектором. В случае расхождения размеров между мелко масштабными чертежами и детализированными необходимо руководствоваться только размерами детализированного чертежа. Не использовать фрагменты плана как шаблон.
 3. Высоты даны от уровня чистого пола этажа. За отм. чистого пола принять верх чистового покрытия коридора.
 4. Заложить устройство теплых полов с учетом установки трапов и разуклонки помещений.
 5. При необходимости установки температурного датчика, его расположение согласовать Дизайнерами.
 6. Регулировка тем-ры и вкл/выкл. "теплых полов" осуществляется централизованно через автоматизацию или индивидуально на усмотрение Заказчика.

План заполнения дверных проемов.
Корпус 1, 4 этаж, N 410. Тип "Делюкс"

Условные обозначения:

- 1 - Номер помещения
- Д-1 Нпр 2370 мм - Высота проема в чистоте
- Маркировка двери

Экспликация помещений		
№	Наименование	Площадь м2
1	Прихожая	3,74
2	Гардеробная комната	4,18
3	Ванная комната	6,77
4	Санузел	1,2
5	Душевая	1,56
6	Спальная комната	10,45
7	Гостиная комната	19,37
Σ общая		47,3

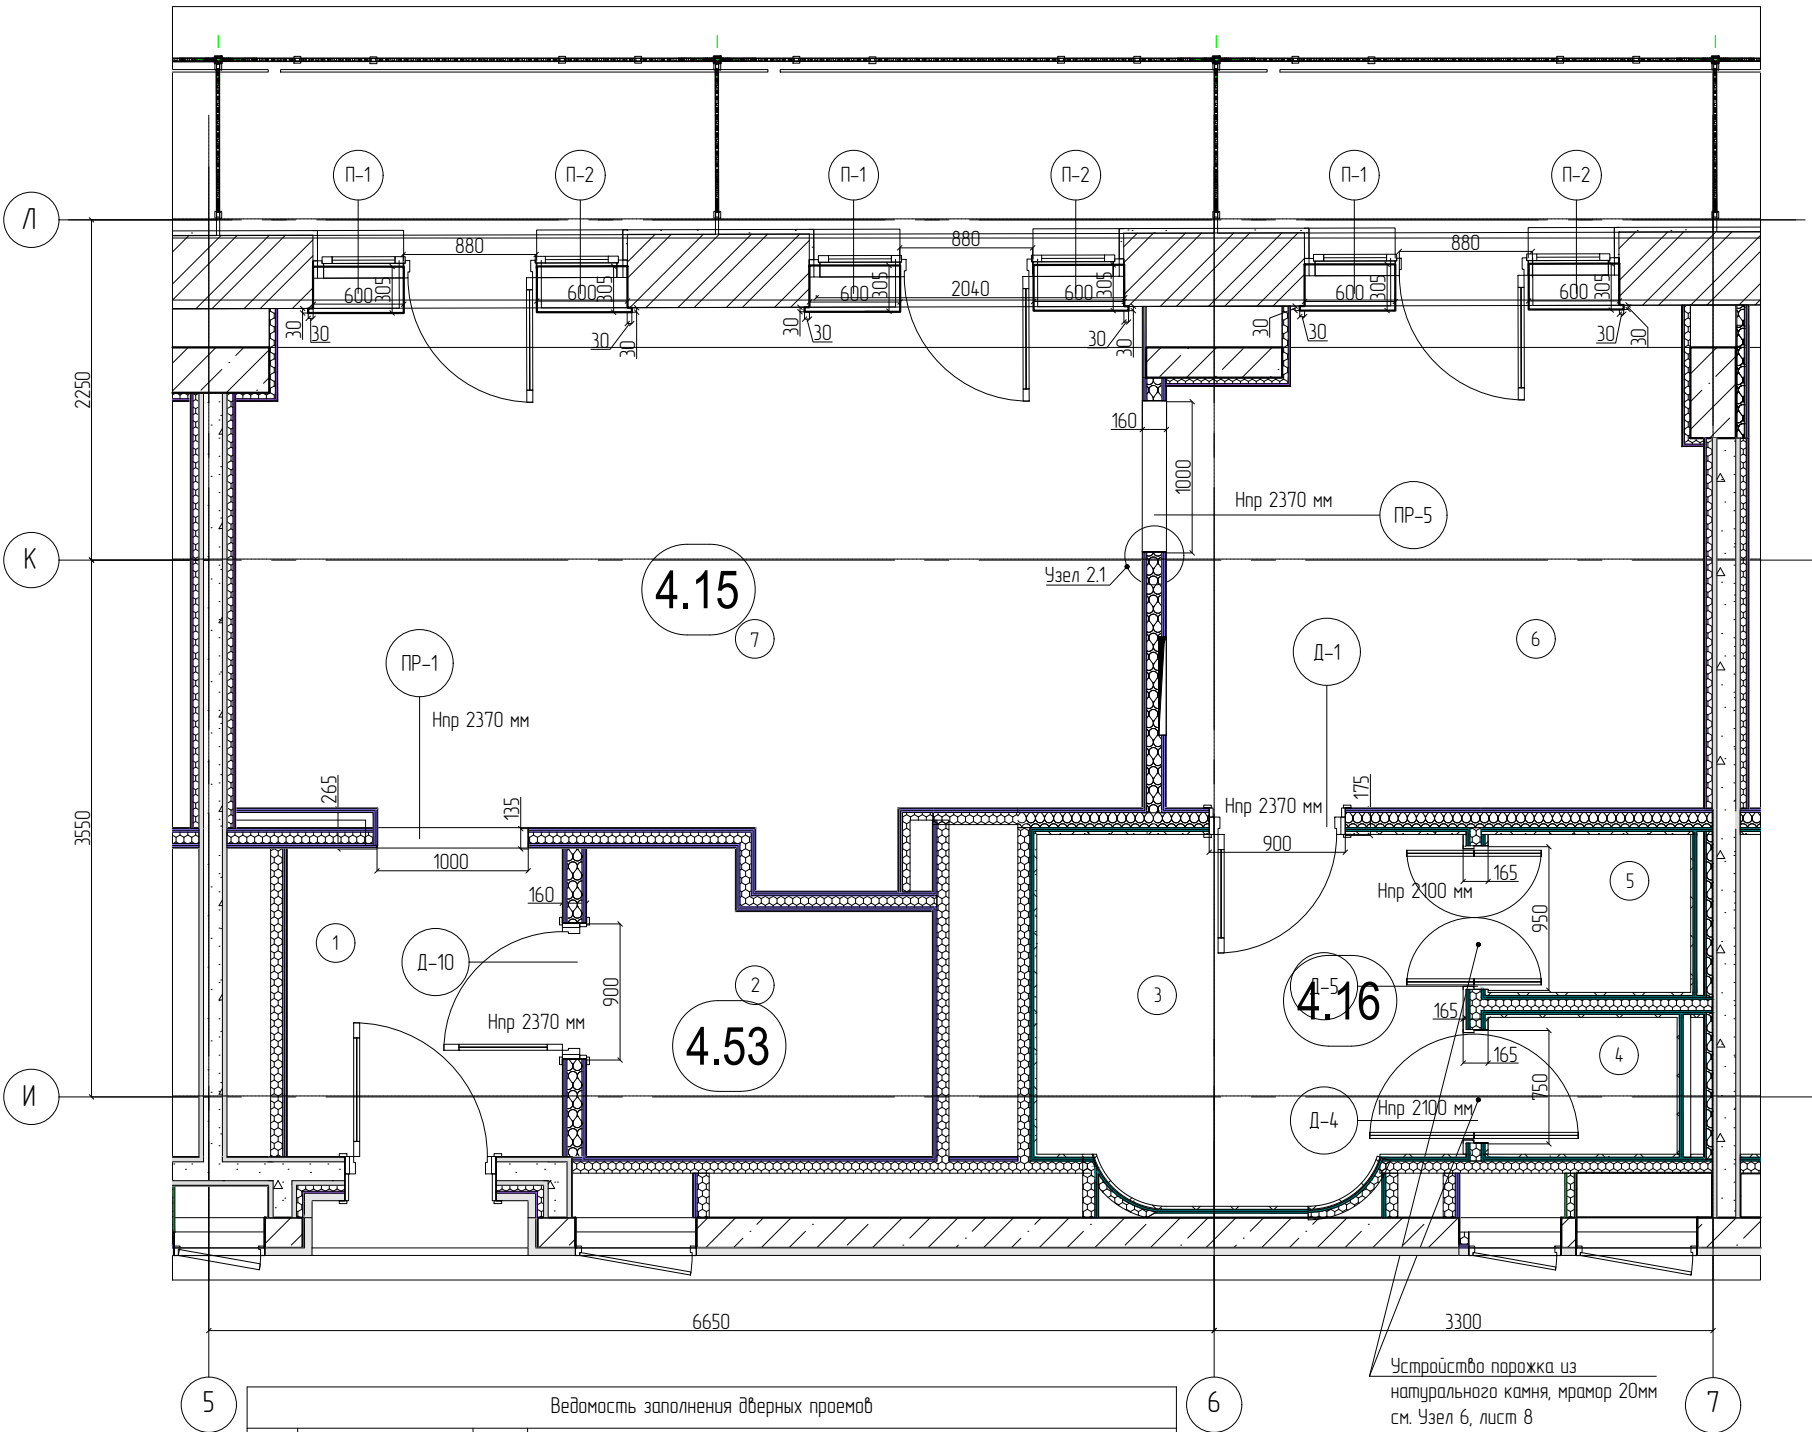


Ведомость заполнения дверных проемов									
№	Размеры по проему			Размеры полотна			Кол-во	Примечание	
	L	H	W	L	H	W			
Д-1	900	2370	175	800	2300	40 (50)	1	Распашная однополосная дверь правая. МДФ, шпон : Ash flowered sea wood/аналог ясень дальневосточный, распил тангенсальный. Фигурный наличник с двух сторон. Петли скрытые. Ручка: Dauby PH1920 /White bronze.	
Д-10	900	2370	160	800	2300	40 (50)	1	Распашная однополосная дверь правая. МДФ, шпон : Ash flowered sea wood/аналог ясень дальневосточный, распил тангенсальный. Фигурный наличник с двух сторон. Петли скрытые. Ручка: Dauby PH1920 /White bronze.	
Д-4	750 (под облицовку)	2100 (под облицовку)	165	700	1900	-	1	Цельностеклянная маятниковая одностворчатая дверь (правое открывание) без обрамления L700xH1900мм: закаленное безопасное текстурированное стекло -12мм DESIGN BY LG, петли и ручки: Old bronze patinated/White bronze finish. Порта в облицовке L700xH2055(верх облицовки)xW160мм: натуральный камень -M3- Calacata Borghini marble, полированный 20мм. Порог L700xH20xW160мм: натуральный камень -M3- Calacata Borghini marble, матовый, толщина 20мм, углы зашлифовать под 45°.	
Д-5	950 (под облицовку)	2100 (под облицовку)	165	900	1900	-	1	Цельностеклянная маятниковая двухстворчатая дверь без обрамления L900xH1900мм: закаленное безопасное текстурированное стекло -12мм DESIGN BY LG, заполировать кромку и снять по краю мин. фасет, петли и ручки: Old bronze patinated/White bronze finish. Порта в облицовке L900xH2055(верх облицовки)xW150мм: натуральный камень -M3- Calacata Borghini marble, полированный 20мм. Порог L900xH20xW150мм: натуральный камень -M3- Calacata Borghini marble, матовый, толщина 20мм, углы зашлифовать под 45°.	
ПР-5	1000	2370	160				1	Порта в облицовке (со встроенным профилем для шторы) L950xH2300xW200мм: натуральный камень -M1- Breccia Carpaia marble, полированный 20мм. Наличники с двух сторон L100ммxH2400xW30мм: натуральный камень -M1- Breccia Carpaia marble, полированный, толщина 30мм с закруглением, углы на стыке с портом зашлифовать под 45°. Цоколь портала и наличника: натуральный камень -M1- Breccia Carpaia marble, полированный, толщина 35мм, ширина 110мм.	


Ведомость заполнения дверных проемов						
№	Размеры по проему			Кол-во	Примечание	
	L	H	W			
ПР-1	1000	2370	135	1	Обрамление проема без заполнения. МДФ, шпон : Ash flowered sea wood/ аналог ясень дальневосточный, распил тангенсальный. Фигурный наличник с двух сторон.	
П-1	600*	305*	20	2	- Подоконник из натур. камня -M4- Botticino stone, матовый, толщина 20мм	
П-2	600*	305*	20	2	- Подоконник из натур. камня -M4- Botticino stone, матовый, толщина 20мм	
П-3	2040*	340*	20	1	- Подоконник из натур. камня -M4- Botticino stone, матовый, толщина 20мм	

Примечания

1. Планировочное решение выполнено на основании чертежей раздела АР, ТЗ и концепции, утвержденной Заказчиком.
2. При расхождении размеров на строительной площадке, превышающих ± 40 мм, их необходимо согласовать с Архитектором. В случае расхождения размеров между мелко масштабными чертежами и детализированными необходимо руководствоваться только размерами детализированного чертежа. Не использовать фрагменты плана как шаблон.
3. За отм. чистого пола принять верх чистового покрытия коридора этажа.
4. В ведомости заполнения дверных проемов даны ширина стен без учета отделки. Перед заказом дверей произвести контрольный замер проемов.
5. См. совместно с детализированным чертежом: План, вид и разрез: Д-1, Д-2. Виды и разрезы по ПР-1. Узел 2.
6. Расположение и кол-во подоконников не определено, возможны изменения конфигурации оконных проемов согласно АР в части фасады и оконные проемы.
7. Габаритные размеры подоконников выданы по проектным размерам. Заказ готовых изделий произвести после дополнительного замера силами фирм производителей.


 
						Заказчик: ООО «Приморская» Технический заказчик: АО «СЗ «ЛСР. Недвижимость – М»			ПриМ-0001/2024-АИ.01-410			
						Развитие гостиницы «Приморская» в г. Сочи. Приспособление и сохранение объекта культурного наследия «Здание, где в годы Великой Отечественной войны размещались госпитали № 2095, 2120, 1941-1945 годы», расположенного по адресу: г. Сочи, Центральный район, ул. Соколова, д. 1.						
Изм.	Кол.уч.	Лист	№ док.	Подпись	Дата	Интерьерные решения. Гостиница “Приморская”, корпус 1, 4 этаж, N 410. Тип “Делюкс”			Стадия	Лист	Листов	
Разработал		Казыева А.Р.			02.02.26				РД	8	40	
Проверил		Новикова Е.			02.02.26							
						План заполнения дверных проемов. М 1:50			ООО “Арх-И-Арм”			
Н.контр.		Бахвалова Л.В.			02.02.26							
ГАП		Сафронова Е.			02.02.26							

Лист дополнительной информации.
Детализированный чертеж к плану заполнения дверных проемов.

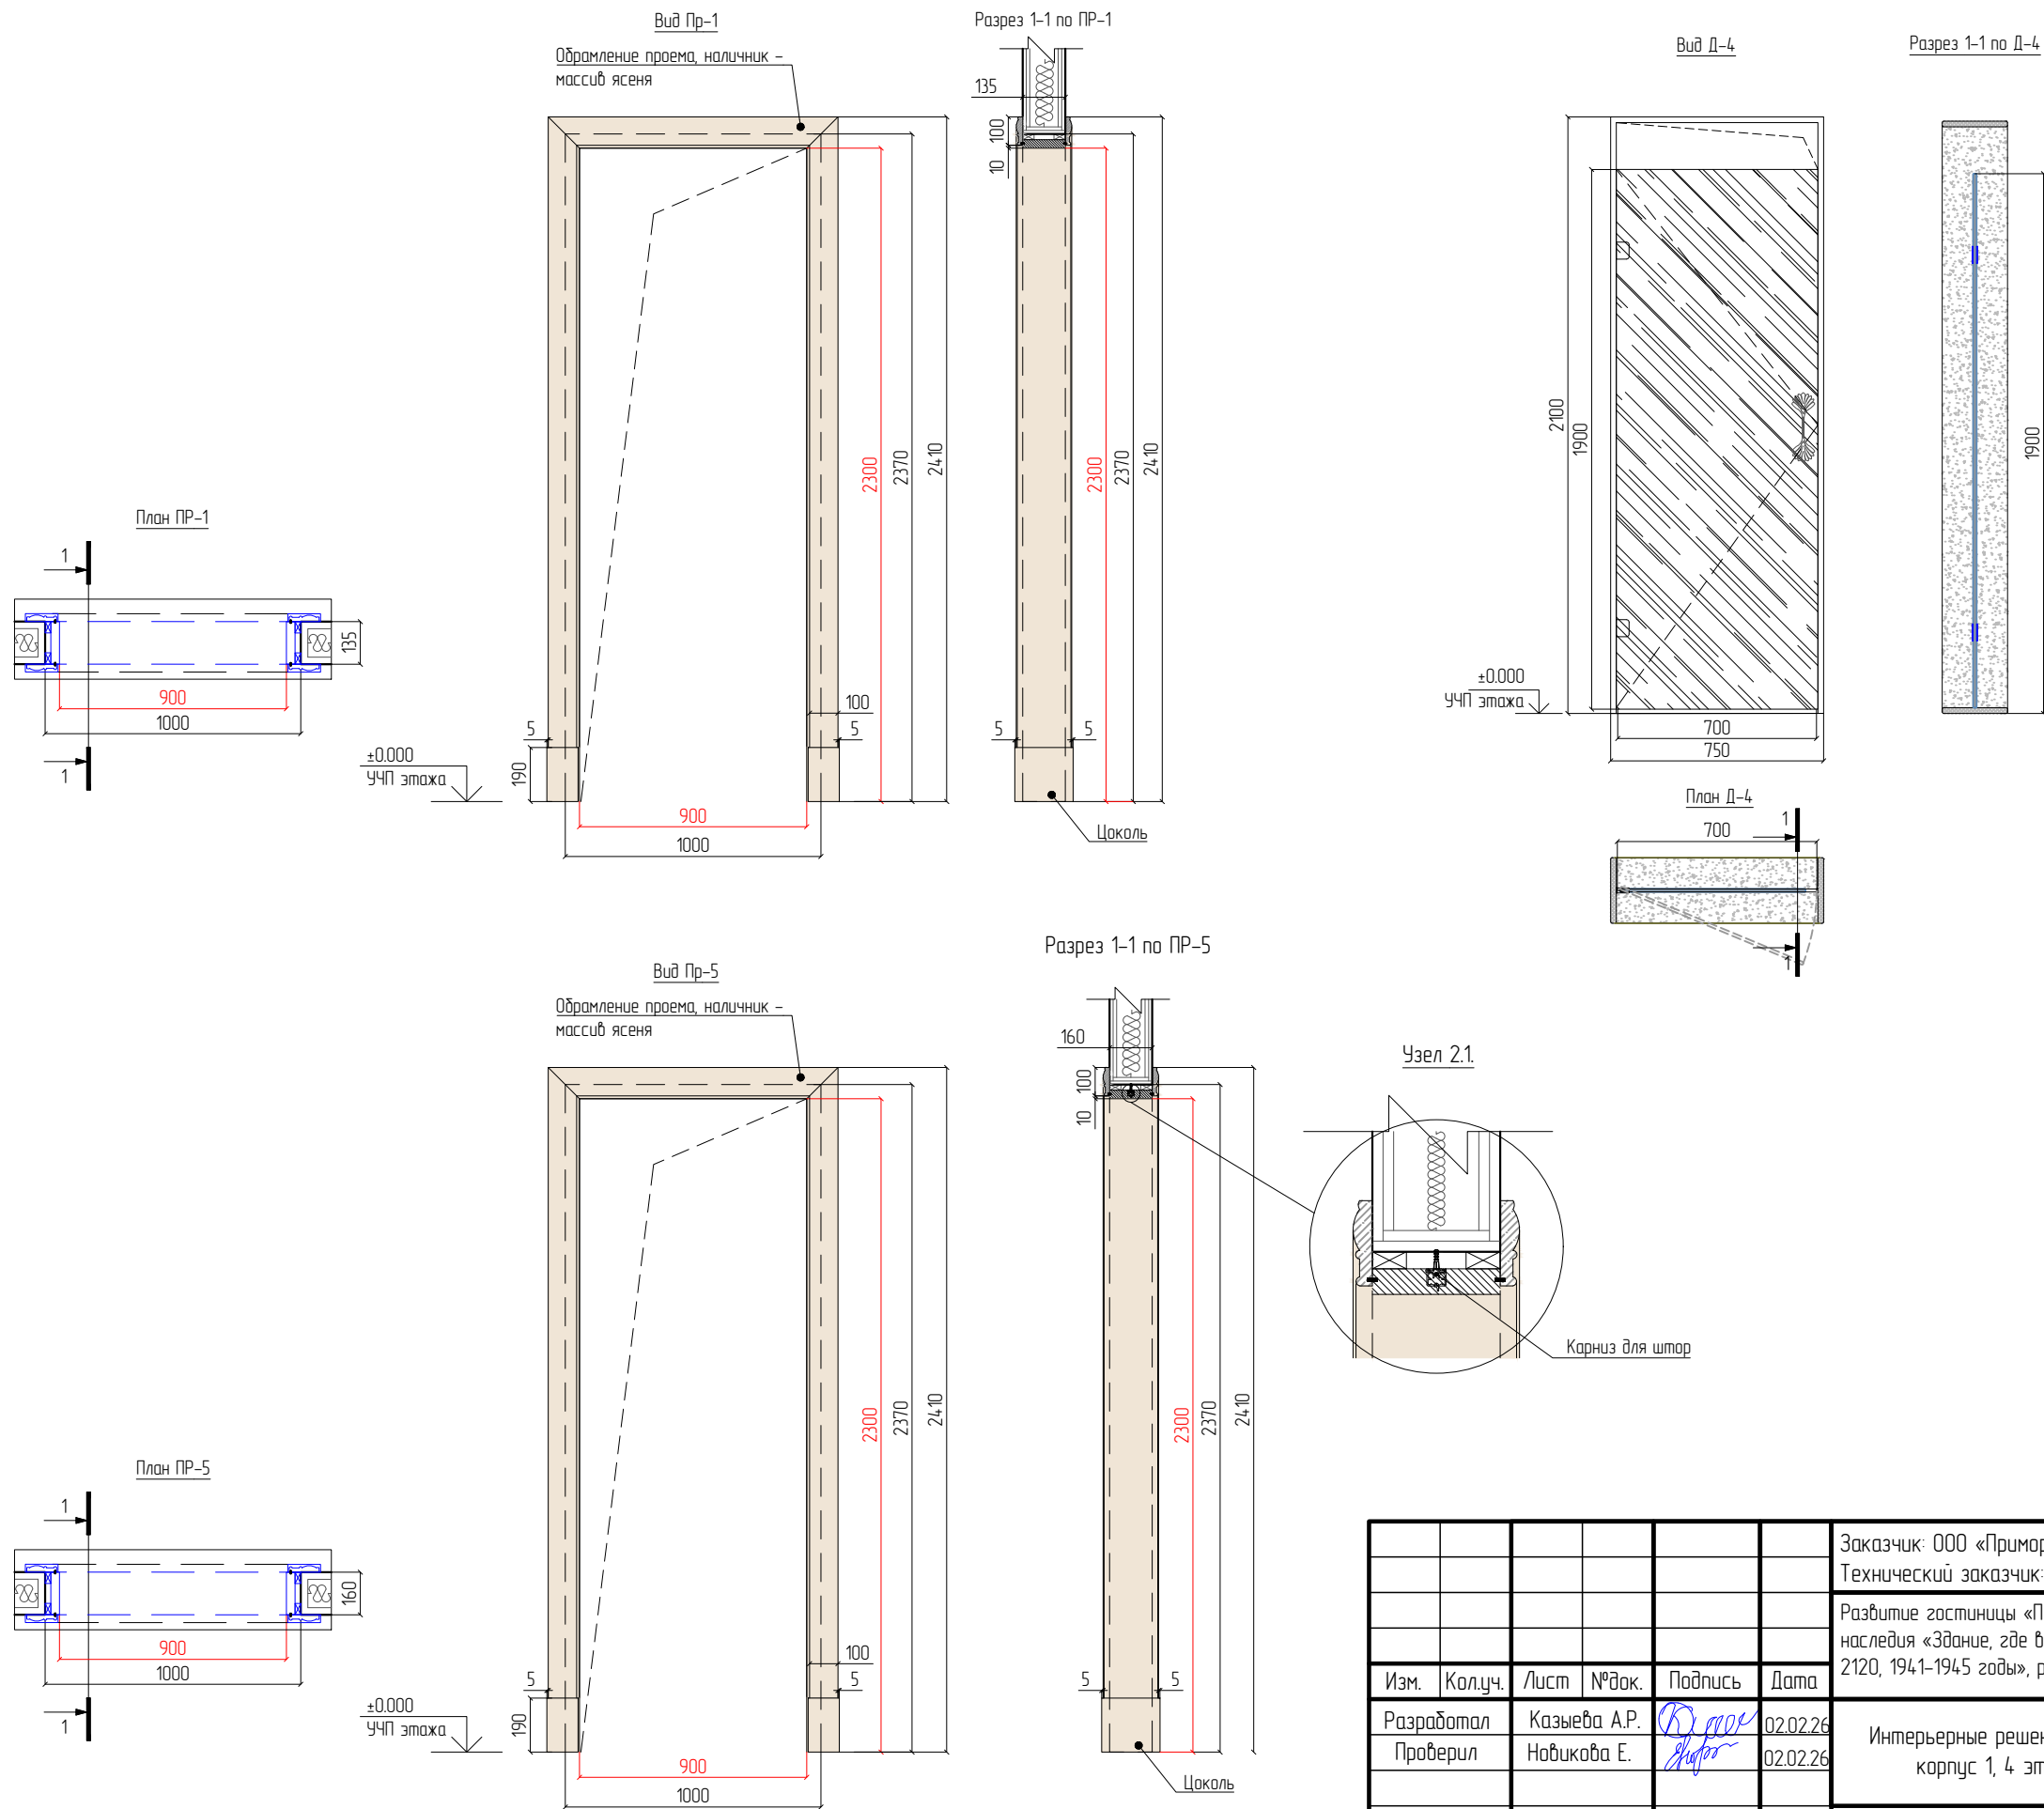


Заказчик: ООО «Приморская»						ПриМ-0001/2024-АИ.01-410		
Технический заказчик: АО «СЗ «ЛСР. Недвижимость - М»								
Развитие гостиницы «Приморская» в г. Сочи. Приспособление и сохранение объекта культурного наследия «Здание, где в годы Великой Отечественной войны размещались госпитали № 2095, 2120, 1941-1945 годы», расположенного по адресу: г. Сочи, Центральный район, ул. Саколова, д. 1.								
Изм.	Кол.уч.	Лист	№ док.	Подпись	Дата	Интерьерные решения. Гостиница "Приморская", корпус 1, 4 этаж, N 410. Тип "Делюкс"	Стадия	Лист
Разработал	Казыева А.Р.				02.02.26		РД	9
Проверил	Новикова Е.				02.02.26			40
						Детализированный чертеж к плану заполнения дверных проемов. Лист 1.	ООО "Арх-И-Арм"	
Н.контр.	Бахвалова Л.В.				02.02.26			
ГАП	Сафронова Е.				02.02.26			

Инф. № подл.	Подп. и дата	Взам. инф. №	Согласовано			

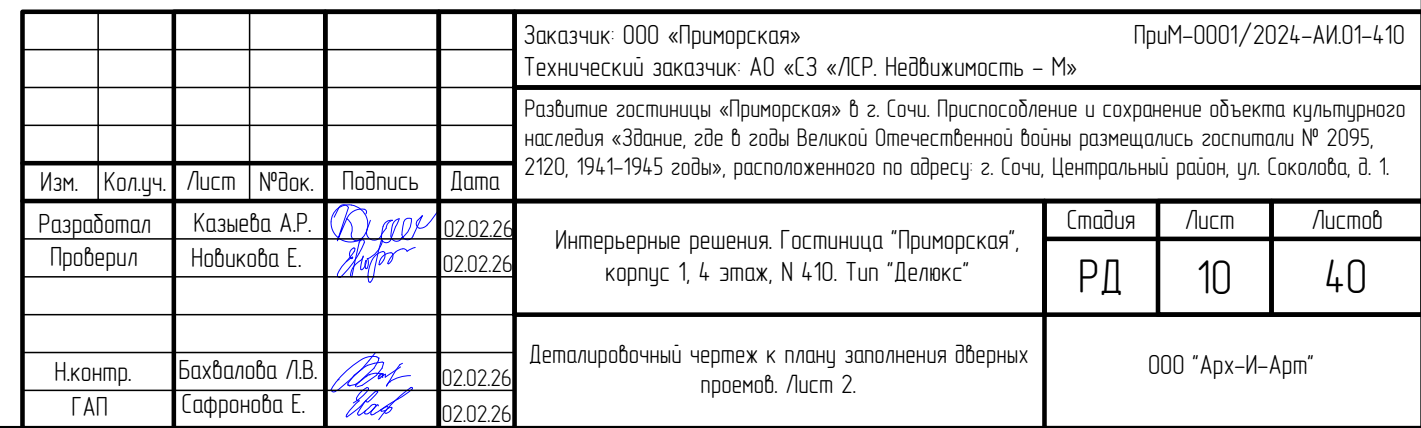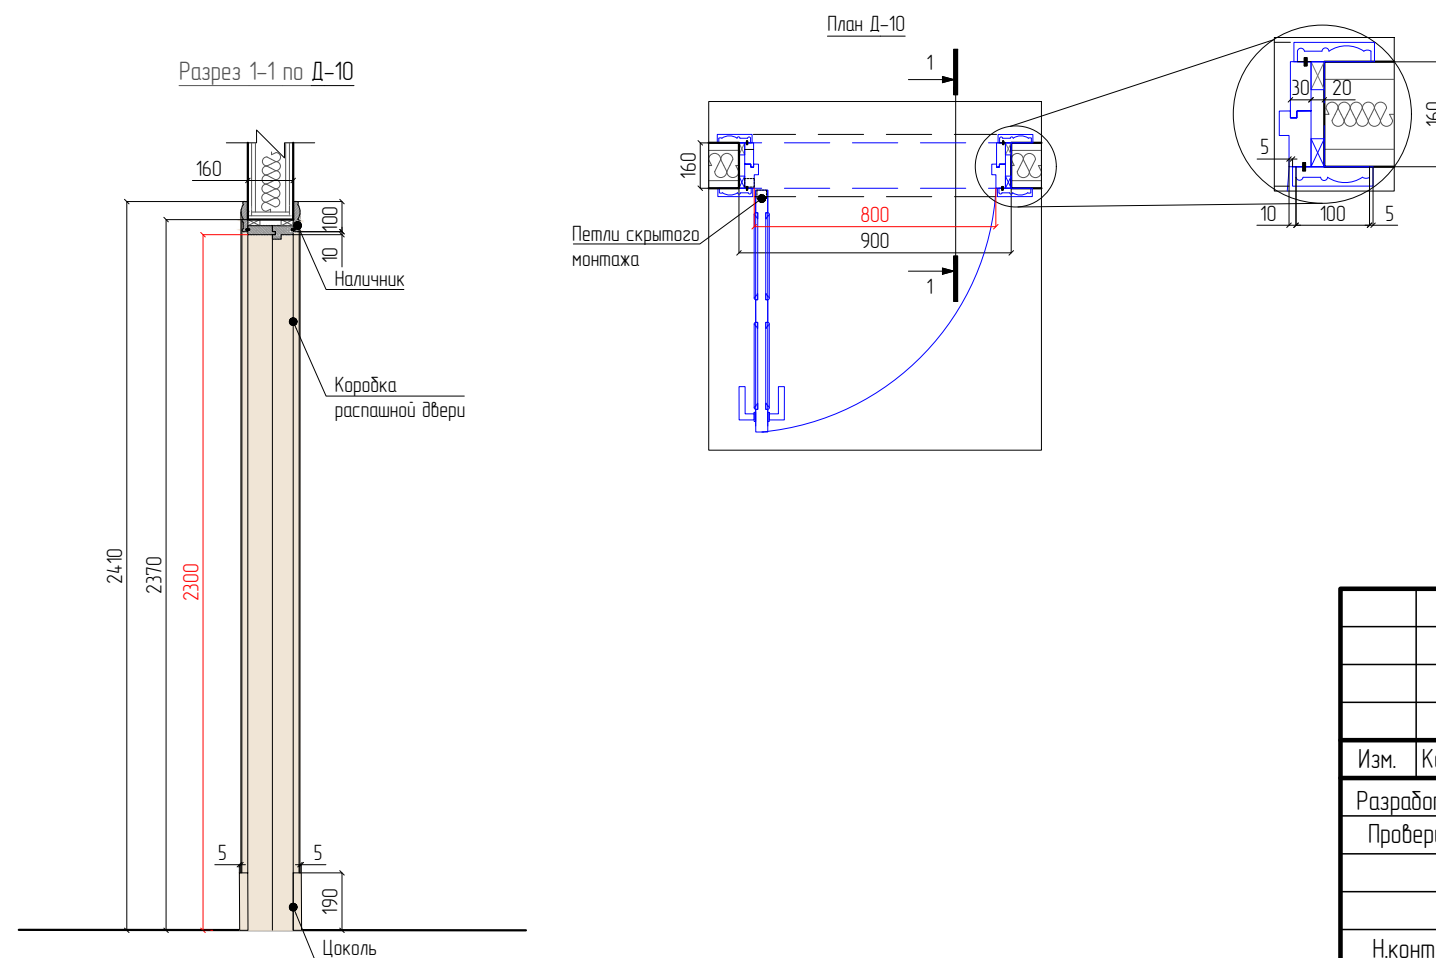

План расположения розеток и выключателей. Лист 1.
Корпус 1, 4 этаж, N 410. Тип "Делюкс"

Экспликация помещений		
№	Наименование	Площадь м2
1	Прихожая	3,74
2	Гардеробная комната	4,18
3	Ванная комната	6,77
4	Санузел	12
5	Душевая	156
6	Спальная комната	10,45
7	Гостиная комната	19,37
Σ общая		47,3

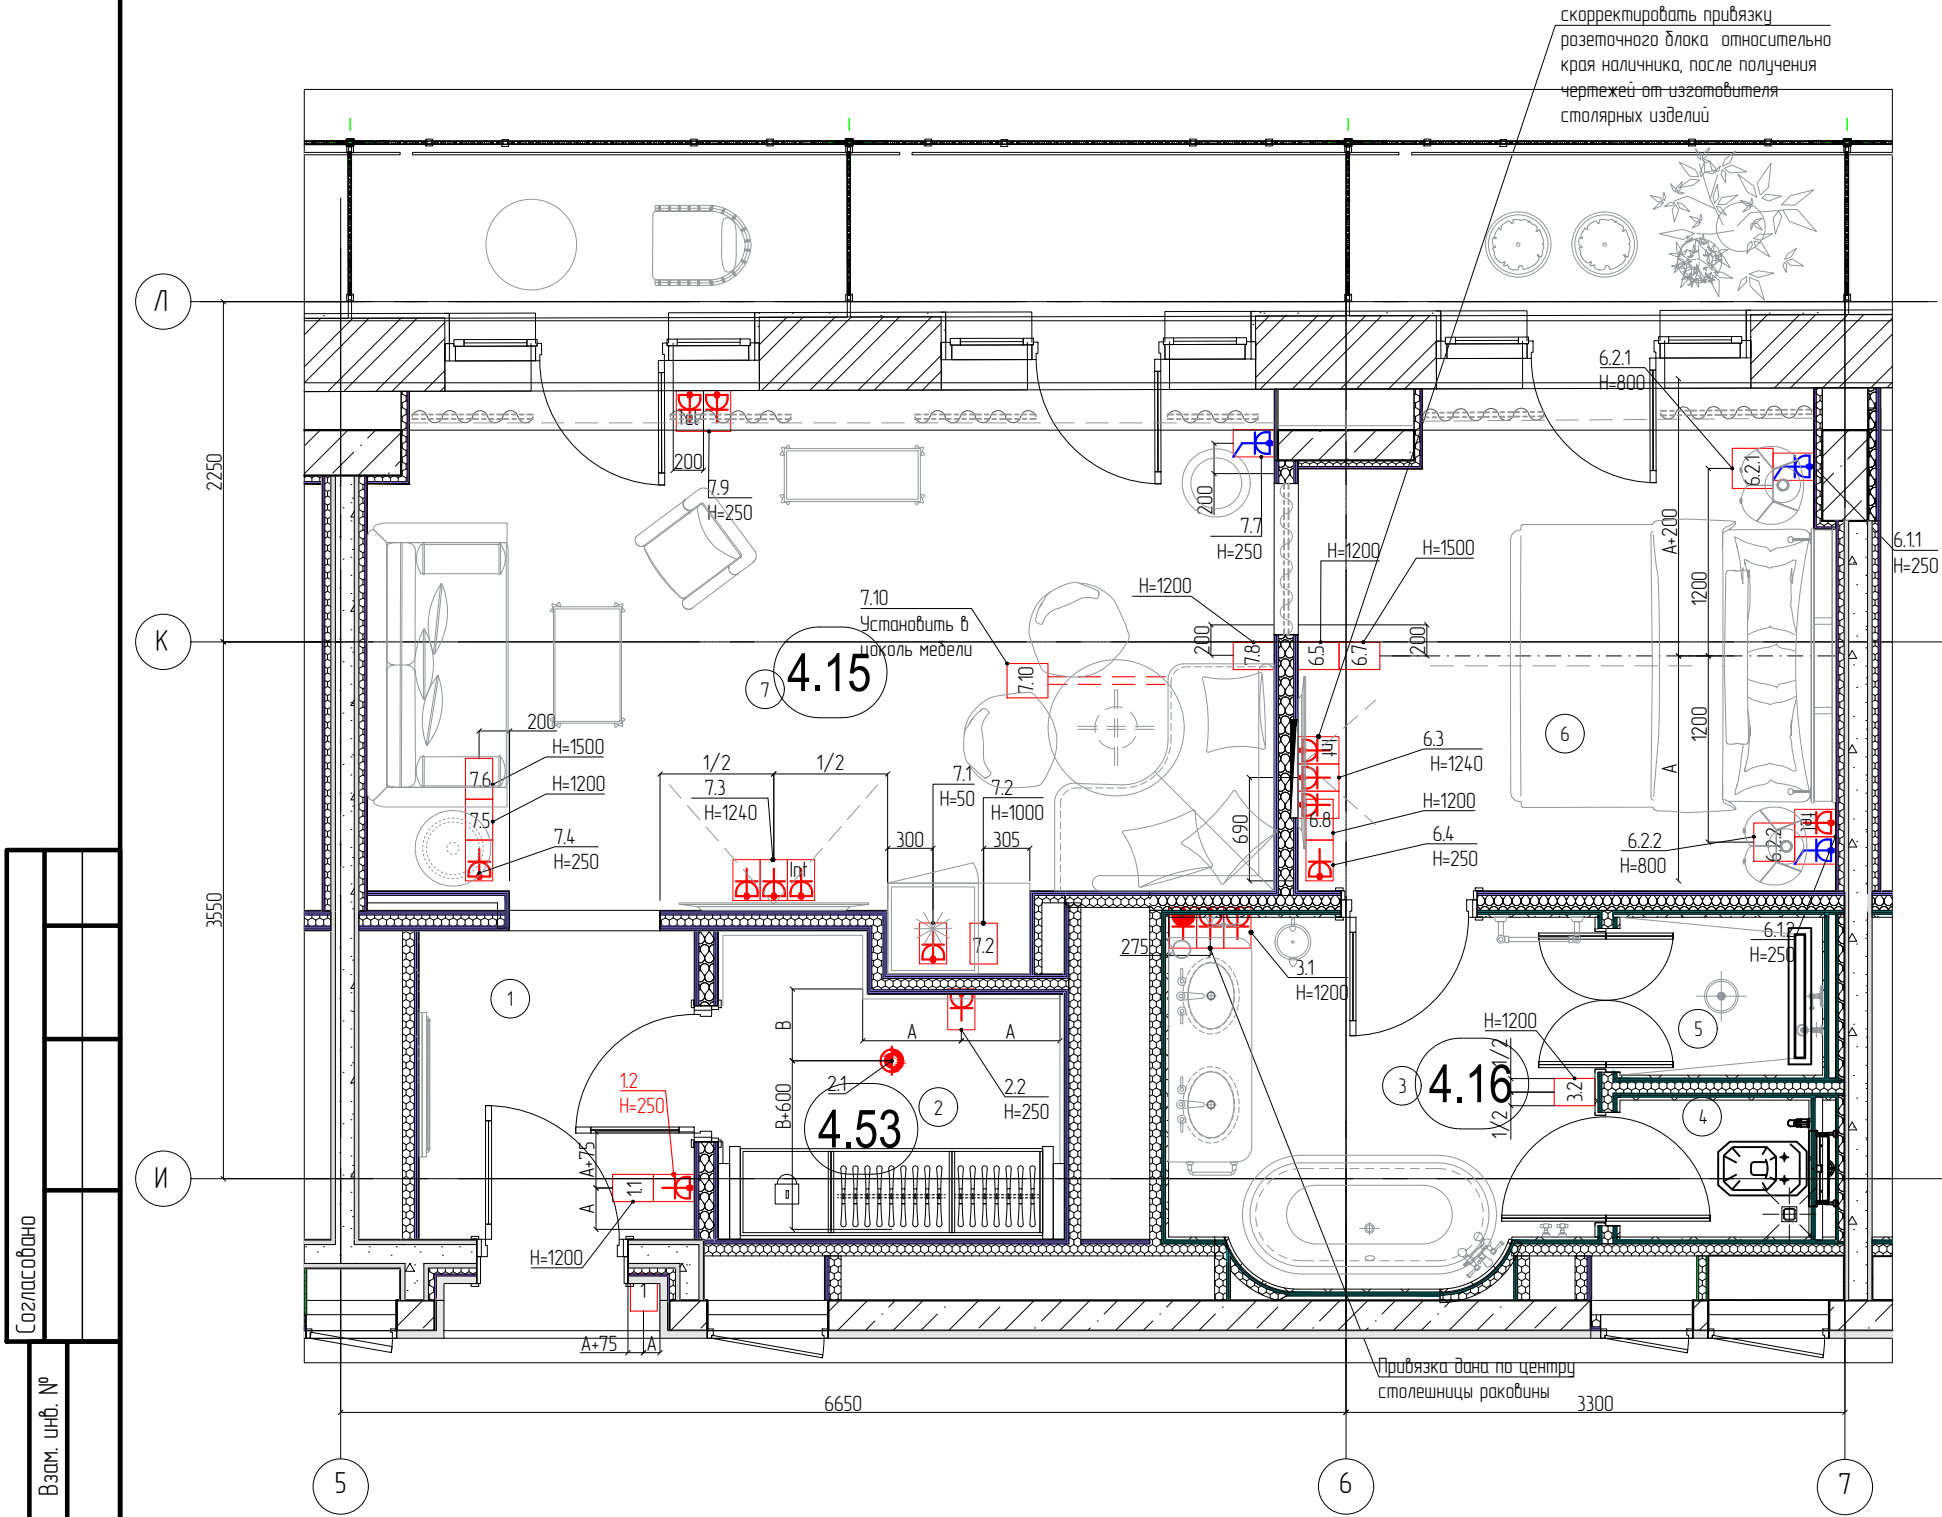

Спецификация электрооборудования номера.								
№пом.	№ блока	Условное обозначение	Функции	Группа освещения	Н от УЧП, мм (до центра блока)	Артикул	Размер блока, мм	Примечания
Снаружи номера	1		Дверной звонок					
			DND (не беспокоить)					
			MUR (уберите номер)					
			Считыватель карт-ключей					
1 Прихожая	11	11	Мастер-выключатель				120x90x6	
	12	12	Вкл/выкл верхнего света: прихожая	Гр. 1.1	1200			
2 Гардеробная	2.1	2.1	Потолочный датчик движения на: верх. свет, бра, встра. освещение шкафа	Гр 2.1	потолочный			Автономная система
	2.2	2.2	Розетка 220 для утюга		250			
3 Ванная	3.1	3.1	Розетка для бритвы 230/110В		1200			Влагозащитные
	3.1	3.1	Розетка бытовая 220					
	3.2	3.2	Вкл/выкл верх. света для ванны (пом.3)	Гр 3.1	1290		120x90x6	
			Вкл/выкл бра (подсветка зеркала)	Гр 3.2				
			Вкл/выкл для су (пом.4) верхнего света + потолочная LED-подсветка	Гр 4.2				
			Вкл/выкл для душа (пом.5) верх. свет + потолочная LED-подсветка	Гр 5.1				

Условные обозначения:

1	- Номер помещения	Гр 4.1	- Обозначение группы освещения		- Розетка для бритвы 230/110В
	- Эвакуационный динамик		- Бытовая розетка		- USB двойная розетка
4.4	- Маркировка датчика		- Телефонная розетка		- Розетка управляемая
4.1	- Обозначение номера блока		- Розетка RJ45 двойная		- Датчик движения

Примечания

1. Планировочное решение выполнено на основании чертежей раздела АР, ТЗ и концепции, утвержденных Заказчиком.
2. При расхождении размеров на строительной площадке, превышающих ± 40 мм, их необходимо согласовать с Архитектором. В случае расхождения размеров между мелко масштабными чертежами и детализированными необходимо руководствоваться только размерами детализированного чертежа. Не использовать фрагменты плана как шаблон.
3. Высоты даны от уровня чистого пола этажа. За отм. чистого пола принять верх чистового покрытия коридора.
4. Высота бытовых розеток +250мм от УЧП, если не указано иное. Высота модулей управляющих освещением +1200мм от УЧП, если не указано иное. Все размеры даны от чистовой поверхности. Размеры указаны до центра блока, если не указано иное.
5. Бытовые розетки для уборки привязаны строго по оси с выключателями, если не указано иное.
6. Привязка электрики в пом.Н8(гостиная), Н7(спальня), Н4(ванная) см. детализированные чертежи с развертками помещений.
7. Привязка электрики в зоне минидара по техзаданию поставщика/изготовителя после выбора и согласования Заказчиком оборудования.
8. Предусмотреть установку датчиков протечки в пом. N2(санузел), Н4(ванная), Н5(санузел).
9. План смотреть совместно с Планом потолков, Планом расположения светильников и Планом расположения электрических выводов.
10. Комплектация оснащения модулей для управления всем освещением согласно рекомендациям поставщика.

Заказчик: ООО «Приморская» ПриМ-0001/2024-АИ.01-410					
Технический заказчик: АО «СЗ «ЛСР. Недвижимость – М»					
Развитие гостиницы «Приморская» в г. Сочи. Приспособление и сохранение объекта культурного наследия «Здание, где в годы Великой Отечественной войны размещались госпитали № 2095, 2120, 1941-1945 годы», расположенного по адресу: г. Сочи, Центральный район, ул. Соколова, д. 1.					
Изм.	Кол.уч.	Лист	№ док.	Подпись	Дата
Разработал	Казыева А.Р.				02.02.26
Проверил	Нобикова Е.				02.02.26
Интерьерные решения. Гостиница "Приморская", корпус 1, 4 этаж, N 410. Тип "Делюкс"					
Н.контр.	Бахвалова Л.В.				02.02.26
ГАП	Сафронова Е.				02.02.26
План расположения розеток и выключателей. Лист 1 М 1:50					
000 "Арх-И-Арм"					

Согласовано

Взам. инв. №

Подп. и дата

Инв. № подл.

План расположения розеток и выключателей. Лист 2.
Корпус 1, 4 этаж, N 410. Тип "Делюкс"

Условные обозначения:

- 1

- Номер помещения
- Эвакуационный динамик
- 4.4/

- Маркировка датчика
- 8.5

- Обозначение номера блока
- Гр 4.1

- Обозначение группы освещения
- Бытовая розетка
- Телефонная розетка
- Розетка RJ45 двойная
- Розетка для бритвы 230/110В
- USB

- USB двойная розетка
- Розетка управляемая
- Датчик присутствия/датчик движения


Экспликация помещений		
№	Наименование	Площадь м2
1	Прихожая	2,79
2	Санузел	1,89
3	Гардеробная комната	3,88
4	Ванная комната	6,73
5	Санузел	1,17
6	Душевая	1,6
7	Спальная комната	10,2
8	Гостиная комната	19,46
S общая		47,7

Спецификация электрооборудования номера								
№пом.	№ блока	Условное обозначение	Функции	Группа освещения	Н от УЧП,мм (до центра блока)	Артикул	Размер блока, мм	Примечания
6 Спальная комната	6.11		Розетка 220 для прикроватной лампы Управление 6.11 инд. со своей стороны	Гр 6.3	250			
	6.12		Телефонная розетка					
	6.21		Управление 6.12 инд. со своей стороны	Гр 6.4	800			
	6.21		Мастер-выключатель для архитектурного света всего номера					
			Вкл./выкл. розетки под прикроватную лампу (индивидуально со своей стороны) –	Гр 6.3				
			Вкл./выкл. ночной подсветки в зоне тумбочки (инд. со своей стороны) + ночная подсветка в с/у (инд со своей стороны)	Гр 6.5				
			DND (не беспокоить)					
			Розетка универсальная + USB					
			кнопка шторы открыть	Гр 6.7				
			кнопка шторы закрыть					
			кнопка таль открыть	Гр 6.8				
			кнопка таль закрыть					
	6.22		Мастер-выключатель для архитектурного света всего номера		800			
	6.22		Вкл./выкл. розетки под прикроватную лампу (индивидуально со своей стороны) –	Гр 6.4				
			Вкл./выкл. ночной подсветки в зоне тумбочки (инд. со своей стороны) + ночная подсветка в с/у (инд со своей стороны)	Гр 6.6				
			DND (не беспокоить)					
			Розетка универсальная + USB					
			кнопка шторы открыть	Гр 6.7				
			кнопка шторы закрыть					
			кнопка таль открыть	Гр 6.8				
			кнопка таль закрыть					
	6.3		Розетка бытовая 220		1240 в нише сбоку от кронштейна			
	6.4		Розетка бытовая 220		250			
			Розетка RJ45 двойная					
	6.5		Розетка бытовая 220		1200			
	6.5		Вкл./выкл. для архитектурного света: верхний свет	Гр 6.1				
			Бра 2шт	Гр 6.2				
	6.7		Термостат		1500			
	6.8		Вкл./выкл для ванной: верхний свет	Гр 3.1	1200			
	6.8		Вкл./выкл бра ванная (подсветка зеркала)	Гр 3.2				

Спецификация электрооборудования номера								
№пом.	№ блока	Условное обозначение	Функции	Группа освещения	Н от УЧП, мм (до центра блока)	Артикул	Размер блока, мм	Примечания
7 гостиная комната	7.1		Розетка 220 для минибара		50			
	7.2		Розетка 220 для кофемашины		1000			
			Розетка 220 для чайника					
	7.3		Розетка бытовая 220		1240			
			Розетка бытовая 220					
			Розетка RJ45 двойная					
	7.4		Розетка бытовая 220		250			
	7.5		Вкл/выкл люстры над обеденным столом	Гр 7.1	1200			
			Вкл/выкл точечных светильников	Гр 7.3				
			Вкл/выкл бра (2шт.) на стене + Вкл/выкл розетки под торшер + Вкл/выкл LED-подсветки 4шт. полка в зоне минибара	Гр 7.2+ 7.4+ 7.5				
			кнопка шторы открыть	Гр 7.6				
			кнопка шторы закрыть					
			кнопка таль открыть	Гр 7.7				
			кнопка таль закрыть					
			7.6			Термостат		1500
	7.7		Розетка под торшер. Управление 7.5 + 7.8	Гр 7.5	250			
	7.8		Вкл/выкл люстры над обеденным столом	Гр 7.1	1500			
			Вкл/выкл точечных светильников	Гр 7.3				
			Вкл/выкл бра (2шт.) на стене + Вкл/выкл розетки под торшер + Вкл/выкл LED-подсветки 4шт. полка в зоне минибара	Гр 7.2+ 7.4+ 7.5				
			кнопка шторы открыть	Гр 7.6				
			кнопка шторы закрыть					
			кнопка таль открыть	Гр 7.7				
			кнопка таль закрыть					
7.9				телефонная розетка			250	
	Розетка универсальная бытовая 220+USB							
7.10		Розетка RJ45		встр. в цоколь мебели				
		Розетка универсальная бытовая 220+USB						

Примечания									
1. Планировочное решение выполнено на основании чертежей раздела АР, ТЗ и концепции, утвержденной Заказчиком. 2. При расхождении размеров на строительной площадке , превышающих ± 40 мм, их необходимо согласовать с Архитектором. В случае расхождения размеров между мелко масштабными чертежами и детализированными необходимо руководствоваться только размерами детализированного чертежа. Не использовать фрагменты плана как шаблон. 3. Высоты даны от уровня чистого пола этажа. За отм. чистого пола принять верх чистового покрытия коридора. 4. Высота бытовых розеток +250мм от УЧП, если не указано иное. Высота модулей управляющих освещением +1200мм от УЧП, если не указано иное. Все размеры даны от чистовой поверхности. Размеры указаны до центра блока, если не указано иное. 5. Бытовые розетки для уборки привязаны строго по оси с выключателями, если не указано иное. 6. Привязка электрики в пом.Н8(гостиная), Н7(спальня), Н4(ванная) см. детализированные чертежи с развертками помещений. 7. Привязка электрики в зоне минибара по техзаданию поставщика/изготовителя после выбора и согласования Заказчиком оборудования. 8. Предусмотреть установку датчиков протечки в пом. N2(санузел), N4(ванная), N5(санузел). 9. План смотреть совместно с Планом потолков, Планом расположения светильников и Планом расположения электрических выводов. 10. Комплектация оснащения модулей для управления всем освещением согласно рекомендациям поставщика.									
						Заказчик: ООО «Приморская» ПриМ-0001/2024-АИ.01-410 Технический заказчик: АО «СЗ «ЛСР. Недвижимость – М»			
						Развитие гостиницы «Приморская» в г. Сочи. Приспособление и сохранение объекта культурного наследия «Здание, где в годы Великой Отечественной войны размещались госпитали № 2095, 2120, 1941-1945 годы», расположенного по адресу: г. Сочи, Центральный район, ул. Соколова, д. 1.			
	Изм.	Кол.уч.	Лист	№ док.	Подпись	Дата	Интерьерные решения. Гостиница "Приморская", корпус 1, 4 этаж, N 410. Тип "Делюкс"		
	Разработал	Казыева А.Р.				02.02.26			
	Проверил	Нобикова Е.				02.02.26	РД 12 40		
	Н.контр.	Бахвалова Л.В.				02.02.26	План расположения розеток и выключателей. Лист 2 М 1:50		
	ГАП	Сафронова Е.				02.02.26			
							ООО "Арх-И-Арм"		

План расположения электрических выводов.
Корпус 1, 4 этаж, N 410. Тип "Делюкс"

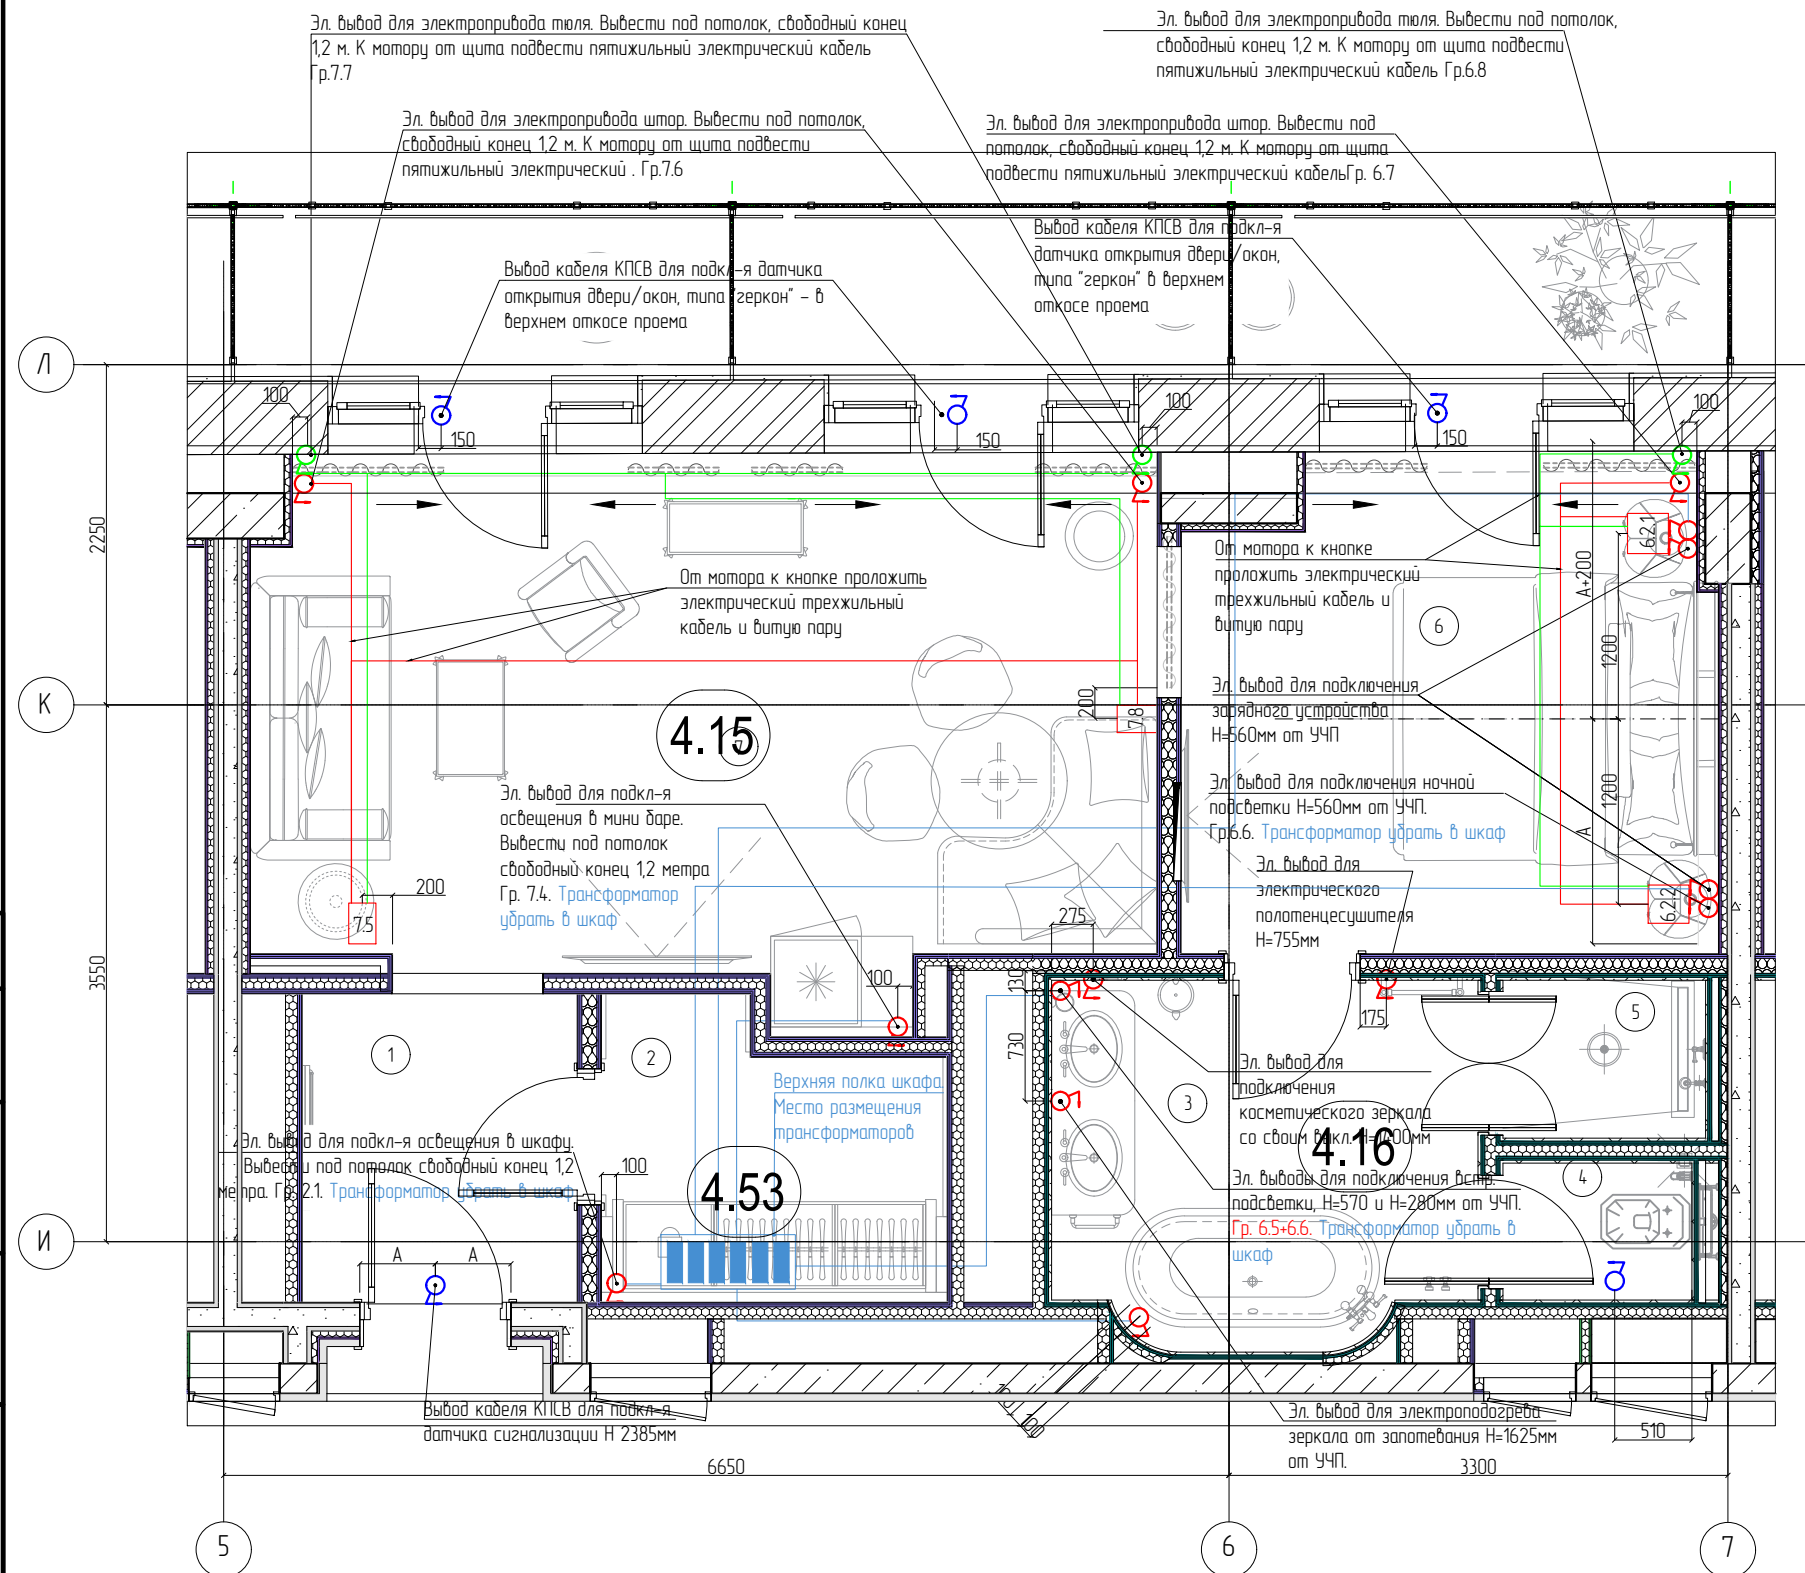


Условные обозначения:


-  – Номер помещения
-  – Электрический вывод
-  – Слаботочный электрический вывод
-  – Направление открывания штор
- Гр 4.1 – Обозначение группы освещения

Деталь.


Устройство встроенной подсветки прикроватной тумбочки. Пом.№6

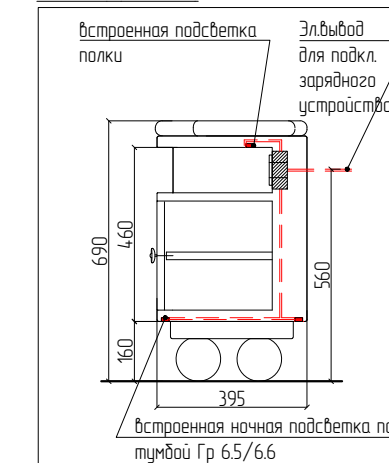


Светодиодная подсветка под тумбой

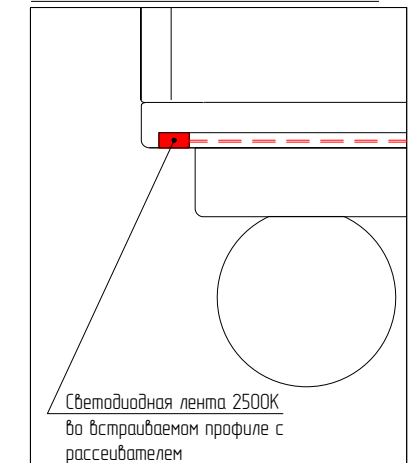

План түмбөчки.

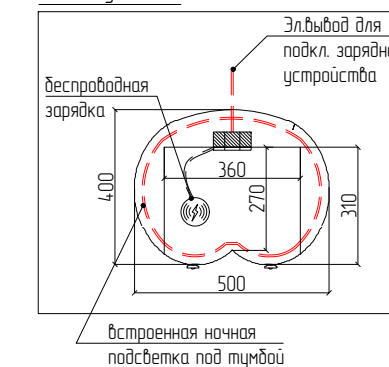

Светодиодная подсветка полки.

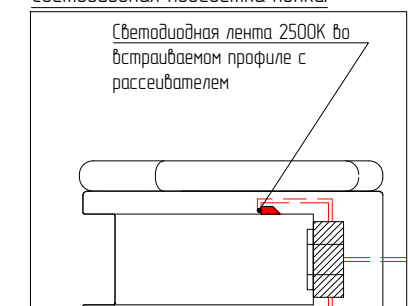

Примечания


1. Планировочное решение выполнено на основании чертежей раздела АР, ТЗ и концепции, утвержденной Заказчиком.
2. При расхождении размеров на строительной площадке, превышающих ± 40 мм, их необходимо согласовать с Архитектором. В случае расхождения размеров между мелко масштабными чертежами и детализационными необходимо руководствоваться только размерами детализационного чертежа. Не использовать фрагменты плана как шаблон.
3. Высоты даны от уровня чистого пола этажа. За отм. чистого пола принять верх чистового покрытия коридора.
4. Привязка электротки в пом. N8(гостиная), N7(спальня), N4(ванная) см. детализационные чертежи с развертками помещений.
5. Предусмотреть установку датчиков протечки в пом. N2(санузел), N4(ванная), N5(санузел).
6. План смотреть совместно с Планом потолков и Планом расположения светильников и выключателей. Планом расположения розеток и выключателей.
7. Кол-во и тип кабелей для электромонтажных работ определяется в проекте автоматизации.
8. Размещение трансформаторов для светодиодной скрытой подсветки предусмотреть в прихожей на верхней полке шкафа.
9. Скорректировать привязку выводов для датчиков открывания балконных дверей – зерком, т.к. возможны изменения конфигурации оконных проемов согласно АР в части фасады и оконные проемы.

						Заказчик: ООО «Приморская»			ПрМ-0001/2024-АИ.01-410		
						Технический заказчик: АО «СЗ «ЛСР. Недвижимость – М»					
						Развитие гостиницы «Приморская» в г. Сочи. Приспособление и сохранение объекта культурного наследия «Здание, где в годы Великой Отечественной войны размещались госпитали № 2095, 2120, 1941–1945 годы», расположенного по адресу: г. Сочи, Центральный район, ул. Соколова, д. 1.					
Изм.	Кол.уч.	Лист	№ док.	Подпись	Дата						
Разработал		Казыева А.Р.			02.02.26	Интерьерные решения. Гостиница "Приморская", корпус 1, 4 этаж, N 410. Тип "Делюкс"			Стандия	Лист	Листов
Проверил		Нобикова Е.			02.02.26				РД	13	40
						План расположения электрических выводов. М 1:50			ООО "Арх-И-Арт"		
Н.контр.		Бахвалова Л.В.			02.02.26						
ГАП		Сафронова Е.			02.02.26						

План с привязкой светильников и указанием групп освещения.
Корпус 1, 4 этаж, N 410. Тип "Делюкс"

- Условные обозначения:
- 1 - Номер помещения
 - Гр11 - Маркировка группы освещения
 - Цветовое обозначение групп освещения
 - 7.8 - Маркировка датчика

Экспликация помещений		
№	Наименование	Площадь м2
1	Прихожая	3,74
2	Гардеробная комната	4,18
3	Ванная комната	6,77
4	Санузел	12
5	Душевая	156
6	Спальная комната	10,45
7	Гостиная комната	19,37
S общая		47,3

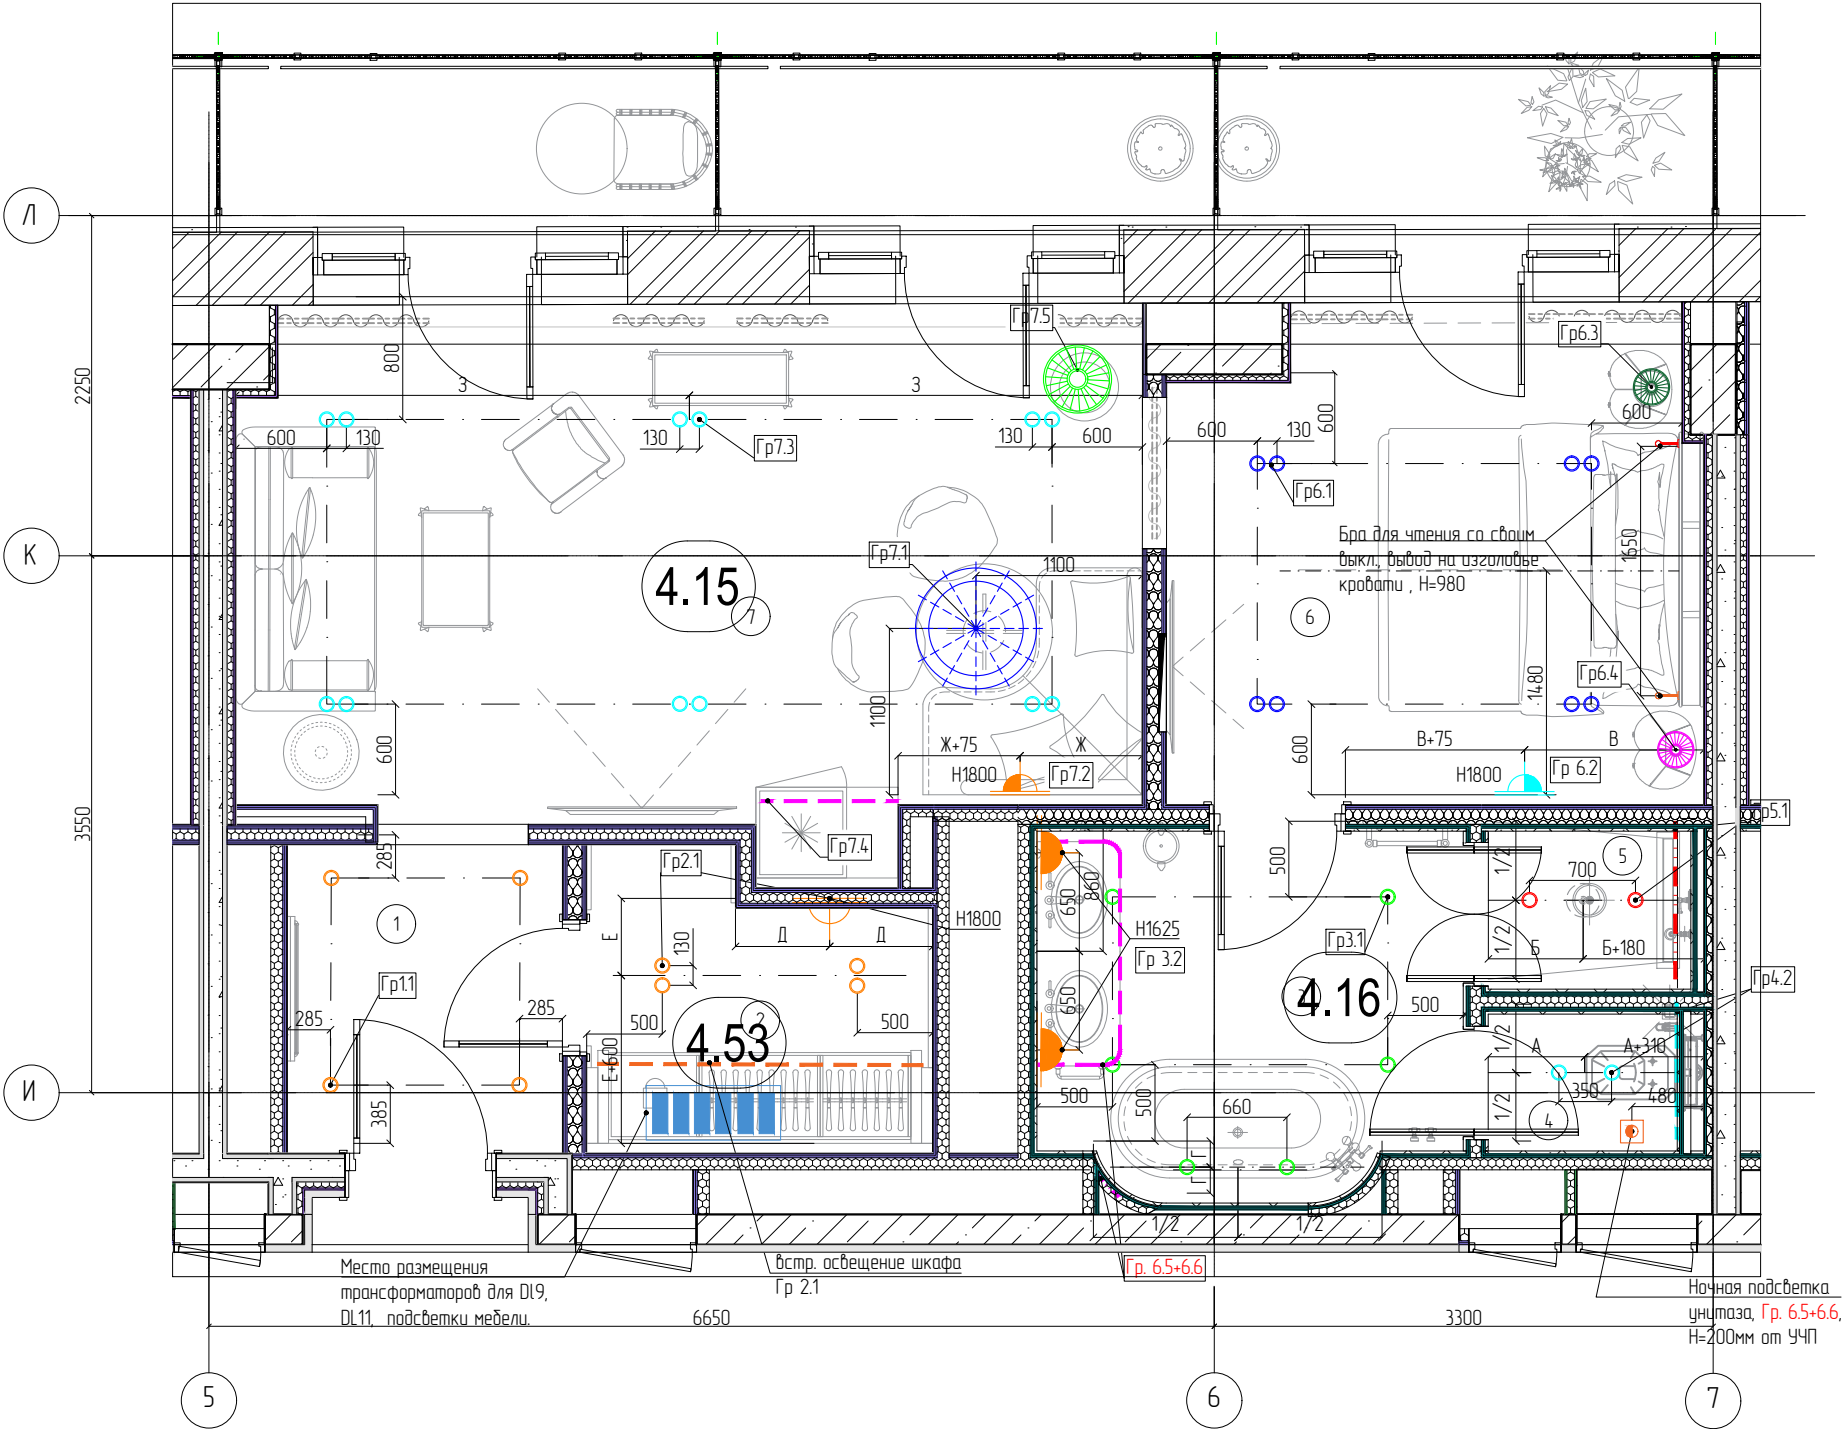

Спецификация светильников номера Deluxe:				
Тип	Изображение типоразмера	Описание	Вид	Кол-во (шт.)
DL1		- Настенный светильник (бра), NYMPHEA wall light, керамика: H=255мм, Dmax=220мм, W=145мм от стены.		2
DL12		- Настенный светильник (бра), SOGNI DI CRISTALLO WALL LIGHT, стекло: H=600мм, W=250мм.		2
DL2		- Настольный светильник, LG DESIGN bedside lamp, керамика и текстиль: H=460мм, Dплафона max=235мм, Dоснования max=135мм		2
DL3		- Подвесной светильник, CORAIL CHANDELIER, LG DESIGN pendant lamp, D=820мм, Hплафона=210мм		1
DL4		- Напольный светильник, торшер		1
DL5		- Настенный светильник (бра), MAHE wall light: 360x130x370мм, E27 4W LED		1
DL6		- Бра для чтения арт. MEL JAC READING LIGHT, цвет: Chromi Vif с кнопкой вкл. F21-0260-V1		2
DL8		- светильник точечный полнонастраиваемый арт. 284-25933 FW ENTERO RD-S TRIMLESS 93045 FW		28
DL8.1		- светильник точечный полнонастраиваемый влагозащи. IP 45 арт. 284-509330 FW ENTERO RD-S TRIMLESS		10
DL9		- встроеныый светильник для ночной подсветки, IP 65		1
DL11		- светодиодная лента, IP-65		19 пог.м.

Согласовано				
Взам. инв. №				
Подп. и дата				
Инв. № подл.				

Примечания:

- Планировочное решение выполнено на основании чертежей раздела АР, ТЗ и концепции, утвержденной Заказчиком.
- При расхождении размеров на строительной площадке, превышающих ± 40 мм, их необходимо согласовать с Архитектором. В случае расхождения размеров между мелко масштабными чертежами и детализированными необходимо руководствоваться только размерами детализированного чертежа. Не использовать фрагменты плана как шаблон.
- Высоты даны от уровня чистого пола этажа. За отм. чистого пола принять верх чистового покрытия коридора.
- Таблица с оснащением блоков для управления всем освещением см. лист: План расположения розеток и выключателей, расположения электрических выходов, расположения и маркировки светильников.
- Группы освещения выделены одним цветом, один цвет соответствует одной группе.
- Размещение трансформаторов для светодиодной скрытой подсветки предусмотреть в прихожей на верхней полке шкафа.

Заказчик: ООО «Приморская»						ПриМ-0001/2024-АИ.01-410		
Технический заказчик: АО «СЗ «ЛСР. Недвижимость – М»								
Развитие гостиницы «Приморская» в г. Сочи. Приспособление и сохранение объекта культурного наследия «Здание, где в годы Великой Отечественной войны размещались госпитали № 2095, 2120, 1941-1945 годы», расположенного по адресу: г. Сочи, Центральный район, ул. Соколова, д. 1.								
Изм.	Кол.уч.	Лист	№ док.	Подпись	Дата	Интерьерные решения. Гостиница "Приморская", корпус 1, 4 этаж, N 410. Тип "Делюкс"	Стадия	Лист
Разработал	Казыева А.Р.				02.02.26		РД	14
Проверил	Нобикова Е.				02.02.26			40
						План с привязкой светильников и указанием групп освещения. М 1:50	ООО "Арх-И-Арт"	
Н.контр.	Бахвалова Л.В.				02.02.26			
ГАП	Сафронова Е.				02.02.26			

План с расположением и маркировкой светильников.
Корпус 1, 4 этаж, N 410. Тип "Делюкс"

Условные обозначения:


- 1

– Номер помещения
- Гр11

– Маркировка группы освещения
- Цветовое обозначение групп освещения
- 7.8

– Маркировка датчика

Экспликация помещений		
№	Наименование	Площадь м2
1	Прихожая	3,74
2	Гардеробная комната	4,18
3	Ванная комната	6,77
4	Санузел	12
5	Душевая	156
6	Спальная комната	10,45
7	Гостиная комната	19,37
S общая		47,3

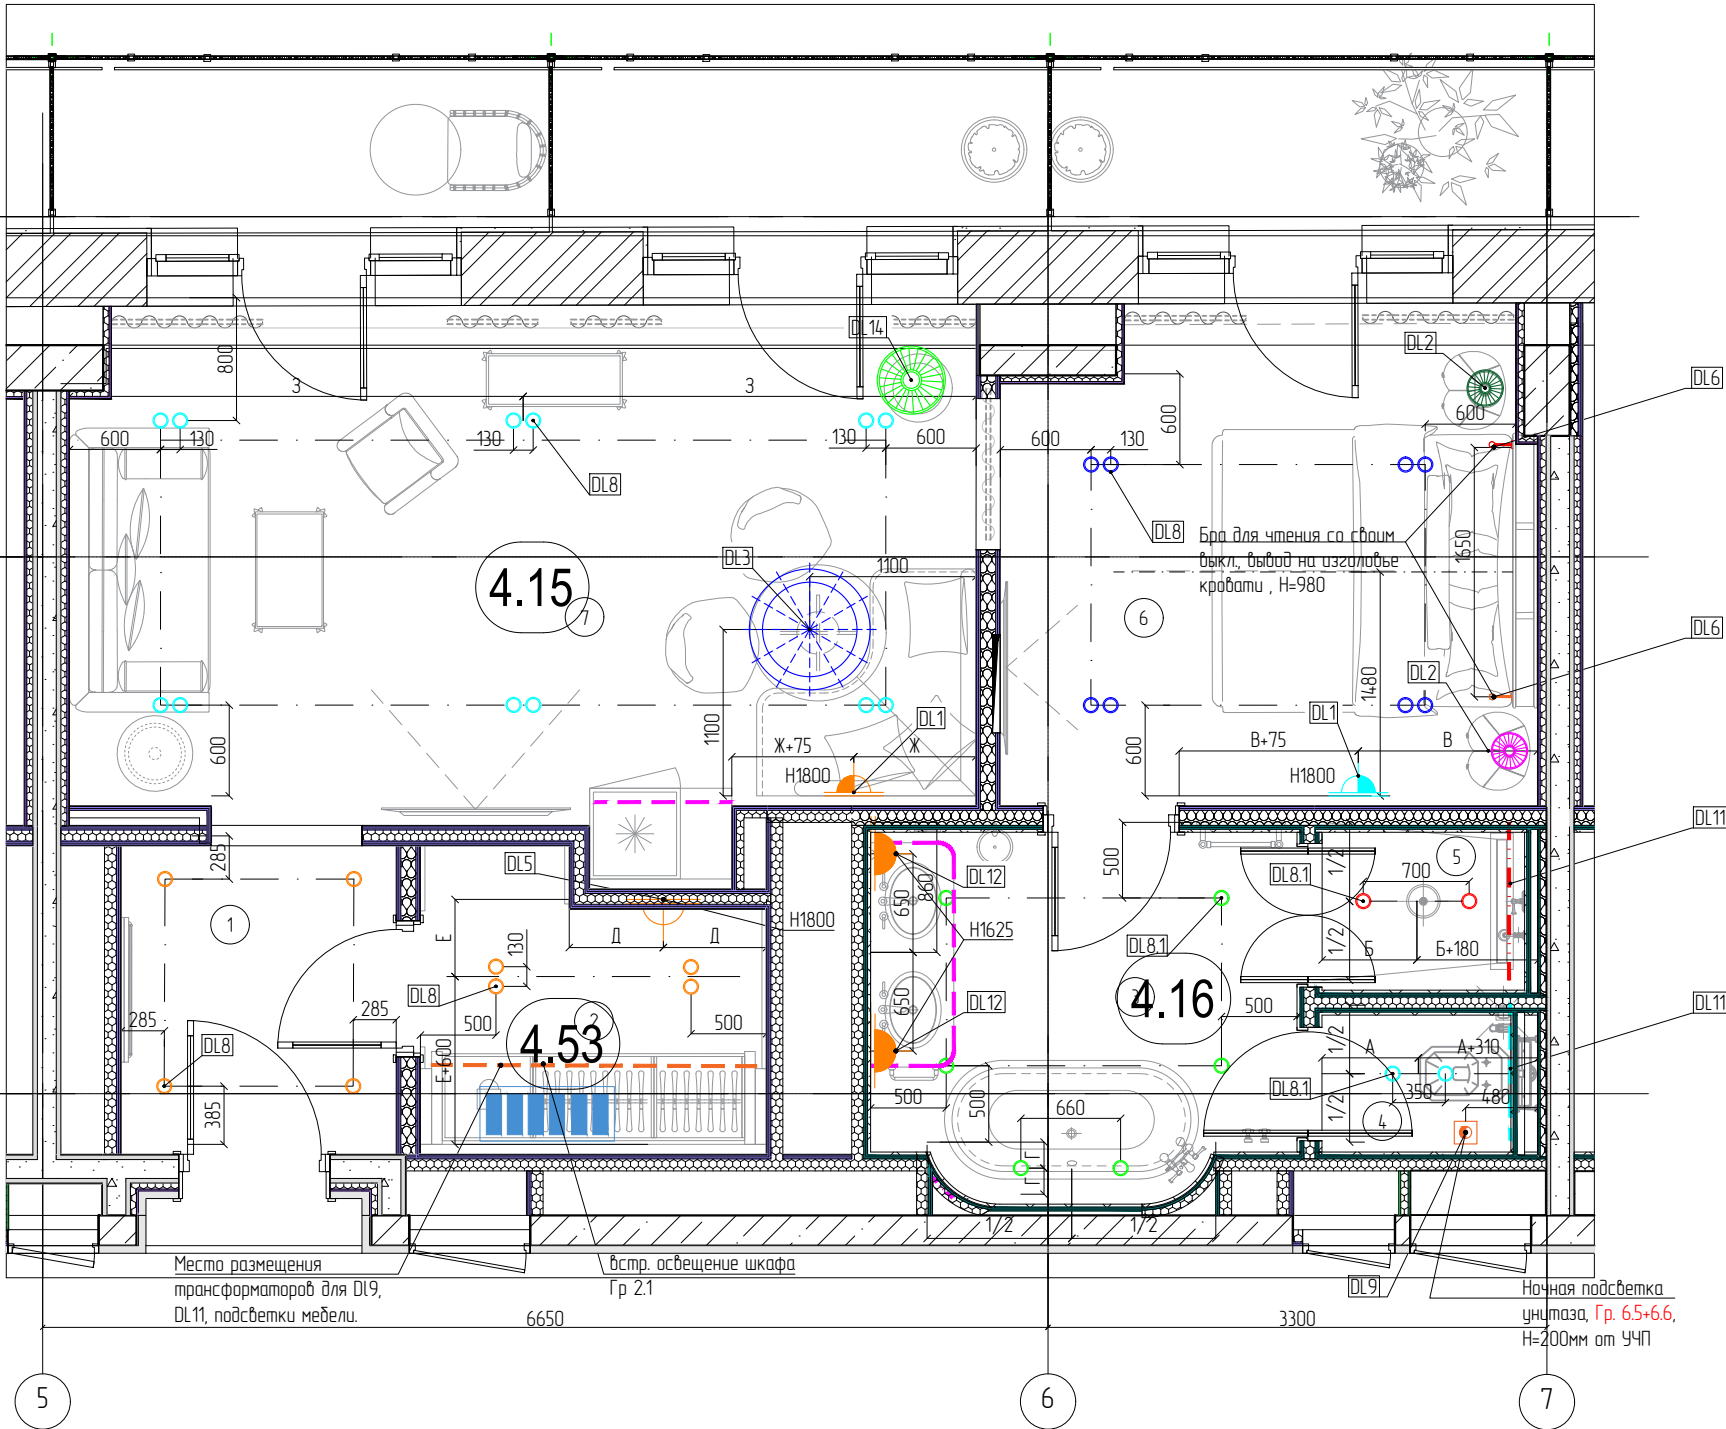

Спецификация светильников номера Deluxe:				
Тип	Изображение типоразмера	Описание	Вид	Кол-во (шт.)
DL1		– Настенный светильник (бра), NYMPHEA wall light, керамика: H=255мм, Dmax=220мм, W=145мм от стены.		2
DL12		– Настенный светильник (бра), SOGNI DI CRISTALLO WALL LIGHT, стекло: H=600мм, W=250мм.		2
DL2		– Настольный светильник, LG DESIGN bedside lamp, керамика и текстиль: H=460мм, Dплафона max=235мм, Dоснования max=135мм		2
DL3		– Подвесной светильник, CORAIL CHANDELIER, LG DESIGN pendant lamp, D=820мм, Hплафона=210мм		1
DL4		– Напольный светильник, торшер		1
DL5		– Настенный светильник (бра), MAHE wall light: 360x130x370мм, E27 4W LED		1
DL6		– Бра для чтения арт. MEL JAC READING LIGHT, цвет: Chromi Vif с кнопкой вкл. F21-0260-V1		2
DL8		– светильник точечный полнострайбаемый арт. 28425933 FW ENTERO RD-S TRIMLESS 93045 FW		28
DL8.1		– светильник точечный полнострайбаемый влагозащ. IP 45 арт. 284509330 FW ENTERO RD-S TRIMLESS		10
DL9		– встроенный светильник для ночной подсветки, IP 65		1
DL11		– светодиодная лента, IP-65		19 пог.м.

Согласовано	
Взам. инв. №	
Подп. и дата	
Инв. № подл.	


Примечания

1. Планировочное решение выполнено на основании чертежей раздела АР, ТЗ и концепции, утвержденной Заказчиком.
2. При расхождении размеров на строительной площадке, превышающих ± 40 мм, их необходимо согласовать с Архитектором. В случае расхождения размеров между мелко масштабными чертежами и детализированными необходимо руководствоваться только размерами детализированного чертежа. Не использовать фрагменты плана как шаблон.
3. Высоты даны от уровня чистого пола этажа. За отм. чистого пола принять верх чистового покрытия коридора.
4. План смотреть совместно с планами: потолков, расположения розеток, расположения электрических выводов, с привязкой светильников и указанием групп освещения.
5. Таблица с оснащением модулей для управления всем освещением см. лист: План расположения розеток.
6. Группы освещения выделены одним цветом, один цвет соответствует одной группе.


						Заказчик: ООО «Приморская» Технический заказчик: АО «СЗ «ЛСР. Недвижимость – М»				Прим-0001/2024-АИ.01-410		
						Развитие гостиницы «Приморская» в г. Сочи. Приспособление и сохранение объекта культурного наследия «Здание, где в годы Великой Отечественной войны размещались госпитали № 2095, 2120, 1941-1945 годы», расположенного по адресу: г. Сочи, Центральный район, ул. Соколова, д. 1.						
Изм.	Кол.уч.	Лист	№ док.	Подпись	Дата	Интерьерные решения. Гостиница "Приморская", корпус 1, 4 этаж, N 410. Тип "Делюкс"				Стадия	Лист	Листов
Разработал	Казыева А.Р.				02.02.26					РД	15	40
Проверил	Новикова Е.				02.02.26							
						План с расположением и маркировкой светильников. М 1:50				ООО "Арх-И-Арм"		
Н.контр.	Бахвалова Л.В.				02.02.26							
ГАП	Сафронова Е.				02.02.26							

План потолков.
Корпус 1, 4 этаж, N 410. Тип "Делюкс"


Экспликация помещений		
№	Наименование	Площадь м2
1	Прихожая	3,74
2	Гардеробная комната	4,18
3	Ванная комната	6,77
4	Санузел	12
5	Душевая	1,56
6	Спальная комната	10,45
7	Гостиная комната	19,37
Σ общая		47,3

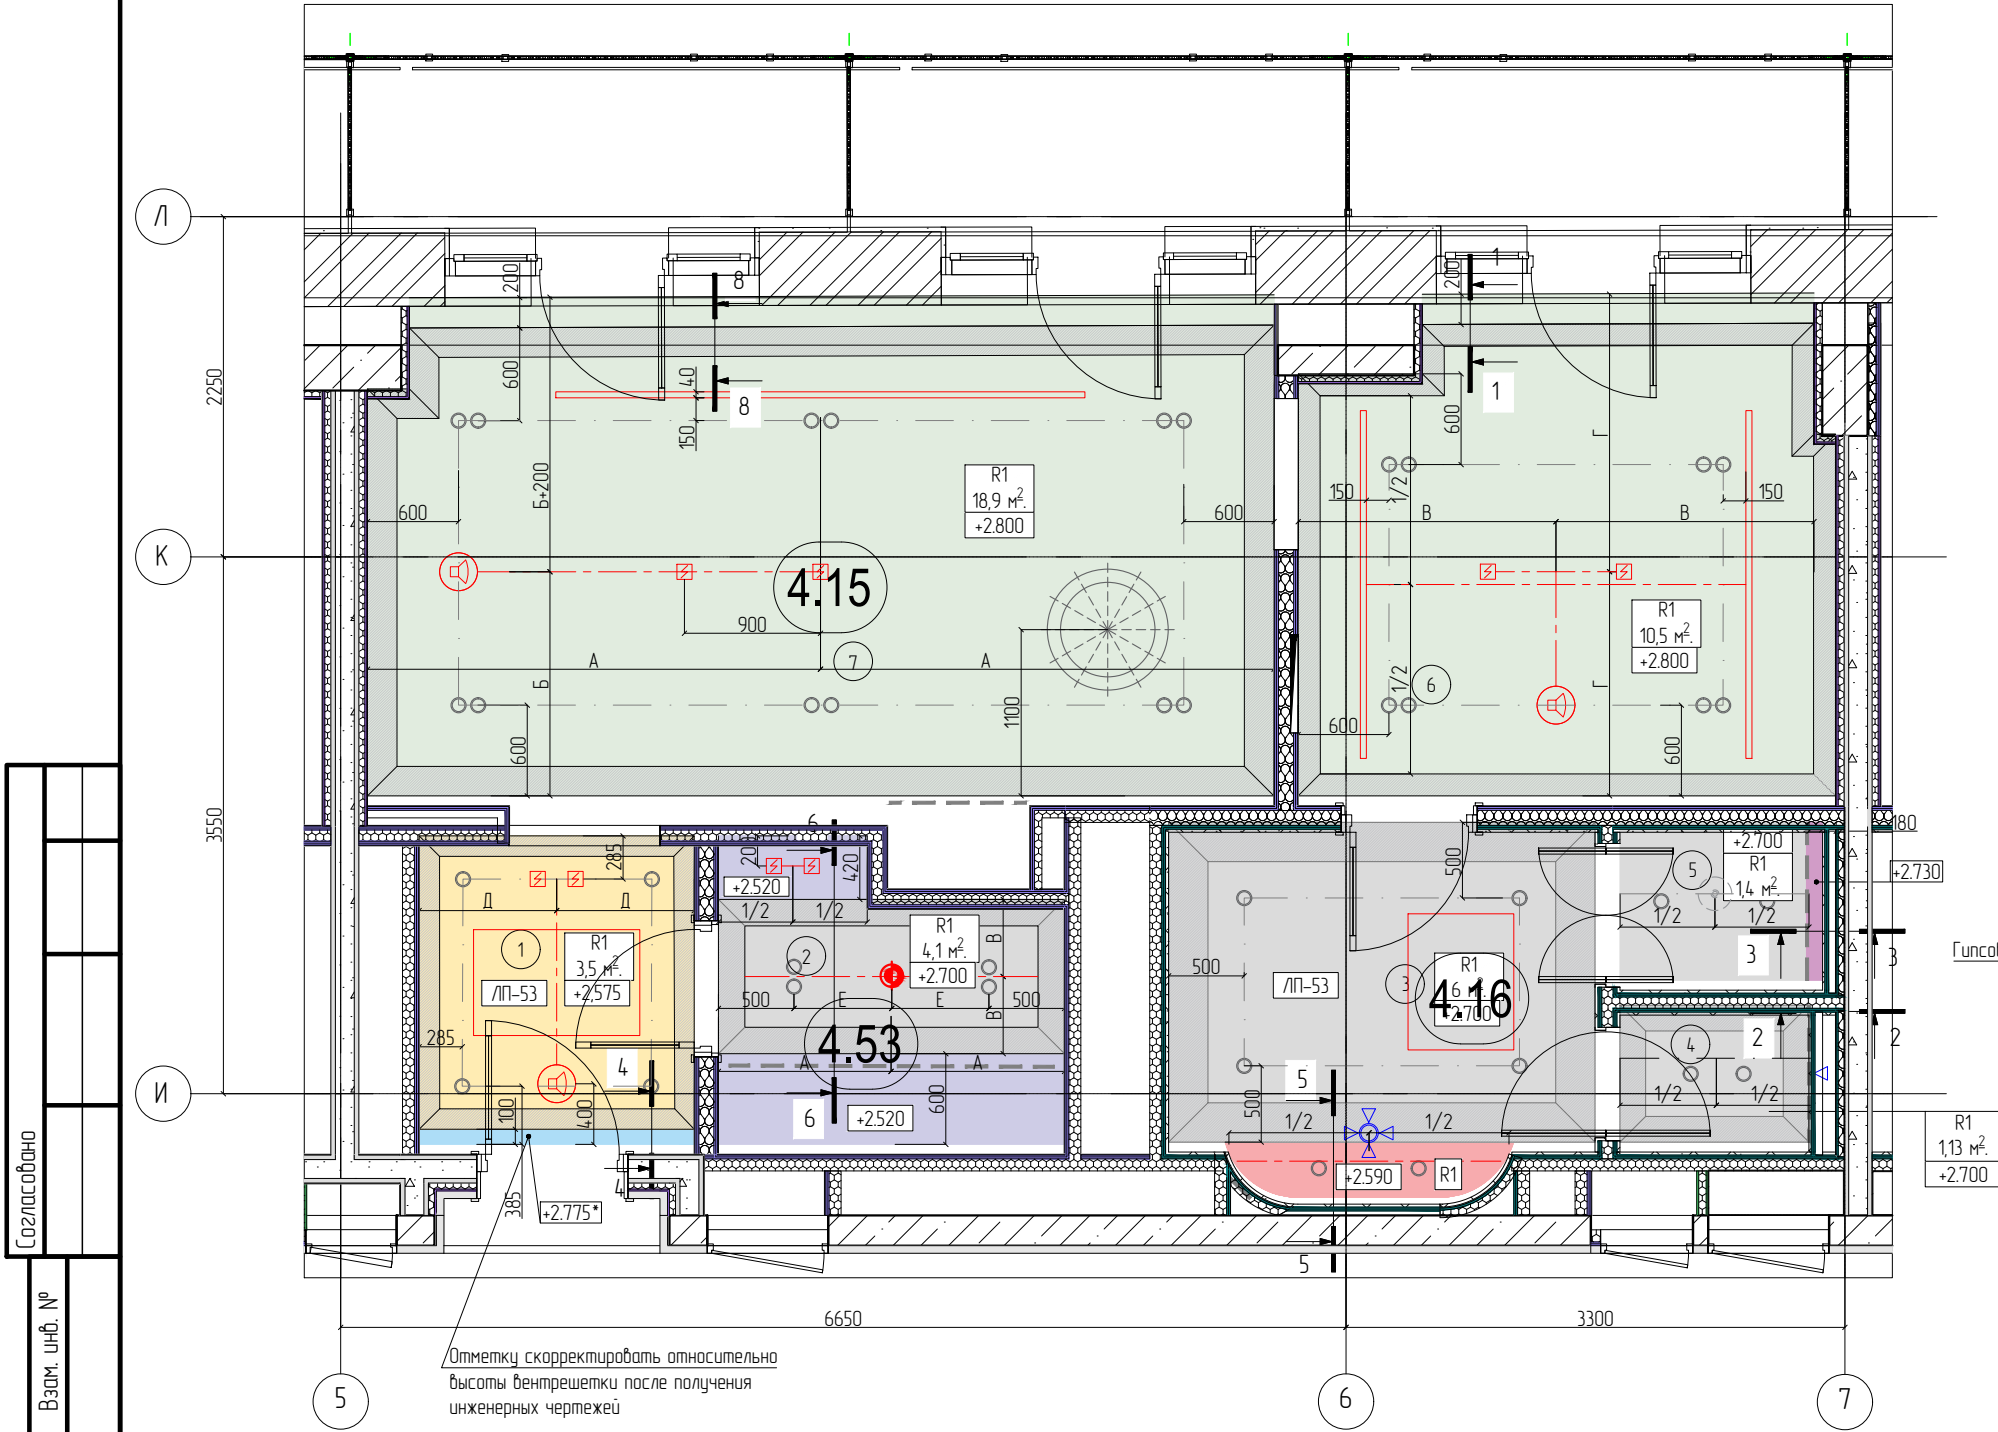

Разрез 5-5
пом. 3 (ванная)

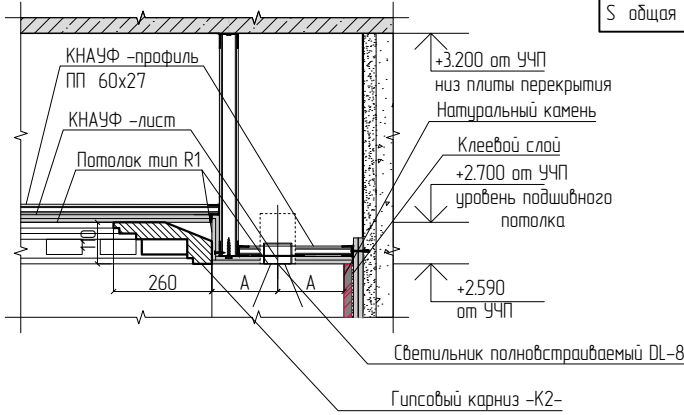

Разрез 6-6
пом. 2 (гардеробная)

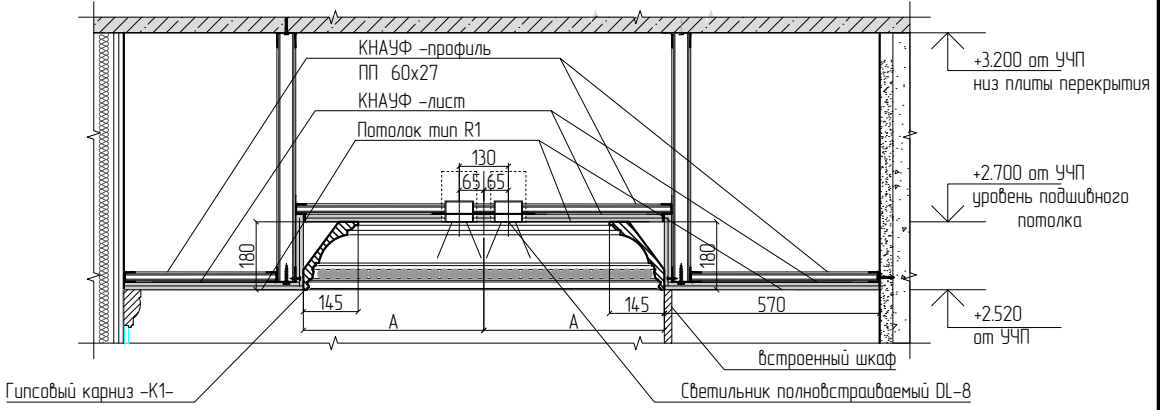

Спецификация потолков номера Deluxe				
Тип	Изображение типоразмера	Описание	Вид	Кол-во
- R1 -		Примечание: R1 - Тип потолка П113.2 (Гипскартон Кнауф Аквamarin x2 листа) Тип отделки О1 (Грунтовка глубокого проникновения Кнауф Тифенгрунд - 1 мм, Клей Семин - 1 мм, Стеклохолст Wellton - 1 мм, Шпаклевка Кнауф Ротбанд Профи - 5 мм, Ротбанд Паста Профи - 2 мм, Грунтовка глубокого проникновения Кнауф Тифенгрунд - 1 мм, Покраска 2 сл./Обои по ДП)		45,53 + 10% = 50,08 м²

Условные обозначения:

- 1 - Номер помещения
- +2.800 - Отметка потолка от УЧП этажа
- R1 - Маркировка потолка
- - Полноэстраваемые точечные светильники
- Светодиодная подсветка
- - Громкоговоритель потолочный BIAO SCS-06-03
- - Извещатель пожарный дымовой точечный BF
- - Датчик присутствия/датчик движения


Примечания:

- Планировочное решение выполнено на основании чертежей раздела АР, ТЗ и концепции, утвержденной Заказчиком.
- При расхождении размеров на строительной площадке, превышающих ± 40 мм, их необходимо согласовать с Архитектором. В случае расхождения размеров между мелко масштабными чертежами и детализированными необходимо руководствоваться только размерами детализированного чертежа. Не использовать фрагменты плана как шаблон.
- Высоты даны от уровня чистого пола этажа. За отм. чистого пола принять верх чистового покрытия коридора.
- Подшивной потолок по периметру помещений с гипсовым лепниной, металлокаркас, установить с шагом 300мм. Предусмотреть усиление конструкции в местах крепления листов и подвесных декоративных светильников.
- План смотреть совместно с планом расположения светильников и выключателей, электрических выводов и планом расположения розеток и выключателей. Разрезы см. детализированный чертеж. Узлы и детали потолка.
- Площади указанные на плане не использовать для покупки материала, кол-во краски учитывать согласно расчету Поставщика в зависимости от укрывистости краски и кол-ва слоев для нанесения.



Заказчик: ООО «Приморская» ПриМ-0001/2024-АИ.01-410					
Технический заказчик: АО «СЗ «ЛСР. Недвижимость - М»					
Развитие гостиницы «Приморская» в г. Сочи. Приспособление и сохранение объекта культурного наследия «Здание, где в годы Великой Отечественной войны размещались госпитали № 2095, 2120, 1941-1945 годы», расположенного по адресу: г. Сочи, Центральный район, ул. Саколова, д. 1.					
Изм.	Кол.уч.	Лист	№ док.	Подпись	Дата
Разработал	Казыева А.Р.	02.02.26			
Проверил	Нобикова Е.	02.02.26			
Н.контр.	Бахвалова Л.В.	02.02.26			
ГАП	Сафронова Е.	02.02.26			
Интерьерные решения. Гостиница "Приморская", корпус 1, 4 этаж, N 410. Тип "Делюкс"					Стадия
План потолков. М 1:50					Лист
000 "Арх-И-Арм"					Листов
					РД
					16
					40

План с маркировкой карнизов.
Корпус 1, 4 этаж, N 410. Тип "Делюкс"

Экспликация помещений		
№	Наименование	Площадь м2
1	Прихожая	3,74
2	Гардеробная комната	4,18
3	Ванная комната	6,77
4	Санузел	1,2
5	Душевая	1,56
6	Спальная комната	10,45
7	Гостиная комната	19,37
Σ общая		47,3

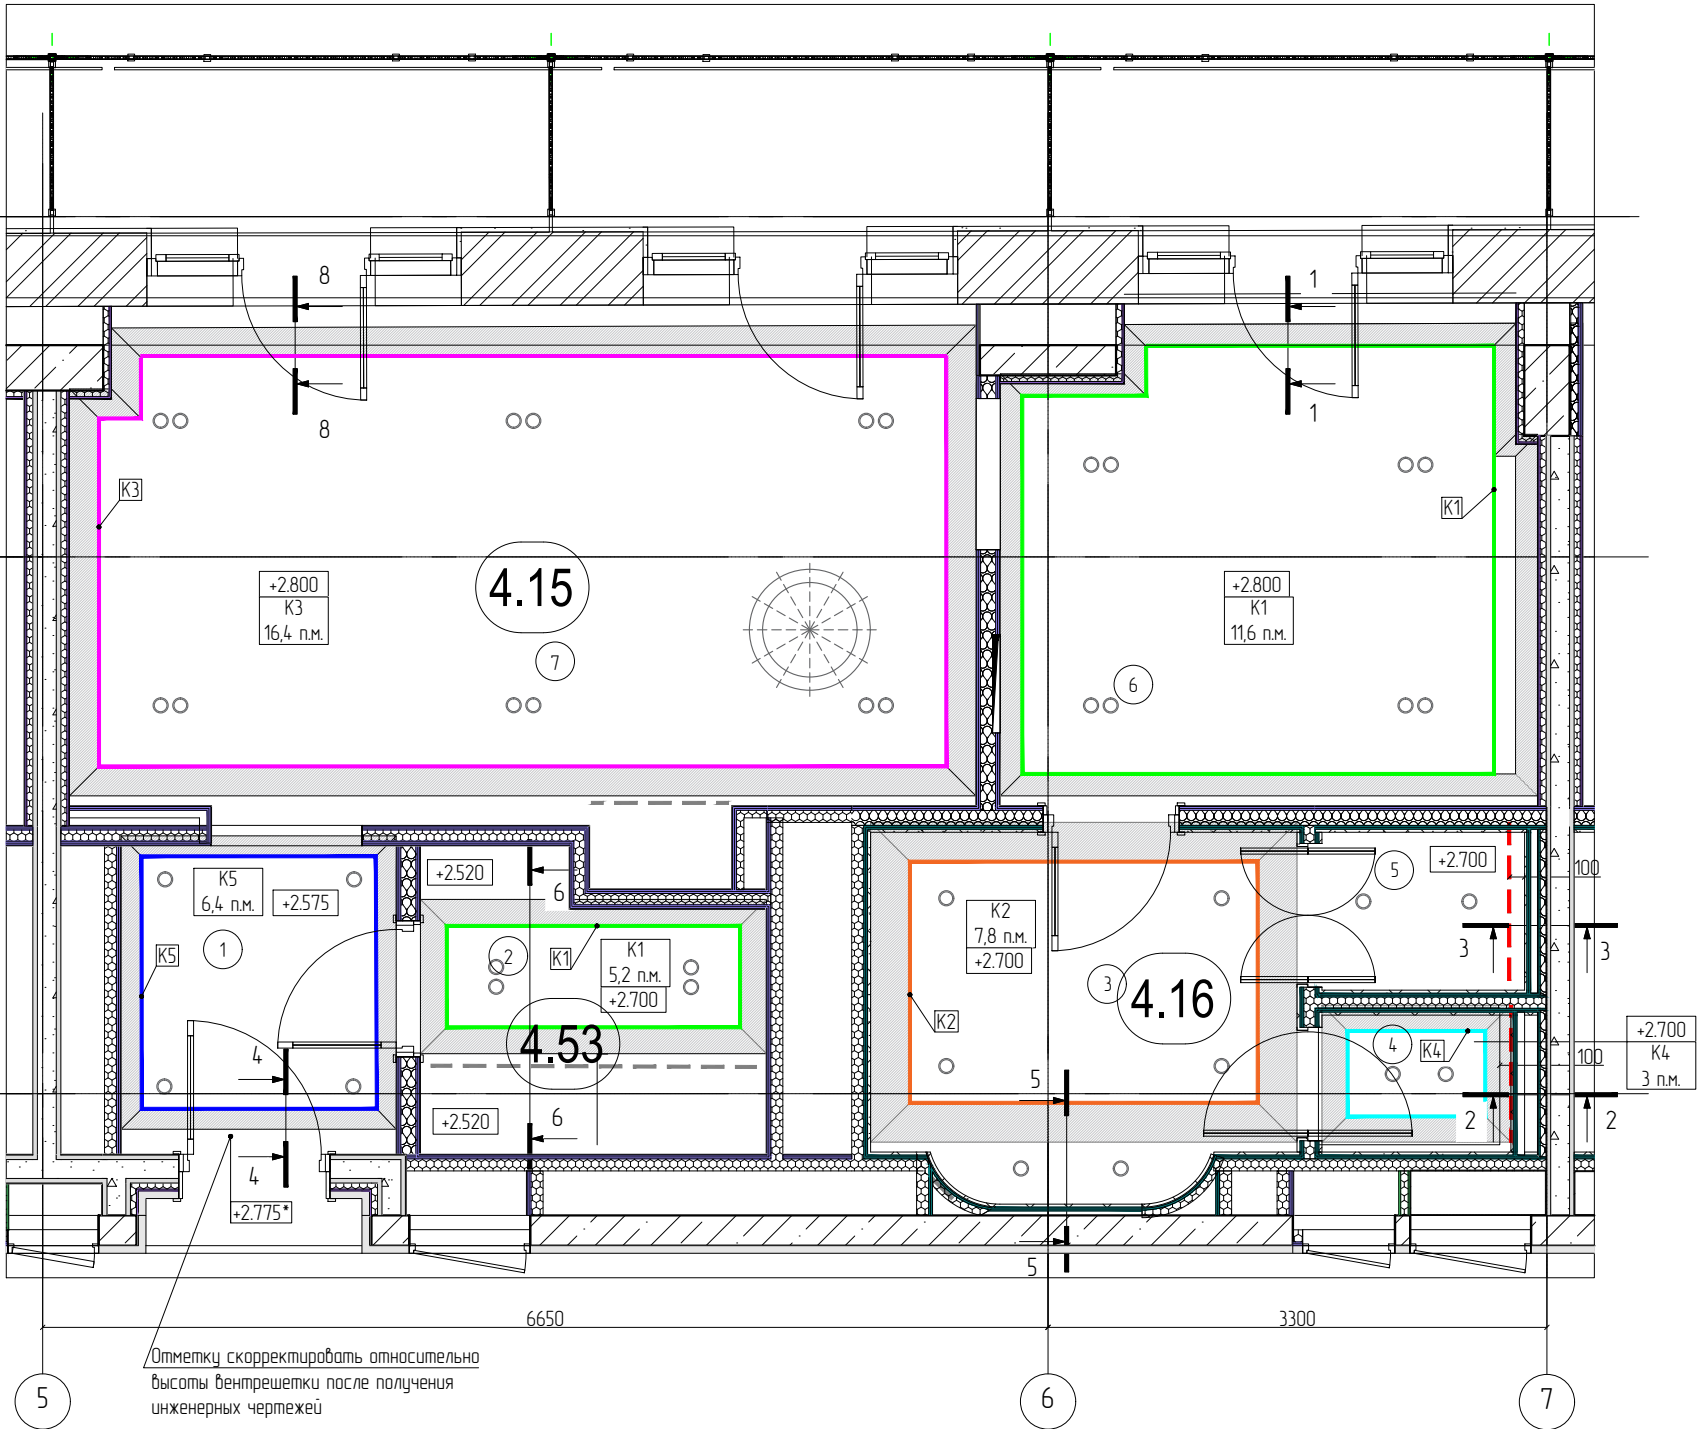

Гипсовые карнизы:

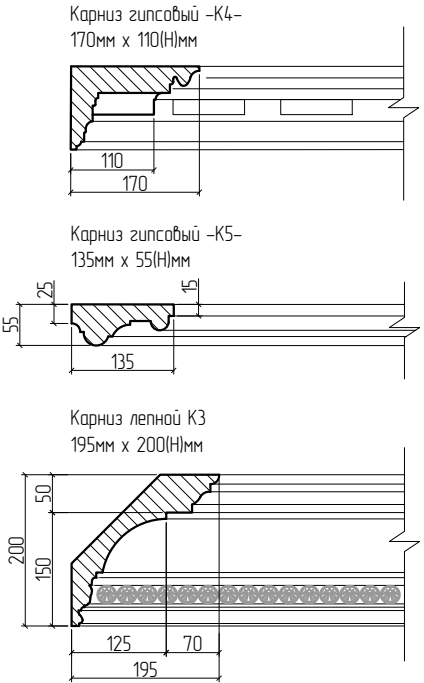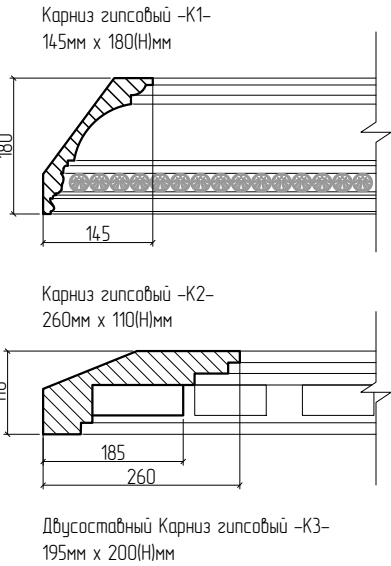

Спецификация карнизов номера Delux				
Тип	Изображение типоразмера	Описание	Вид	Кол-во
- K1 -		- Карниз гипсовый в окраске в тон потолка. Цвет по RAL: 9010. Н-180mm		11,6 поз.м. + 10% = 12,8 поз.м.
- K2 -		- Карниз гипсовый в окраске в тон потолка. Цвет по RAL: 9010. Н-110mm		7,8 поз.м. + 10% = 8,6 поз.м.
- K3 -		- Карниз гипсовый в окраске в тон потолка. Цвет по RAL: 9010. Н общ.-200mm для установки на стене.		16,4 поз.м. + 10% = 18,04 поз.м.
- K4 -		- Карниз гипсовый в окраске в тон потолка. Цвет по RAL: 9010. Н-110mm		3 поз.м. + 10% = 3,3 поз.м.
- K5 -		- Карниз гипсовый в окраске в тон потолка. Цвет по RAL: 9010. Н-55mm		6,4 поз.м. + 10% = 7,04 поз.м.

Условные обозначения:

- 1 - Номер помещения
- +2.800 - Отметка потолка от УЧП этажа
- K1 - Маркировка карниза
- - Полноэстрабаемые точечные светильники
- - Светодиодная подсветка


Примечания:

- Планировочное решение выполнено на основании чертежей раздела АР, ТЗ и концепции, утвержденной Заказчиком.
- При расхождении размеров на строительной площадке, превышающих ± 40 мм, их необходимо согласовать с Архитектором. В случае расхождения размеров между мелко масштабными чертежами и детализированными необходимо руководствоваться только размерами детализированного чертежа. Не использовать фрагменты плана как шаблон.
- Высоты даны от уровня чистого пола этажа. За отм. чистого пола принять верх чистового покрытия коридора.
- План смотреть совместно с планом расположения светильников и выключателей, электрических выводов и планом расположения розеток и выключателей. Разрезы см. детализированный чертеж: Узлы и детали потолка.


Заказчик: ООО «Приморская»						ПриМ-0001/2024-АИ.01-410		
Технический заказчик: АО «СЗ «ЛСР. Недвижимость - М»								
Развитие гостиницы «Приморская» в г. Сочи. Приспособление и сохранение объекта культурного наследия «Здание, где в годы Великой Отечественной войны размещались госпитали № 2095, 2120, 1941-1945 годы», расположенного по адресу: г. Сочи, Центральный район, ул. Саколова, д. 1.								
Изм.	Кол.уч.	Лист	№ док.	Подпись	Дата	Интерьерные решения. Гостиница "Приморская", корпус 1, 4 этаж, N 410. Тип "Делюкс"	Стадия	Лист
Разработал	Казыева А.Р.				02.02.26		РД	17
Проверил	Нобикова Е.				02.02.26			40
Н.контр.	Бахвалова Л.В.				02.02.26	План с маркировкой карнизов. М 1:50	ООО "Арх-И-Арм"	
ГАП	Сафронова Е.				02.02.26			

Лист дополнительной информации. Детализированный чертеж к плану потолка.
Узлы и детали потолка.


Разрез 1-1
Устройство шторной ниши и примыкания к балке
двухсоставного гипсового карниза

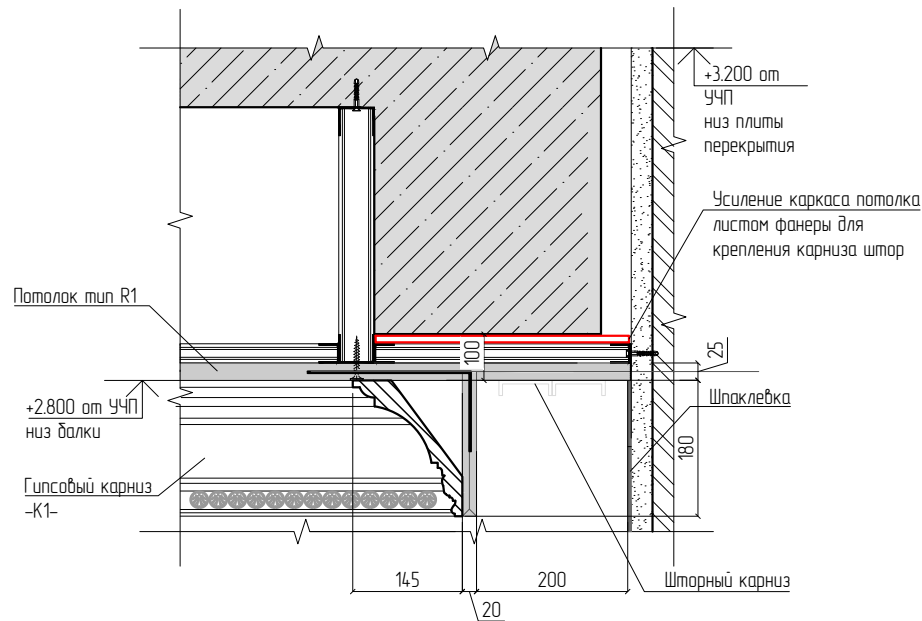


Разрез 2-2
Устройство закарнизной подсветки
в пом. N 4 (санузел).

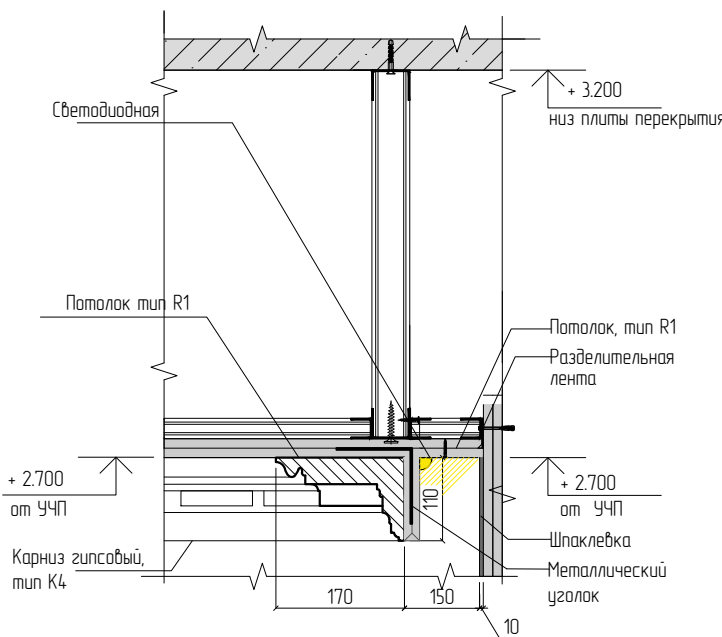


Разрез 3-3
Устройство закарнизной подсветки
в пом. N 5 (душевая).

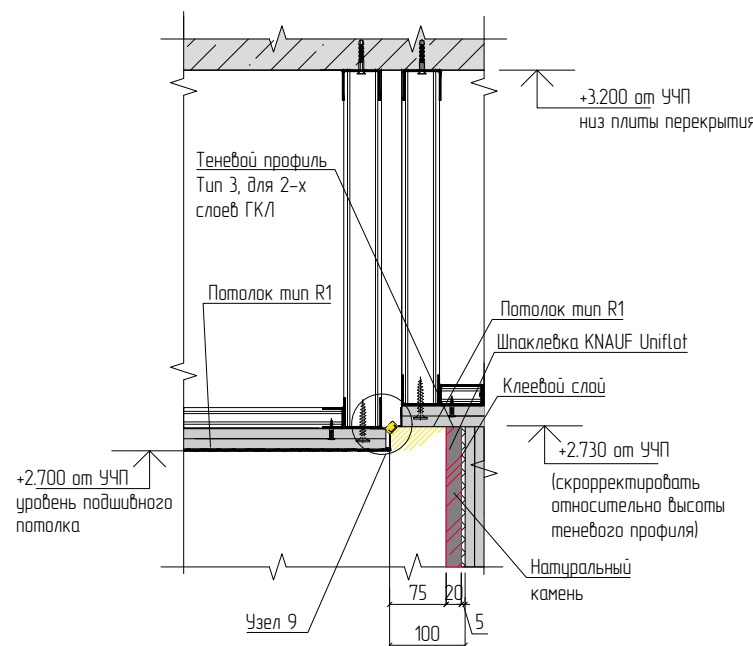


Узел 8
Устройство закарнизной подсветки
в пом. N 5 (душевая).


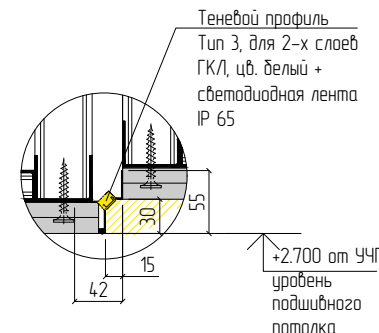


Разрез 4-4
Узел устройства ниши
для установки решетки вентрешетки в пом. N1 (прихожая)

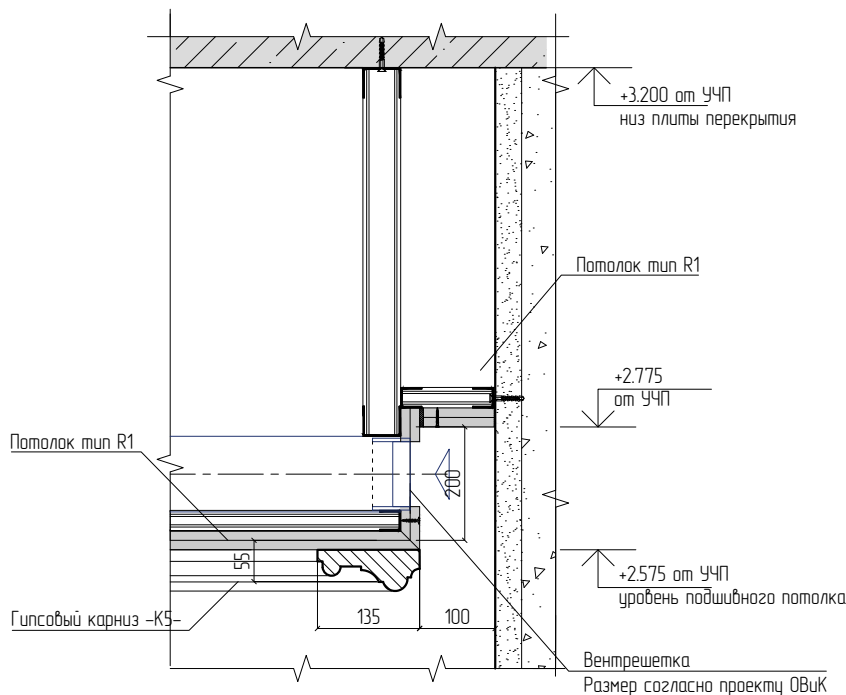

Разрез 8-8
пом. 2 (гардеробная)

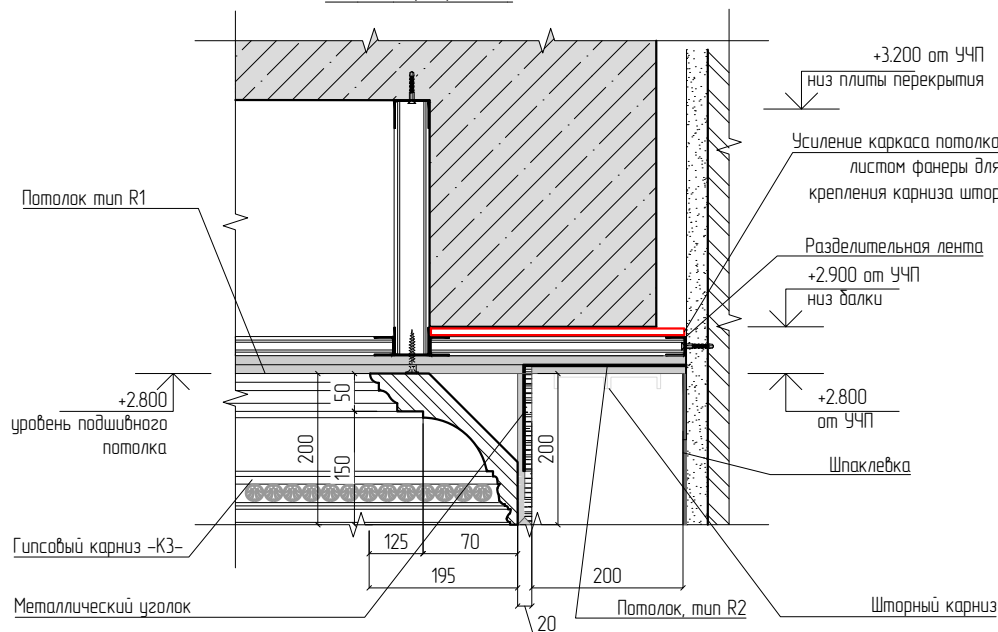

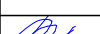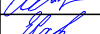						Заказчик: ООО «Приморская» Технический заказчик: АО «СЗ «ЛСР. Недвижимость – М»				ПриМ-0001/2024-АИ.01-410		
						Развитие гостиницы «Приморская» в г. Сочи. Приспособление и сохранение объекта культурного наследия «Здание, где в годы Великой Отечественной войны размещались госпитали № 2095, 2120, 1941-1945 годы», расположенного по адресу: г. Сочи, Центральный район, ул. Соколова, д. 1.						
Изм.	Кол.уч.	Лист	№ док.	Подпись	Дата							
Разработал	Казыева А.Р.				02.02.26	Интерьерные решения. Гостиница "Приморская", корпус 1, 4 этаж, N 410. Тип "Делюкс"				Стадия	Лист	Листов
Проверил	Нобикова Е.				02.02.26					РД	18	40
Н.контр.	Бахдалова Л.В.				02.02.26	Детализированный чертеж к плану потолка. Узлы и детали потолка.				ООО "Арх-И-Арт"		
ГАП	Сафронова Е.				02.02.26							

Л

К

И

2250

3550

6650

4.15

4.53

4.16

1

2

3

4

5

6

7

Вид В

Вид А

Вид Б

24 Устройство трапа 100x100мм

х.б. для раковины

з.б. для раковины

Привязку сливного отверстия в полу скорректировать после получения проекта ВК

Условные обозначения:

1

2

3

4

5

6

7

Номер помещения

Сохраняемые конструкции

Возводимые перегородки из газобетонного блока (D600 600x125x250 с облицовкой из акустической панели АкустикГипс Basic 40), толщина 240мм

Ограждающие перегородки по технологии шахтных стен KNAUF

Возводимые стены, ГК/ЛВ по металлокаркасу в 2 слоя 12,5мм с перехлестом шва, с шумоизоляцией внутри

Возводимые стены, газобетонные блоки Ytong 50мм

размеры даны до центра сантехнических приборов

Примечания:

1. Планировочное решение выполнено на основании чертежей раздела АР, ТЗ и концепции, утвержденной Заказчиком.

2. При расхождении размеров на строительной площадке, превышающих ± 40 мм, их необходимо согласовать с Архитектором. В случае расхождения размеров между мелко масштабными чертежами и детализированными необходимо руководствоваться только размерами детализированного чертежа. Не использовать фрагменты плана как шаблон.

3. Высоты даны от уровня чистого пола этажа. За отм. чистого пола принять верх чистового покрытия коридора.

4. План смотреть совместно с Детализированными чертежами: Развертки по пом. N2 (су), N4(ванная), N5(су), N6(ванная), а так же со Спецификацией отделочных материалов.

Экспликация помещений

№	Наименование	Площадь м2
1	Прихожая	3,74
2	Гардеробная комната	4,18
3	Ванная комната	6,77
4	Санузел	12
5	Душевая	1,56
6	Спальная комната	10,45
7	Гостиная комната	19,37
S общая		47,3

Спецификация сантехнического оборудования номера Deluxe

Марка	Описание	Отделка	Кол-во
-1-	- Duravit Cape Cod 700459000000000 Ванна отдельная 1650x780x630 мм белый, (1680x785 мм размер по проекту), арт: 700459000000000	White finish	1
-2-	- Смеситель напольный GESSI BATH TUB MIXER Bath tub Mixer 031 chrome+внутренняя часть, арт. 65128+65099	031 chrome	1
-3-	- Раковина встраиваемая снизу под столешницу без отверстий Duravit Architec 375мм. Арт: 319370000	White ceramic finish chrome	2
-4-	- Сифон для раковины Gessi 01377.031		2
-5-	- Смеситель GESSI MIXER TAP арт. 65011+29263 bassin flap	031 chrome	2
-6-	- Унитаз подвесной длина 58 см. White ceramic+сиденье белый пластик (64890000). DURAVIT	White ceramic	1
-7-	- Инсталляция Geberit Omega 12 для подвесного унитаза, высота 980мм, глубина ботр. 140мм		1
-8-	- Клавиша двойного смыка 115.085.KH.1, GEBERIT	031 chrome	1
-9-	- Гигиенический душ Bossini Paloma. E37005B00030015, хром	031 chrome	1
-10-	- Подвесной ершик GESSI TOILET BRUSH арт. 65419.	031 chrome	1
-11-	- Мыльница GESSI SOAP HOLDER арт. 65401.	031 chrome	1
-12-	- Бумагодержатель GESSI PAPER TOILET ROLL HOLDER арт. 65449.	031 chrome	1
-13-	- Полотенцедержатель GESSI TOWEL RAIL арт. 65497.	031 chrome	1
-14-	- Крючок одинарный настенный GESSI ROBE HOOK Арт. 65521	031 chrome	2
-15-	- Полотенцесушитель электрический SBORDONI TOWEL HEATER sbspar4/2	chrome	1
-16-	- Полотенцедержатель GESSI VENTI20 65509 PORTA SALVIETTA ANELLO.	031 chrome	1
-17-	- Мусорное ведро DEVON&DEVON PEDAL BIN Waltz	Chrome	2
-18-	- Душевая лейка GESSI SHOWER HEAD арт. 65153	031 chrome	1
-19-	- Душевой комплект, состоящий из вывода воды, держателя, шланга 150 м и лейки GESSI SHOWER SET арт. 65123	031 chrome	1
-20-	- Термостат GESSI SHOWER MIXER 65079#031 + внутренняя часть 44673	031 chrome	1
-23-	- Канал для укладки натурального камня 900 мм нержавеющая сталь+сифон+комплектующие (высота стяжки 100 мм), L-900/800 мм, произ-ль TECE. арт. TECEdrainline 650800/650900	chrome	1
-24-	- Основа для плитки 100 мм. из нержавеющей стали + сифон + комплектующие (высота стяжки 100 мм). арт. 36014 00+3660016. Произ-ль TECE.	chrome	1

Примечание: спецификация по помещениям с аксессуарами см. детализированные чертежи, листы: Развертка стен по пом.N2(су), N4(ванная), N5 (санузел), N6(душевая).

Заказчик: ООО «Приморская»

Технический заказчик: АО «СЗ «ЛСР. Недвижимость – М»

Развитие гостиницы «Приморская» в г. Сочи. Приспособление и сохранение объекта культурного наследия «Здание, где в годы Великой Отечественной войны размещались госпитали № 2095, 2120, 1941-1945 годы», расположенного по адресу: г. Сочи, Центральный район, ул. Соколова, д. 1.

Изм.

Кол.уч.

Лист

№ док.

Подпись

Дата

Разработал

Проверил

Н.контр.

ГАП

Казыева А.Р.

Нобикова Е.

Бахвалова Л.В.

Сафронова Е.

02.02.26

02.02.26

02.02.26

02.02.26

Интерьерные решения. Гостиница "Приморская", корпус 1, 4 этаж, N 410. Тип "Делюкс"

План с привязкой сантехники. М 1:50

000 "Арх-И-Арт"

Стадия

Лист

Листов


РД

19

40

Формат А3

Развертка стен А-А. Помещение №1 (прихожая).
Корпус 1, 4 этаж, N 410. Тип "Делюкс"

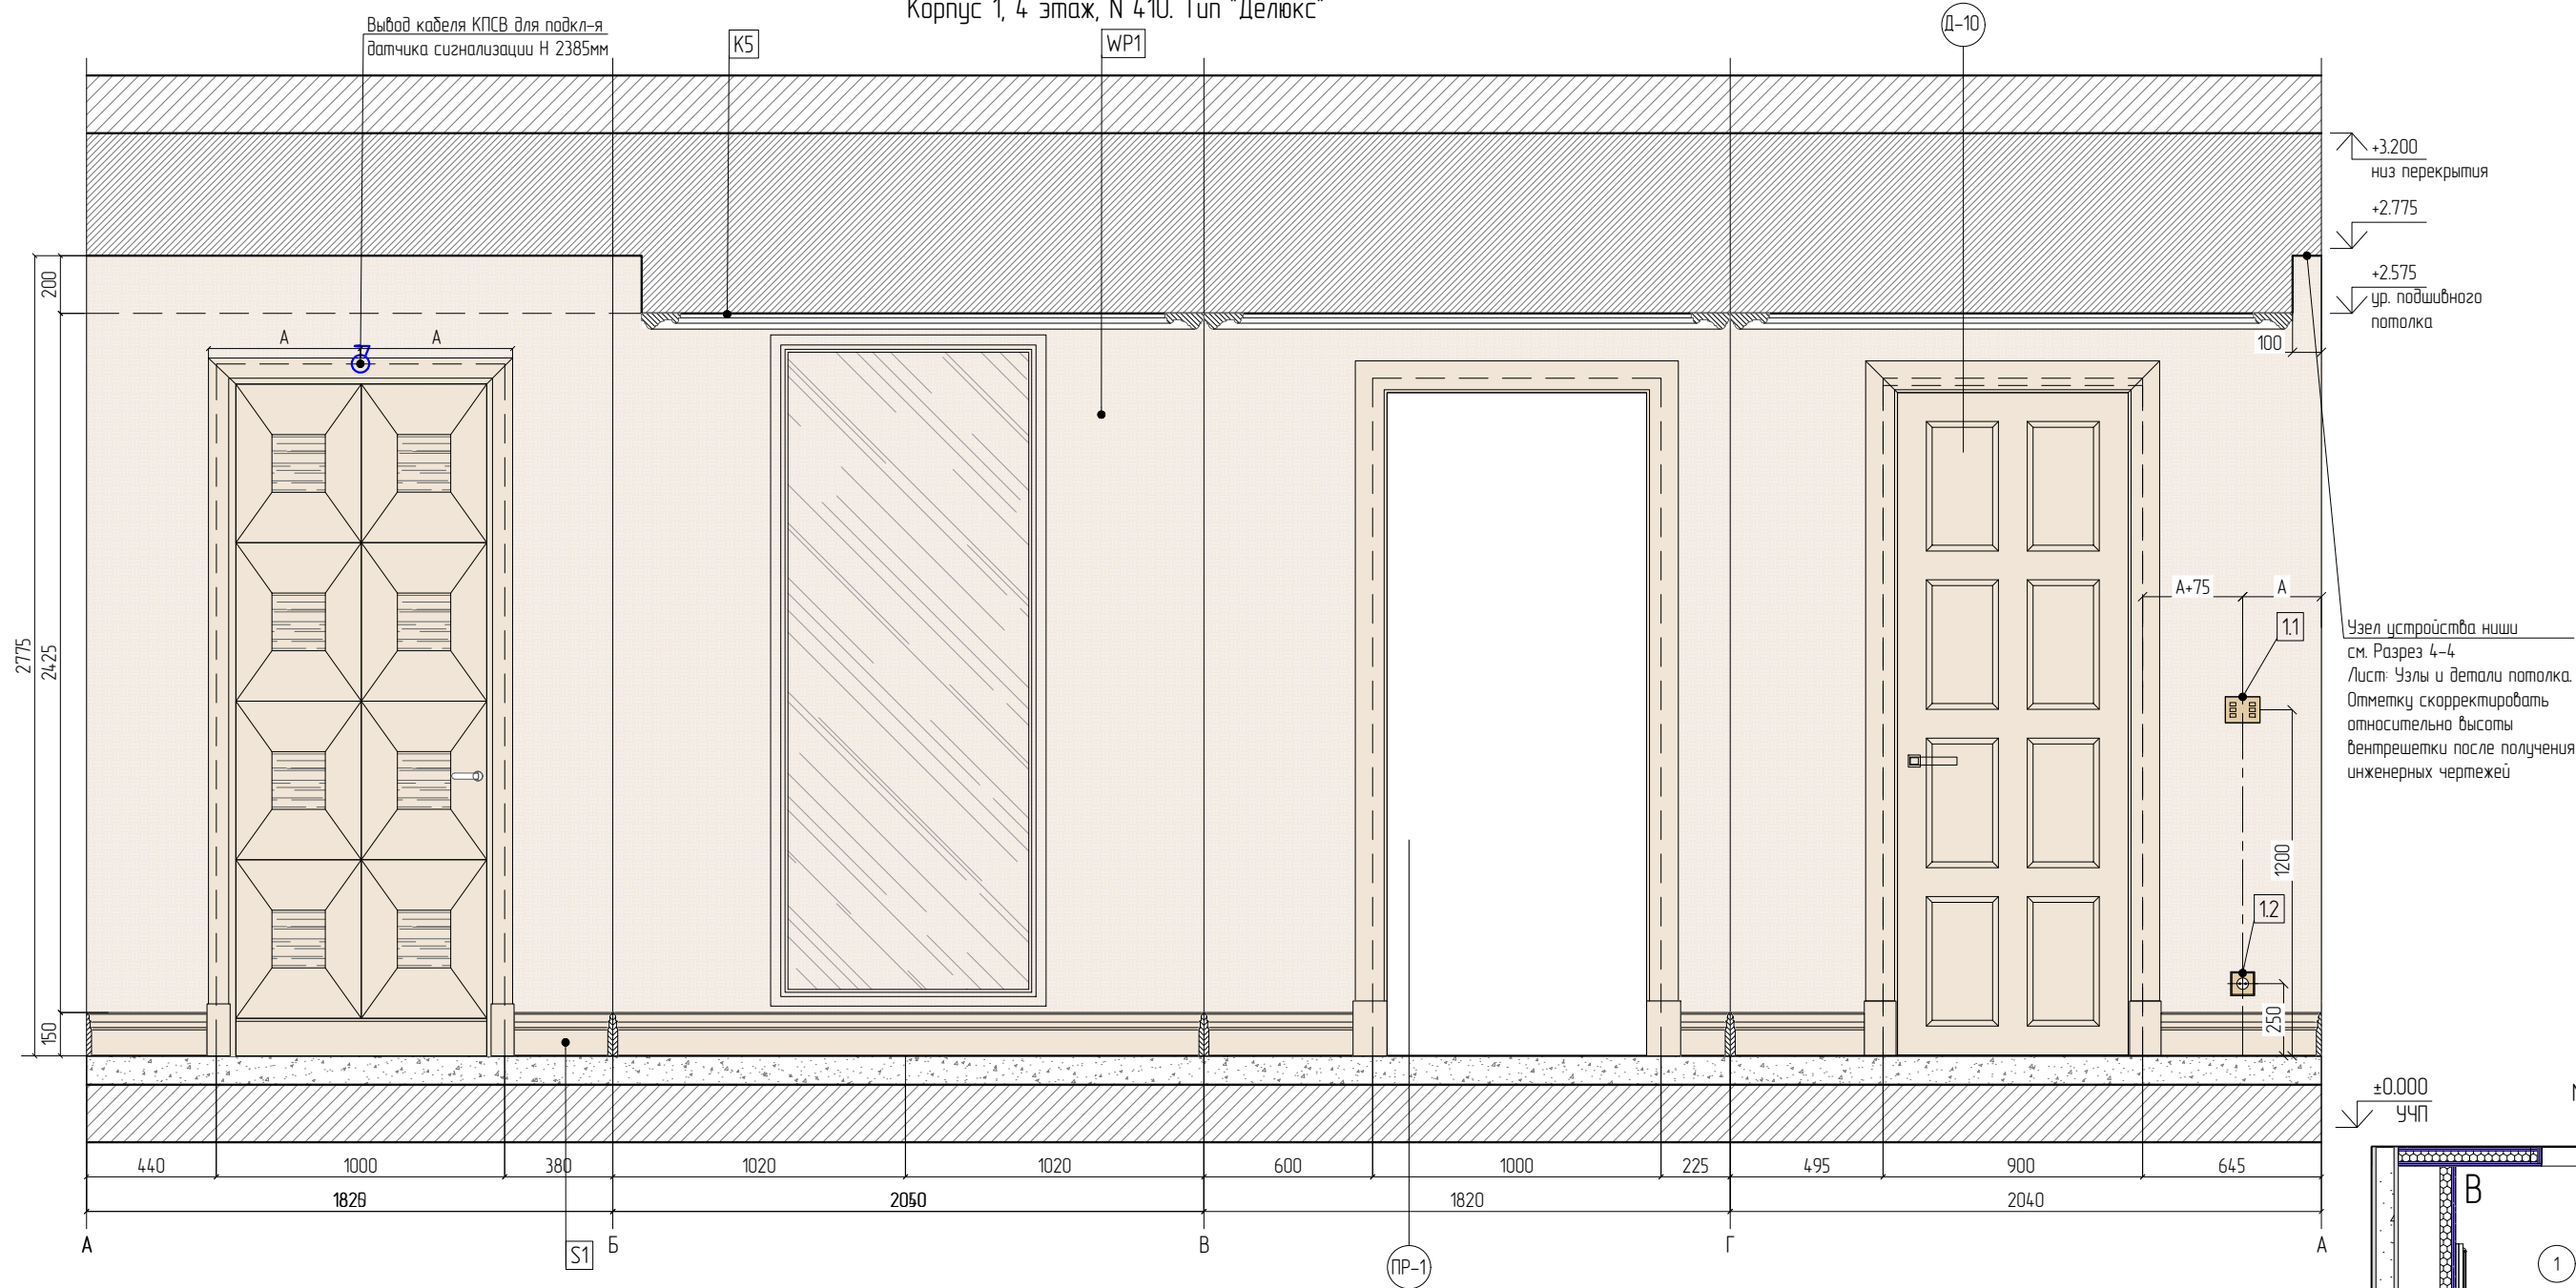

Условные обозначения:



- Панель управления



- Розетка 220V



- Маркировка дверей



- Нумерация электрооборудования
(Таблица с оснащением модулей для
управления всем освещением см. лист:
План расположения розеток.)



- Маркировка осветительного оборудования



- Слаботочный электрический выход



- Электрический выход

- LED подсветка 1,8 м.п.



-WP1- Виниловые обои арт. Vinyl Island Raffia col. Sun Bleached 9441, произ-ль PHILLIP JEFFRIES, ширина рулона 132,1см (137,2 см) без обрезки
 $S_{общ. по пом.} = 7,14 + 10\% = 7,86 \text{ м}^2$



-K5- Карниз гипсовый 135мм x 55мм в окраске в тон потолка. Цвет по RAL: 9010.
 $L_{общ. по пом.} = 6,68 + 10\% = 7,35 \text{ м.п.}$




-S1- Плинтус из массива натурального дерева, Ash Wood (ясень), покрытие матовым бесцветным лаком. Н-150мм, толщина 17мм
 $L_{общ. по пом.} = 2,62 + 10\% = 2,89 \text{ м.п.}$

Примечания:

- Планировочное решение выполнено на основании чертежей раздела АР, ТЗ и концепции, утвержденной Заказчиком.
- Высоты даны от уровня чистого пола этажа. За отм. чистого пола принять верх чистового покрытия коридора.
- Расчет отделочных материалов взят с запасом в 5-15%. Подсчет натурального камня скорректировать согласно раскроя Поставщика.
- Перед заказом встроенной мебели необходимо произвести замер силами инженеров от фирмы производителей. Чертежи встр. мебели см. Лист дополнительной информации к планировочному решению.
- Цвет и вид отделочных материалов согласовать с автором проекта.
- Таблица с оснащением модулей для управления всем освещением см. лист: План расположения розеток.

						Заказчик: ООО «Приморская» Технический заказчик: АО «СЗ «ЛСР. Недвижимость – М»				ПриМ-0001/2024-АИ.01-410		
						Развитие гостиницы «Приморская» в г. Сочи. Приспособление и сохранение объекта культурного наследия «Здание, где в годы Великой Отечественной войны размещались госпитали № 2095, 2120, 1941-1945 годы», расположенного по адресу: г. Сочи, Центральный район, ул. Соколова, д. 1.						
Изм.	Кол.уч.	Лист	№ док.	Подпись	Дата	Интерьерные решения. Гостиница "Приморская", корпус 1, 4 этаж, N 410. Тип "Делюкс"				Стадия	Лист	Листов
Разработал	Казыева А.Р.				02.02.26					РД	20	40
Проверил	Новикова Е.				02.02.26							
						Помещение №1 (прихожая) Маркировочный план. Развертка стен А-А. М 1:25				ООО "Арх-И-Арм"		
Н.контр.	Бахдалова Л.В.				02.02.26							
ГАП	Сафронова Е.				02.02.26							

Маркировочный план. Помещение №2 (гардеробная комната).
Корпус 1, 4 этаж, N 410. Тип "Делюкс"

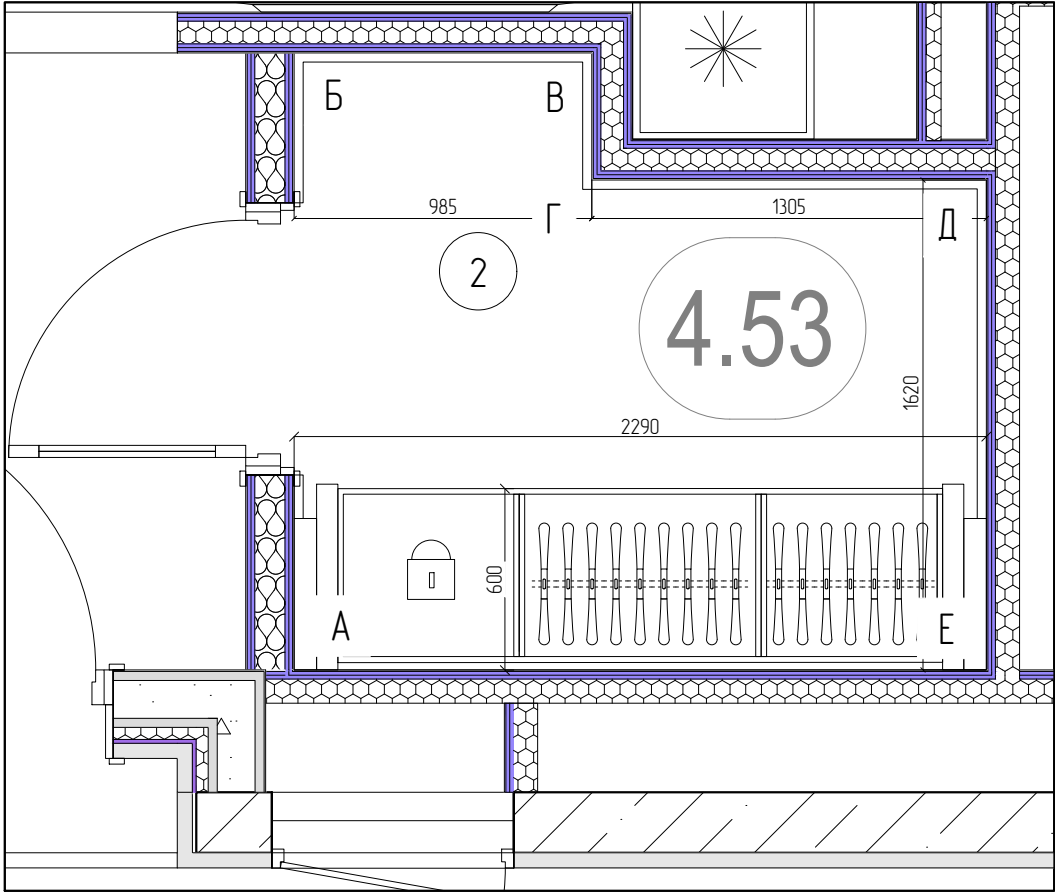

Согласовано				
Взам. инв. №				
Подп. и дата				
Инв. № подл.				


Условные обозначения:

2 - Номер помещения

Примечания:
1. Планировочное решение выполнено на основании чертежей раздела АР, ТЗ и концепции, утвержденной Заказчиком.

						Заказчик: ООО «Приморская» Технический заказчик: АО «СЗ «ЛСР. Недвижимость – М»				ПриМ-0001/2024-АИ.01-410		
						Развитие гостиницы «Приморская» в г. Сочи. Приспособление и сохранение объекта культурного наследия «Здание, где в годы Великой Отечественной войны размещались госпитали № 2095, 2120, 1941-1945 годы», расположенного по адресу: г. Сочи, Центральный район, ул. Соколова, д. 1.						
Изм.	Кол.уч.	Лист	№ док.	Подпись	Дата	Интерьерные решения. Гостиница "Приморская", корпус 1, 4 этаж, N 410. Тип "Делюкс"				Стадия	Лист	Листов
Разработал			Казыева А.Р.		02.02.26					РД	21	40
Проверил			Новикова Е.		02.02.26							
Н.контр.			Бахвалова Л.В.		02.02.26	Помещение №2 (гардеробная комната). Маркировочный план. М 1:25				ООО "Арх-И-Арм"		
ГАП			Сафронова Е.		02.02.26							

Развертка стен А-А. Помещение №2 (гардеробная комната).
Корпус 1, 4 этаж, N 410. Тип "Делюкс"

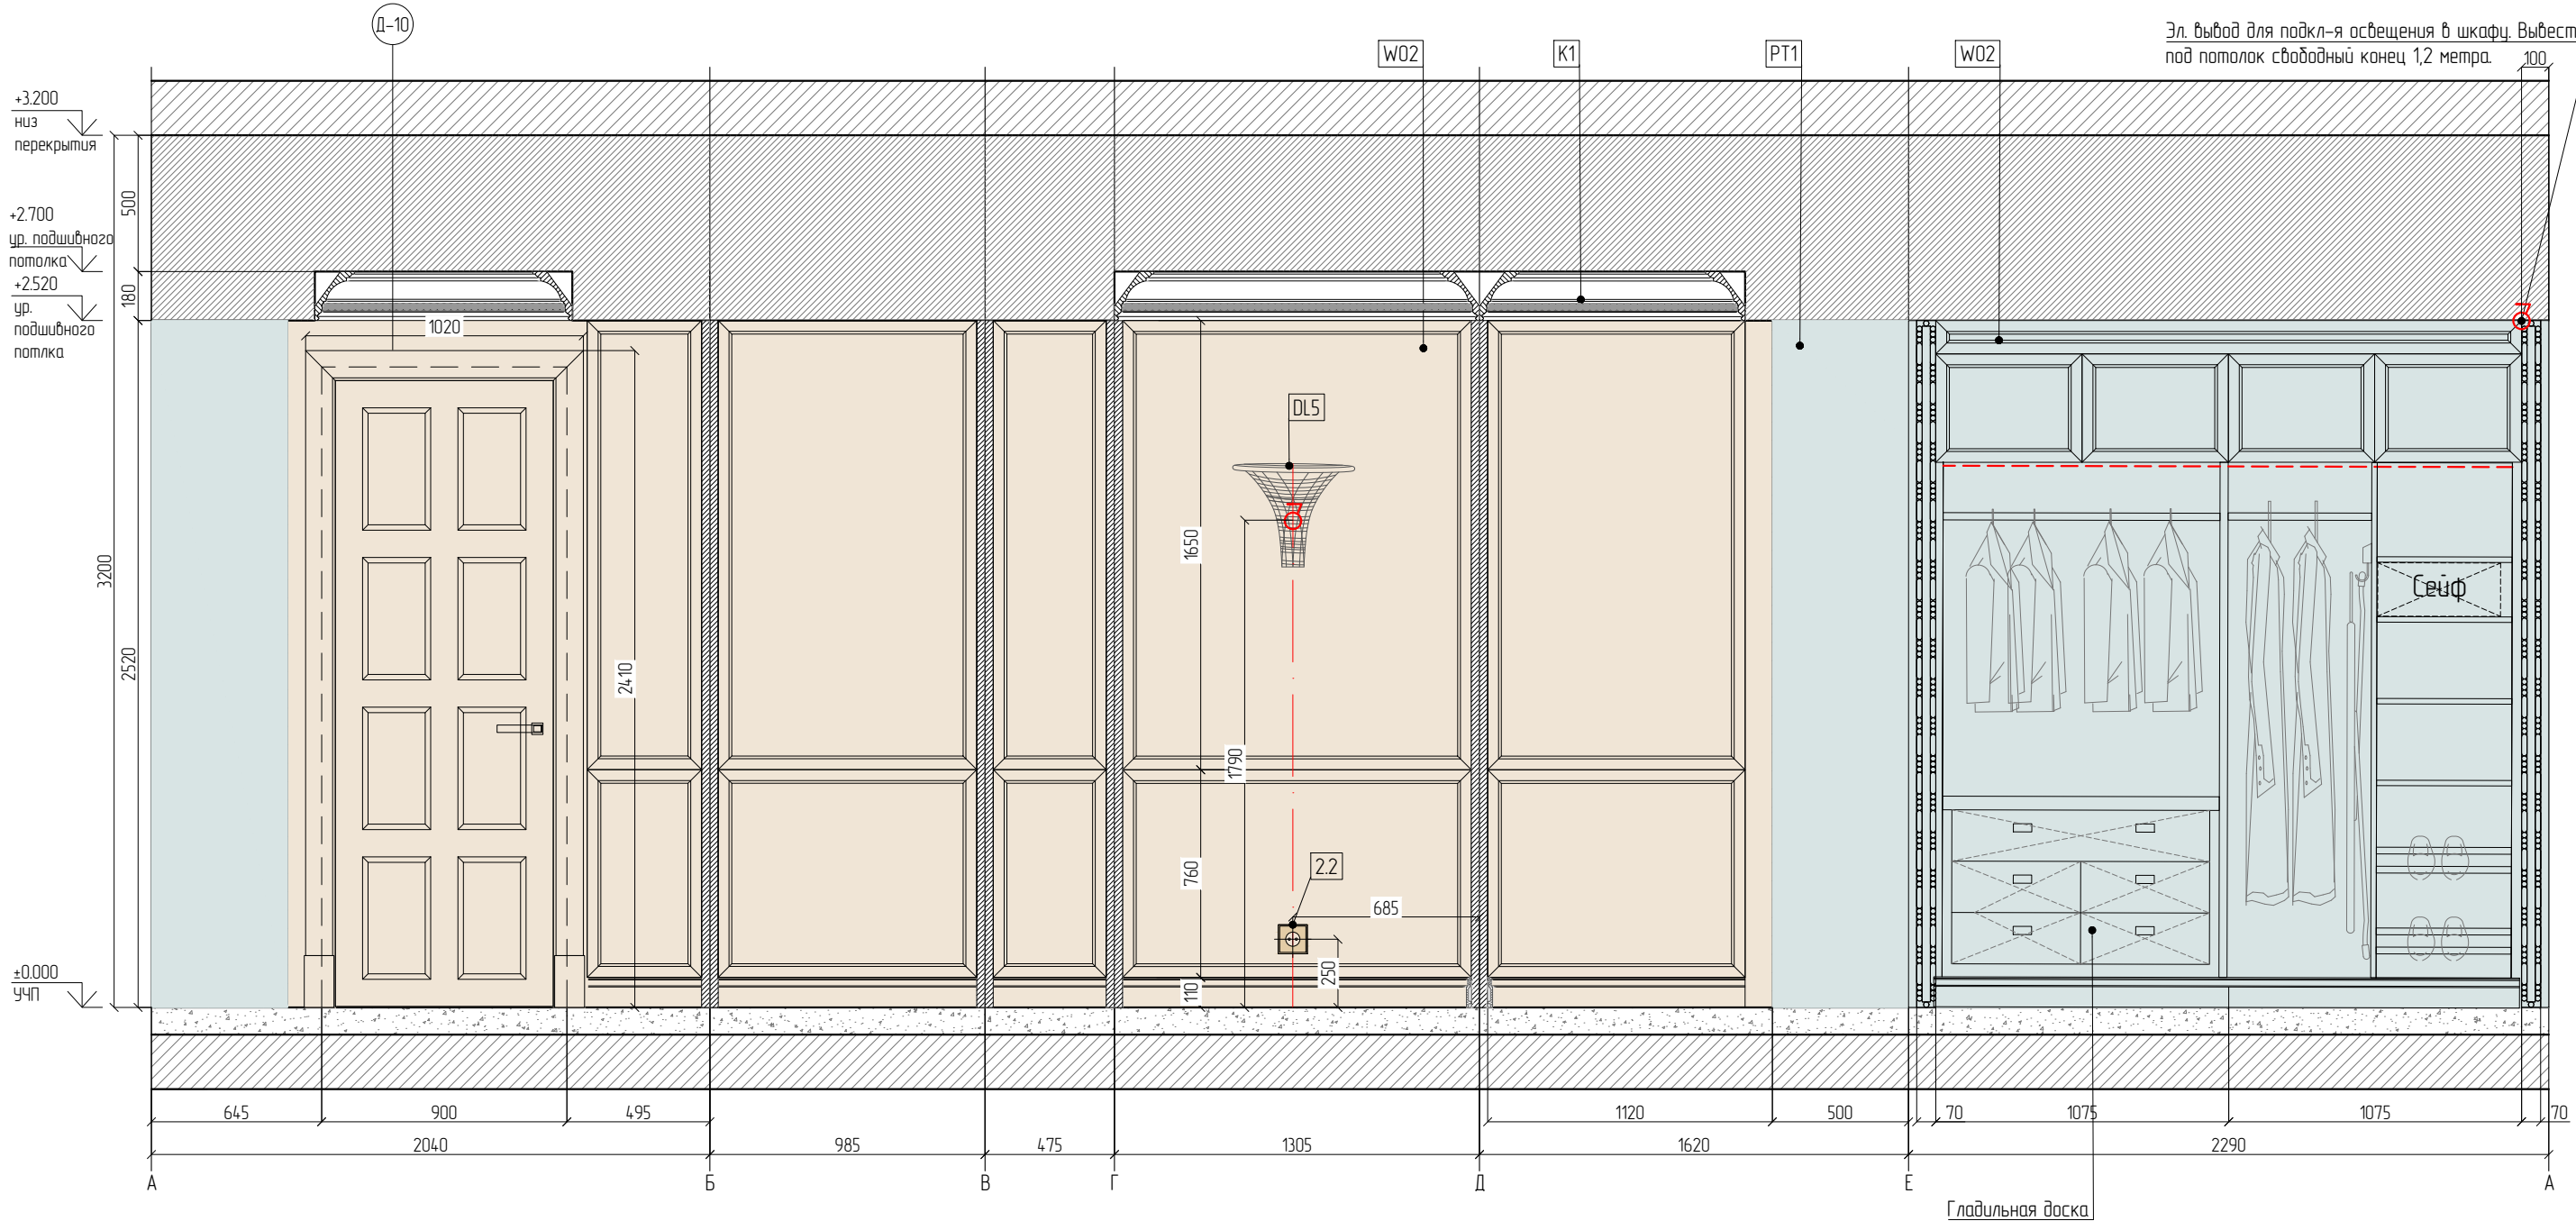

Согласовано					
Взам. инв. №					
Подп. и дата					
Инв. № подл.					

Условные обозначения

⊕ - Розетка 220V

Д-1 - Маркировка дверей и проемов

1.1 - Нумерация электрооборудования
(Таблица с оснащением модулей для управления всем освещением см. лист: План расположения розеток.)

DL1 - Маркировка осветительного оборудования

1 - Маркировка отделочных материалов

⊕ - Электрический вывод

--- - LED подсветка 4,3 м.л.

PT1

-PT1- высококачественная окраска по штукатурной поверхности в 2 слоя. Цвет по RAL: 9010, матовая
S=13,02 м2 + 10% = 14,32 м2

W02

-W02- Декоративная панель, Ash flowered sea wood, satin finish
S=6,74 м2 + 10% = 7,41 м2

K1


-K1- Карниз гипсовый окраске в тон потолка. Цвет по RAL: 9010.
H=180mm
Lобщая пок. = 6,43 м.л. +10%= 7,07 м.л.

Примечания:

1. Планировочное решение выполнено на основании чертежей раздела АР, ТЗ и концепции, утвержденной Заказчиком.
2. Высоты даны от уровня чистого пола этажа. За отм. чистого пола принять верх чистового покрытия коридора.
3. Расчет отделочных материалов взят с запасом в 5-15%. Подсчет натурального камня скорректировать согласно раскроя Поставщика.
4. Перед заказом встроенной мебели необходимо произвести замер силами инженеров от фирм производителей.
5. Цвет и вид отделочных материалов согласовать с автором проекта.
6. Таблица с оснащением модулей для управления всем освещением см. лист: План расположения розеток.

						Заказчик: ООО «Приморская» Технический заказчик: АО «СЗ «ЛСР. Недвижимость – М»			ПриМ-0001/2024-АИ.01-410			
						Развитие гостиницы «Приморская» в г. Сочи. Приспособление и сохранение объекта культурного наследия «Здание, где в годы Великой Отечественной войны размещались госпитали № 2095, 2120, 1941-1945 годы», расположенного по адресу: г. Сочи, Центральный район, ул. Соколова, д. 1.						
Изм.	Кол.уч.	Лист	№ док.	Подпись	Дата	Интерьерные решения. Гостиница "Приморская", корпус 1, 4 этаж, N 410. Тип "Делюкс"			Стадия	Лист	Листов	
Разработал	Казыева А.Р.				02.02.26				РД	22	40	
Проверил	Новикова Е.				02.02.26	Помещение №2 (гардеробная комната). Развертка стен А-А. М 1:25			ООО "Арх-И-Арм"			
Н.контр.	Бахвалова Л.В.				02.02.26							
ГАП	Сафронова Е.				02.02.26							

План с привязкой сантехники и маркировкой оборудования. Помещение № 3 (ванная комната).
Корпус 1, 4 этаж, N 410. Тип "Делюкс"

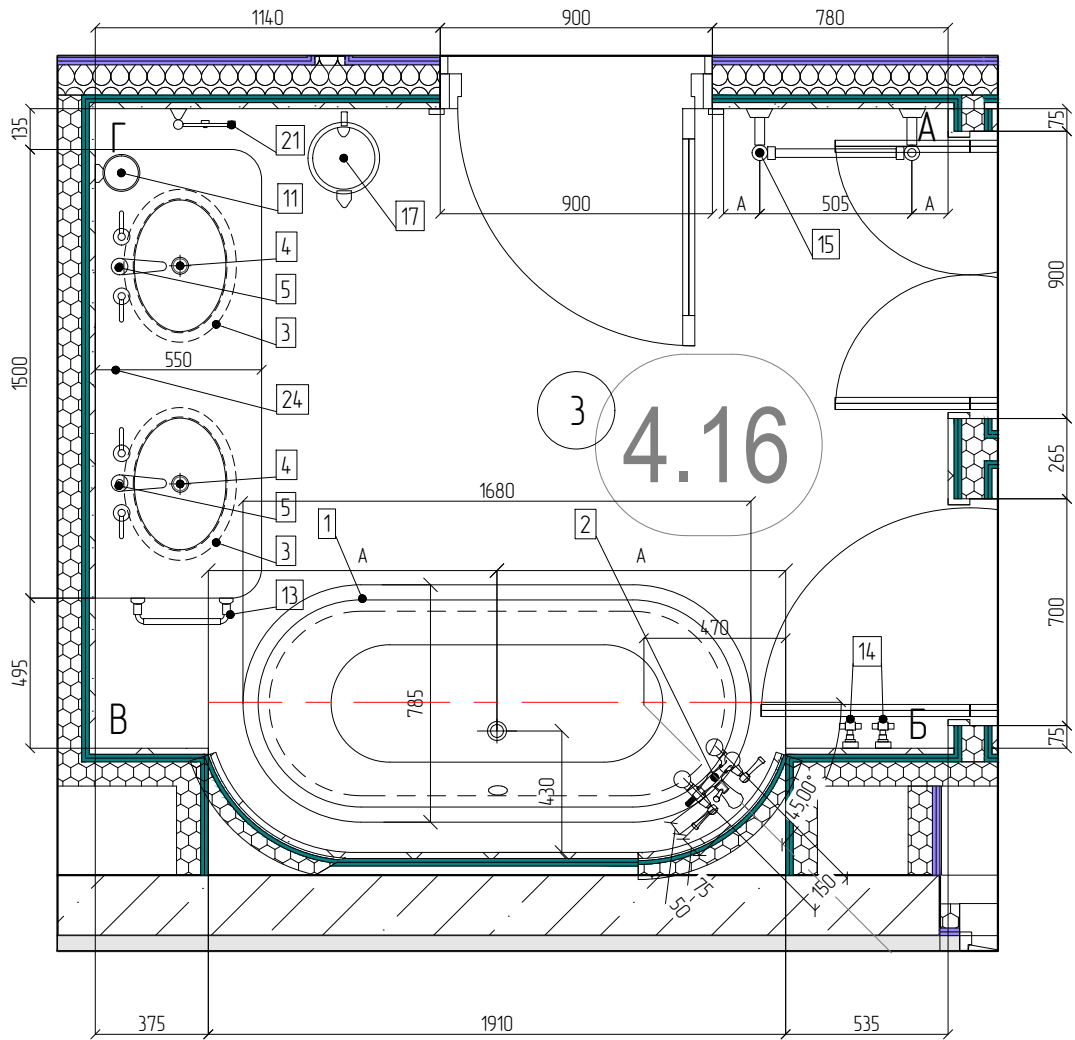

Условные обозначения:

- 1 - Номер помещения
- 1 - Маркировка сантехнического оборудования
- Устройство трапа 100х100мм


Спецификация сантехнического оборудования номера Delux			
Марка	Описание	Отделка	Кол-во
-1-	- Duravit Care Cod 70045900000000 Ванна отдельная 1650x780x630 мм белая, (1680x785 мм размер по проекту), арт: 70045900000000	White ceramic	1
-2-	- Смеситель напольный GESSI BATH TUB MIXER Bath tub Mixer 031 chrome+внутренняя часть, арт. 65128+65099	031 chrome	1
-3-	- Раковина встраиваемая снизу под столешницу без отверстий Duravit Architec 375мм. Арт: 319370000	White ceramic	2
-4-	- Сифон для раковины Gessi 01377.031	finish chrome	2
-5-	- Смеситель GESSI MIXER TAP арт. 65011+29263 basin flap	031 chrome	2
-11-	- Мыльница GESSI SOAP HOLDER арт. 65401.	031 chrome	1
-13-	- Полотенцедержатель GESSI TOWEL RAIL арт. 65497.	031 chrome	1
-14-	- Крючок одинарный настенный GESSI ROBE HOOK Art. 65521	031 chrome	2
-15-	- Полотенцесушитель электрический SBORDONI TOWEL HEATER sbpar4/2	chrome	1
-17-	- Мусорное ведро DEVON-DEVON PEDAL BIN Waltz	Chrome	1
-21-	- Косметическое зеркало AXOR SHAVING MIRROR axor montreux	Chrome	1
-24-	- Основа для плитки 100 мм. из нержавеющей стали + сифон + комплектующие (высота стяжки 100 мм). арт. 36014 00+3660016. Произ-ль TEECE.	Chrome	1
Примечание: см. Спецификацию отделочных материалов и оборудования			

Примечания:
1. Планировочное решение выполнено на основании чертежей раздела АР, ТЗ и концепции, утвержденной Заказчиком.
2. Высоты даны от уровня чистого пола этажа. За отм. чистого пола принять верх чистового покрытия коридора.

Согласовано					
Взам. инв. №					
Подп. и дата					
Инв. № подл.					


Заказчик: ООО «Приморская»						ПриМ-0001/2024-АИ.01-410		
Технический заказчик: АО «СЗ «ЛСР. Недвижимость – М»								
Развитие гостиницы «Приморская» в г. Сочи. Приспособление и сохранение объекта культурного наследия «Здание, где в годы Великой Отечественной войны размещались госпитали № 2095, 2120, 1941-1945 годы», расположенного по адресу: г. Сочи, Центральный район, ул. Саколова, д. 1.								
Изм.	Кол.уч.	Лист	№ док.	Подпись	Дата	Интерьерные решения. Гостиница "Приморская", корпус 1, 4 этаж, N 410. Тип "Делюкс"	Стадия	Лист
Разработал	Казыева А.Р.	02.02.26					РД	23
Проверил	Новикова Е.	02.02.26						40
						План с привязкой сантехники и маркировкой оборудования. Помещение №3 (ванная комната). М 1:25	ООО "Арх-И-Арм"	
Н.контр.	Бахвалова Л.В.	02.02.26						
ГАП	Сафронова Е.	02.02.26						

План раскладки напольных покрытий. Помещение N3 (ванная).
Корпус 1, 4 этаж, N 410. Тип "Делюкс"

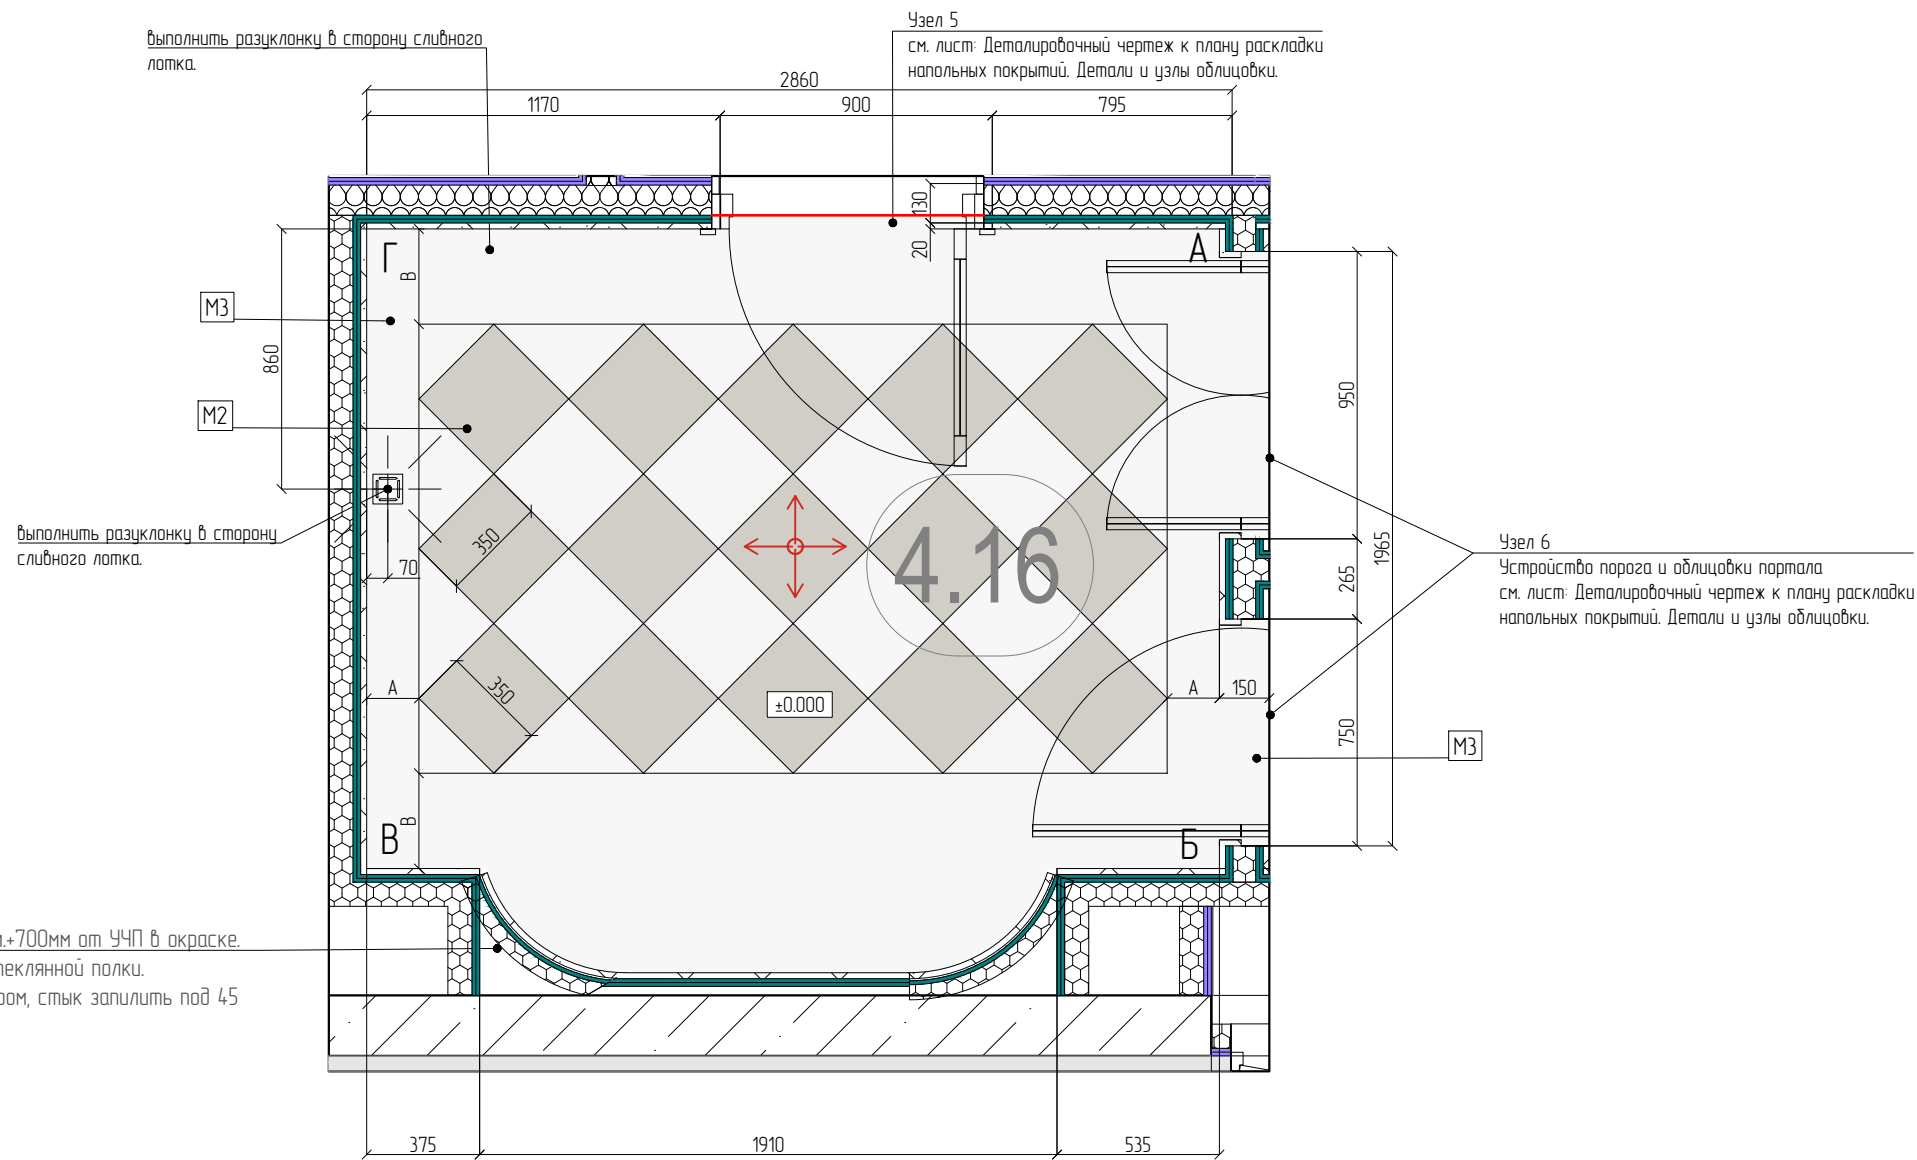

Устройство ниши H690мм на отм.+700мм от УЧП в окраске.
Предусмотреть крепление для стеклянной полки.
Нижняя полка в облицовке мрамором, стык запилить под 45
градусов, снять фаску по краю.
См. Узел 9, лист 29.

Облицовка полки
L200xP140xW20мм

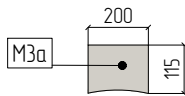

Условные обозначения:

- 1 - Номер помещения
- ±0.000 - Уровень чистого пола этажа
- 1 - Маркировка отделочных материалов
- - Направление укладки
- - Устройство трапа 100x100мм

Примечания:



- Планировочное решение выполнено на основании чертежей раздела АР, ТЗ и концепции, утвержденной Заказчиком.
- Расчет отделочных материалов взят с запасом в 10%. Подсчет натурального камня скорректировать согласно раскроя Поставщика.
- Перед заказом встроенной мебели необходимо произвести замер силами инженеров от фирм производителей. Чертежи мебели, МДФ и стеновые панели см. Лист дополнительной информации к планировочному решению.
- Цвет и вид отделочных материалов согласовать с автором проекта.
- На границе разных напольных покрытий переходной шов закрыть металлическим порогом. Шов выполнить по центру дверного полотна см. План заполнения дверных проемов.
- Начало раскладки на чертеже указано стрелками. Весь натуральный камень выкладывать с минимальным швом, образовавшиеся зазоры обрабатывать затиркой в цвет камня.

Спецификация напольных покрытий номера Deluxe				
Тип	Изображение типоразмера	Описание	Вид	Кол-во
- M2 -		- натуральный камень Carrara marble, матовый, толщина 20мм		1,84 + 10% = 2,02 м²
- M3 -		- натуральный камень Calacatta Borghini marble, матовый, толщина 20мм		5,1 + 10% = 5,61 м²
		- Металлический профиль, L = 900мм, ширина 13мм, цвет: брашированная бронза		0,94 поз.м. + 10% = 1,03 поз.м.
Примечание: см. Спецификация отделочных материалов и оборудования				

Заказчик: ООО «Приморская»						ПриМ-0001/2024-АИ.01-410		
Технический заказчик: АО «СЗ «ЛСР. Недвижимость – М»								
Развитие гостиницы «Приморская» в г. Сочи. Приспособление и сохранение объекта культурного наследия «Здание, где в годы Великой Отечественной войны размещались госпитали № 2095, 2120, 1941-1945 годы», расположенного по адресу: г. Сочи, Центральный район, ул. Саколова, д. 1.								
Изм.	Кол.уч.	Лист	№ док.	Подпись	Дата	Интерьерные решения. Гостиница "Приморская", корпус 1, 4 этаж, N 410. Тип "Делюкс"	Стадия	Лист
Разработал	Казыева А.Р.	02.02.26					РД	24
Проверил	Нобикова Е.	02.02.26						40
Н.контр.	Бахвалова Л.В.	02.02.26				Помещение №3 (ванная комната). План раскладки напольных покрытий. М 1:25	ООО "Арх-И-Арм"	
ГАП	Сафронова Е.	02.02.26						

Схема привязки сантехники. Развертка стен А-В. Лист 1. Помещение № 3 (ванная комната).
Корпус 1, 4 этаж, N 410. Тип "Делюкс"

План с маркировкой разверток. М 1:50

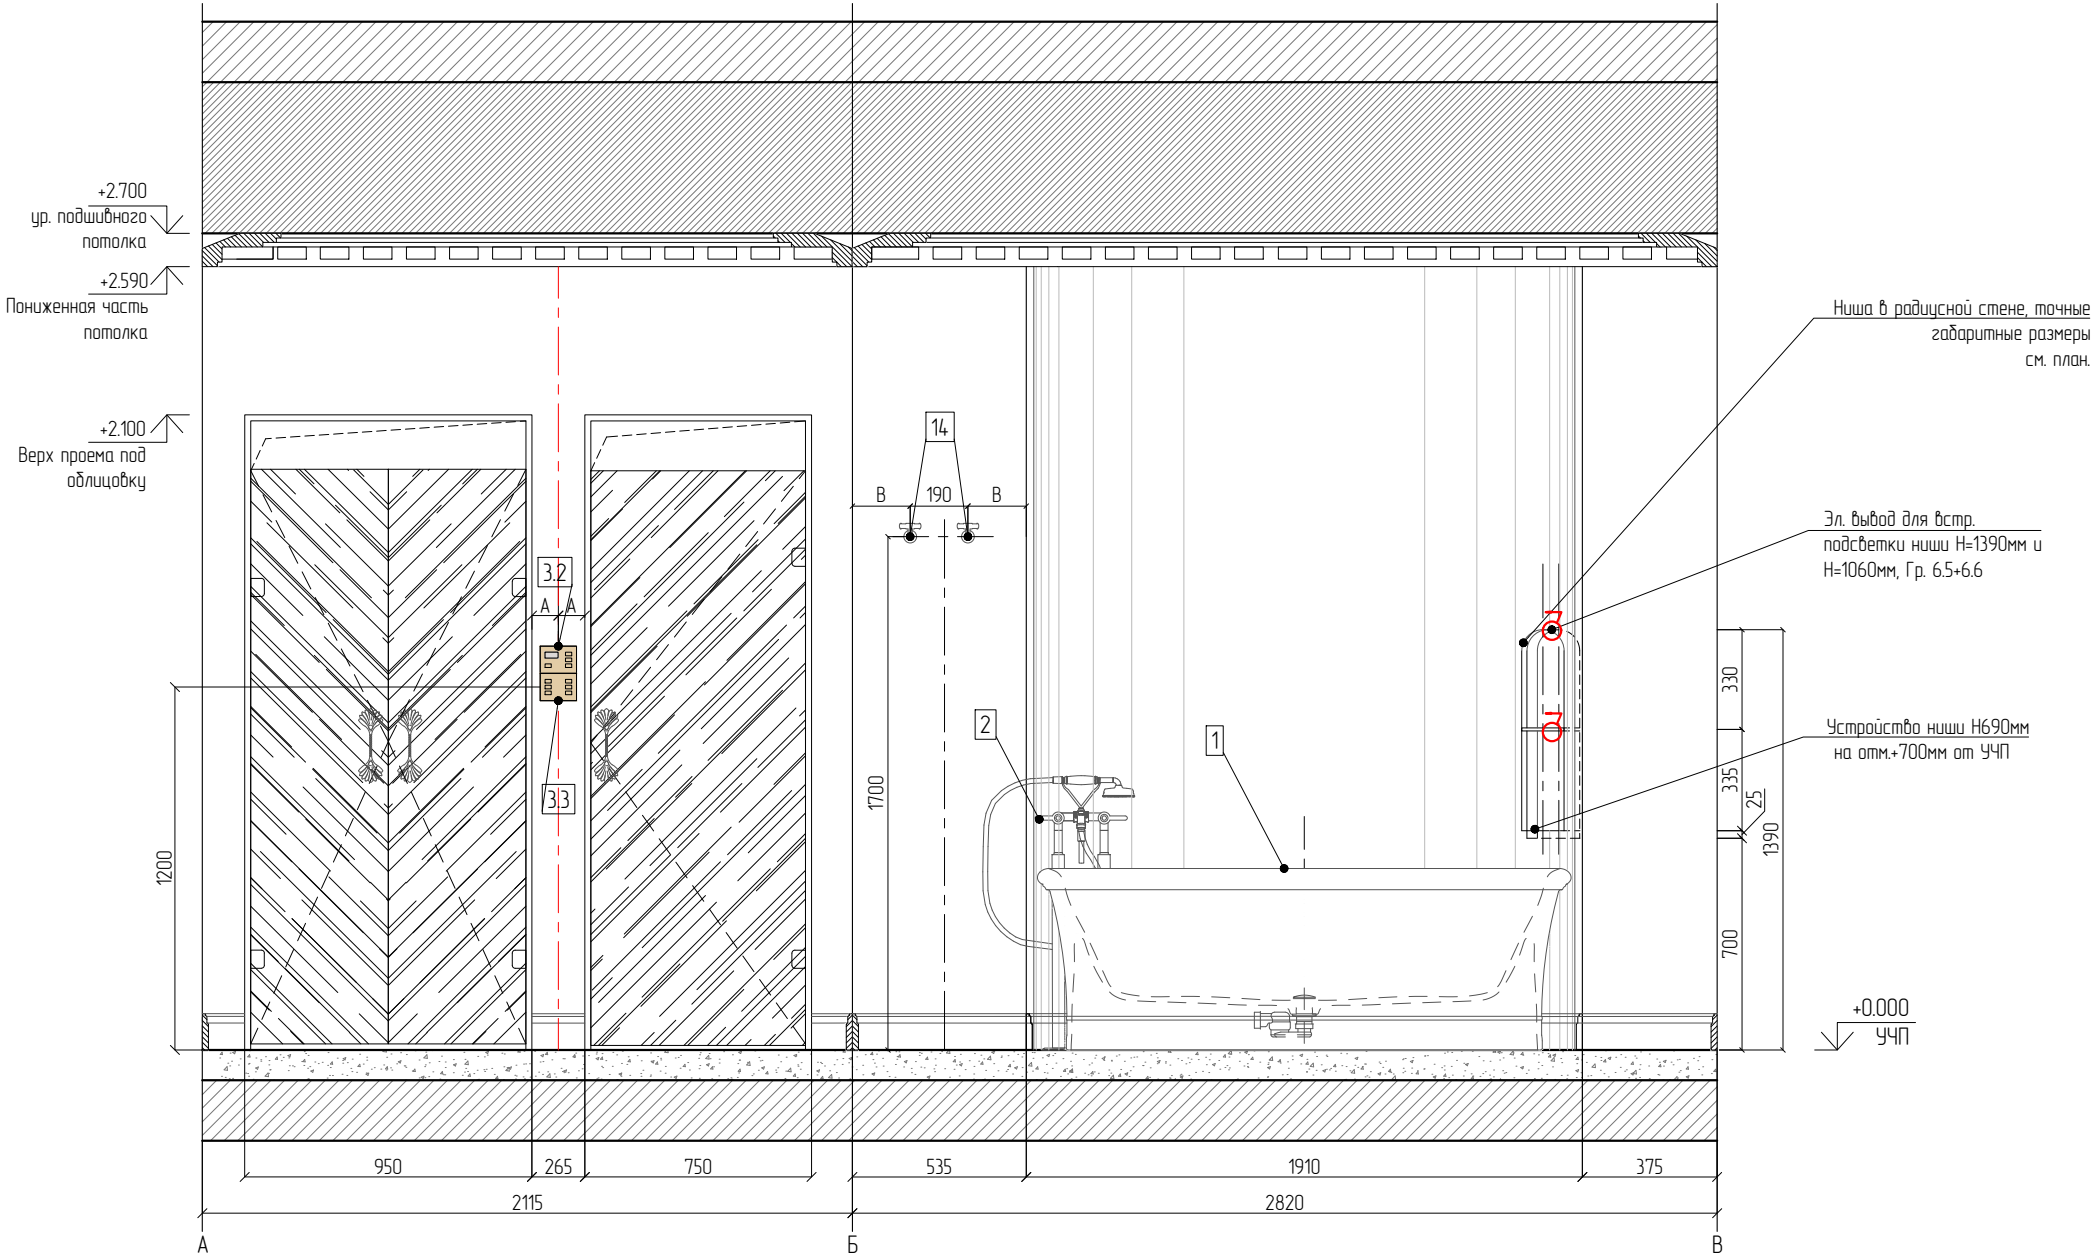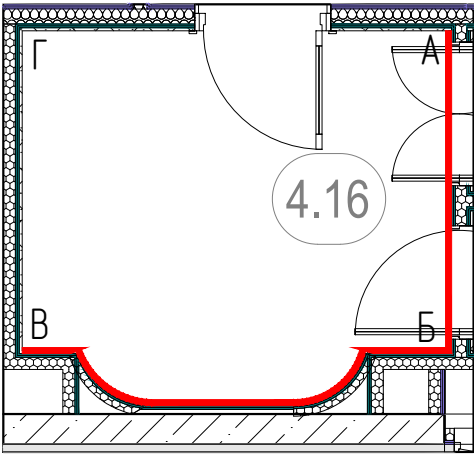

Примечания:
1. Планировочное решение выполнено на основании чертежей раздела АР, ТЗ и концепции, утвержденной Заказчиком.
2. Высоты даны от уровня чистого пола этажа. За отм. чистого пола принять верх чистового покрытия коридора.

Условные обозначения:

- Панель управления
- Терморегулятор
- Нумерация электрооборудования (Таблица с оснащением модулей для управления всем освещением см. лист: План расположения розеток.)
- Электрический вывод


Спецификация сантехнического оборудования номера Deluxe			
Марка	Описание	Отделка	Кол-во
-1-	- Dugavit Care Cad 7004590000000000 Ванна отдельная 1650x780x630 мм белый, (1680x785 мм размер по проекту), арт: 7004590000000000	White ceramic	1
-2-	- Смеситель напольный GESSI BATH TUB MIXER Bath tub Mixer 031 chrome+внутренняя часть, арт. 65128+65099	031 chrome	1
-14-	- Крючок одинарный настенный GESSI ROBE HOOK Art. 65521	031 chrome	2
-15-	- Полотенцесушитель электрический SBORDONI TOWEL HEATER sbpar4/2	chrome	1
-17-	- Мусорное ведро DEVON-DEVON PEDAL BIN Waltz	Chrome	1
-24-	- Основа для плитки 100 мм. из нержавеющей стали + сифон + комплектующие (высота стяжки 100 мм). арт. 36014 00+3660016. Произ-ль TECE.		
Примечание: см. Спецификацию отделочных материалов и оборудования			

Изм.	Кол.уч.	Лист	№ док.	Подпись	Дата
Разработал	Казыева А.Р.				02.02.26
Проверил	Новикова Е.				02.02.26
Н.контр.	Бахвалова Л.В.				02.02.26
ГАП	Сафронова Е.				02.02.26


Заказчик: ООО «Приморская»		Прим-0001/2024-АИ.01-410	
Технический заказчик: АО «СЗ «ЛСР. Недвижимость – М»			
Развитие гостиницы «Приморская» в г. Сочи. Приспособление и сохранение объекта культурного наследия «Здание, где в годы Великой Отечественной войны размещались госпитали № 2095, 2120, 1941-1945 годы», расположенного по адресу: г. Сочи, Центральный район, ул. Саколова, д. 1.			
Интерьерные решения. Гостиница "Приморская", корпус 1, 4 этаж, N 410. Тип "Делюкс"		Стадия	Лист
		РД	25
Схема привязки сантехники. Развертка стен А-В. Лист 1. М 1:25		Листов	40
		ООО "Арх-И-Арм"	

Схема привязки сантехники. Развертка стен В-А. Лист 2. Помещение № 3 (ванная комната).
Корпус 1, 4 этаж, N 410. Тип "Делюкс"

+2.700
ур. подшивного
потолок
+2.590
Пониженная часть
потолок

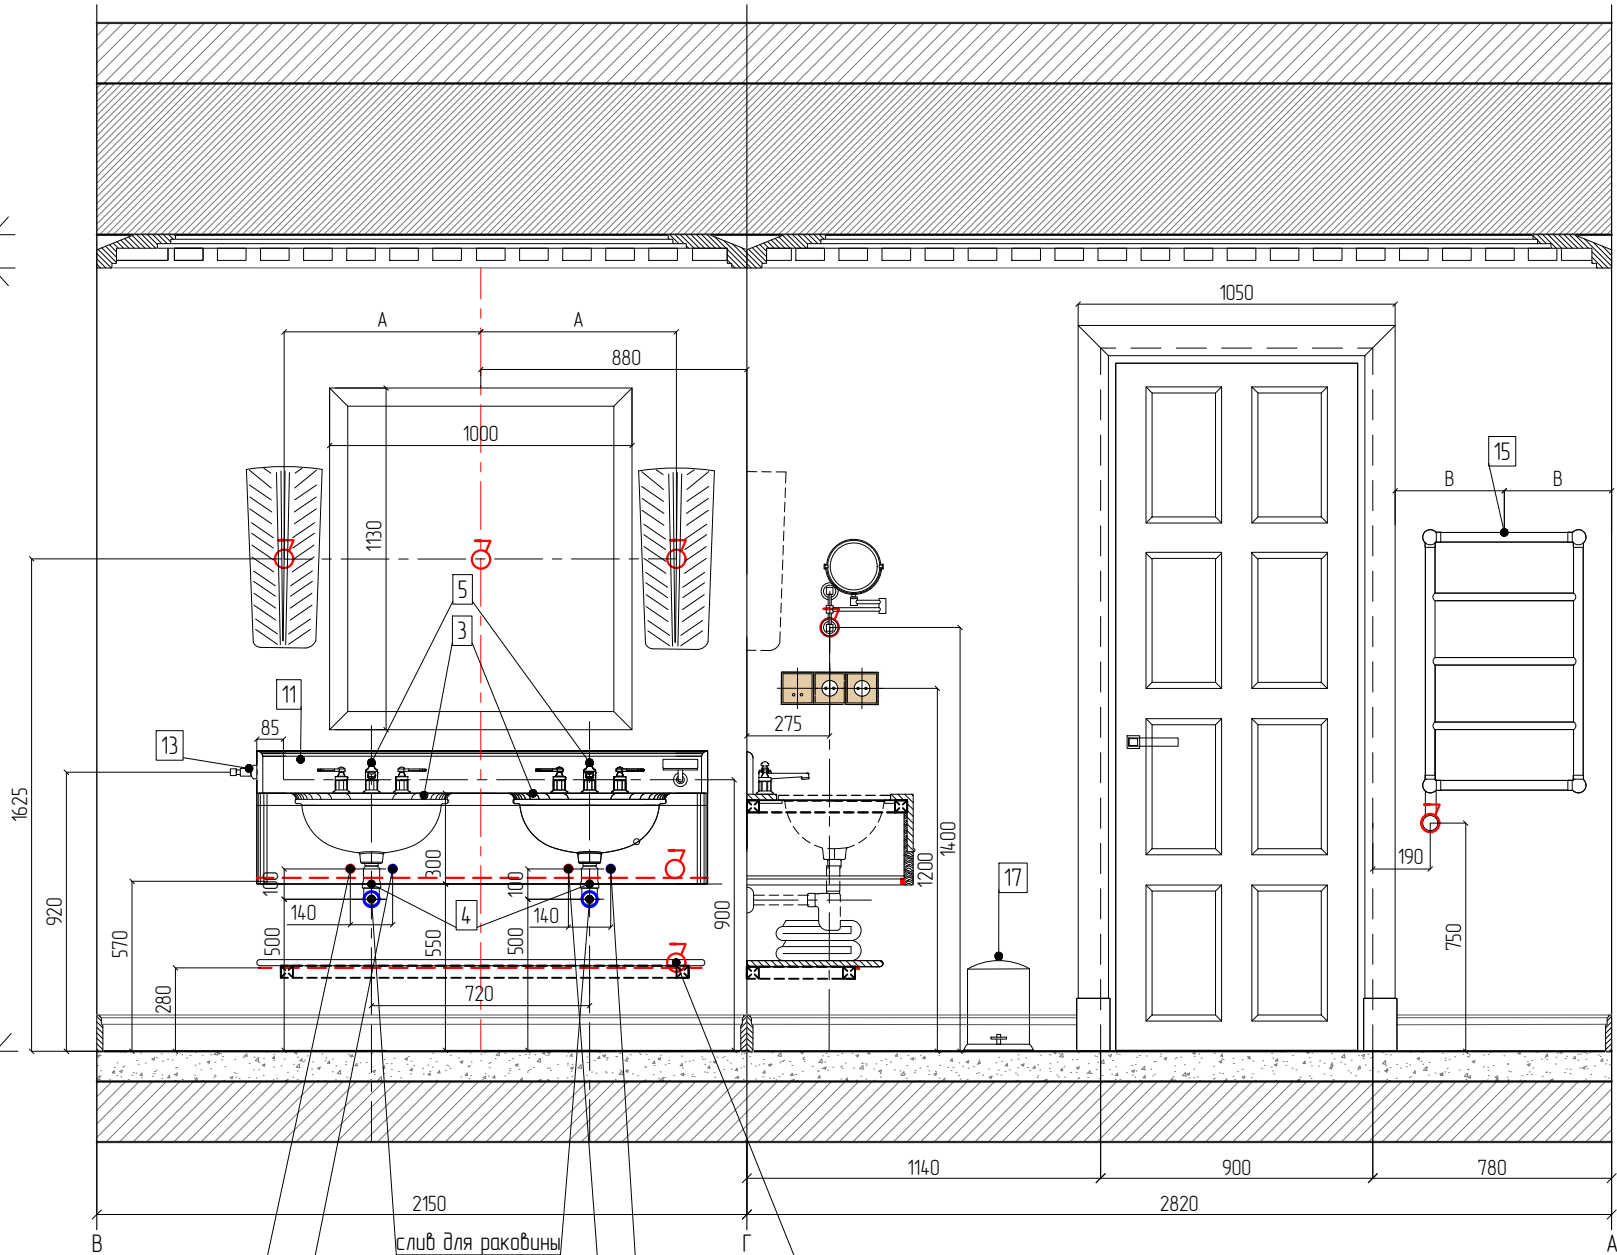

План с маркировкой разверток. М 1:50

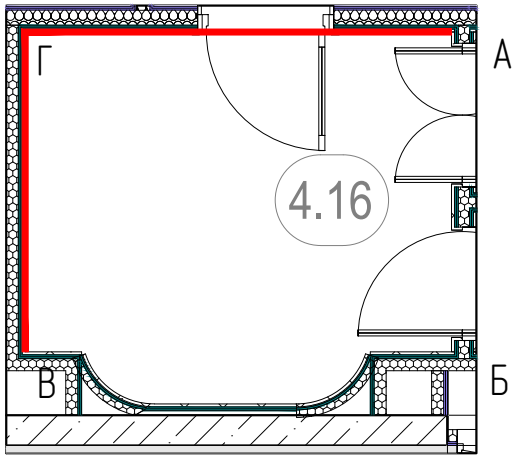

з.в. для раковины
х.в. для раковины
слив для раковины
х.в. для раковины
Предусмотреть закладные для консольной
навески раковины встр. в мраморную столешницу
1500x550мм на отм. +850мм от УЧП и мраморной
полки под ней 1500x450мм на отм. +300мм от УЧП

Условные обозначения:

— Розетка влагозащитная 220V

— Розетка для дротвы 230/110В

— Электрический вывод

— Слаботочный электрический вывод

— LED подсветка 3 м.п.

— Нумерация электрооборудования

— Маркировка сантехнического оборудования

— Настенный светильник (бра) 2шт,
SOGNI DI CRISTALLO wall light, стекло,
H=600мм, W=250мм, max2x40W, 2xЕ14

Примечания:

1. Планировочное решение выполнено на основании чертежей раздела АР, ТЗ и концепции, утвержденной Заказчиком.
2. Высоты даны от уровня чистого пола этажа. За отм. чистого пола принять верх чистового покрытия коридора.

Спецификация сантехнического оборудования номера Delux


Марка	Описание	Отделка	Кол-во
-1-	- Dugavit Care Cad 70045900000000 Ванна отдельная 1650x780x630 мм белый, (1680x785 мм размер по проекту), арт: 70045900000000	White ceramic	1
-2-	- Смеситель напольный GESSI BATH TUB MIXER Bath tub Mixer 031 chrome+внутренняя часть, арт. 65128+65099	031 chrome	1
-14-	- Крючок одинарный настенный GESSI ROBE HOOK Art. 65521	031 chrome	2
-15-	- Полотенцесушитель электрический SBORDONI TOWEL HEATER sbpar4/2	chrome	1
-17-	- Мусорное ведро DEVON-DEVON PEDAL BIN Waltz	Chrome	1
-24-	- Основа для плитки 100 мм. из нержавеющей стали + сифон + комплектующие (высота стяжки 100 мм). арт. 36014.00+3660016. Произ-ль TECE.		

Примечание: см. Спецификацию отделочных материалов и оборудования

Изм.	Кол.уч.	Лист	№ док.	Подпись	Дата
Разработал	Казыева А.Р.	02.02.26			
Проверил	Нобикова Е.	02.02.26			
Н.контр.	Бахвалова Л.В.	02.02.26			
ГАП	Сафронова Е.	02.02.26			

Заказчик: ООО «Приморская»		ПриМ-0001/2024-АИ.01-410		
Технический заказчик: АО «СЗ «ЛСР. Недвижимость – М»				
Развитие гостиницы «Приморская» в г. Сочи. Приспособление и сохранение объекта культурного наследия «Здание, где в годы Великой Отечественной войны размещались госпитали № 2095, 2120, 1941-1945 годы», расположенного по адресу: г. Сочи, Центральный район, ул. Саколова, д. 1.				
Интерьерные решения. Гостиница "Приморская", корпус 1, 4 этаж, N 410. Тип "Делюкс"	Стадия	Лист	Листов	
	РД	26	40	
Схема привязки сантехники. Развертка стен В-А. Лист 2. М 1:25	ООО "Арх-И-Арм"			

Развертка стен А-В. Лист 1. Помещение №3 (ванная комната).
Корпус 1, 4 этаж, N 410. Тип "Делюкс"

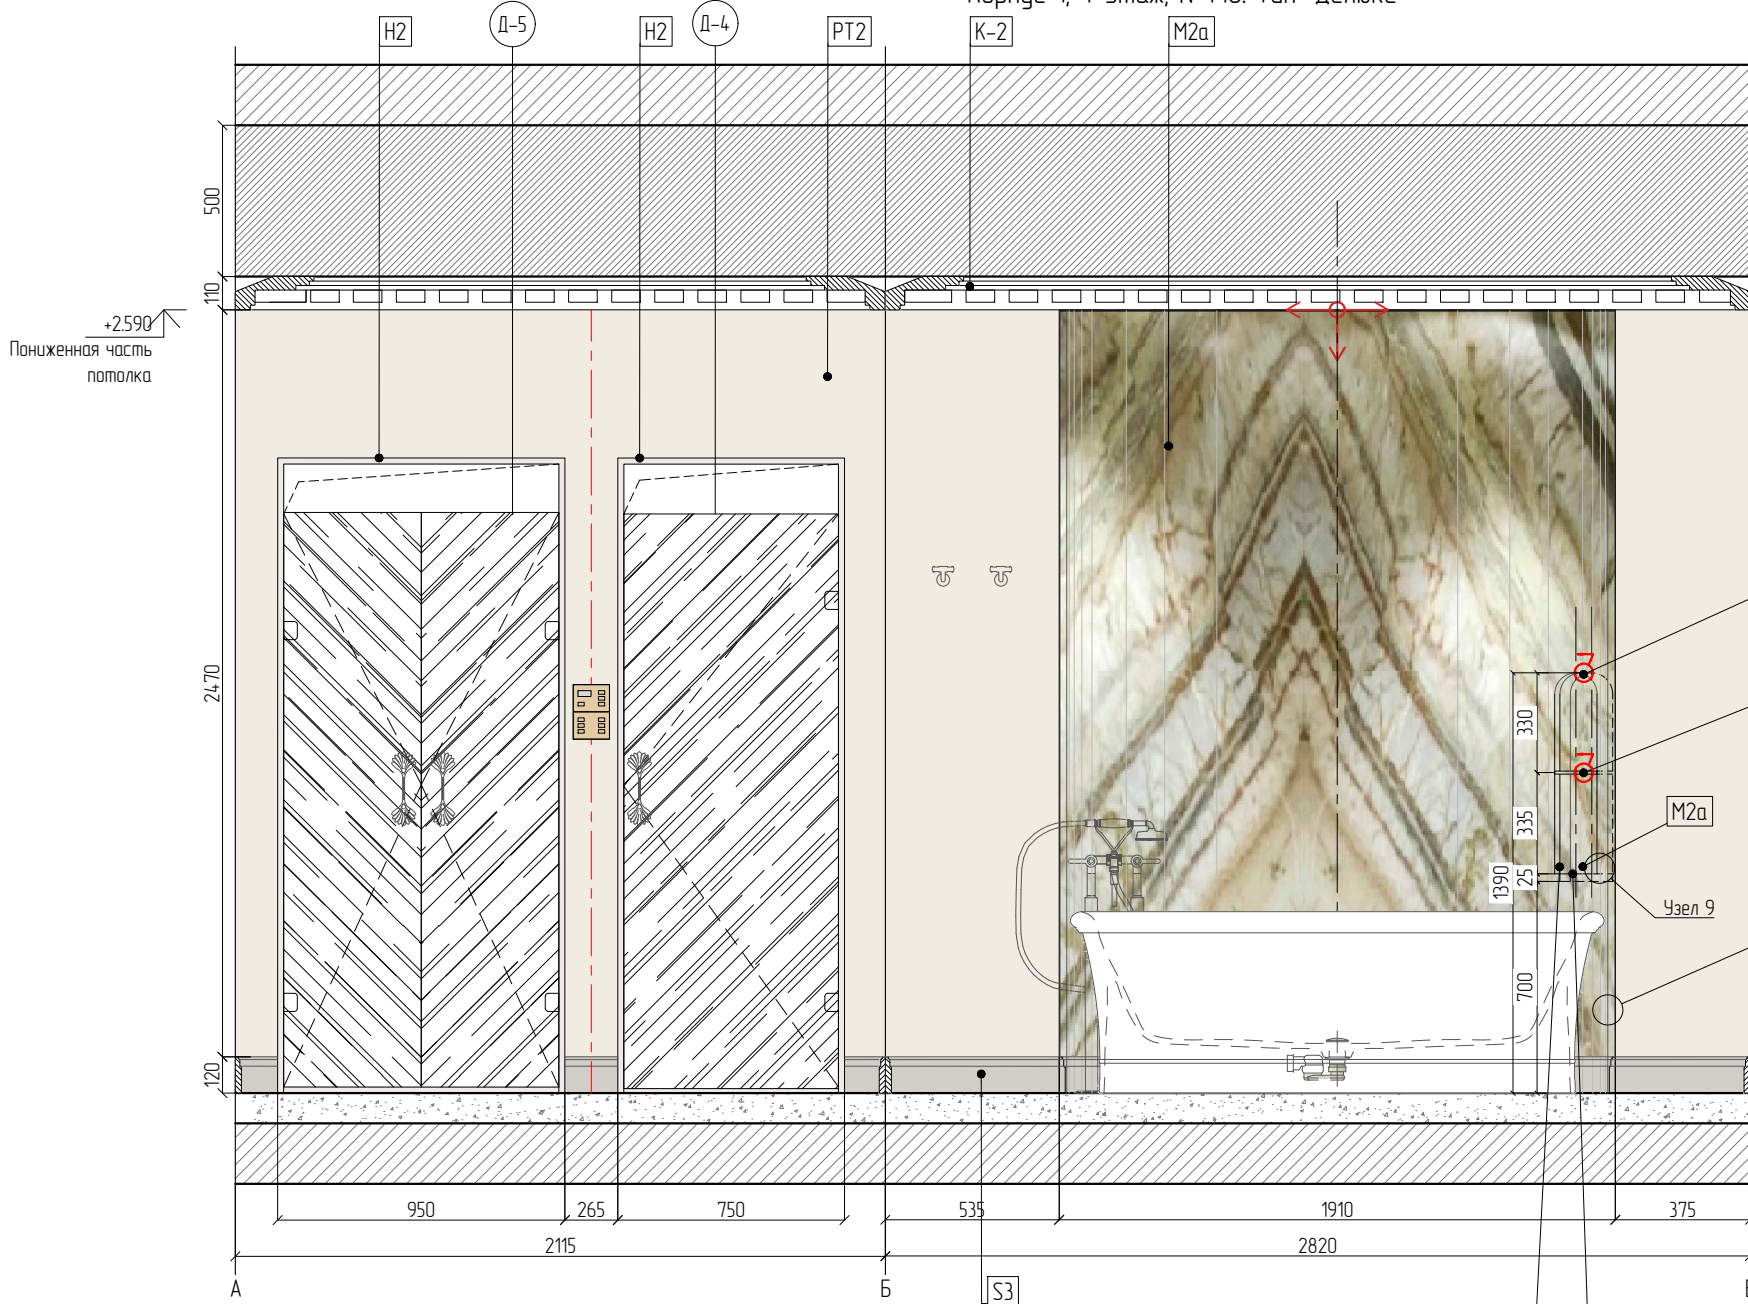

+3.200
низ перекрытия

+2.700
Пониженная часть
потолок

+2.100
Верх проема под
облицовку

Устройство ниши H690мм на отст.+700мм от
УЧП в окраске. Встроенная подсветка полок
Гр. 6,5+6,6

Предусмотреть крепление для
стеклянной полки


узел 1
лист 3

+0.000
УЧП


Устройство ниши H690мм
на отст.+700мм от УЧП

Нижняя полка в облицовке мрамором, стык
запилить под 45 градусов, снять фаску по краю

План с маркировкой разверток. М 1:50

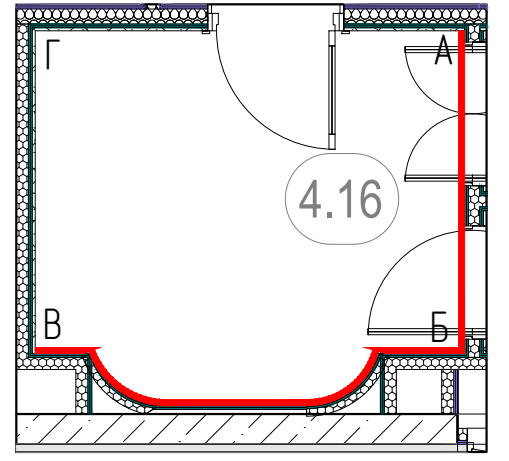

Узел 9.
Устройство полки в нише.

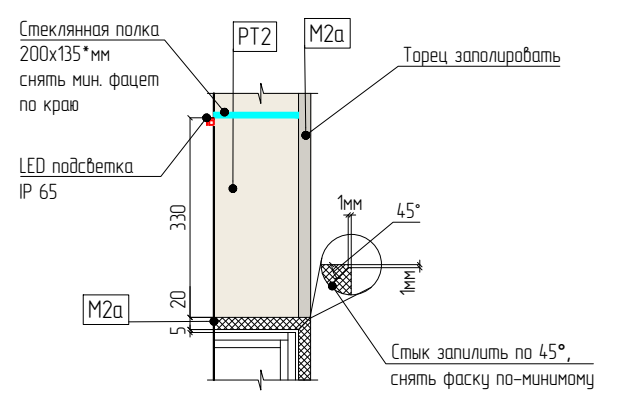

Условные обозначения:



- Панель управления



- Регулятор



- Электрический выход



- Маркировка отделочных
материалов




- Маркировка дверей




- Направление укладки




- Встроенная светодиодная лента
IP 65 с матовым рассеивателем
0,5 поз.м.

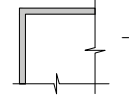

-H2- Портал в облицовке
L150 x H2100 x W20(30)мм - 4шт., L150x P950 x W20(30)мм - 2шт.
из натурального полированного мрамора -Ma3- Calacatta Borghini marble

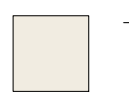


- PT2- декоративное покрытие арт.
ROMAN PLASTER ERS3 Calcite, произ-ль RESSOURCE
S_{общ. по пом.}: 14,04 + 10% = 15,4 м²

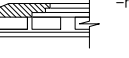

-K2- Карниз лепной 110мм x 260мм
L_{общ. по пом.}: 10+10%= 11 м.п.



-S3- Плинтус из натурального полированного мрамора
- M2a- Cortecchia marble 120мм x 20мм
L_{общ. по пом.}: 7,4+10%=8,25 м.п.

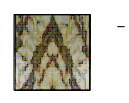



- M2a- Облицовка полукруглой стены "скорлупа"/вар: каменный шпон из
полированного мрамора Cortecchia marble. Рисунок слэба "бабочка"
S_{общ. по пом.}: 5,55 + 10% = 6,1 м²

Примечания:

1. Планировочное решение выполнено на основании чертежей раздела АР, ТЗ и концепции, утвержденной Заказчиком.
2. Расчет отделочных материалов - взят с запасом в 10%. Подсчет натурального камня скорректировать согласно раскроя Поставщика.
3. Перед заказом встроенной мебели необходимо произвести замер силами инженеров от фирм производителей. Чертежи встр. мебели см. Лист дополнительной информации к планировочному решению.
4. Цвет и вид отделочных материалов согласовать с автором проекта.
5. Весь натуральный камень выкладывать с минимальным швом, образовавшиеся зазоры обрабатывать затиркой в цвет камня.

Заказчик: ООО «Приморская»						ПриМ-0001/2024-АИ.01-410		
Технический заказчик: АО «СЗ «ЛСР. Недвижимость - М»								
Развитие гостиницы «Приморская» в г. Сочи. Приспособление и сохранение объекта культурного наследия «Здание, где в годы Великой Отечественной войны размещались госпитали № 2095, 2120, 1941-1945 годы», расположенного по адресу: г. Сочи, Центральный район, ул. Саколова, д. 1.								
Изм.	Кол.уч.	Лист	№ док.	Подпись	Дата	Интерьерные решения. Гостиница "Приморская", корпус 1, 4 этаж, N 410. Тип "Делюкс"	Стадия	Лист
Разработал	Казыева А.Р.				02.02.26		РД	27
Проверил	Нобикова Е.				02.02.26			40
						Развертка стен А-В. Лист 1. Помещение №3 (ванная комната). М 1:25	ООО "Арх-И-Арм"	
Н.контр.	Бахвалова Л.В.				02.02.26			
ГАП	Сафронова Е.				02.02.26			

Развертка стен В-А. Лист 2. Помещение №3 (ванная комната).
Корпус 1, 4 этаж, N 410. Тип "Делюкс"

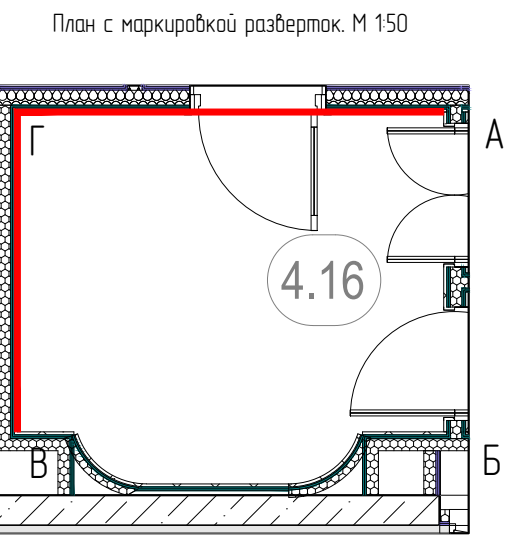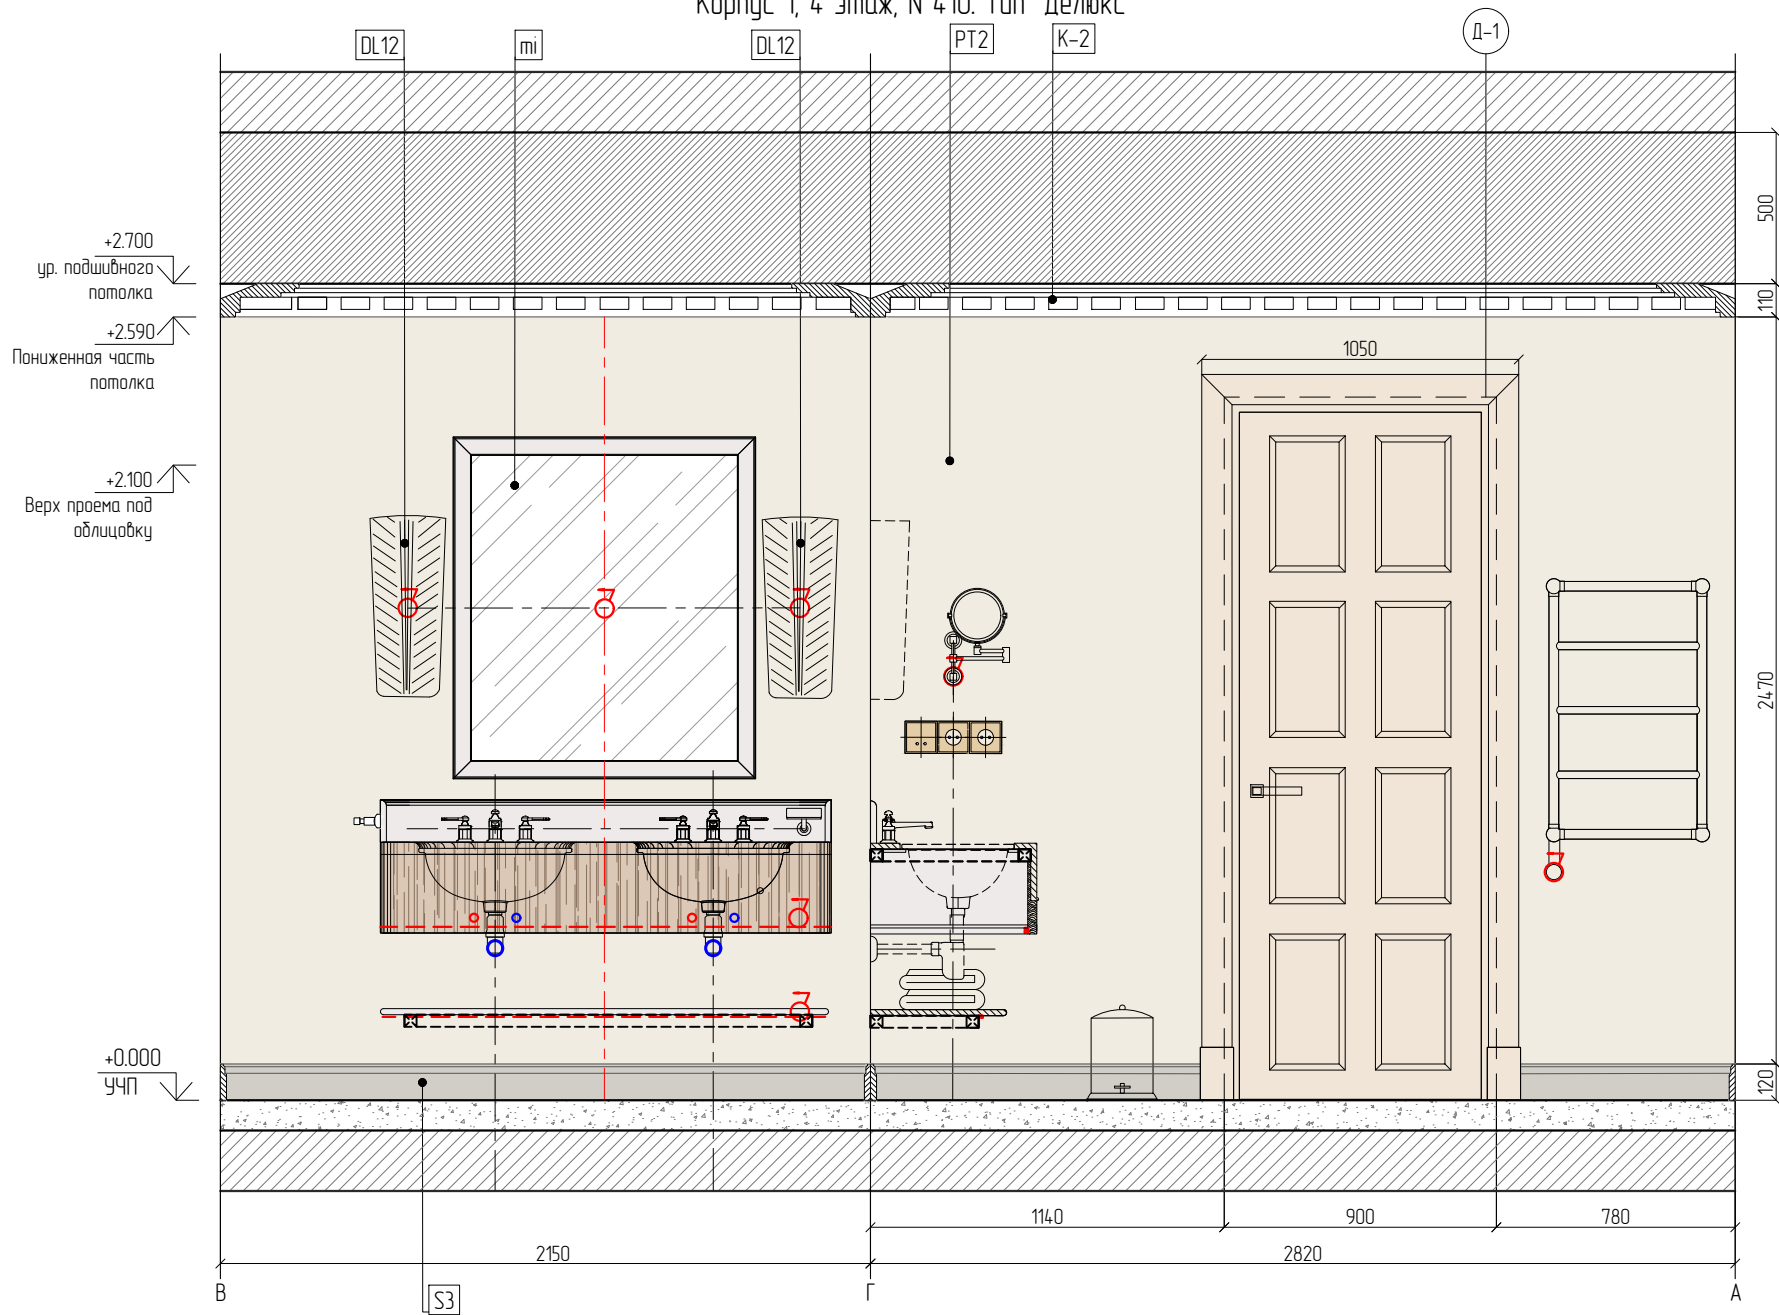

Д-6
Обрамление портала L(70+120) x H2150 x W20мм – 2шт.
L(70+120) x P1100 x W20мм – 1шт.
Цоколь L(75+125) x H175 x W25 мм – 2шт.
из полированного мрамора –M1a- Breccia Capraia marble

Согласовано	
Взам. инв. №	
Подп. и дата	
Инв. № подл.	


Условные обозначения:

- Розетка влагозащищенная 220V
- Розетка для дротвы 230/110В
- Электрический вывод
- LED подсветка 3 м.п.
- Маркировка отделочных материалов
- Маркировка дверей
- Маркировка осветительного оборудования
- Настенный светильник (бра) 2шт, SOGNI DI CRISTALLO wall light, стекло, H=600мм, W=250мм, max2x40W, 2xЕ14
- Зеркало 1080мм x 1130(Н)мм, S=1,05м2 в обрамлении из натурального камня: толщина 10мм, ширина 60мм –M1a – мрамор Breccia Capraia marble, полированный P=4 пог.м.
- Слаботочный электрический вывод
- PT2– декоративное покрытие арт. ROMAN PLASTER ER53 Calcite, произ-ль RESSOURCE S_{общ. по пок.}: 14,04 + 10% = 15,4 м2
- K2– Карниз лепной 110мм x 260мм L_{общ. по пок.}: 10+10%= 11 м.п.
- S3– Плинтус из натурального полированного мрамора – M2a– Carreccia marble 120мм x 20мм L_{общ. по пок.}: 7,4+10%=8,25 м.п.


- Примечания:
1. Планировочное решение выполнено на основании чертежей раздела АР, ТЗ и концепции, утвержденной Заказчиком.
 2. Расчет отделочных материалов – взят с запасом в 10%. Подсчет натурального камня скорректировать согласно раскрасу Поставщика.
 3. Перед заказом встроенной мебели необходимо произвести замер силами инженеров от фирм производителей. Чертежи встр. мебели см. Лист дополнительной информации к планировочному решению.
 4. Цвет и вид отделочных материалов согласовать с автором проекта.
 5. Весь натуральный камень выкладывать с минимальным швом, образовавшиеся зазоры обрабатывать затиркой в цвет камня.

						Заказчик: ООО «Приморская» Технический заказчик: АО «СЗ «ЛСР. Недвижимость – М»			ПриМ-0001/2024-АИ.01-410			
						Развитие гостиницы «Приморская» в г. Сочи. Приспособление и сохранение объекта культурного наследия «Здание, где в годы Великой Отечественной войны размещались госпитали № 2095, 2120, 1941-1945 годы», расположенного по адресу: г. Сочи, Центральный район, ул. Саколова, д. 1.						
Изм.	Кол.уч.	Лист	№ док.	Подпись	Дата	Интерьерные решения. Гостиница "Приморская", корпус 1, 4 этаж, N 410. Тип "Делюкс"			Стадия	Лист	Листов	
Разработал		Казыева А.Р.			02.02.26				РД	28	40	
Проверил		Новикова Е.			02.02.26							
						Развертка стен В-А. Лист 2. Помещение №3 (ванная комната). М 1:25			ООО "Арх-И-Арм"			
Н.контр.		Бахвалова Л.В.			02.02.26							
ГАП		Сафронова Е.			02.02.26							

План с привязкой сантехники и маркировкой оборудования. Помещение №4 (санузел).
Корпус 1, 4 этаж, N 410. Тип "Делюкс"

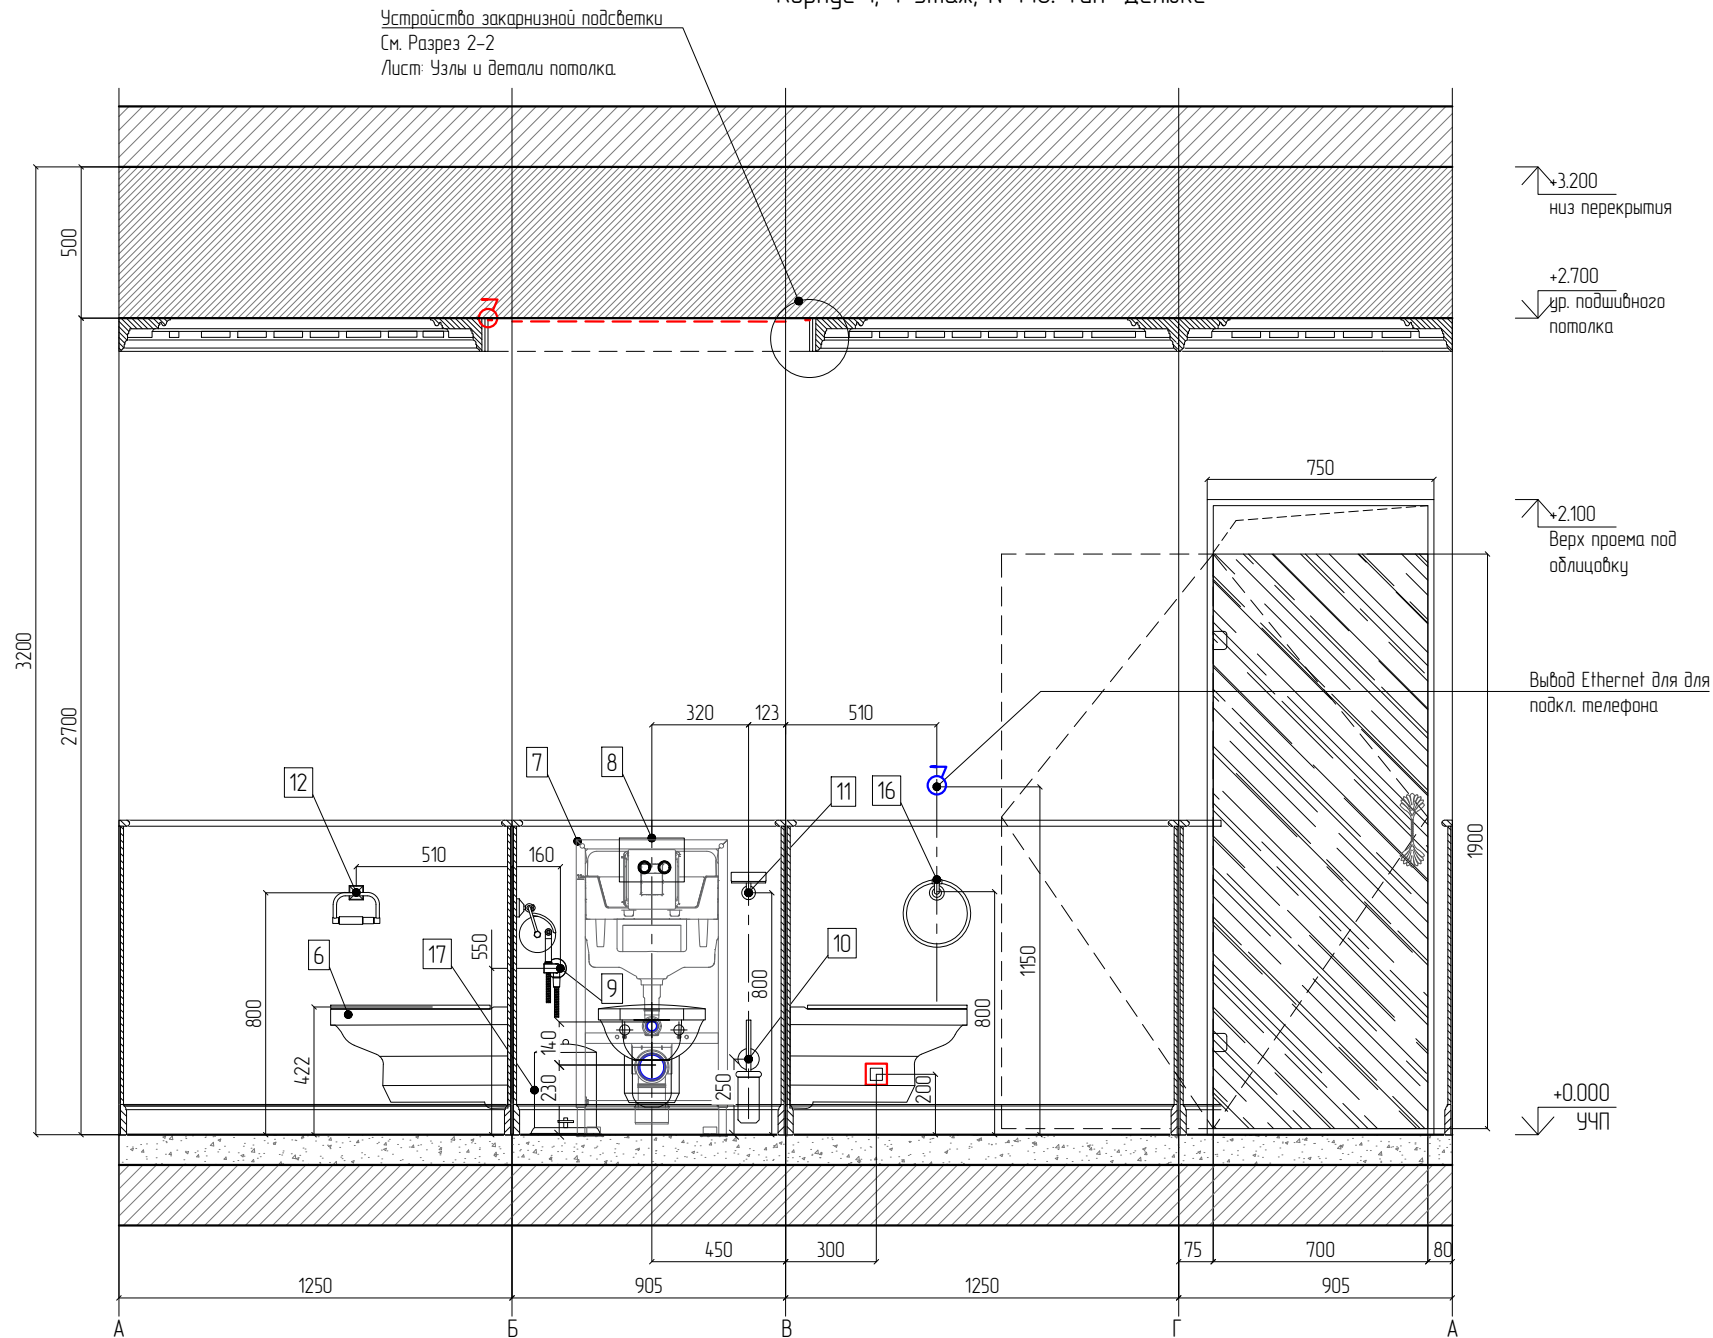

План с привязкой сантехники и маркировкой оборудования.

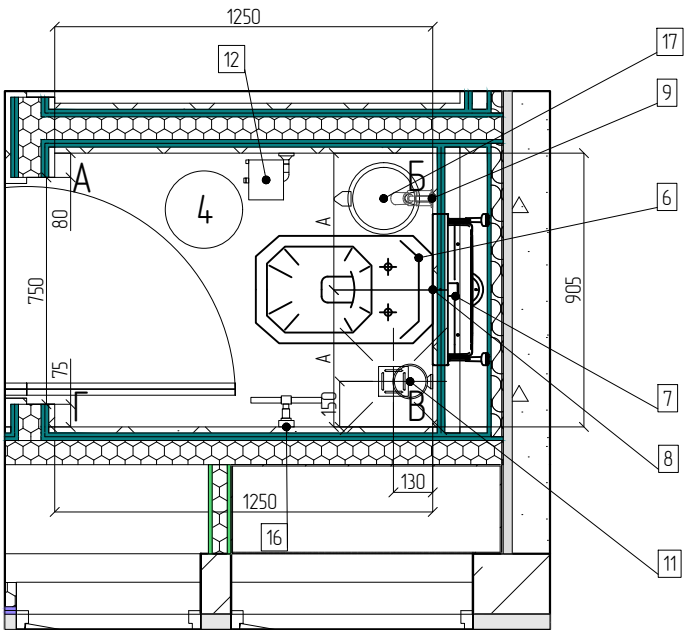

Условные обозначения:

- 1 - Номер помещения
1 - Маркировка сантехнического оборудования
Э - Электрический выход
Э - Слаботочный электрический выход
--- - LED подсветка 1 м.л.
□ - встроены светильники для ночной подсветки, IP 65

Спецификация сантехнического оборудования номера Deluxe			
Марка	Описание	Отделка	Кол-во
-6-	Унитаз подвесной длина 58 см. White ceramic+сиденье белый пластик (64890000). DURAVIT	White ceramic	1
-7-	Инсталляция Geberit Omega 12 для подвешенного унитаза, высота 980мм, глубина встра. 140мм		1
-8-	Клавиша двойного смыва 115.085.KH1, GEBERIT	031 chrome	1
-9-	Гигиенический душ Bossini Paloma. E37005B00030015, хром	031 chrome	1
-10-	Подвесной ершик GESSI TOILET BRUSH art. 65419.	031 chrome	1
-11-	Мыльница GESSI SOAP HOLDER art. 65401.	031 chrome	1
-12-	Бумагодержатель GESSI PAPER TOILET ROLL HOLDER art. 65449.	031 chrome	1
-16-	Полотенцедержатель GESSI VENTI20 65509 PORTA SALVIETTA ANELLO.	031 chrome	1
-17-	Мусорное ведро DEVON&DEVON PEDAL BIN Waltz	Chrome	1
-24-	Основа для плитки 100 мм. из нержавеющей стали + сифон + комплектующие (высота стяжки 100 мм). арт. 36014. 00+3660016. Произ-ль TESCO.	Chrome	1

Примечание: см. Спецификацию отделочных материалов и оборудования

Примечания:

1. Планировочное решение выполнено на основании чертежей раздела АР, ТЗ и концепции, утвержденной Заказчиком.
2. Высоты даны от уровня чистого пола этажа. За отм. чистого пола принять верх чистового покрытия коридора.

						Заказчик: ООО «Приморская» Технический заказчик: АО «СЗ «ЛСР. Недвижимость – М»							ПриМ-0001/2024-АИ.01-410					
						Развитие гостиницы «Приморская» в г. Сочи. Приспособление и сохранение объекта культурного наследия «Здание, где в годы Великой Отечественной войны размещались госпитали № 2095, 2120, 1941-1945 годы», расположенного по адресу: г. Сочи, Центральный район, ул. Соколова, д. 1.												
Изм.	Кол.уч.	Лист	№ док.	Подпись	Дата	Интерьерные решения. Гостиница "Приморская", корпус 1, 4 этаж, N 410. Тип "Делюкс"							Стадия	Лист	Листов			
Разработал		Казыева А.Р.			02.02.26								РД	29	40			
Проверил		Новикова Е.			02.02.26													
						Помещение N4 (санузел). Схема и план с привязкой сантехники. Развертка стен А-А. М 1:25							ООО "Арх-И-Арм"					
Н.контр.		Бахвалова Л.В.			02.02.26													
ГАП		Сафронова Е.			02.02.26													

Согласовано					
Взам. инв. №					
Подп. и дата					
Инв. № подл.					

Условные обозначения:

- Электрический вывод
Слаботочный электрический вывод
LED подсветка 1,05 м.п.
Маркировка отделочных материалов
Встроенный светильник 1шт. для ночной подсветки, IP 65
Направление укладки

WP3

M2a

K4

-WP3 - Обои моющиеся, артикул TBD
S= 6,1 + 10% = 6,71 м²

-M2a - Облицовка стен камнем- Corteccia marble, полированный, толщина 10мм, H-920 мм
S=3,45 + 10% = 3,79 м²

-K4- Карниз лепной 110мм x 170мм
L= 4,2+10%=4,65 м.п.

H2

S4

f2

-H2- Портал в облицовке H2100 (верх облицовки)xL150мм, полированный мрамор -M3a- Calacata Borghini marble.


-S4- Плинтус каменный из полированного мрамора Calacata Borghini -M3a- 100мм x 20мм
L = 3,6+10%=3,96 м.п.

-f2- Молдинг каменный Corteccia marble, полированный, -M2a- 20мм x 25мм
L= 3,6+10%=3,96 м.п.

Спецификация напольных покрытий номера Deluxe:

Тип	Изображение типоразмера	Описание	Вид	Кол-во
- M2 -		- натуральный камень Corteccia marble, матовый, толщина 20мм		0,37 + 10% = 0,4 м²
- M3 -		- натуральный камень Calacata Borghini marble, матовый, толщина 20мм		0,80 + 10% = 0,88 м²

Развертка стен А-А. Помещение №4 (санузел).
Корпус 1, 4 этаж, N 410. Тип "Делюкс"

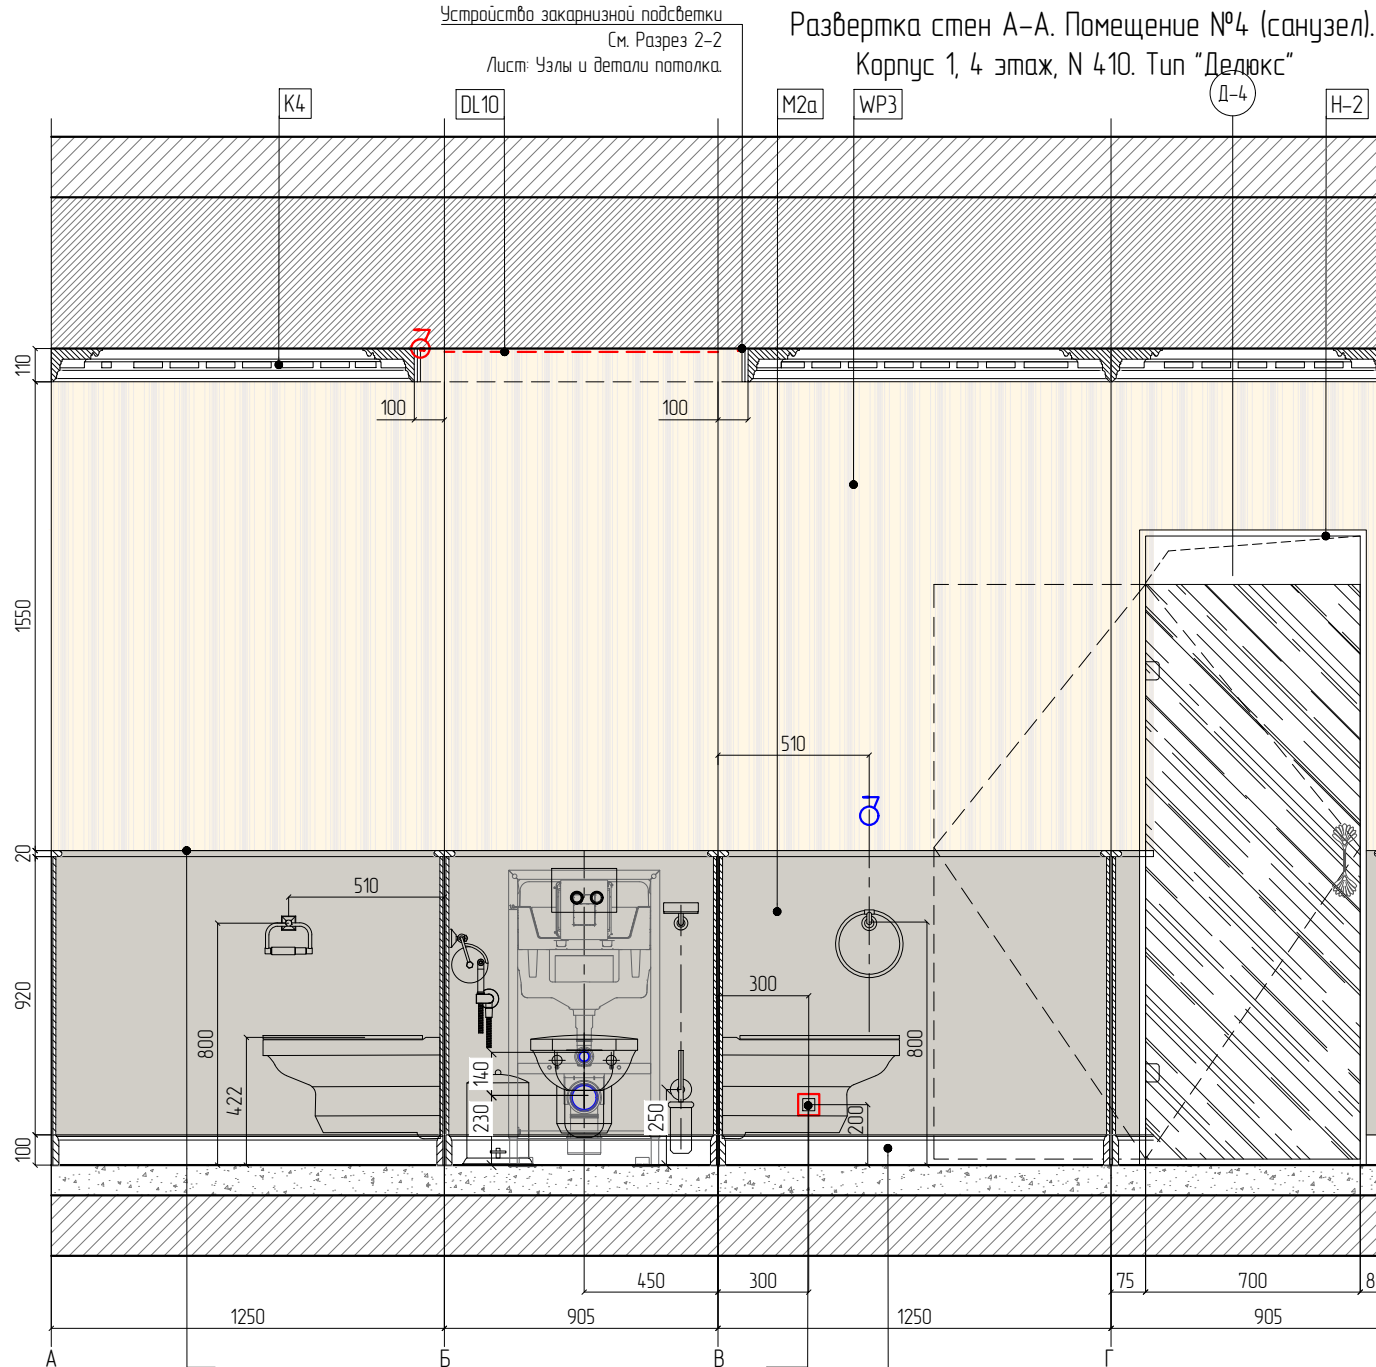


+3.200
низ перекрытия

+2.700
ур. подшивного потолка


+2.100
Верх проема под облицовку

+0.000
учп

Маркировочный план. М 1:25

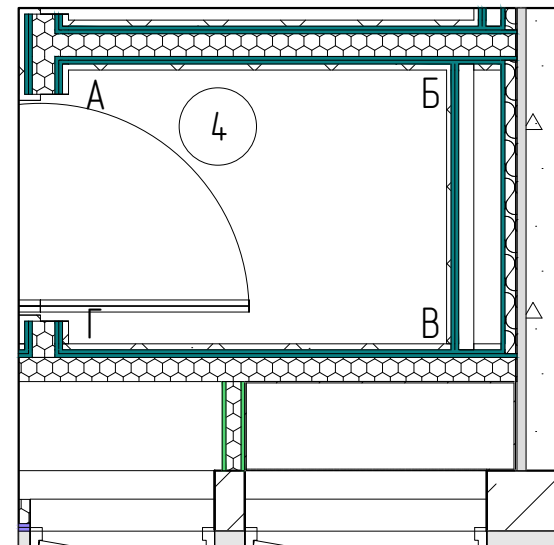

План раскладки напольных покрытий. М 1:25

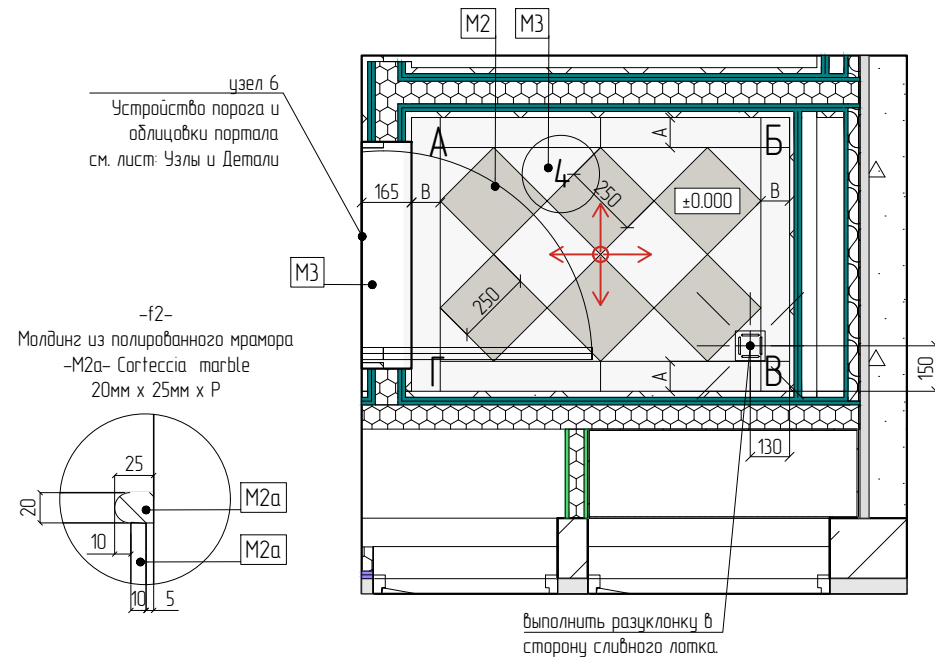


выполнить раскладку в сторону сливного лотка.


Изм.	Кол.уч.	Лист	№ док.	Подпись	Дата	Заказчик: ООО «Приморская» Технический заказчик: АО «СЗ «ЛСР. Недвижимость – М»	ПриМ-0001/2024-АИ.01-410
Разработал	Казыева А.Р.	02.02.26	Проверил	Нобикова Е.	02.02.26	Развитие гостиницы «Приморская» в г. Сочи. Приспособление и сохранение объекта культурного наследия «Здание, где в годы Великой Отечественной войны размещались госпитали № 2095, 2120, 1941-1945 годы», расположенного по адресу: г. Сочи, Центральный район, ул. Саколова, д. 1.	
Н.контр.	Бахвалова Л.В.	02.02.26	Г.АП	Сафронова Е.	02.02.26	Интерьерные решения. Гостиница "Приморская", корпус 1, 4 этаж, N 410. Тип "Делюкс"	Стадия РД
						Помещение N4 (санузел). Маркировочный план. План с раскладкой напольных покрытий. Развертка стен А-А. М 1:25	Лист 30
							Листов 40
						ООО "Арх-И-Арм"	

Согласовано				
Взам. инв. №				
Подп. и дата				
Инв. № подл.				

План с привязкой сантехники и маркировкой оборудования. Помещение №5 (душевая).
Корпус 1, 4 этаж, N 410. Тип "Делюкс"

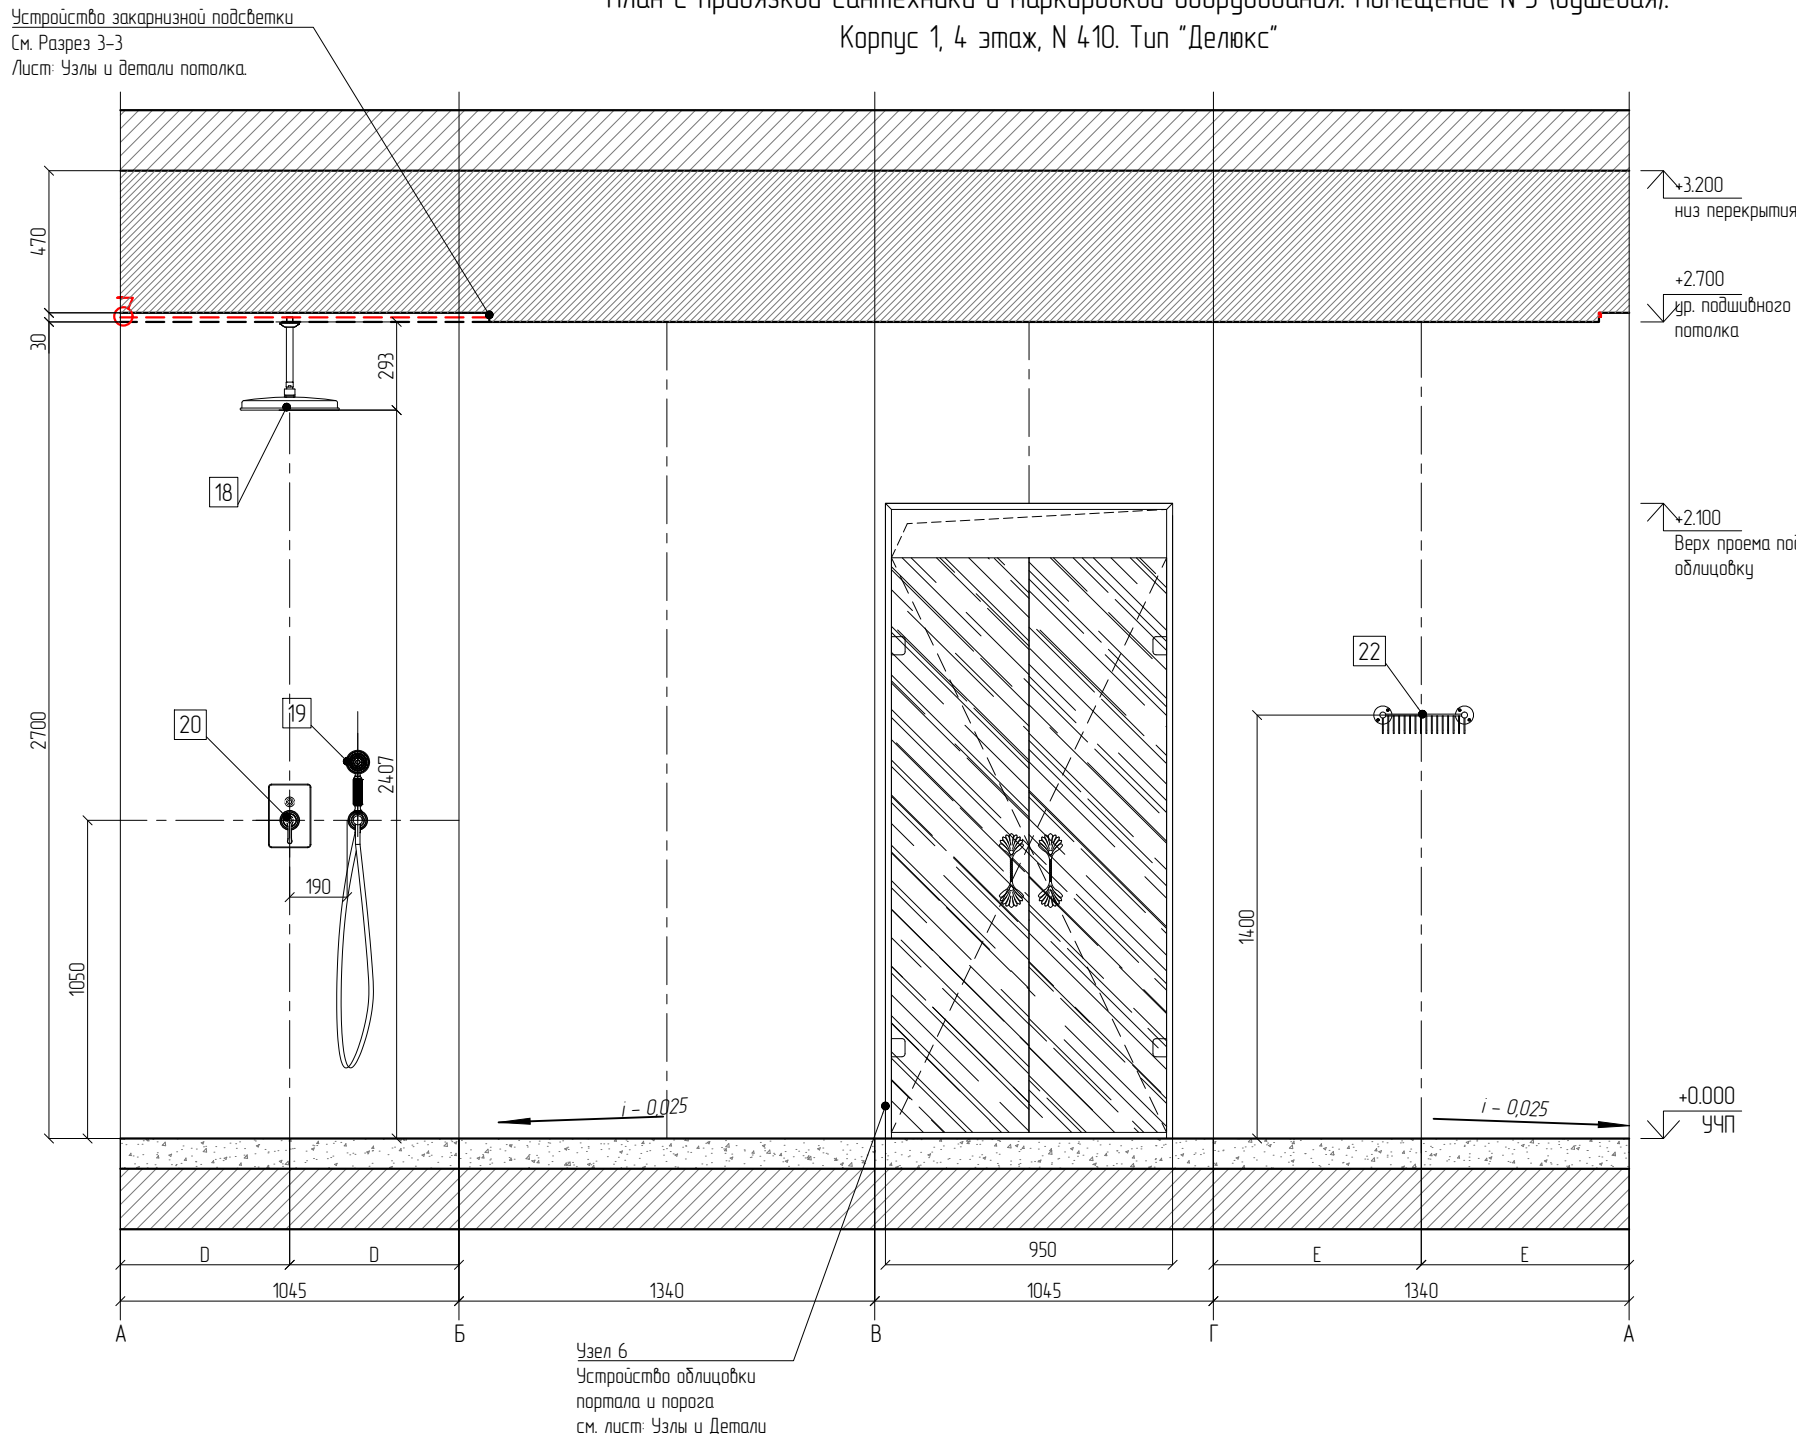

План с привязкой сантехники и маркировкой оборудования.

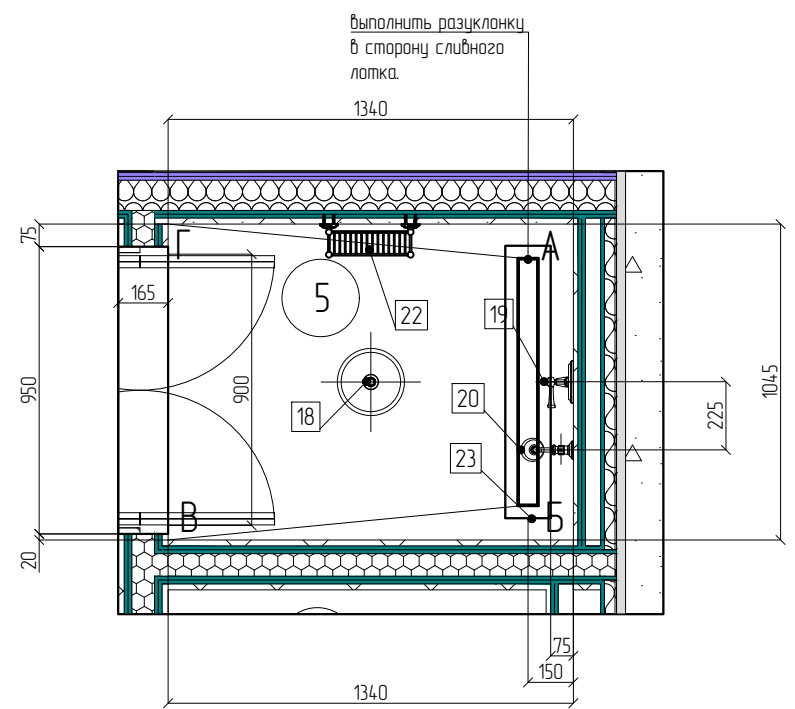


Заказчик: ООО «Приморская»						ПриМ-0001/2024-АИ.01-410		
Технический заказчик: АО «СЗ «ЛСР. Недвижимость – М»								
Развитие гостиницы «Приморская» в г. Сочи. Приспособление и сохранение объекта культурного наследия «Здание, где в годы Великой Отечественной войны размещались госпитали № 2095, 2120, 1941-1945 годы», расположенного по адресу: г. Сочи, Центральный район, ул. Саколова, д. 1.								
Изм.	Кол.уч.	Лист	№ док.	Подпись	Дата	Интерьерные решения. Гостиница "Приморская", корпус 1, 4 этаж, N 410. Тип "Делюкс"	Стадия	Лист
Разработал	Казыева А.Р.			<i>Казыева А.Р.</i>	02.02.26		РД	31
Проверил	Нобикова Е.			<i>Нобикова Е.</i>	02.02.26			40
						Помещение N5 (душевая). Схема и план с привязкой сантехники. Развертка стен А-А. М 1:25	ООО "Арх-И-Арм"	
Н.контр.	Бахвалова Л.В.			<i>Бахвалова Л.В.</i>	02.02.26			
ГАП	Сафронова Е.			<i>Сафронова Е.</i>	02.02.26		Формат А3	

Условные обозначения:

- 1 - Номер помещения
- 1 - Маркировка сантехнического оборудования
- Устройство трапа арт. TECEdrainline 650900
- Электрический вывод
- LED подсветка 1,05 м.п.

Спецификация сантехнического оборудования номера Deluxe			
Марка	Описание	Отделка	Кол-во
-18-	Душевая лейка GESSI SHOWER HEAD art. 65153	031 chrome	1
-19-	Душевой комплект, состоящий из вывода воды, держателя, шланга 1,50 м и лейки GESSI SHOWER SET art. 65123	031 chrome	1
-20-	Термостат GESSI SHOWER MIXER 65079#031 + внутренняя часть 44673	031 chrome	1
-22-	Полочка для душа LEFROY BROOKS SHELF SHOWER RT 4510	Chrome	1
-23-	Канал для укладки натурального камня 900 мм нержавеющая сталь+ сифон+комплектующие (высота стяжки 100 мм) , L-900/800 мм, произ-ль TECE. арт. TECEdrainline 650800/650900	Chrome	1
Примечание: см. Спецификацию отделочных материалов и оборудования			

Маркировочный план. Помещение №6 (спальная комната).
Корпус 1, 4 этаж, N 410. Тип "Делюкс"

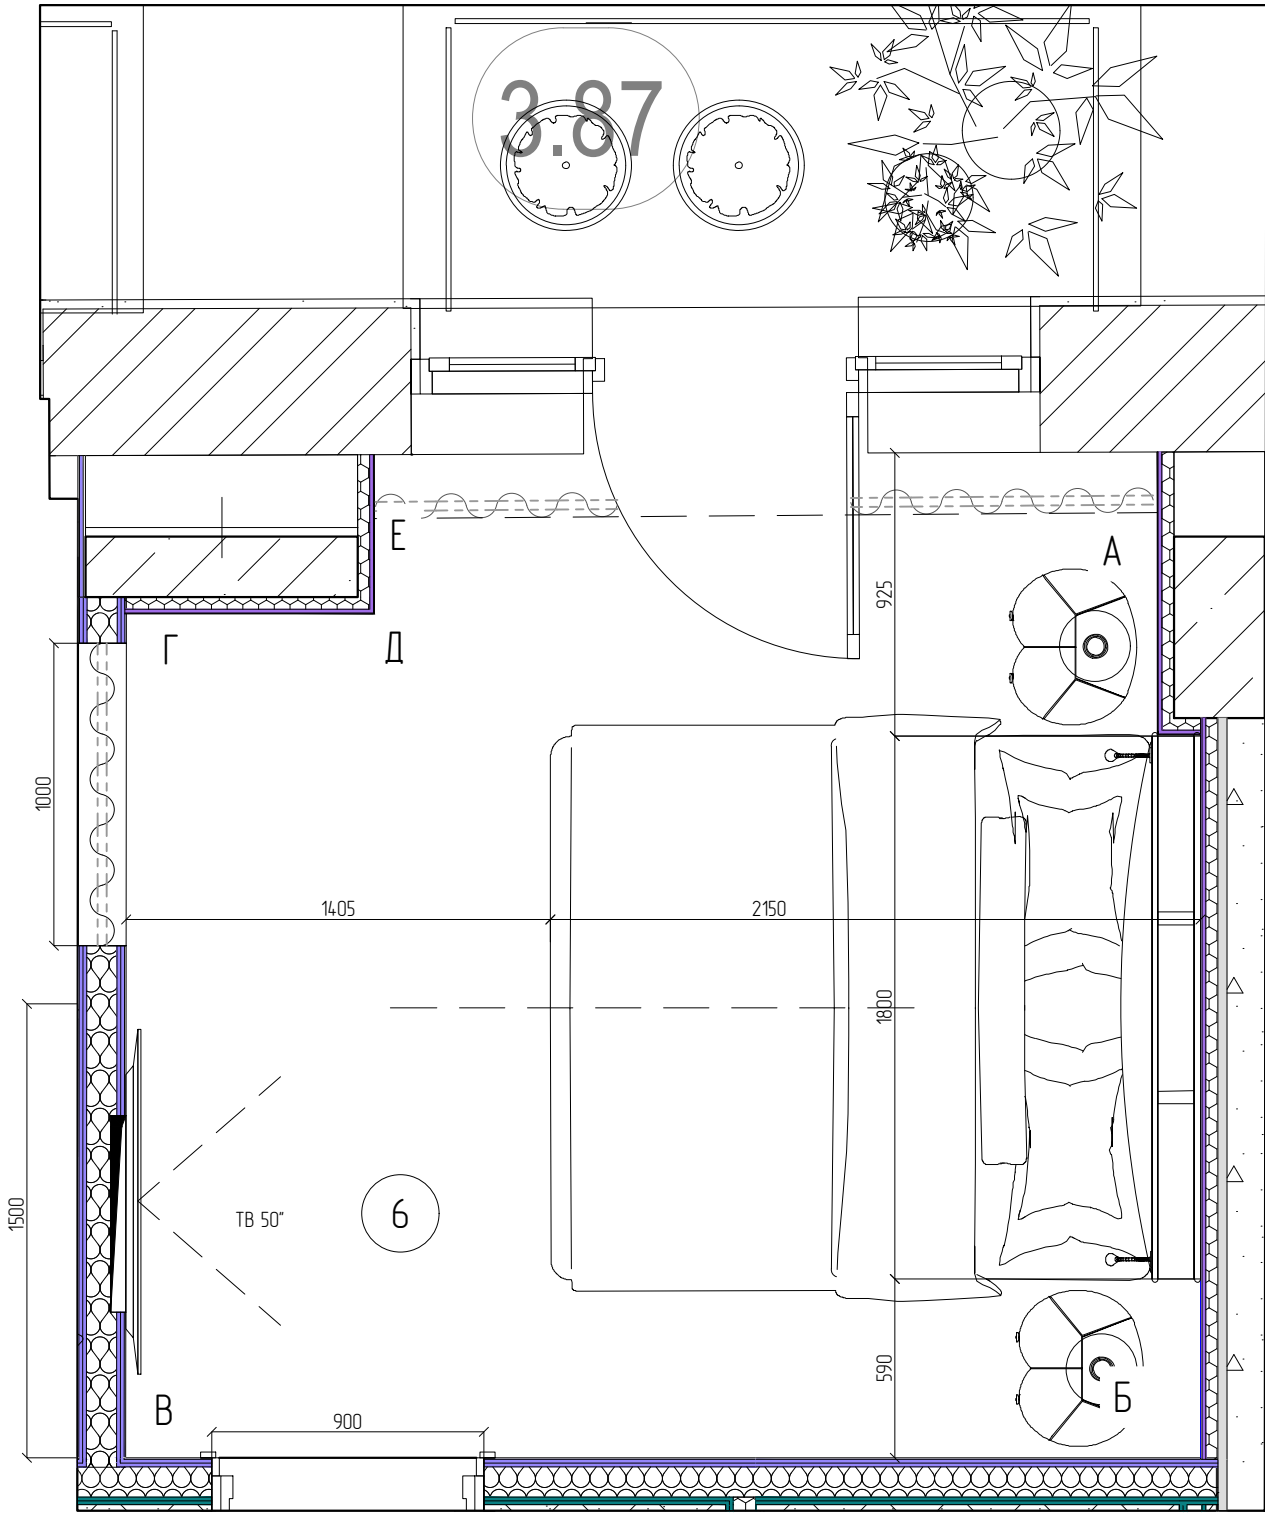


Условные обозначения:
7 - Номер помещения

Примечания:
1. Планировочное решение выполнено на основании чертежей раздела АР, ТЗ и концепции, утвержденной Заказчиком.


						Заказчик: ООО «Приморская» Технический заказчик: АО «СЗ «ЛСР. Недвижимость – М»				ПриМ-0001/2024-АИ.01-410		
						Развитие гостиницы «Приморская» в г. Сочи. Приспособление и сохранение объекта культурного наследия «Здание, где в годы Великой Отечественной войны размещались госпитали № 2095, 2120, 1941-1945 годы», расположенного по адресу: г. Сочи, Центральный район, ул. Соколова, д. 1.						
Изм.	Кол.уч.	Лист	№ док.	Подпись	Дата	Интерьерные решения. Гостиница "Приморская", корпус 1, 4 этаж, N 410. Тип "Делюкс"				Стадия	Лист	Листов
Разработал		Казыева А.Р.			02.02.26					РД	33	40
Проверил		Новикова Е.			02.02.26							
						Помещение №6 (спальная комната). Маркировочный план. М 1:25				ООО "Арх-И-Арт"		
Н.контр.		Бахвалова Л.В.			02.02.26							
ГАП		Сафронова Е.			02.02.26							

Развертка стен А-В. Помещение №6 (спальная комната).
Корпус 1, 4 этаж, N 410. Тип "Делюкс"

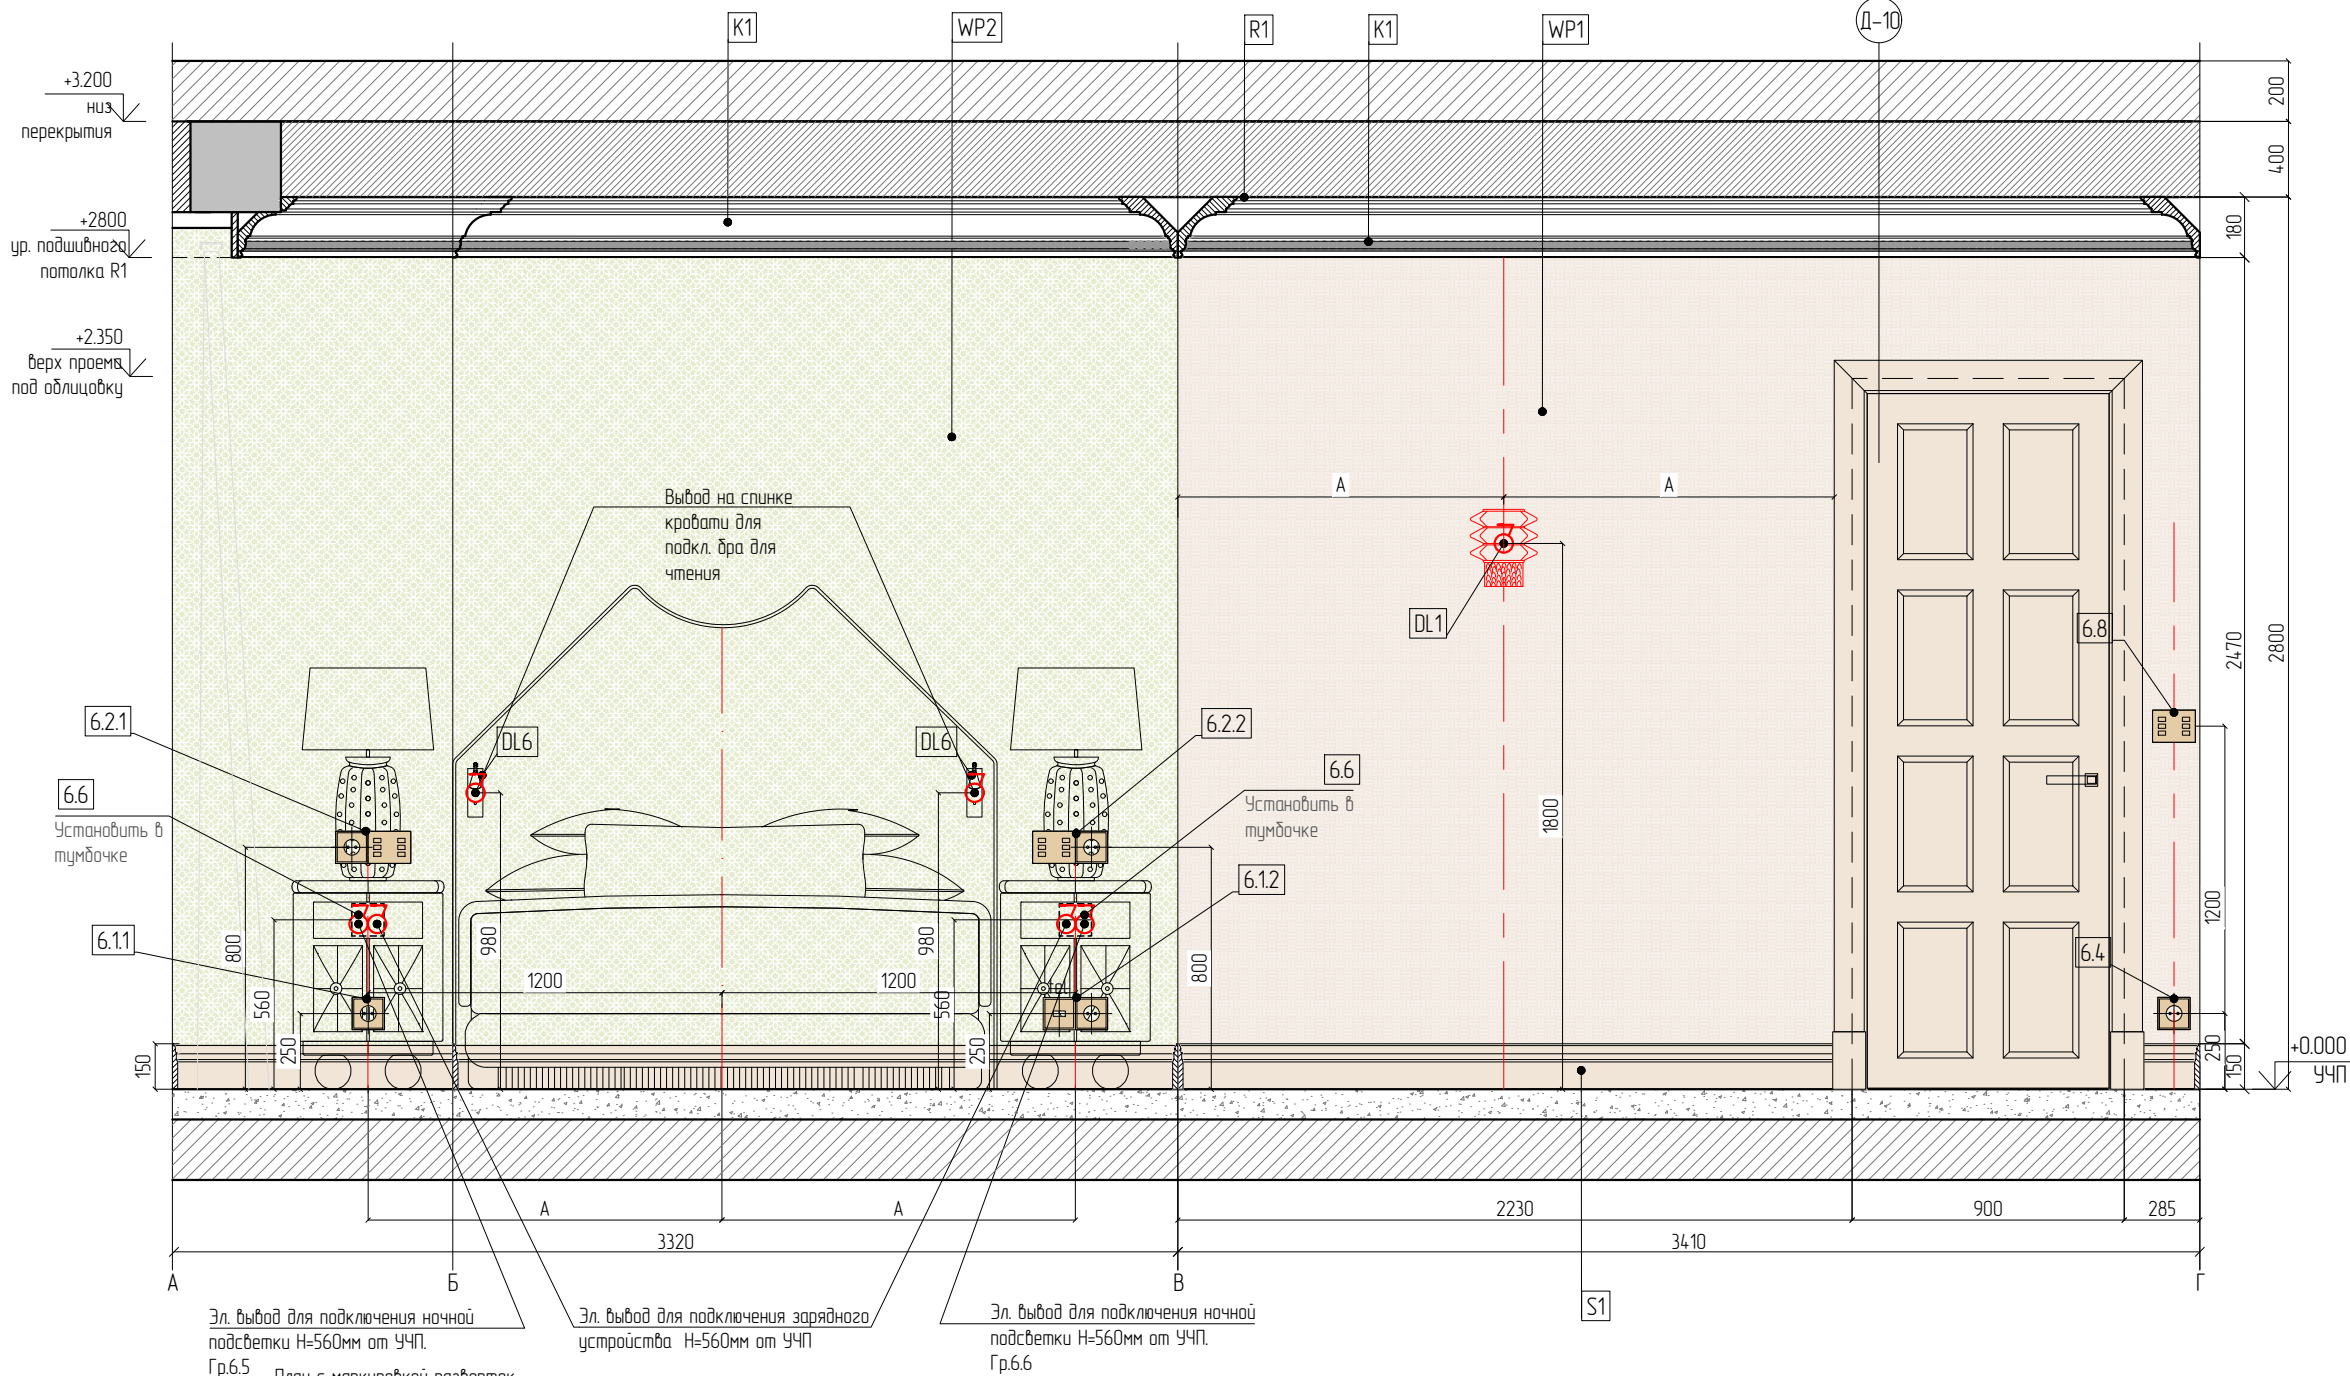

- Условные обозначения
- Панель управления
 - Розетка 220V
 - Телефонная розетка
 - Д-1 - Маркировка дверей и проемов
 - 11 - Нумерация электрооборудования (Таблица с оснащением модулей для управления всем освещением см. лист: План расположения розеток.)
 - DL1 - Маркировка осветительного оборудования
 - 1 - Маркировка отделочных материалов
 - Э - Электрический вывод

Согласовано					
Взам. инв. №					
Подп. и дата					
Инв. № подл.					

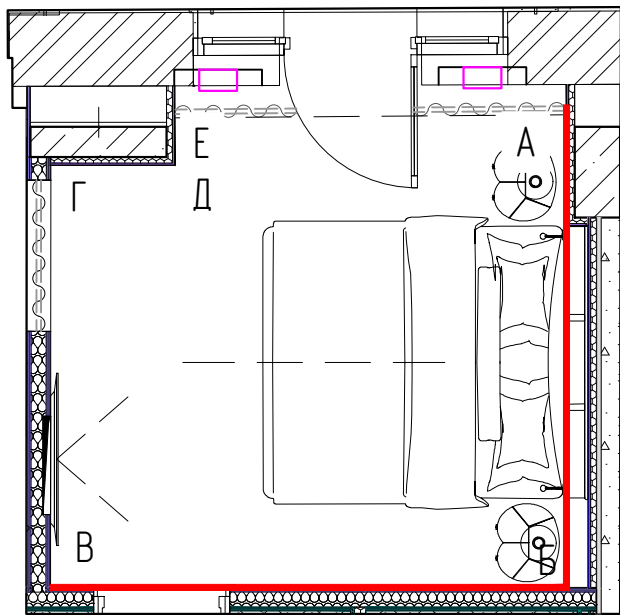


- WP1— Виноловые обои арт. Vinyl Island Raffia col. Sun Bleached 9441, произ-ль PHILLIP JEFFRIES, ширина рулона 132,1см (137,2 см) без обрезки
S_{общ. по пом.}: 11,22 м² + 10% = 12,34 м²
- WP2— обои, панно арт. Plump Tulips RW211 cs01 Original, произ-ль IKSEL WALLPAPER, ширина рулона 35,375" (89,8525см), повтор рисунка 12.375" (31,4325см)
S_{краски в тон потолка}: 10,12+10%= 11,02 м.п.
- K1— Карниз из массива натурального дерева, Ash Wood (ясень), покрытие матовым бесцветным лаком. Н=150мм, толщина 17мм L_{общ. по пом.}: 11,19+10%= 12,30 м.п.
- S1— Плинтус из массива натурального дерева, Ash Wood (ясень), покрытие матовым бесцветным лаком. Н=150мм, толщина 17мм L_{общ. по пом.}: 11,19+10%= 12,30 м.п.

- Примечания:
- Планировочное решение выполнено на основании чертежей раздела АР, ТЗ и концепции, утвержденной Заказчиком.
 - Высоты даны от уровня чистого пола этажа. За отм. чистого пола принять верх чистового покрытия коридора.
 - Расчет отделочных материалов взят с запасом в 5-15%. Подсчет натурального камня скорректировать согласно раскроя Постащика.
 - Перед заказом встроенной мебели необходимо произвести замер силами инженеров от фирм производителей.
 - Цвет и вид отделочных материалов согласовать с автором проекта.
 - Таблица с оснащением модулей для управления всем освещением см. лист: План расположения розеток.

Заказчик: ООО «Приморская»						ПриМ-0001/2024-АИ.01-410		
Технический заказчик: АО «СЗ «ЛСР. Недвижимость – М»								
Развитие гостиницы «Приморская» в г. Сочи. Приспособление и сохранение объекта культурного наследия «Здание, где в годы Великой Отечественной войны размещались госпитали № 2095, 2120, 1941-1945 годы», расположенного по адресу: г. Сочи, Центральный район, ул. Саколова, д. 1.								
Изм.	Кол.уч.	Лист	№ док.	Подпись	Дата	Интерьерные решения. Гостиница "Приморская", корпус 1, 4 этаж, N 410. Тип "Делюкс"	Стадия	Лист
Разработал	Казыева А.Р.	02.02.26					РД	34
Проверил	Нобикова Е.	02.02.26						40
						Помещение №6 (спальная комната). Развертка стен А-В. М 1:25	ООО "Арх-И-Арм"	
Н.контр.	Бахвалова Л.В.	02.02.26						
ГАП	Сафронова Е.	02.02.26						


Развертка стен В-А. Помещение №6 (спальная комната).
Корпус 1, 4 этаж, N 410. Тип "Делюкс"

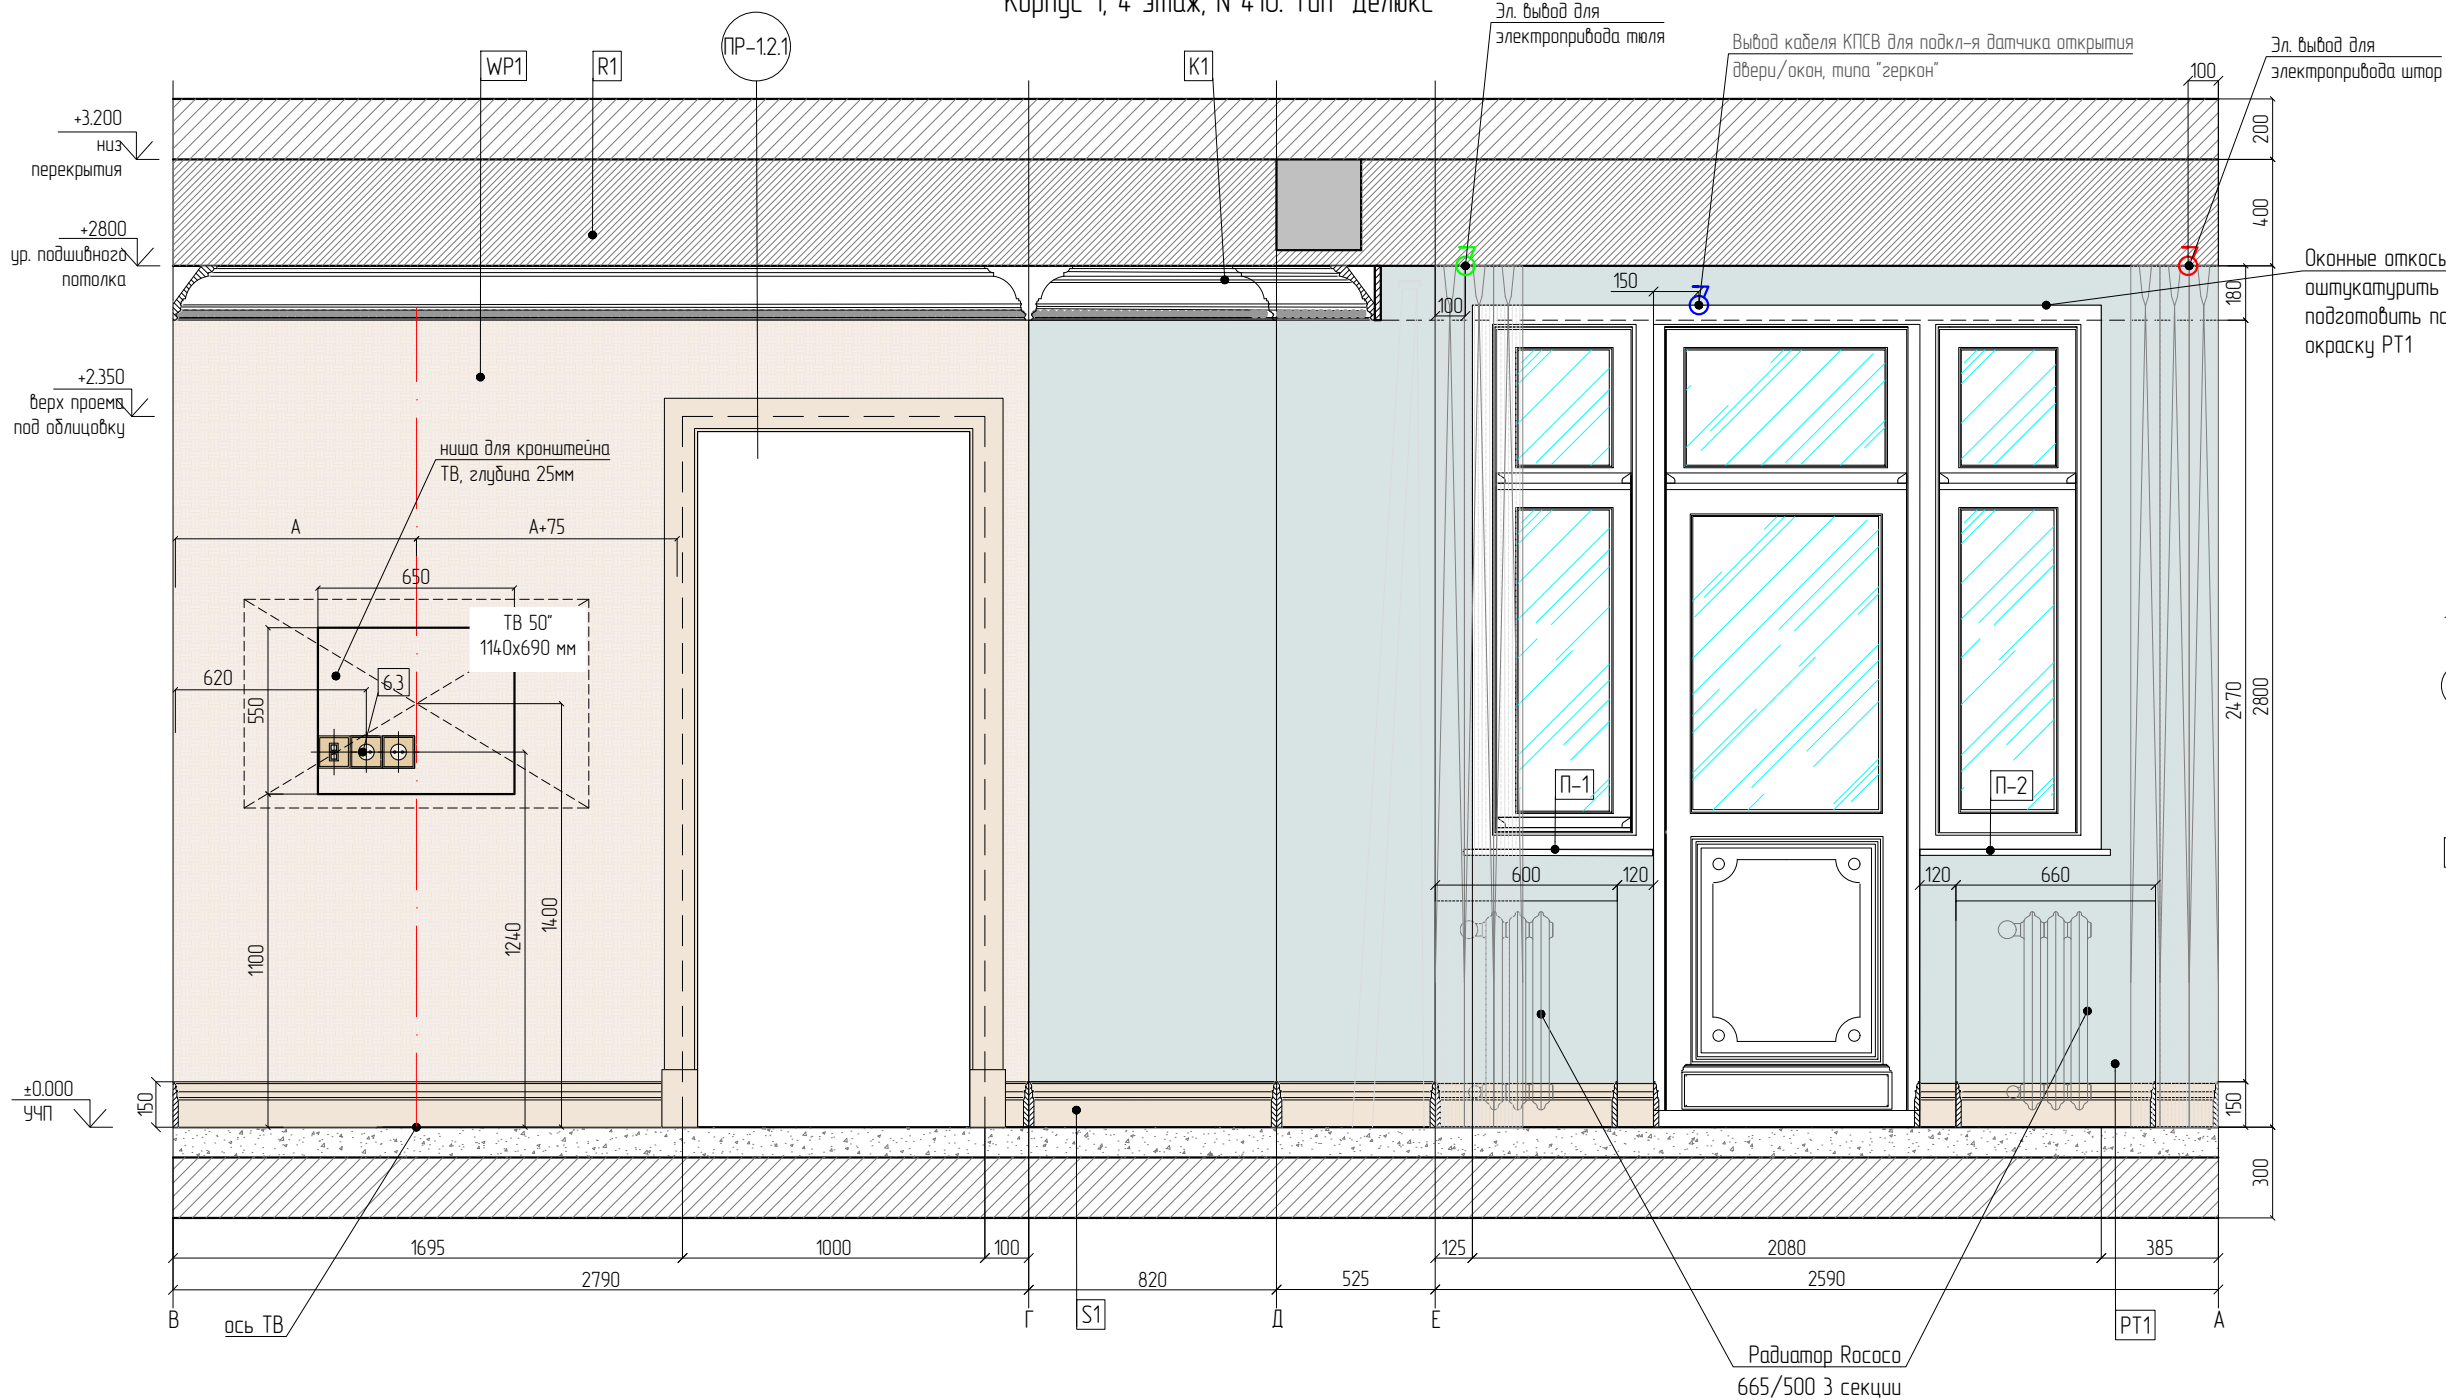

Условные обозначения

- ⊕ - Розетка 220V
- ⊕ - Розетка RJ45 двойная
- Д-1 - Маркировка дверей и проемов
- 1.1 - Нумерация электрооборудования (Таблица с оснащением модулей для управления всем освещением см. лист: План расположения розеток.)
- DL1 - Маркировка осветительного оборудования
- 1 - Маркировка отделочных материалов
- Э - Электрический вывод

План с маркировкой разверток

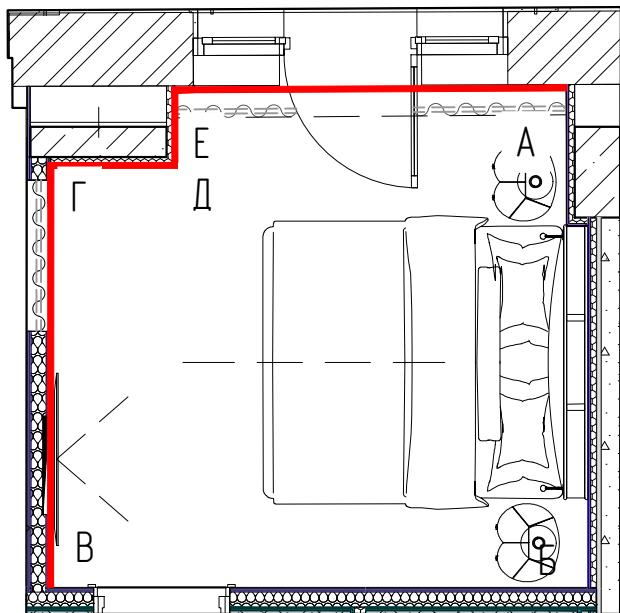


- WP1 - Виниловые обои arm. Vinyl Island Raffia col. Sun Bleached 9441, произ-ль PHILLIP JEFFRIES, ширина рулона 132,1см (137,2 см) без обрезки
S_{общ. по пом.}: 13,1 м2 + 10% = 14,4 м2
- WP2 - обои, панно arm. Plump Tulips RW211 cs01 Original, произ-ль IKSEL WALLPAPER, ширина рулона 35,375" (89,8525см), повтор рисунка 12.375" (31,4325см)
S_{общ. по пом.}: 13,4 м2 + 10% = 14,7 м2
- K1 - Плинтус из массива натурального дерева, Ash Wood (ясень), покрытие матовым бесцветным лаком. Н-150мм, толщина 17мм
L_{общ. по пом.}: 11,19 м + 10% = 12,30 м.п.
- S1 - Плинтус из массива натурального дерева, Ash Wood (ясень), покрытие матовым бесцветным лаком. Н-150мм, толщина 17мм
L_{общ. по пом.}: 11,19 м + 10% = 12,30 м.п.
- PT1 - высококачественная окраска по штукатурной поверхности в 2 слоя. Цвет по RAL: 9010, матовая
S_{общ. по пом.}: 5,79 м2 + 10% = 6,36 м2

Примечания:

- Планировочное решение выполнено на основании чертежей раздела АР, ТЗ и концепции, утвержденной Заказчиком.
- Высоты даны от уровня чистого пола этажа. За отм. чистого пола принять верх чистого покрытия коридора.
- Расчет отделочных материалов взят с запасом в 5-15%. Подсчет натурального камня скорректировать согласно раскроя Поставщика.
- Перед заказом встроенной мебели необходимо произвести замер силами инженеров от фирм производителей.
- Цвет и вид отделочных материалов согласовать с автором проекта.
- Таблица с оснащением модулей для управления всем освещением см. лист: План расположения розеток.

						Заказчик: ООО «Приморская»			ПриМ-0001/2024-АИ.01-410		
						Технический заказчик: АО «СЗ «ЛСР. Недвижимость – М»					
						Развитие гостиницы «Приморская» в г. Сочи. Приспособление и сохранение объекта культурного наследия «Здание, где в годы Великой Отечественной войны размещались госпитали № 2095, 2120, 1941-1945 годы», расположенного по адресу: г. Сочи, Центральный район, ул. Соколова, д. 1.					
Изм.	Кол.уч.	Лист	№ док.	Подпись	Дата	Интерьерные решения. Гостиница "Приморская", корпус 1, 4 этаж, N 410. Тип "Делюкс"			Стадия	Лист	Листов
Разработал	Казыева А.Р.				02.02.26				РД	35	40
Проверил	Новикова Е.				02.02.26						
						Помещение №6 (спальная комната). Развертка стен А-В. М 1:25			ООО "Арх-И-Арм"		
Н.контр.	Бахвалова Л.В.				02.02.26						
ГАП	Сафронова Е.				02.02.26						

Маркировочный план. Помещение №7 (гостиная комната).
Корпус 1, 4 этаж, N410. Тип "Делюкс".

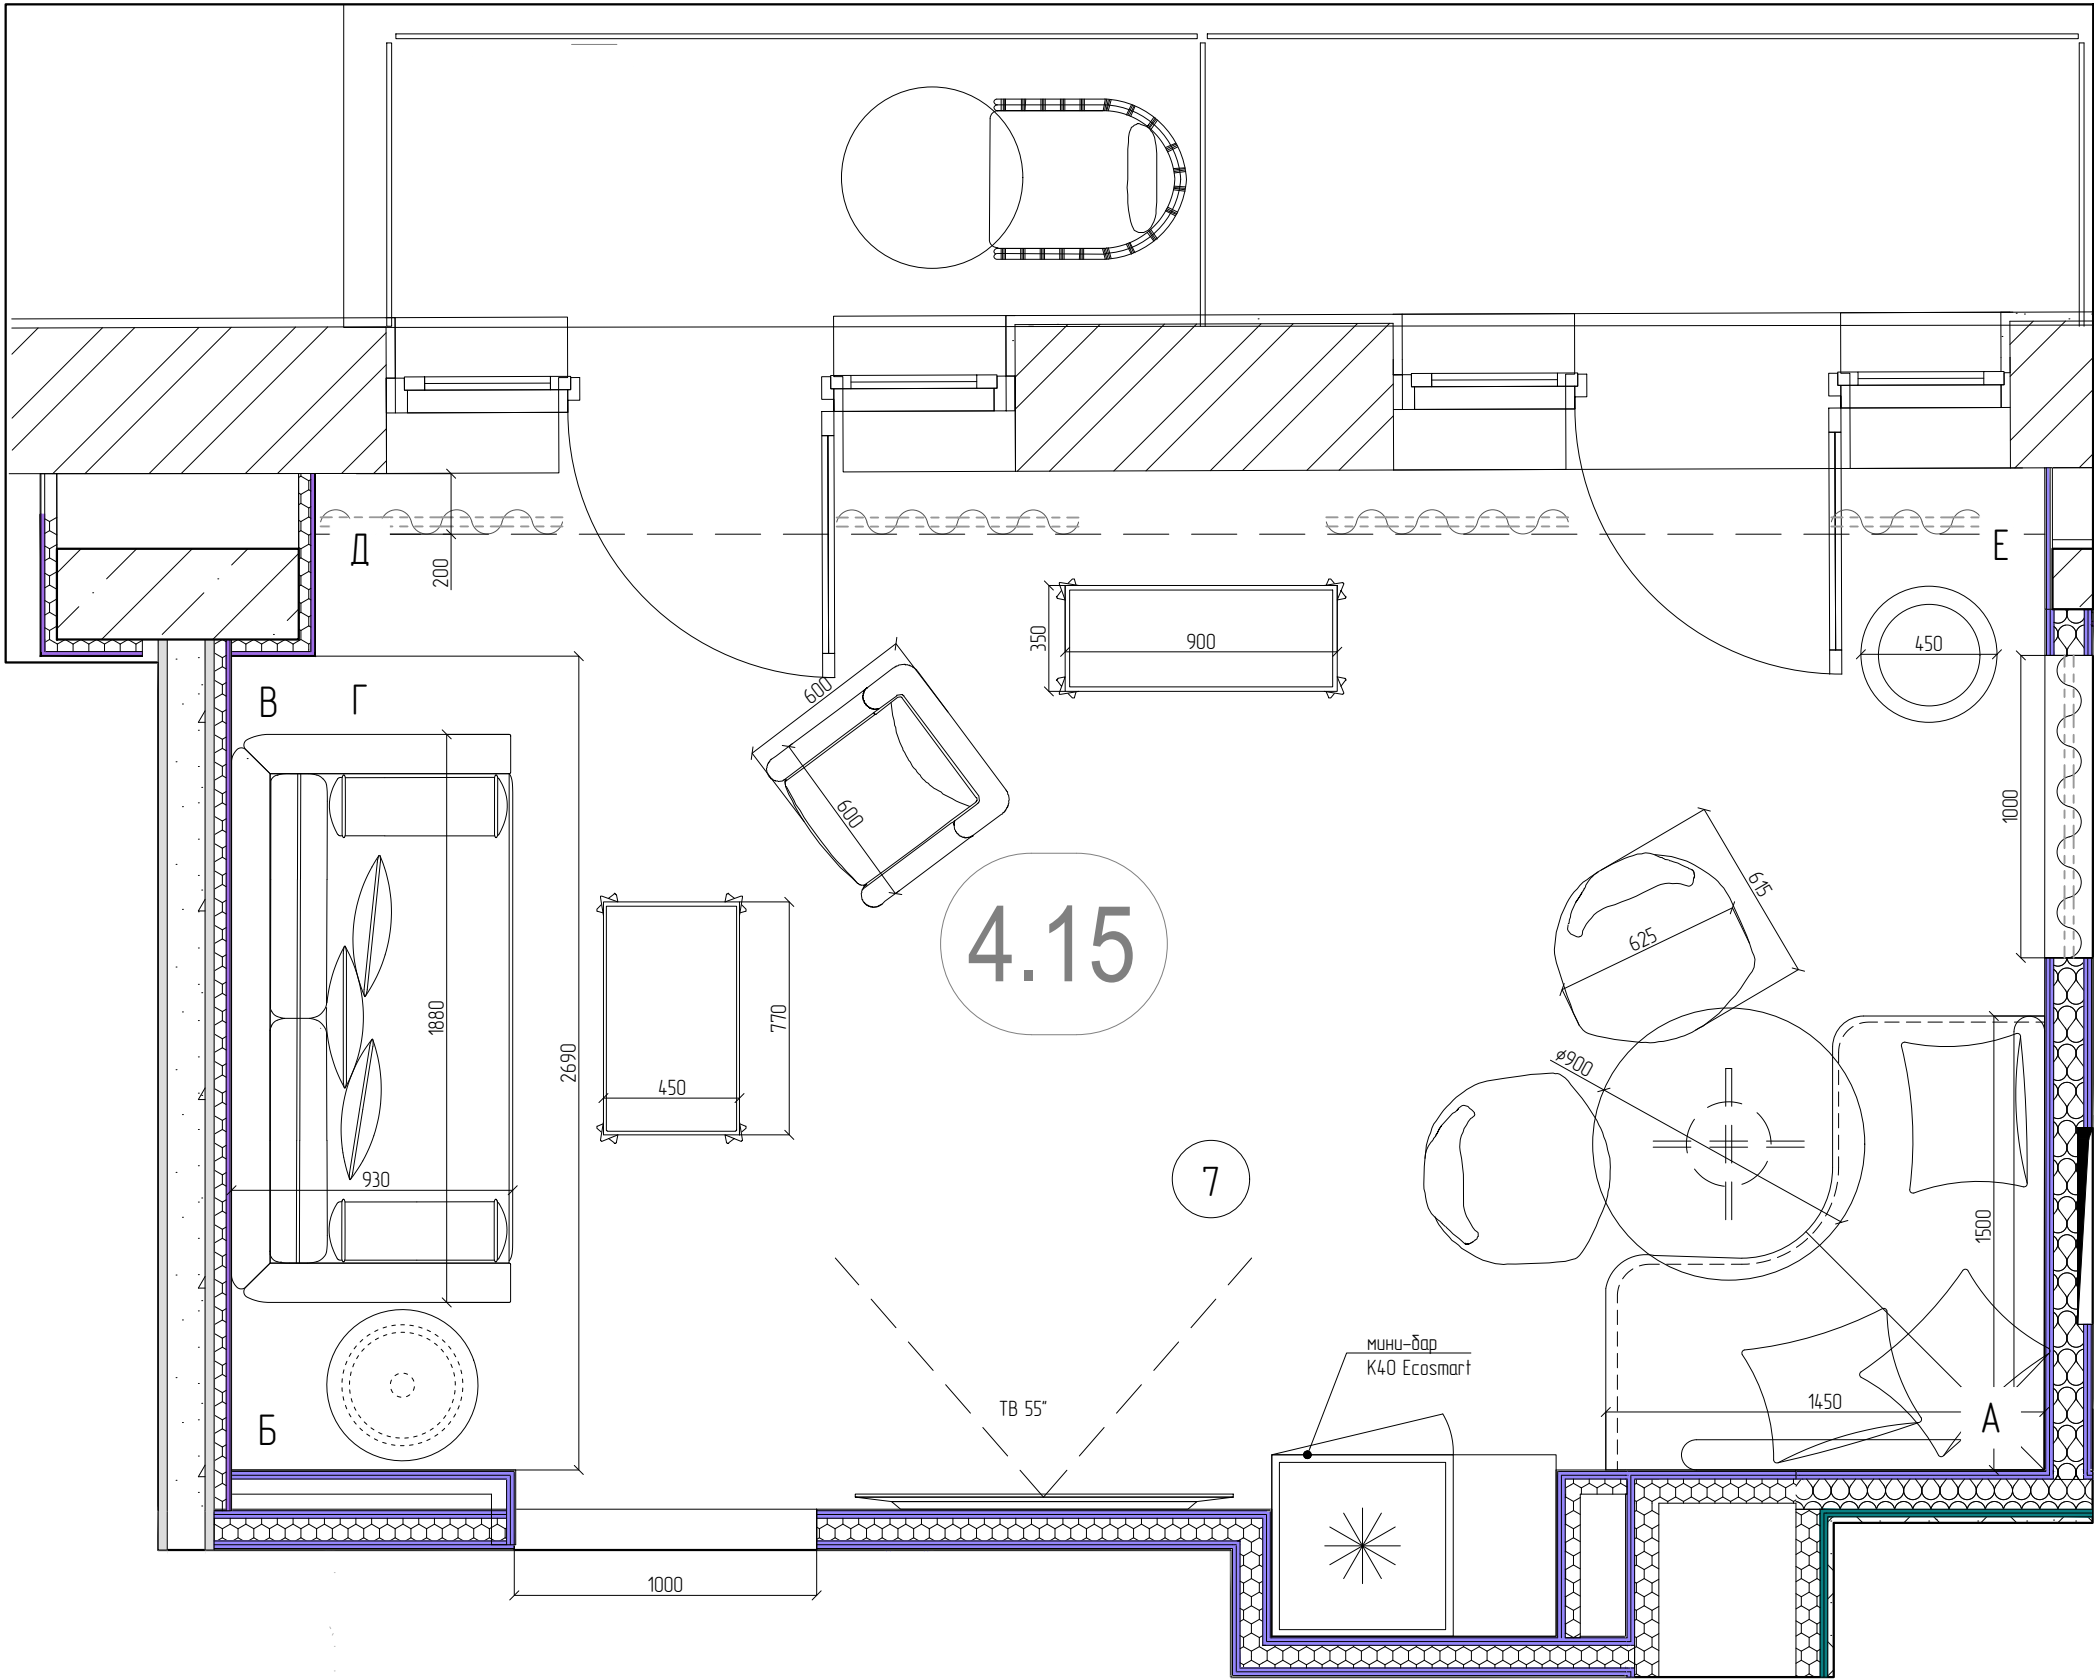

Условные обозначения:

2 - Номер помещения

Примечания:


1. Планировочное решение выполнено на основании чертежей раздела АР, ТЗ и концепции, утвержденной Заказчиком.

						Заказчик: ООО «Приморская» Технический заказчик: АО «СЗ «ЛСР. Недвижимость – М»			ПриМ-0001/2024-АИ.01-410			
						Развитие гостиницы «Приморская» в г. Сочи. Приспособление и сохранение объекта культурного наследия «Здание, где в годы Великой Отечественной войны размещались госпитали № 2095, 2120, 1941-1945 годы», расположенного по адресу: г. Сочи, Центральный район, ул. Соколова, д. 1.						
Изм.	Кол.уч.	Лист	№ док.	Подпись	Дата	Интерьерные решения. Гостиница "Приморская", корпус 1, 4 этаж, N 410. Тип "Делюкс"			Стадия	Лист	Листов	
Разработал		Казыева А.Р.			02.02.26				РД	36	40	
Проверил		Новикова Е.			02.02.26							
						Помещение №7 (гостиная комната). Маркировочный план. М 1:25			ООО "Арх-И-Арм"			
Н.контр.		Бахвалова Л.В.			02.02.26							
ГАП		Сафронова Е.			02.02.26							

Развертка стен А-Б. Помещение №7 (гостиная комната).


Корпус 1, 4 этаж, N 410. Тип "Делюкс"

Эл. вывод для подкл-я освещения в мини баре. Вывести под потолок свободный конец 1,2 метра

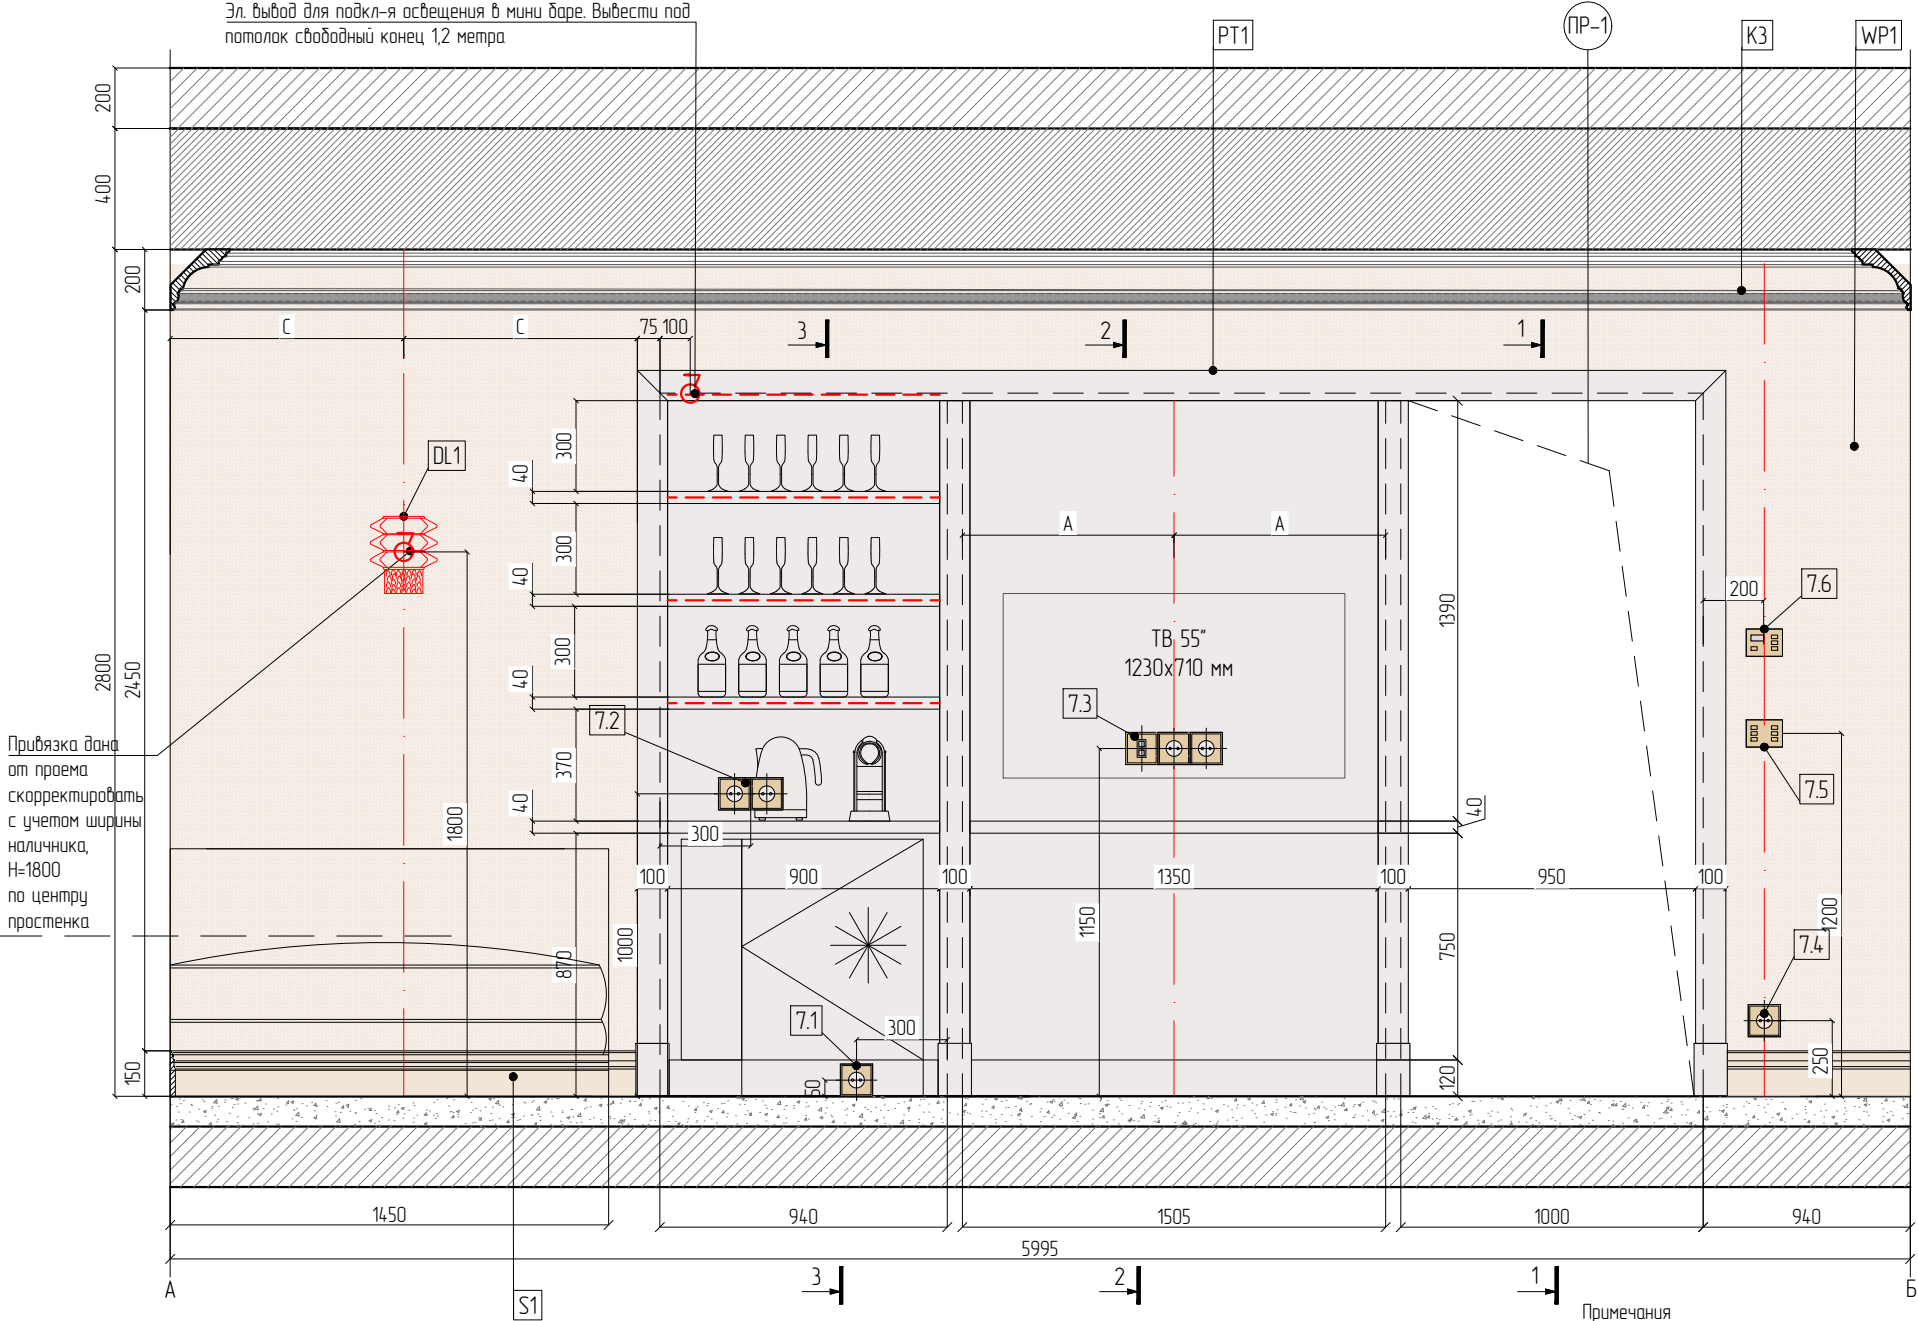


Приблизка дана от проема скорректировать с учетом ширины наличника, Н=1800 по центру простенка

+3.200 низ перекрытия
+2.800 ур. подшивного потолка
+2.350 верх проема под облицовку
+0.000 члп

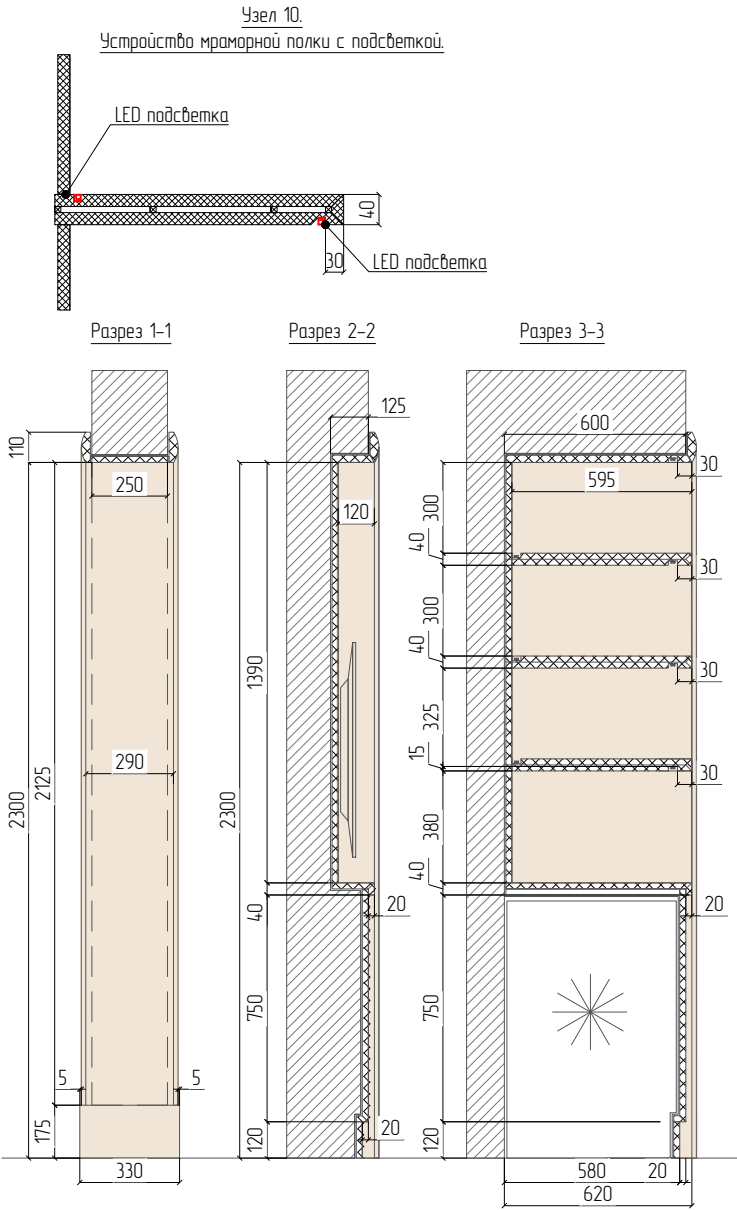

План с маркировкой разверток

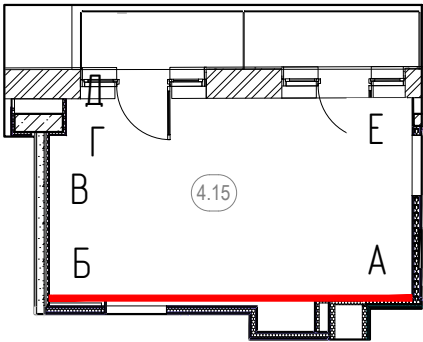

Согласовано

Взам. инв. №

Подп. и дата

Инв. № подл.

Условные обозначения

- Панель управления
- Терморегулятор
- Розетка 220V
- Розетка RJ45 двойная

Д-1 - Маркировка дверей и проемов

11 - Нумерация электрооборудования (Таблица с оснащением модулей для управления всем освещением см. лист: План расположения розеток)

DL1 - Маркировка осветительного оборудования

Э - Электрический вывод

LED подсветка

1 - Маркировка отделочных материалов

WP1 - WP1- Виниловые обои arm. Vinyl Island Raffia col. Sun Bleached 9441, произ-ль PHILLIP JEFFRIES, ширина рулона 132,1см (137,2 см) без обрезки
S_{общ. по пом.} = 23,4 м2 + 10% = 25,74 м2

K3 - K3- Карниз гипсовый окрашен в тон потолка. Цвет по RAL: 9010. Н общ. ~200mm для установки на стене.
L_{общ. по пом.} = 18,2 + 10% = 20 м.п.

S1 - S1- Плинтус из массива натурального дерева, Ash Wood (ясень), покрытие матовым бесцветным лаком. Н-150мм, толщина 17мм
L_{общ. по пом.} = 14,4 + 10% = 15,84 м.п.


PT1 - PT1- высококачественная окраска по штукатурной поверхности в 2 слоя. Цвет по RAL: 9010, матовая
S_{общ. по пом.} = 5,79 м2 + 10% = 6,36 м2

Примечания

- Планировочное решение выполнено на основании чертежей раздела АР, ТЗ и концепции, утвержденной Заказчиком.
- Высоты даны от уровня чистого пола этажа. За отм. чистого пола принять верх чистового покрытия коридора.
- Расчет отделочных материалов взят с запасом в 5-15%. Подсчет натурального камня скорректировать согласно раскроя Поставщика.
- Перед заказом встроенной мебели необходима произвести замер силами инженеров от фирм производителей.
- Цвет и вид отделочных материалов согласовать с автором проекта.
- Таблица с оснащением модулей для управления всем освещением см. лист: План расположения розеток.


Заказчик: ООО «Приморская»						ПриМ-0001/2024-АИ.01-410		
Технический заказчик: АО «СЗ «ЛСР. Недвижимость - М»								
Развитие гостиницы «Приморская» в г. Сочи. Приспособление и сохранение объекта культурного наследия «Здание, где в годы Великой Отечественной войны размещались госпитали № 2095, 2120, 1941-1945 годы», расположенного по адресу: г. Сочи, Центральный район, ул. Саколова, д. 1.								
Изм.	Кол.уч.	Лист	№ док.	Подпись	Дата	Интерьерные решения. Гостиница "Приморская", корпус 1, 4 этаж, N 410. Тип "Делюкс"	Стадия	Лист
Разработал	Казыева А.Р.				02.02.26		РД	37
Проверил	Нобикова Е.				02.02.26			40
						Помещение №7 (гостиная комната). Развертка стен А-Б. М 1:25	ООО "Арх-И-Арм"	
Н.контр.	Бахвалова Л.В.				02.02.26			
ГАП	Сафронова Е.				02.02.26			

Развертка стен Б-Ж. Помещение №7 (гостиная комната).
Корпус 1, 4 этаж, N 410. Тип "Делюкс"

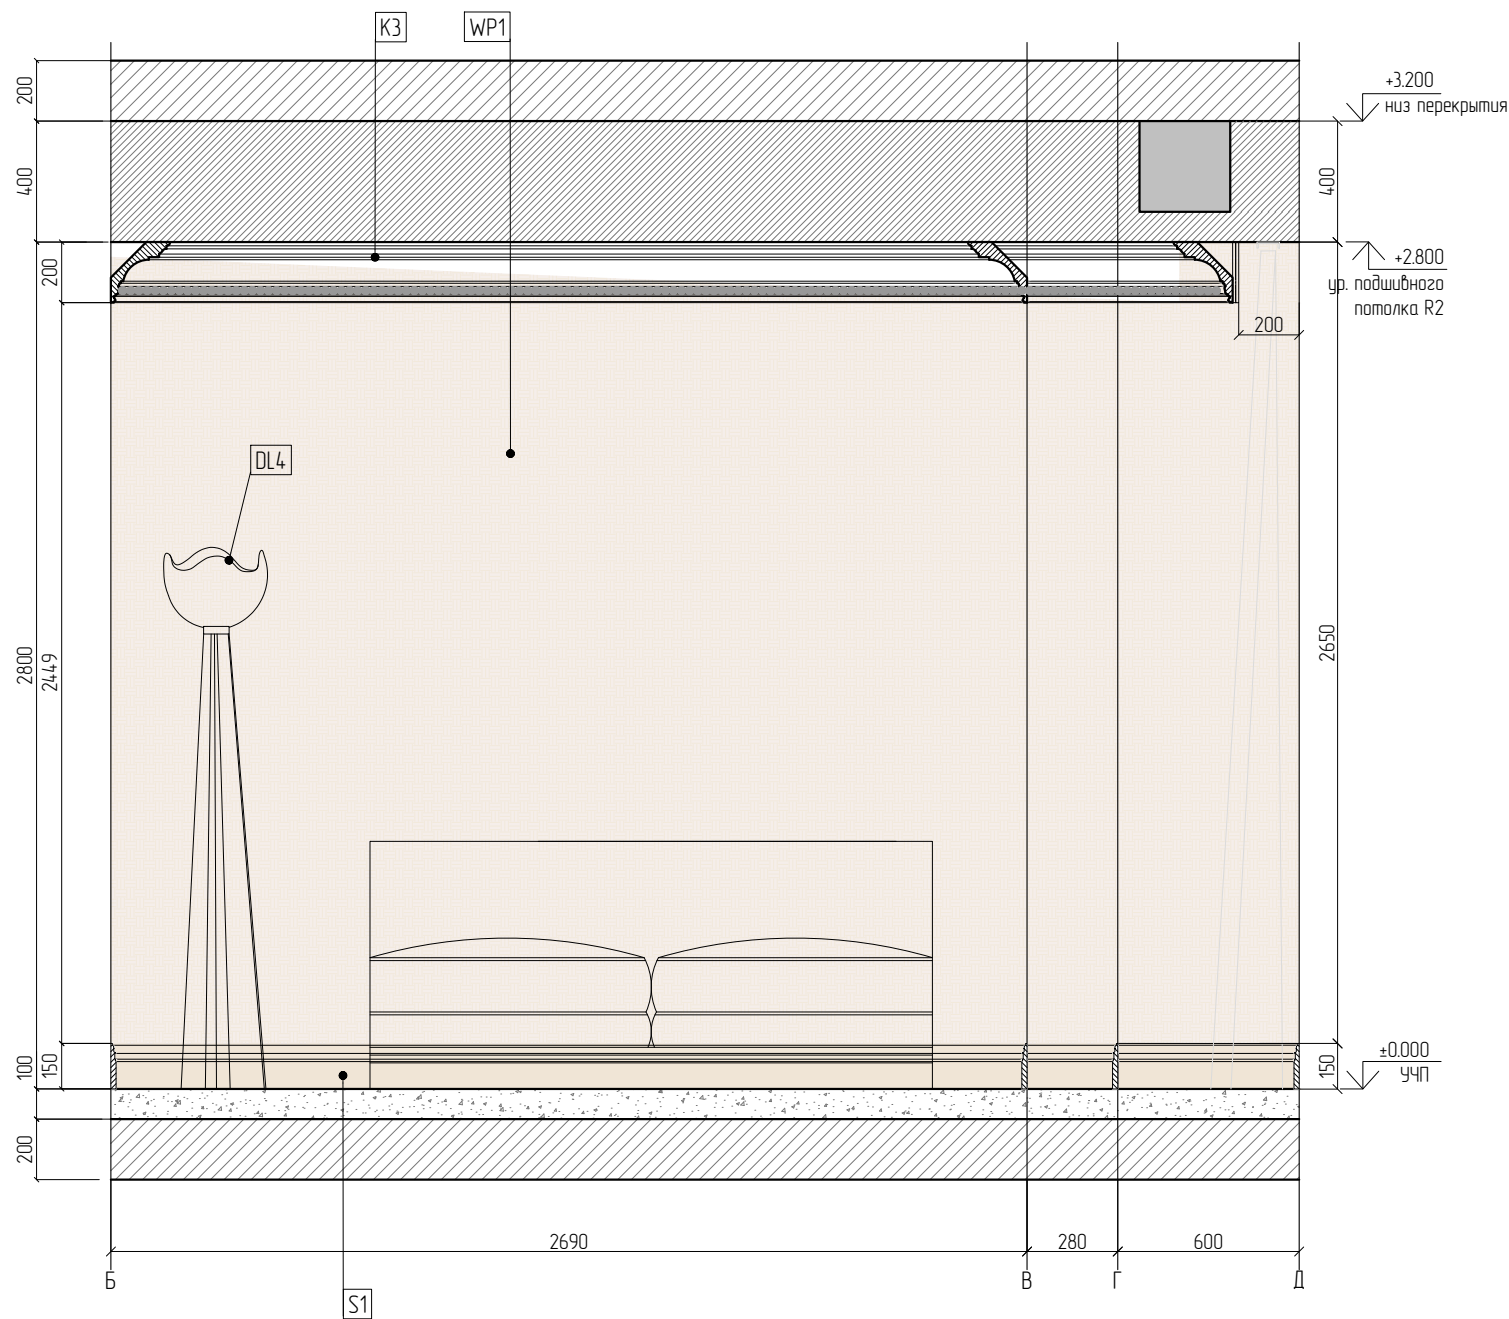

- WP1** – WP1– Виноловые обои арт. Vinyl Island Raffia col. Sun Bleached 9441 , произ– ль PHILLIP JEFFRIES, ширина рулона 132,1см (137,2 см) без обрезки
S_{общ.} по пом. = 23,4 м² + 10% = 25,74 м² RAL 9010.
H общ.–200mm для установки на стене.
L_{общ.} по пом. = 18,2 +10%= 20 м.п.
- K3** – K3– Карнизы из полиуретана, окраска в тон потолка. Цвет по RAL 9010.
H общ.–200mm для установки на стене.
L_{общ.} по пом. = 18,2 +10%= 20 м.п.
- S1** – S1– Плинтус из массива натурального дерева, Ash Wood (ясень), покрытие матовым бесцветным лаком. H–150мм, толщина 17мм
L_{общ.} по пом. = 14,4+10%= 15,84 м.п.
- PT1** – PT1– высококачественная окраска по штукатурной поверхности в 2 слоя. Цвет по RAL: 9010, матовая
S_{общ.} по пом.: 5,79 м² + 10% = 6,36 м²


План с маркировкой разверток

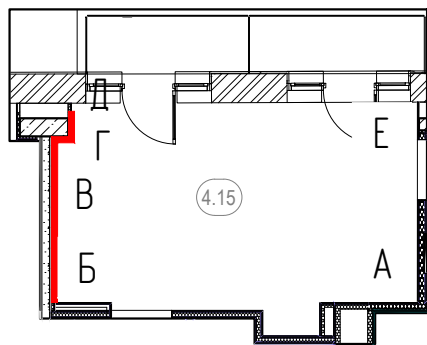

- Примечания:
- Планировочное решение выполнено на основании чертежей раздела АР, ТЗ и концепции, утвержденной Заказчиком.
 - Высоты даны от уровня чистого пола этажа. За отм. чистого пола принять верх чистового покрытия коридора.
 - Расчет отделочных материалов взят с запасом в 5-15%. Подсчет натурального камня скорректировать согласно раскроя Поставщика.
 - Перед заказом встроенной мебели необходимо произвести замер силами инженеров от фирм производителей.
 - Цвет и вид отделочных материалов согласовать с автором проекта.
 - Таблица с оснащением модулей для управления всем освещением см. лист: План расположения розеток.

						Заказчик: ООО «Приморская» Технический заказчик: АО «СЗ «ЛСР. Недвижимость – М»				ПриМ-0001/2024–АИ.01-410		
						Развитие гостиницы «Приморская» в г. Сочи. Приспособление и сохранение объекта культурного наследия «Здание, где в годы Великой Отечественной войны размещались госпитали № 2095, 2120, 1941-1945 годы», расположенного по адресу: г. Сочи, Центральный район, ул. Соколова, д. 1.						
Изм.	Кол.уч.	Лист	№ док.	Подпись	Дата	Интерьерные решения. Гостиница “Приморская”, корпус 1, 4 этаж, N 410. Тип “Делюкс”				Стадия	Лист	Листов
Разработал				Казыева А.Р.	02.02.26					РД	38	40
Проверил				Новикова Е.	02.02.26							
Н.контр.				Бахвалова Л.В.	02.02.26	Помещение №7 (гостиная комната). Развертка стен Б-Ж. М 1:25				ООО “Арх-И-Арм”		
ГАП				Сафронова Е.	02.02.26							

Корпус 1, 4 этаж, Н 410. Тип "Делюкс"

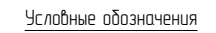


-  – Панель управления
-  – Розетка 220V
-  – Телефонная розетка
-  – Маркировка дверей и проемов
-  – Нумерация электрооборудования
(Таблица с оснащением модулей для управления всем освещением см. лист: План расположения розеток.)
-  – Маркировка осветительного оборудования
-  – Маркировка отделочных материалов
-  – Электрический вывод
-  – Слаботочный электрический вывод

- WP1– Виниловые обои aprm. Vinyl Island Raffia col. Sun Bleached 9441 , произ- ль PHILLIP JEFFRIES, ширина рулона 132,1 см (137,2 см) без обрезки
 $S_{\text{общ. по пом.}} = 23,4 \text{ м}^2 + 10\% = 25,74 \text{ м}^2$
 Виз. Карниз из ламинации окраске в тон потолка. Цвет по RAL-9010.
 Н.общ.–200мм для установки на стене.
 $L_{\text{общ. по пом.}} = 18,2 + 10\% = 20 \text{ м.п.}$
 - S1– Плинтус из массива натурального дерева, Ash Wood (ясень), покрытие матовым бесцветным лаком. Н-150мм, толщина 17мм
 $L_{\text{общ. по пом.}} = 14,4 + 10\% = 15,84 \text{ м.п.}$
 - PT1– высококачественная окраска по штукатурной поверхности в 2 слоя. Цвет по RAL: 9010, матовая
 $S_{\text{общ. по пом.}} = 5,79 \text{ м}^2 + 10\% = 6,36 \text{ м}^2$

1. Планировочное решение выполнено на основании чертежей раздела АР, ТЗ и концепции, утвержденной Заказчиком.
2. Высоты даны от уровня чистого пола этажа. За опм. чистого пола принять верх чистового покрытия коридора.
3. Расчет отделочных материалов взят с запасом в 5-15%. Подсчет натурального камня скорректировать согласно раскроя Постащика.
4. Перед заказом встроенной мебели необходимо произвести замер силами инженеров от фирм производителей.
5. Цвет и вид отделочных материалов согласовать с автором проекта.
6. Таблица с оснащением модулей для управления всем освещением см. лист: План расположения розеток.

						Заказчик: ООО «Приморская»	Прим-0001/2024-АИ.01-410		
						Технический заказчик: АО «СЗ «ЛСР. Недвижимость – М»			
						Развитие гостиницы «Приморская» в г. Сочи. Приспособление и сохранение объекта культурного наследия «Здание, где в годы Великой Отечественной войны размещались госпитали № 2095, 2120, 1941–1945 годы», расположенного по адресу: г. Сочи, Центральный район, ул. Соколова, д. 1.			
Изм.	Кол.уч.	Лист	№ док.	Подпись	Дата				
Разработал		Казыева А.Р.			02.02.26	Интерьерные решения. Гостиница “Приморская”, корпус 1, 4 этаж, N 410. Тип “Делюкс”	Стадия	Лист	Листов
Проверил		Нобикова Е.			02.02.26		РД	39	40
						Помещение №7 (гостиная комната). Развертка стен Ж-3. М 1:25	ООО “Арх-И-Арт”		
Н.контр.		Бахдалова Л.В.			02.02.26				
ГАП		Сафронова Е.			02.02.26				

Развертка стен 3-А. Помещение №7 (гостиная комната).
Корпус 1, 4 этаж, N 410. Тип "Делюкс"

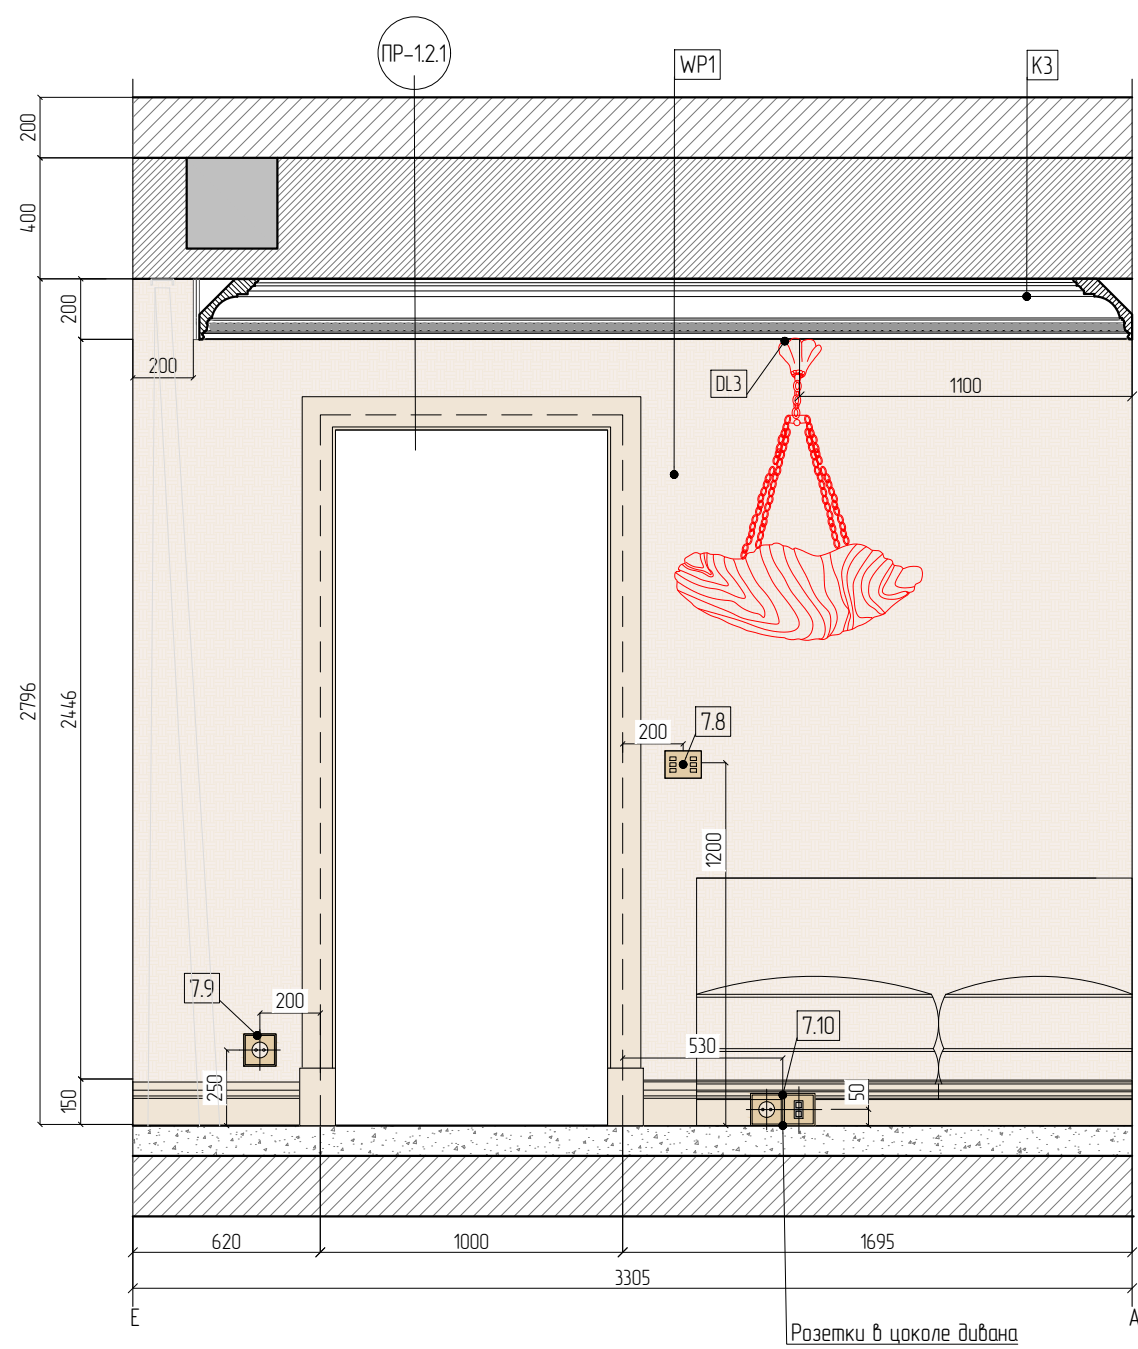

+3.200
низ перекрытия

+2.800
ур.
подшивного
потолка

+0.000
учп


Условные обозначения

- Панель управления
- Розетка 220V
- USB-розетка двойная
- Маркировка дверей и проемов
- Нумерация электрооборудования (Таблица с оснащением модулей для управления всем освещением см. лист: План расположения розеток)
- Маркировка осветительного оборудования
- Маркировка отделочных материалов

- WP1- Виноловые обои арт. Vinyl Island Raffia col. Sun Bleached 9441, произ-ль PHILLIP JEFFRIES, ширина рулона 132,1см (137,2 см) без обрезки
 $S_{общ. по пом.} = 23,4 \text{ м}^2 + 10\% = 25,74 \text{ м}^2$
- K3- Карниз гипсовый в окраске в тон потолка. Цвет по RAL: 9010.
Н общ.-200мм для установки на стене.
 $L_{общ. по пом.} = 18,2 + 10\% = 20 \text{ м.п.}$
- S1- Плинтус из массива натурального дерева, Ash Wood (ясень), покрытие матовым бесцветным лаком. Н-150мм, толщина 17мм
 $L_{общ. по пом.} = 14,4 + 10\% = 15,84 \text{ м.п.}$
- PT1- высококачественная окраска по штукатурной поверхности в 2 слоя. Цвет по RAL: 9010, матовая
 $S_{общ. по пом.} = 5,79 \text{ м}^2 + 10\% = 6,36 \text{ м}^2$

Согласовано					
Взам. инв. №					
Подп. и дата					
Инв. № подл.					

План с маркировкой разверток

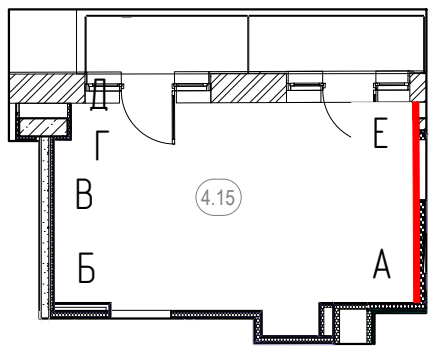

Примечания

- Планировочное решение выполнено на основании чертежей раздела АР, ТЗ и концепции, утвержденной Заказчиком.
- Высоты даны от уровня чистого пола этажа. За отм. чистого пола принять верх чистового покрытия коридора.
- Расчет отделочных материалов взят с запасом в 5-15%. Подсчет натурального камня скорректировать согласно раскроя Поставщика.
- Перед заказом встроенной мебели необходимо произвести замер силами инженеров от фирм производителей.
- Цвет и вид отделочных материалов согласовать с автором проекта.
- Таблица с оснащением модулей для управления всем освещением см. лист: План расположения розеток.

Заказчик: ООО «Приморская»						ПриМ-0001/2024-АИ.01-410		
Технический заказчик: АО «СЗ «ЛСР. Недвижимость – М»								
Развитие гостиницы «Приморская» в г. Сочи. Приспособление и сохранение объекта культурного наследия «Здание, где в годы Великой Отечественной войны размещались госпитали № 2095, 2120, 1941-1945 годы», расположенного по адресу: г. Сочи, Центральный район, ул. Саколова, д. 1.								
Изм.	Кол.уч.	Лист	№ док.	Подпись	Дата	Интерьерные решения. Гостиница "Приморская", корпус 1, 4 этаж, N 410. Тип "Делюкс"	Стадия	Лист
Разработал				Казыева А.Р.	02.02.26		РД	40
Проверил				Новикова Е.	02.02.26			40
						Помещение №7 (гостиная комната). Развертка стен 3-А. М 1:25	ООО "Арх-И-Арт"	
Н.контр.				Бахвалова Л.В.	02.02.26			
ГАП				Сафронова Е.	02.02.26			